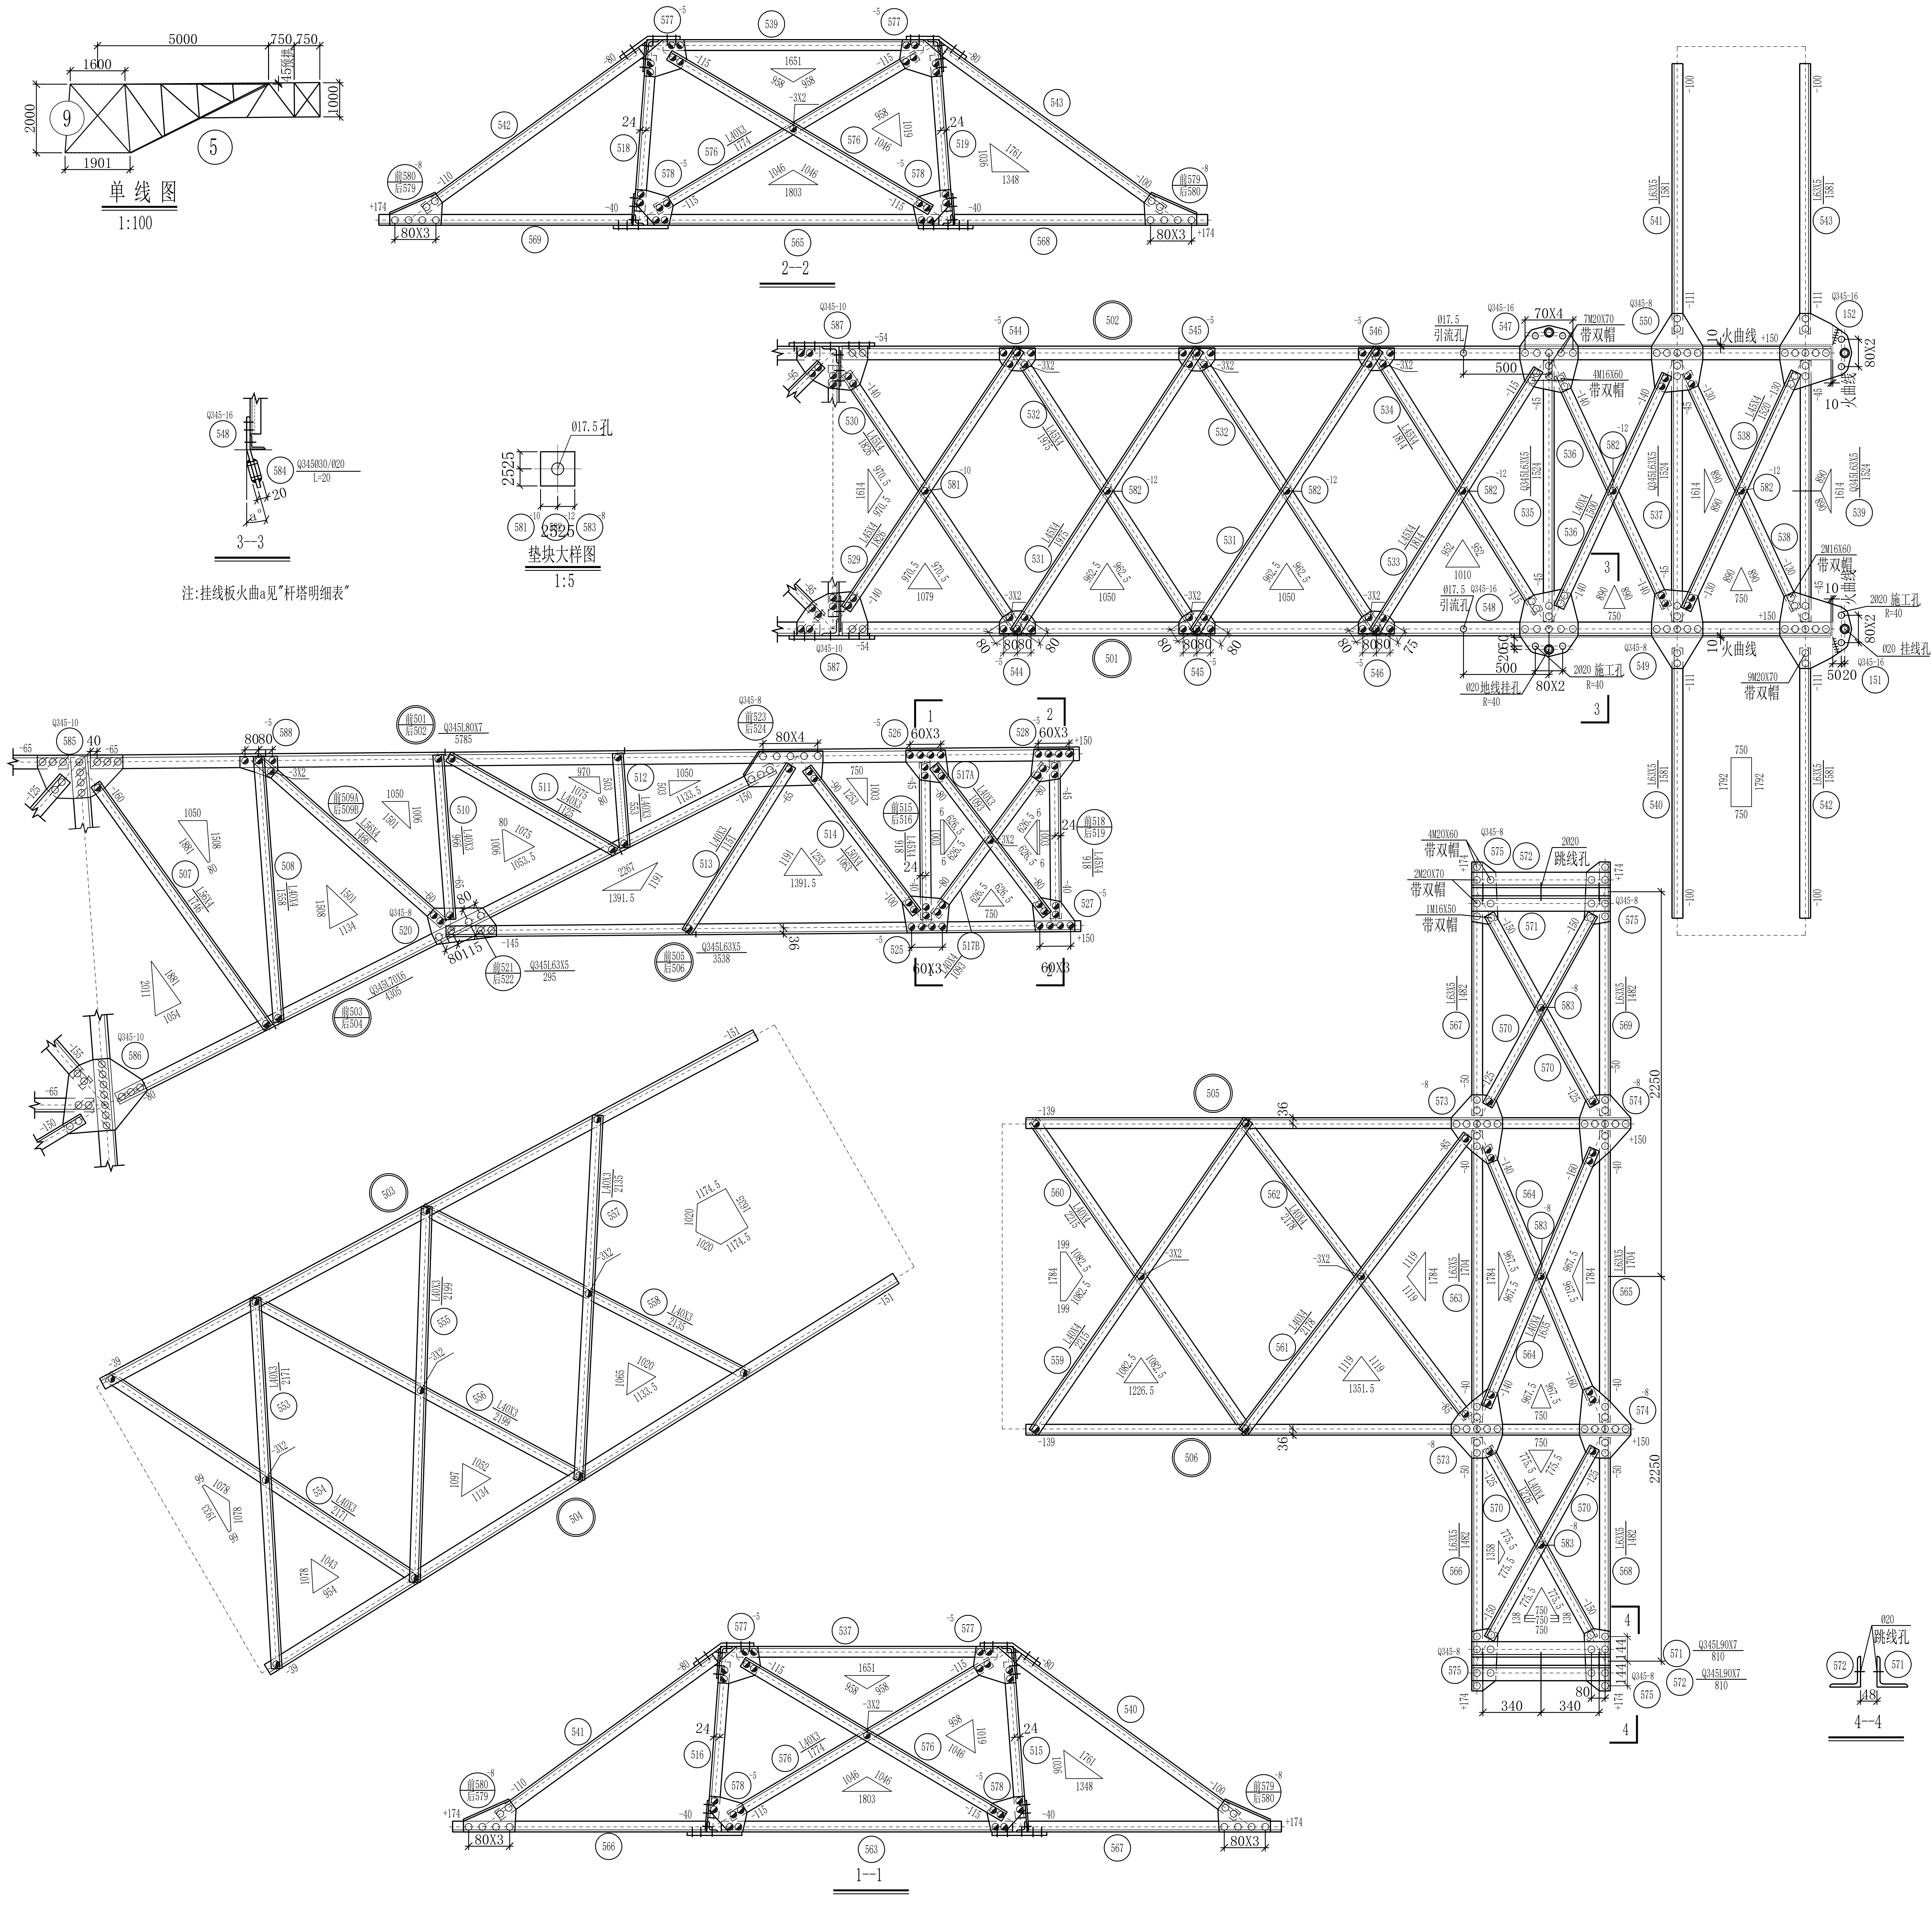

单线图

1:100

2--2

3--3

垫块大样图

1:5

注：挂线板火曲a见"杆塔明细表"

1--1

4--4

构 件 明 细 表

编号	规格	长度(mm)	数量	重量(kg) 一件	重量(kg) 小计	备注
569	L63X5	1482	1	7.15	7.2	
570	L40X4	1276	4	3.09	12.4	
571	Q345L90X7	810	2	7.82	15.6	
572	Q345L90X7	810	2	7.82	15.6	
573	-8X300	404	2	7.61	15.2	
574	-8X300	376	2	7.08	14.2	
575	Q345-8X153	365	4	3.51	14.0	
576	L40X3	1774	4	3.29	13.2	
577	-5X217	249	4	2.12	8.5	
578	-5X209	226	4	1.85	7.4	
579	-8X184	308	2	3.56	7.1	卷边50mm
580	-8X184	308	2	3.56	7.1	卷边50mm
581	-10X50	50	1	0.20	0.2	垫块
582	-12X50	50	5	0.24	1.2	垫块
583	-8X50	50	3	0.16	0.5	垫块
584	Q345Ø30/Ø20	20	4	0.06	0.2	焊接
585	Q345-10X269	500	2	10.56	21.1	
586	Q345-10X435	460	2	15.71	31.4	
587	Q345-10X247	415	2	8.05	16.1	
588	-5X116	220	2	1.00	2.0	
合计		810.1 kg				

螺栓、脚钉、垫圈明细表

名称	级别	规格	符号	数量	重量(kg)	备注
螺栓	6.8级	M16X40	◍	205	29.6	
		M16X50	⊘	47	7.5	
		M16X50	○	4	0.8	带双帽
		M16X60	○	12	2.4	带双帽
		M20X45	○	104	28.1	
		M20X55	⊘	62	18.3	
		M20X60	○	16	5.8	带双帽
		M20X70	○	40	15.5	带双帽
脚钉			⊖ ⊣			
垫圈	Q235	-3(Ø17.5)	规格X个数	34	0.3	
合计			108.3 kg			

构 件 明 细 表

编号	规格	长度(mm)	数量	重量(kg) 一件	重量(kg) 小计	备注
501	Q345L80X7	5785	1	49.32	49.3	局部开角
502	Q345L80X7	5785	1	49.32	49.3	局部开角
503	Q345L70X6	4305	1	27.58	27.6	切角 局部合角
504	Q345L70X6	4305	1	27.58	27.6	切角 局部合角
505	Q345L63X5	3538	1	17.06	17.1	局部合角
506	Q345L63X5	3538	1	17.06	17.1	局部合角
507	L56X4	1746	2	6.02	12.0	
508	L40X4	1558	2	3.77	7.5	
509A	L56X4	1466	1	5.05	5.1	切角
509B	L56X4	1466	1	5.05	5.1	切角
510	L40X3	966	2	1.79	3.6	
511	L40X3	1125	2	2.08	4.2	
512	L40X3	553	2	1.02	2.0	
513	L40X3	1151	2	2.13	4.3	
514	L50X4	1063	2	3.25	6.5	
515	L45X4	918	1	2.51	2.5	
516	L45X4	918	1	2.51	2.5	
517A	L40X3	1093	2	2.02	4.0	
517B	L40X4	1093	2	2.65	5.3	
518	L45X4	918	1	2.51	2.5	
519	L45X4	918	1	2.51	2.5	
520	Q345-8X268	360	2	6.06	12.1	
521	Q345L63X5	295	1	1.42	1.4	
522	Q345L63X5	295	1	1.42	1.4	
523	Q345-8X201	484	1	6.11	6.1	卷边50mm
524	Q345-8X201	484	1	6.11	6.1	卷边50mm
525	-5X216	276	2	2.34	4.7	
526	-5X193	250	2	1.89	3.8	
527	-5X200	247	2	1.94	3.9	
528	-5X193	250	2	1.89	3.8	
529	L45X4	1826	1	5.00	5.0	
530	L45X4	1826	1	5.00	5.0	切角
531	L45X4	1975	2	5.40	10.8	
532	L45X4	1975	2	5.40	10.8	切角
533	L45X4	1814	1	4.96	5.0	
534	L45X4	1814	1	4.96	5.0	切角
535	Q345L63X5	1524	1	7.35	7.4	
536	L40X4	1500	2	3.63	7.3	
537	Q345L63X5	1524	1	7.35	7.4	
538	L45X4	1520	2	4.16	8.3	
539	Q345L63X5	1524	1	7.35	7.4	
540	L63X5	1581	1	7.62	7.6	切角
541	L63X5	1581	1	7.62	7.6	切角
542	L63X5	1581	1	7.62	7.6	切角
543	L63X5	1581	1	7.62	7.6	切角
544	-5X128	210	2	1.06	2.1	
545	-5X128	210	2	1.06	2.1	
546	-5X126	210	2	1.04	2.1	
547	Q345-16X340	380	1	16.23	16.2	火曲 焊接
548	Q345-16X340	380	1	16.23	16.2	火曲 焊接
549	Q345-8X300	462	1	8.70	8.7	火曲
550	Q345-8X300	462	1	8.70	8.7	火曲
551	Q345-16X390	425	1	20.82	20.8	火曲 割豁补焊
552	Q345-16X390	425	1	20.82	20.8	火曲 割豁补焊
553	L40X3	2171	1	4.02	4.0	
554	L40X3	2171	1	4.02	4.0	切角
555	L40X3	2199	1	4.07	4.1	
556	L40X3	2199	1	4.07	4.1	切角
557	L40X3	2135	1	3.95	4.0	
558	L40X3	2135	1	3.95	4.0	切角
559	L40X4	2215	1	5.36	5.4	
560	L40X4	2215	1	5.36	5.4	切角
561	L40X4	2178	1	5.28	5.3	
562	L40X4	2178	1	5.28	5.3	切角
563	L63X5	1704	1	8.22	8.2	
564	L40X4	1635	2	3.96	7.9	
565	L63X5	1704	1	8.22	8.2	
566	L63X5	1482	1	7.15	7.2	
567	L63X5	1482	1	7.15	7.2	
568	L63X5	1482	1	7.15	7.2	

甘肃电通电力工程设计咨询有限公司

甘肃庆阳能化电厂330千伏送出工程 工程		施工图	设计阶段
批 准	曹晓青	曹晓青	330-KC22D-DJ终端塔 ⑤ (40°-90°)内角侧地线支架结构图
审 核	王公阳	王公阳	
	丁国鹏	丁国鹏	
校 核	王文军		
设 计	段增强	段增强	
CAD 制图	段增强	段增强	
比 例			
日 期	2026年7月	图 号	330-KC22D-DJ-06