



单线图


1:100

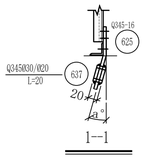

注:挂线板火曲a见"杆塔明细表"

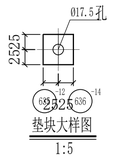

1:5

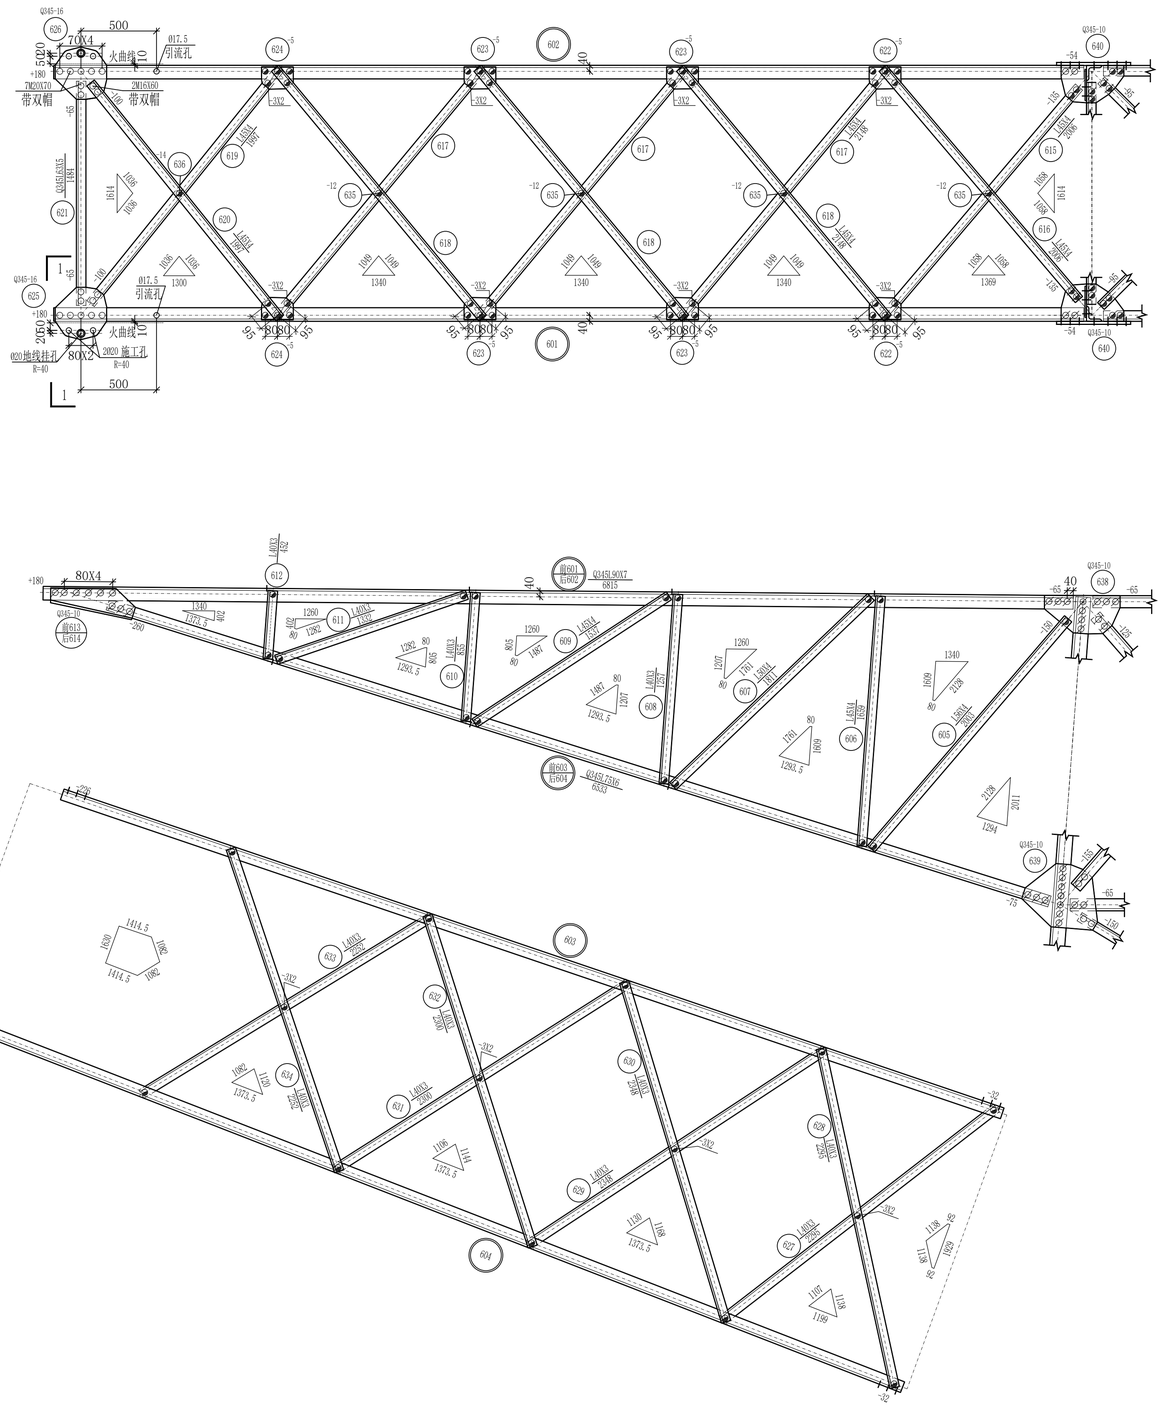

构 件 明 细 表

编号	规 格	长 度 (mm)	数量	重 量 (kg) 一 件	重 量 (kg) 小 计	备 注
601	Q345L90X7	6815	1	65.81	65.8	局部开角
602	Q345L90X7	6815	1	65.81	65.8	局部开角
603	Q345L75X6	6533	1	45.11	45.1	切角 局部合角
604	Q345L75X6	6533	1	45.11	45.1	切角 局部合角
605	L56X4	2003	2	6.90	13.8	
606	L45X4	1659	2	4.54	9.1	
607	L50X4	1811	2	5.54	11.1	
608	L40X3	1257	2	2.33	4.7	
609	L45X4	1537	2	4.21	8.4	
610	L40X3	855	2	1.58	3.2	
611	L40X3	1332	2	2.47	4.9	
612	L40X3	452	2	0.84	1.7	
613	Q345-10X185	569	1	8.26	8.3	卷边60mm
614	Q345-10X185	569	1	8.26	8.3	卷边60mm
615	L45X4	2006	1	5.49	5.5	切角
616	L45X4	2006	1	5.49	5.5	
617	L45X4	2148	3	5.88	17.6	切角
618	L45X4	2148	3	5.88	17.6	
619	L45X4	1997	1	5.46	5.5	切角
620	L45X4	1997	1	5.46	5.5	
621	Q345L63X5	1484	1	7.16	7.2	
622	-5X156	210	2	1.29	2.6	
623	-5X156	210	4	1.29	5.2	
624	-5X157	210	2	1.29	2.6	
625	Q345-16X330	340	1	14.09	14.1	火曲 焊接
626	Q345-16X330	340	1	14.09	14.1	火曲 焊接
627	L40X3	2295	1	4.25	4.2	切角
628	L40X3	2295	1	4.25	4.2	
629	L40X3	2348	1	4.35	4.4	切角
630	L40X3	2348	1	4.35	4.4	
631	L40X3	2300	1	4.26	4.3	切角
632	L40X3	2300	1	4.26	4.3	
633	L40X3	2252	1	4.17	4.2	切角
634	L40X3	2252	1	4.17	4.2	
635	-12X50	50	4	0.24	1.0	垫块
636	-14X50	50	1	0.27	0.3	垫块
637	Q345030/020	20	2	0.06	0.1	焊接
638	Q345-10X269	500	2	10.56	21.1	
639	Q345-10X435	460	2	15.71	31.4	
640	Q345-10X247	415	2	8.05	16.1	
合 计		502.5 kg				

螺栓、脚钉、垫圈明细表

名称	级别	规 格	符号	数量	重量(kg)	备 注
螺栓	6.8级	M16X40	◪	68	9.8	
		M16X50	⊘	39	6.2	
		M16X60	○	4	0.8	带双帽
		M20X45	○	4	1.1	
		M20X55	⊘	74	21.9	
		M20X70	○	14	5.4	带双帽
脚钉			⊕			
垫圈	Q235	-3(Ø17.5)	规格X个数	24	0.3	
合 计			45.5 kg			

甘肃电通电力工程设计咨询有限公司			
甘肃庆阳能化电厂330千伏送出工程	工程	施工图	设计阶段
批 准	曹晓青		330-KC22D-DJ终端塔 6
审 核	王公阳		
	丁国鹏		
校 核	王文军		
设 计	段增强		(0°-90°)外角侧地线支架结构图
CAD 制图	段增强		
比 例			
日 期	2026年7月	图 号	330-KC22D-DJ-07