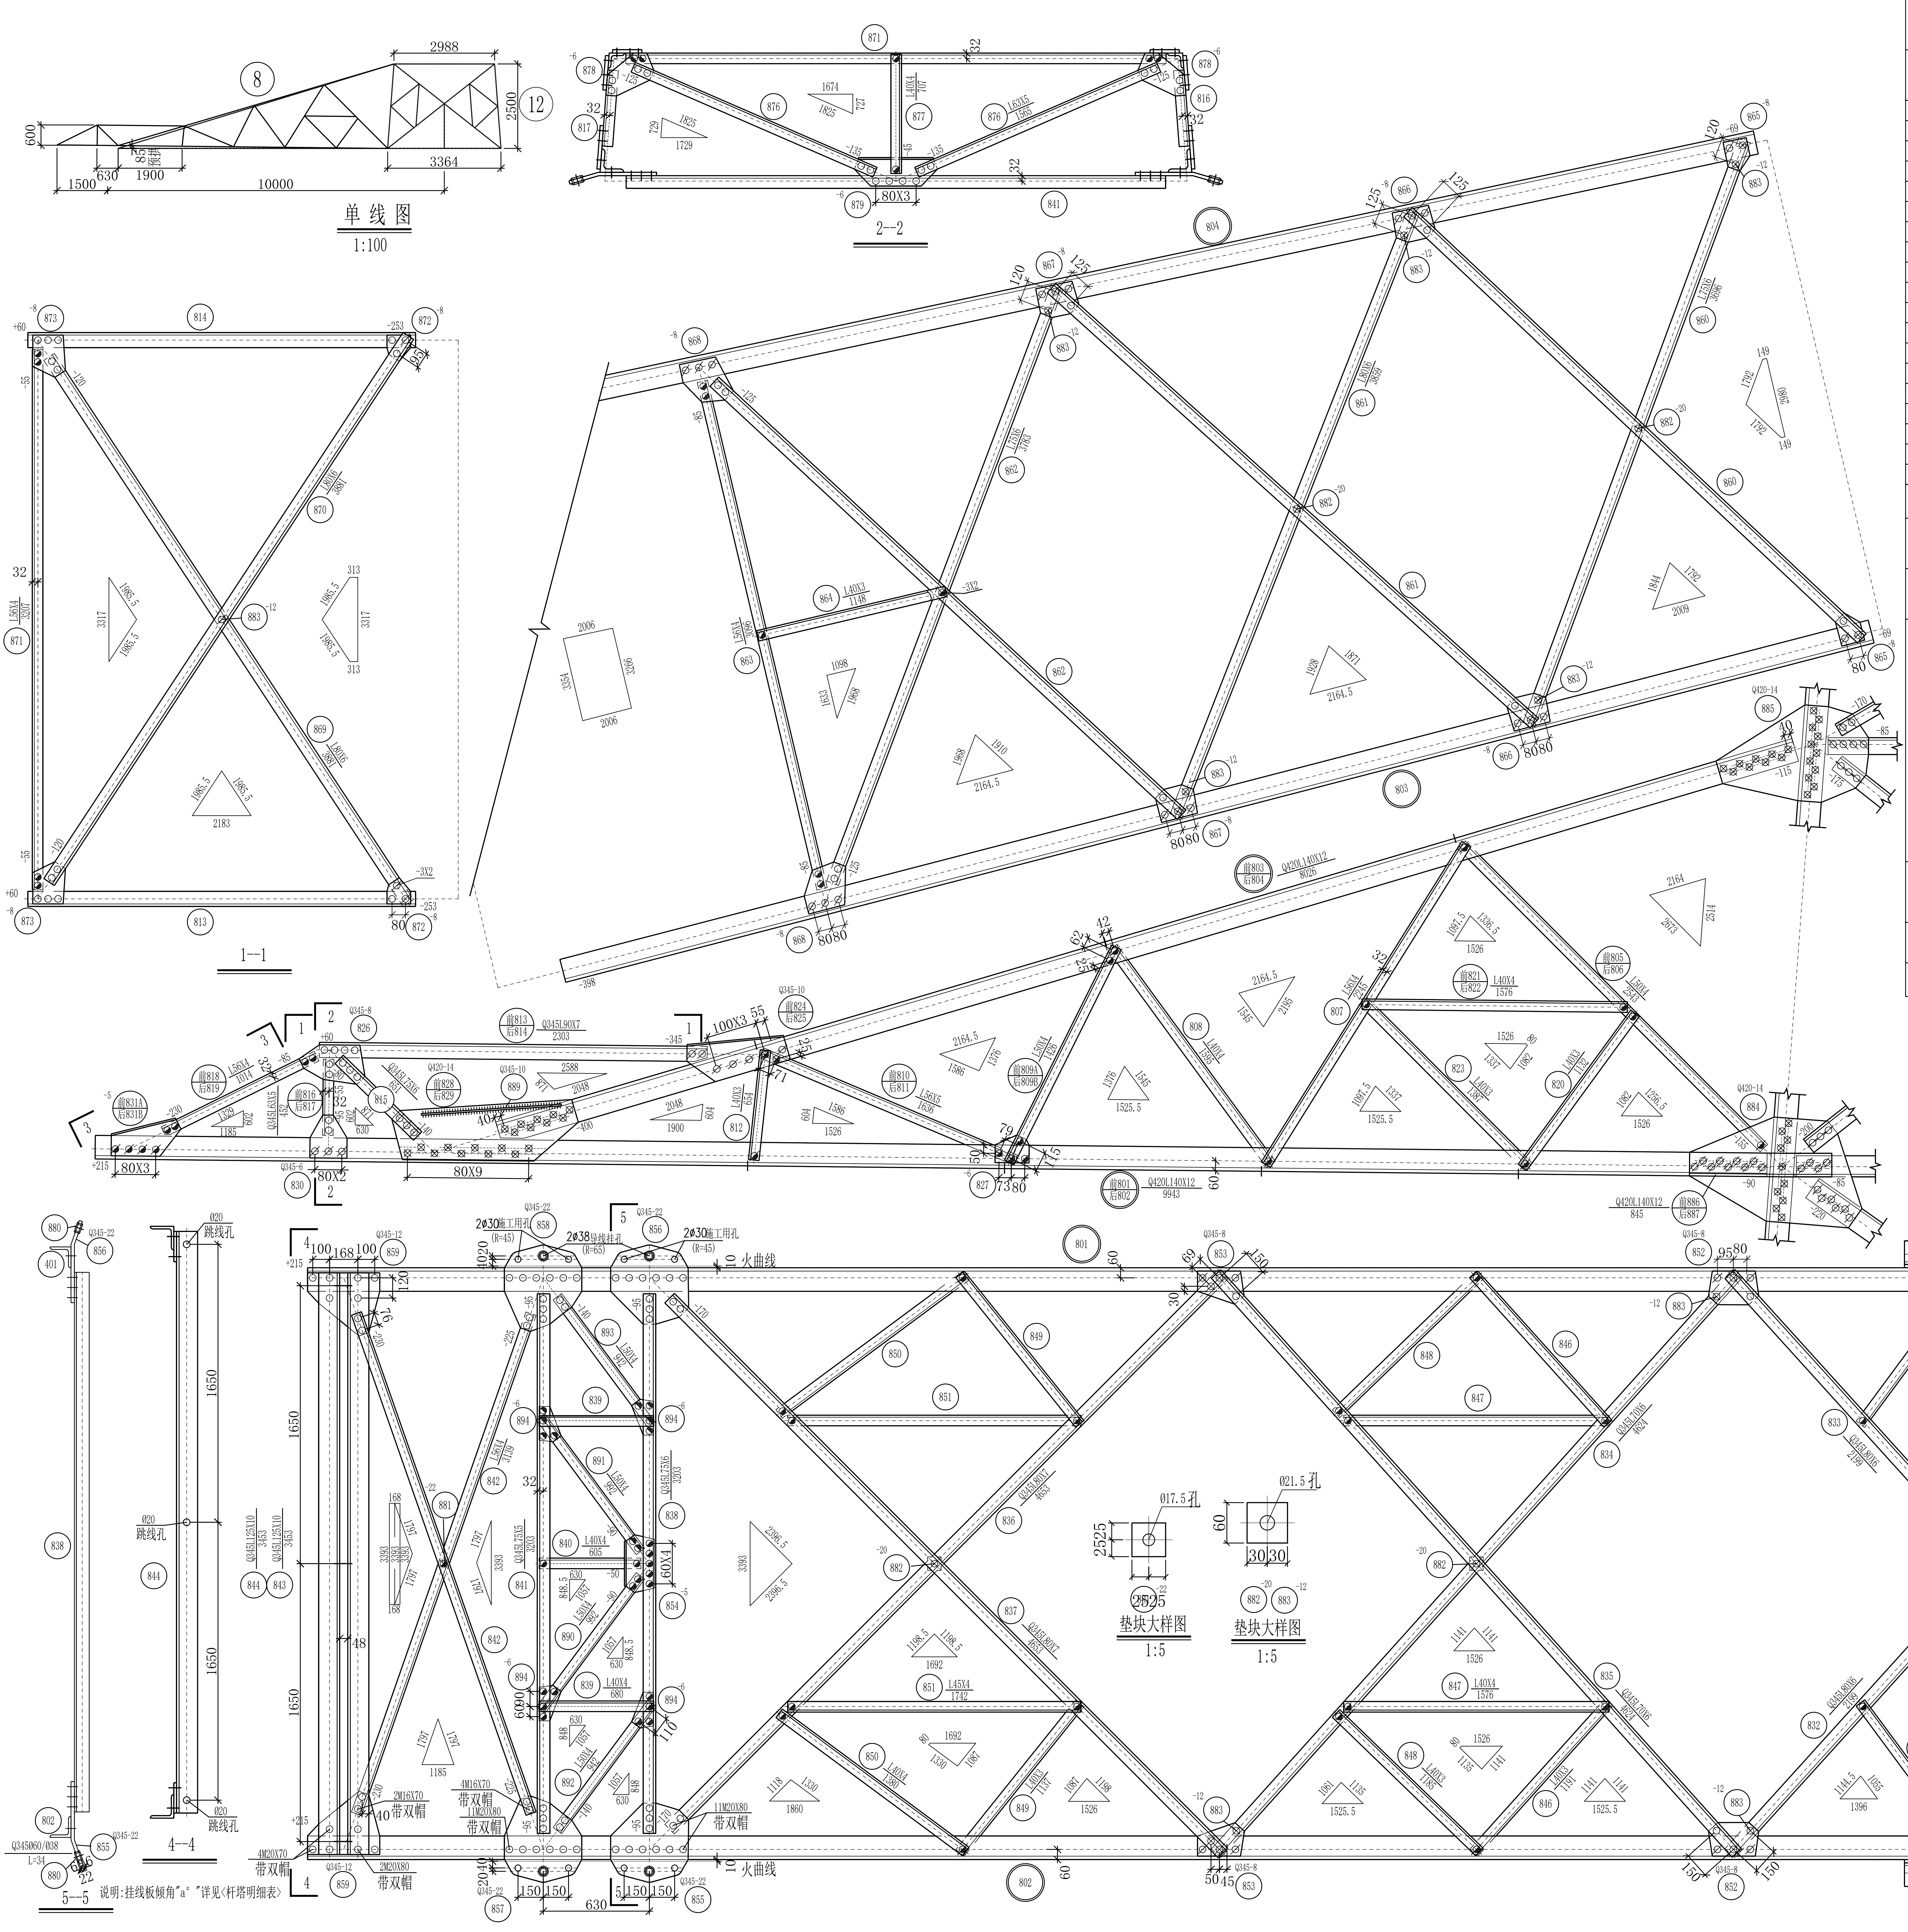

说明:挂线板倾角"a°"详见《杆塔明细表》

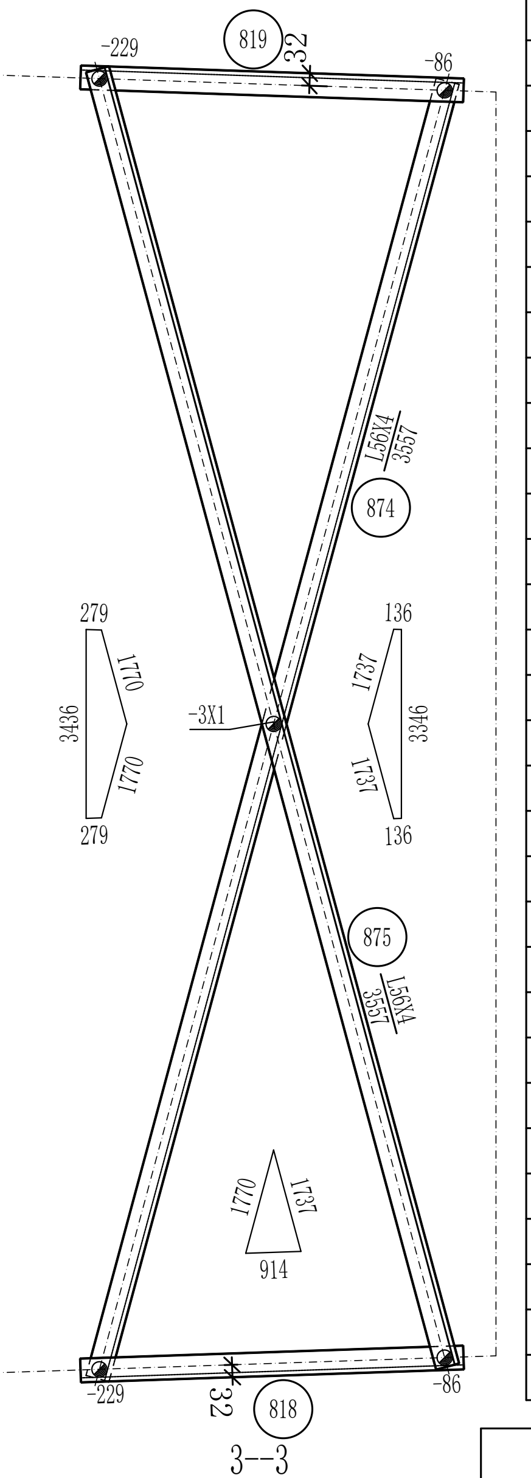

3--3

构　件　明　细　表

编号	规　格	长度 (mm)	数量	重量(kg) 一件	重量(kg) 小计	备　注
876	L63X5	1565	2	7.55	15.1	
877	L40X4	707	1	1.71	1.7	
878	-6X255	313	2	3.76	7.5	
879	-6X209	494	1	4.86	4.9	卷边50mm
880	Q345Ø60/Ø38	34	4	0.45	1.8	焊接
881	-22X50	50	1	0.43	0.4	垫块
882	-20X60	60	4	0.57	2.3	垫块
883	-12X60	60	9	0.34	3.1	垫块
884	Q420-14X615	1035	2	69.95	139.9	
885	Q420-14X570	920	2	57.63	115.3	
886	Q420L140X12	845	1	21.56	21.6	
887	Q420L140X12	845	1	21.56	21.6	
888	Q345-8X389	410	1	10.02	10.0	
889	Q345-10X60	830	2	3.91	7.8	焊接
890	L50X4	992	2	3.34	6.7	
891	L50X4	992	2	4.77	9.5	
892	L50X4	942	2	3.34	6.7	
893	L50X4	942	2	4.77	9.5	
894	-6X130	212	4	1.30	5.2	
合　计	2529.0　kg					

螺栓、脚钉、垫圈明细表

名称	级别	规　格	符号	数量	重量(kg)	备　注
螺栓	6.8级	M16X40	⊘	64	9.2	
		M16X50	⊘	39	6.2	
		M16X60	⊗	10	1.8	
		M16X70	○	12	2.6	带双帽
		M20X45	○	77	20.8	
		M20X55	⊘	88	26.0	
		M20X65	⊗	120	38.5	
		M20X75	⊘	28	9.7	
		M20X70	○	8	3.1	带双帽
		M20X80	○	44	18.1	带双帽
脚钉						
垫圈	Q235	-3(Ø17.5)	规格X个数	3	0.0	
		-3(Ø22)		2	0.0	
合　计			136.0　kg			

构　件　明　细　表

编号	规　格	长度 (mm)	数量	重量(kg) 一件	重量(kg) 小计	备　注
801	Q420L140X12	9943	1	253.77	253.8	局部合角
802	Q420L140X12	9943	1	253.77	253.8	局部合角
803	Q420L140X12	8026	1	204.84	204.8	切角 局部开角
804	Q420L140X12	8026	1	204.84	204.8	切角 局部开角
805	L50X4	2543	1	7.78	7.8	
806	L50X4	2543	1	7.78	7.8	
807	L56X4	2245	2	7.74	15.5	
808	L40X4	1595	2	3.86	7.7	
809A	L50X4	1426	1	4.36	4.4	
809B	L50X4	1426	1	4.36	4.4	
810	L56X5	1636	1	6.95	7.0	
811	L56X5	1636	1	6.95	7.0	
812	L40X3	654	2	1.21	2.4	
813	Q345L90X7	2303	1	22.24	22.2	切角 局部开角
814	Q345L90X7	2303	1	22.24	22.2	切角 局部开角
815	Q345L75X6	651	2	4.50	9.0	
816	Q345L63X5	452	1	2.18	2.2	
817	Q345L63X5	452	1	2.18	2.2	
818	L56X4	1014	1	3.49	3.5	切角
819	L56X4	1014	1	3.49	3.5	切角
820	L40X3	1132	2	2.10	4.2	
821	L40X4	1576	1	3.82	3.8	切角
822	L40X4	1576	1	3.82	3.8	切角
823	L40X3	1387	2	2.57	5.1	
824	Q345-10X371	723	1	21.06	21.1	卷边60mm
825	Q345-10X371	723	1	21.06	21.1	卷边60mm
826	Q345-8X205	360	2	4.63	9.3	
827	-6X165	203	2	1.58	3.2	
828	Q420-14X400	1010	1	44.40	44.4	焊接
829	Q420-14X400	1010	1	44.40	44.4	焊接
830	Q345-6X220	255	2	2.64	5.3	
831A	-5X246	447	1	4.32	4.3	卷边50mm
831B	-5X246	447	1	4.32	4.3	卷边50mm
832	Q345L80X6	2199	1	16.22	16.2	切角
833	Q345L80X6	2199	1	16.22	16.2	
834	Q345L70X6	4624	1	29.62	29.6	切角
835	Q345L70X6	4624	1	29.62	29.6	
836	Q345L80X7	4653	1	39.67	39.7	切角
837	Q345L80X7	4653	1	39.67	39.7	
838	Q345L75X6	3203	1	22.12	22.1	
839	L40X4	680	2	1.65	3.3	
840	L40X4	605	1	1.47	1.5	
841	Q345L75X5	3203	1	18.64	18.6	
842	L56X4	3139	2	10.82	21.6	
843	Q345L125X10	3453	1	66.07	66.1	
844	Q345L125X10	3453	1	66.07	66.1	
845	L40X3	1105	2	2.05	4.1	
846	L40X3	1191	2	2.21	4.4	
847	L40X4	1576	2	3.82	7.6	切角
848	L40X3	1185	2	2.19	4.4	
849	L40X3	1137	2	2.11	4.2	
850	L40X4	1380	2	3.34	6.7	
851	L45X4	1742	2	4.77	9.5	切角
852	Q345-8X244	334	2	5.12	10.2	
853	Q345-8X243	317	2	4.84	9.7	
854	-5X228	345	1	3.09	3.1	卷边50mm
855	Q345-22X460	470	1	37.34	37.3	火曲 焊接
856	Q345-22X460	470	1	37.34	37.3	火曲 焊接
857	Q345-22X460	470	1	37.34	37.3	火曲 焊接
858	Q345-22X460	470	1	37.34	37.3	火曲 焊接
859	Q345-12X374	428	2	15.08	30.2	
860	L75X6	3696	2	25.52	51.0	
861	L80X6	3859	2	28.46	56.9	
862	L75X6	3783	2	26.12	52.2	
863	L56X4	3096	1	10.67	10.7	
864	L40X3	1148	1	2.13	2.1	一端压扁
865	-8X174	238	2	2.60	5.2	
866	-8X188	323	2	3.81	7.6	
867	-8X192	324	2	3.91	7.8	
868	-8X262	283	2	4.66	9.3	
869	L80X6	3881	1	28.63	28.6	切角
870	L80X6	3881	1	28.63	28.6	
871	L56X4	3207	1	11.05	11.0	
872	-8X140	156	2	1.37	2.7	
873	-8X197	251	2	3.11	6.2	
874	L56X4	3557	1	12.26	12.3	切角
875	L56X4	3557	1	12.26	12.3	

甘肃电通电力工程设计咨询有限公司

甘肃庆阳能化电厂330千伏送出工程　工程		施工图	设计阶段
批　准	曹晓青	曹晓青	330-KC22D-DJ终端塔(40°-90°) ⑧ 外角侧横担结构图
审　核	王公阳	王公阳	
	丁国鹏	丁国鹏	
校　核	王文军	王文军	
设　计	段增强	段增强	
CAD 制图	段增强	段增强	
比　例			
日　期	2026年7月	图　号	330-KC22D-J4-09