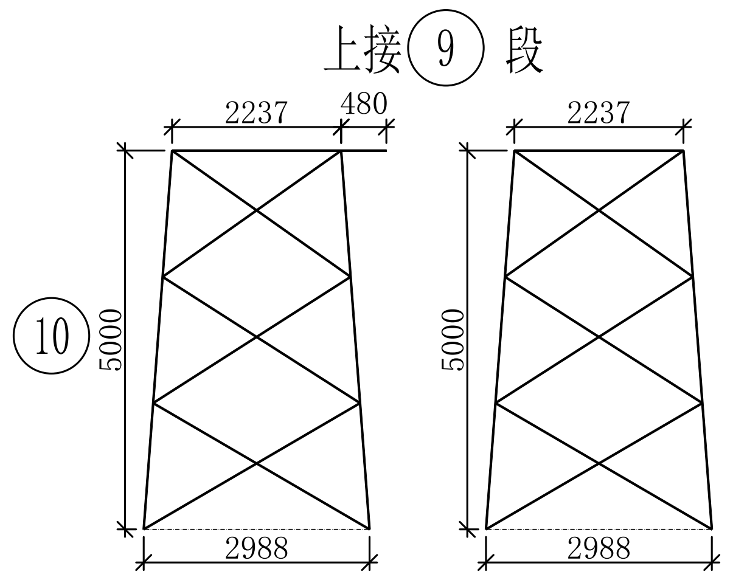

单线图

1:100

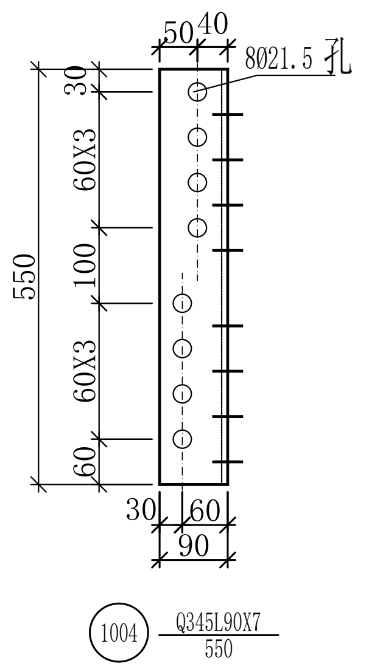

连接角钢大样图

1:10

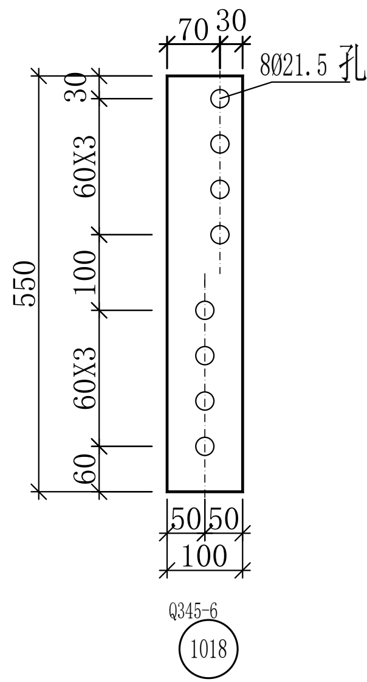

包钢板大样图

1:10

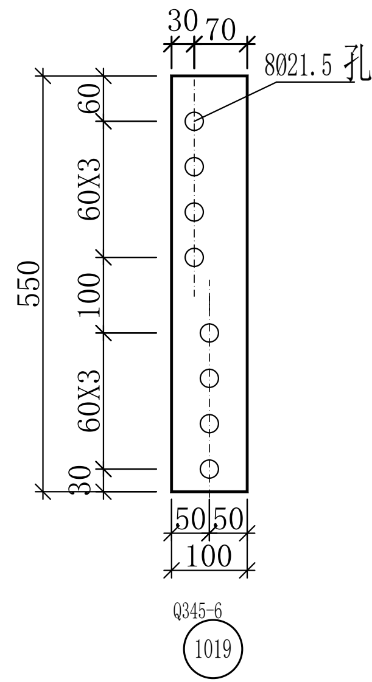

包钢板大样图

1:10

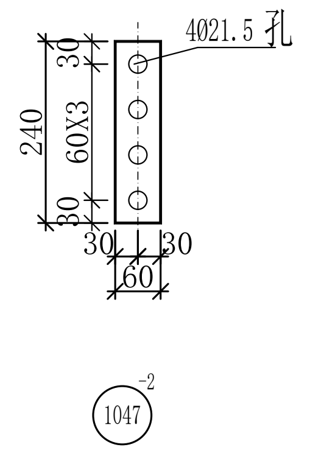

垫板大样图

1:5

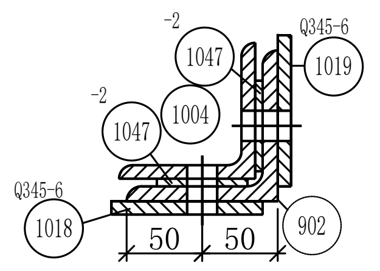

3—3

1:5

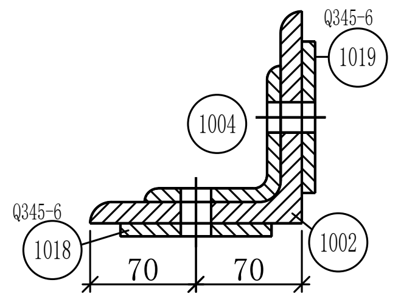

4—4

1:5

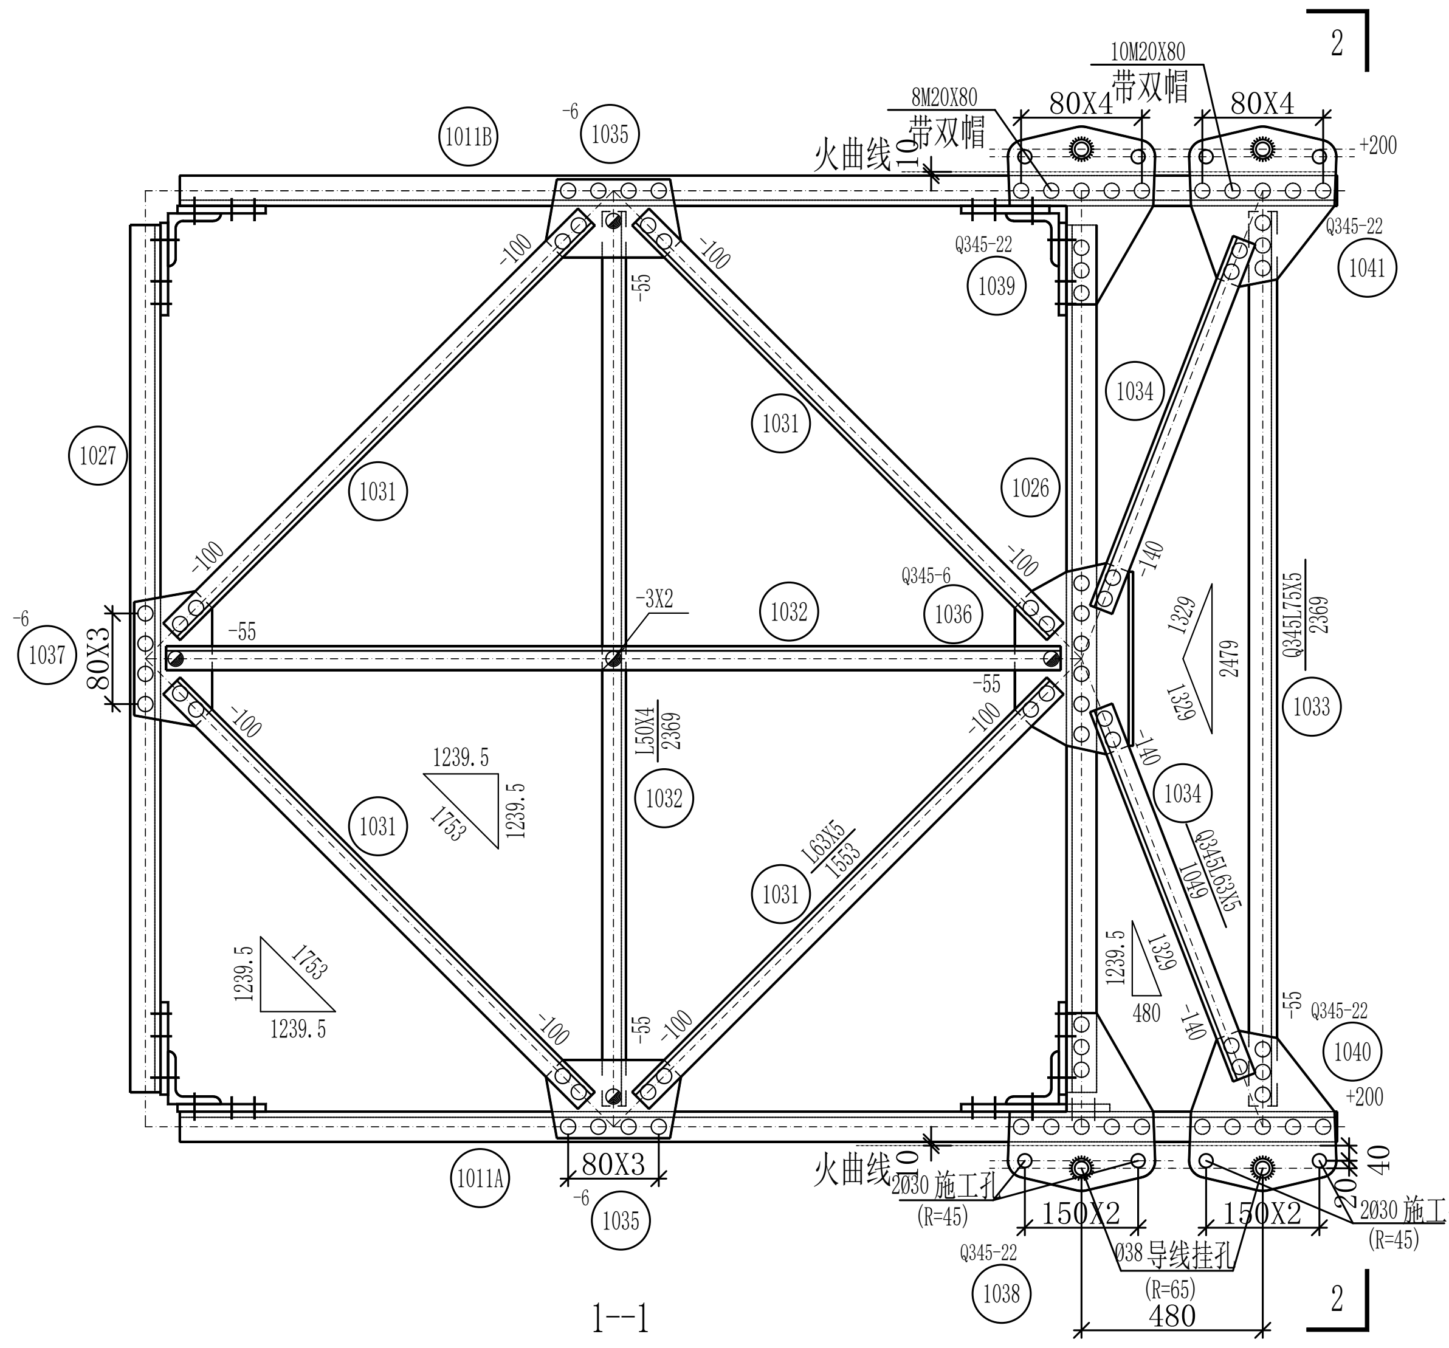

1--1

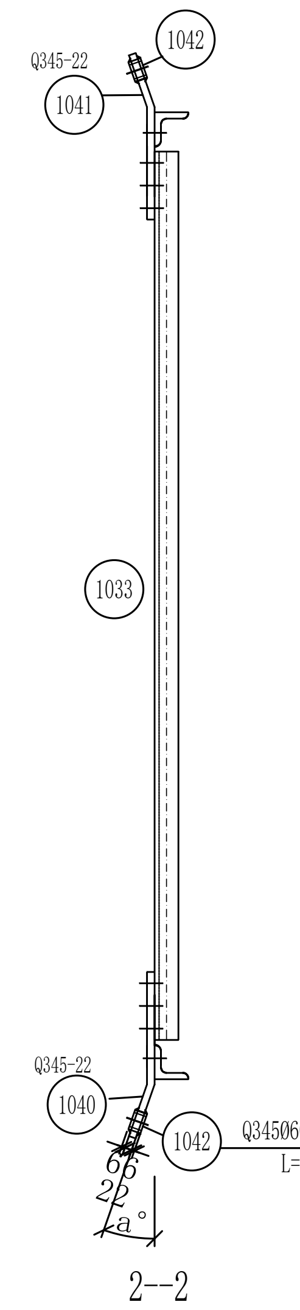

2--2

说明:挂线板倾角"a°"详见<杆塔明细表>

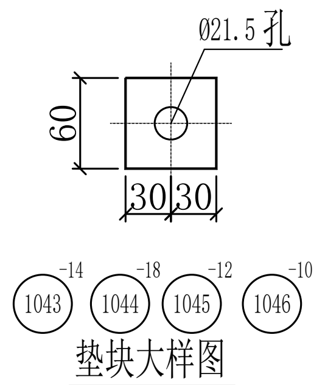

垫块大样图

1:5

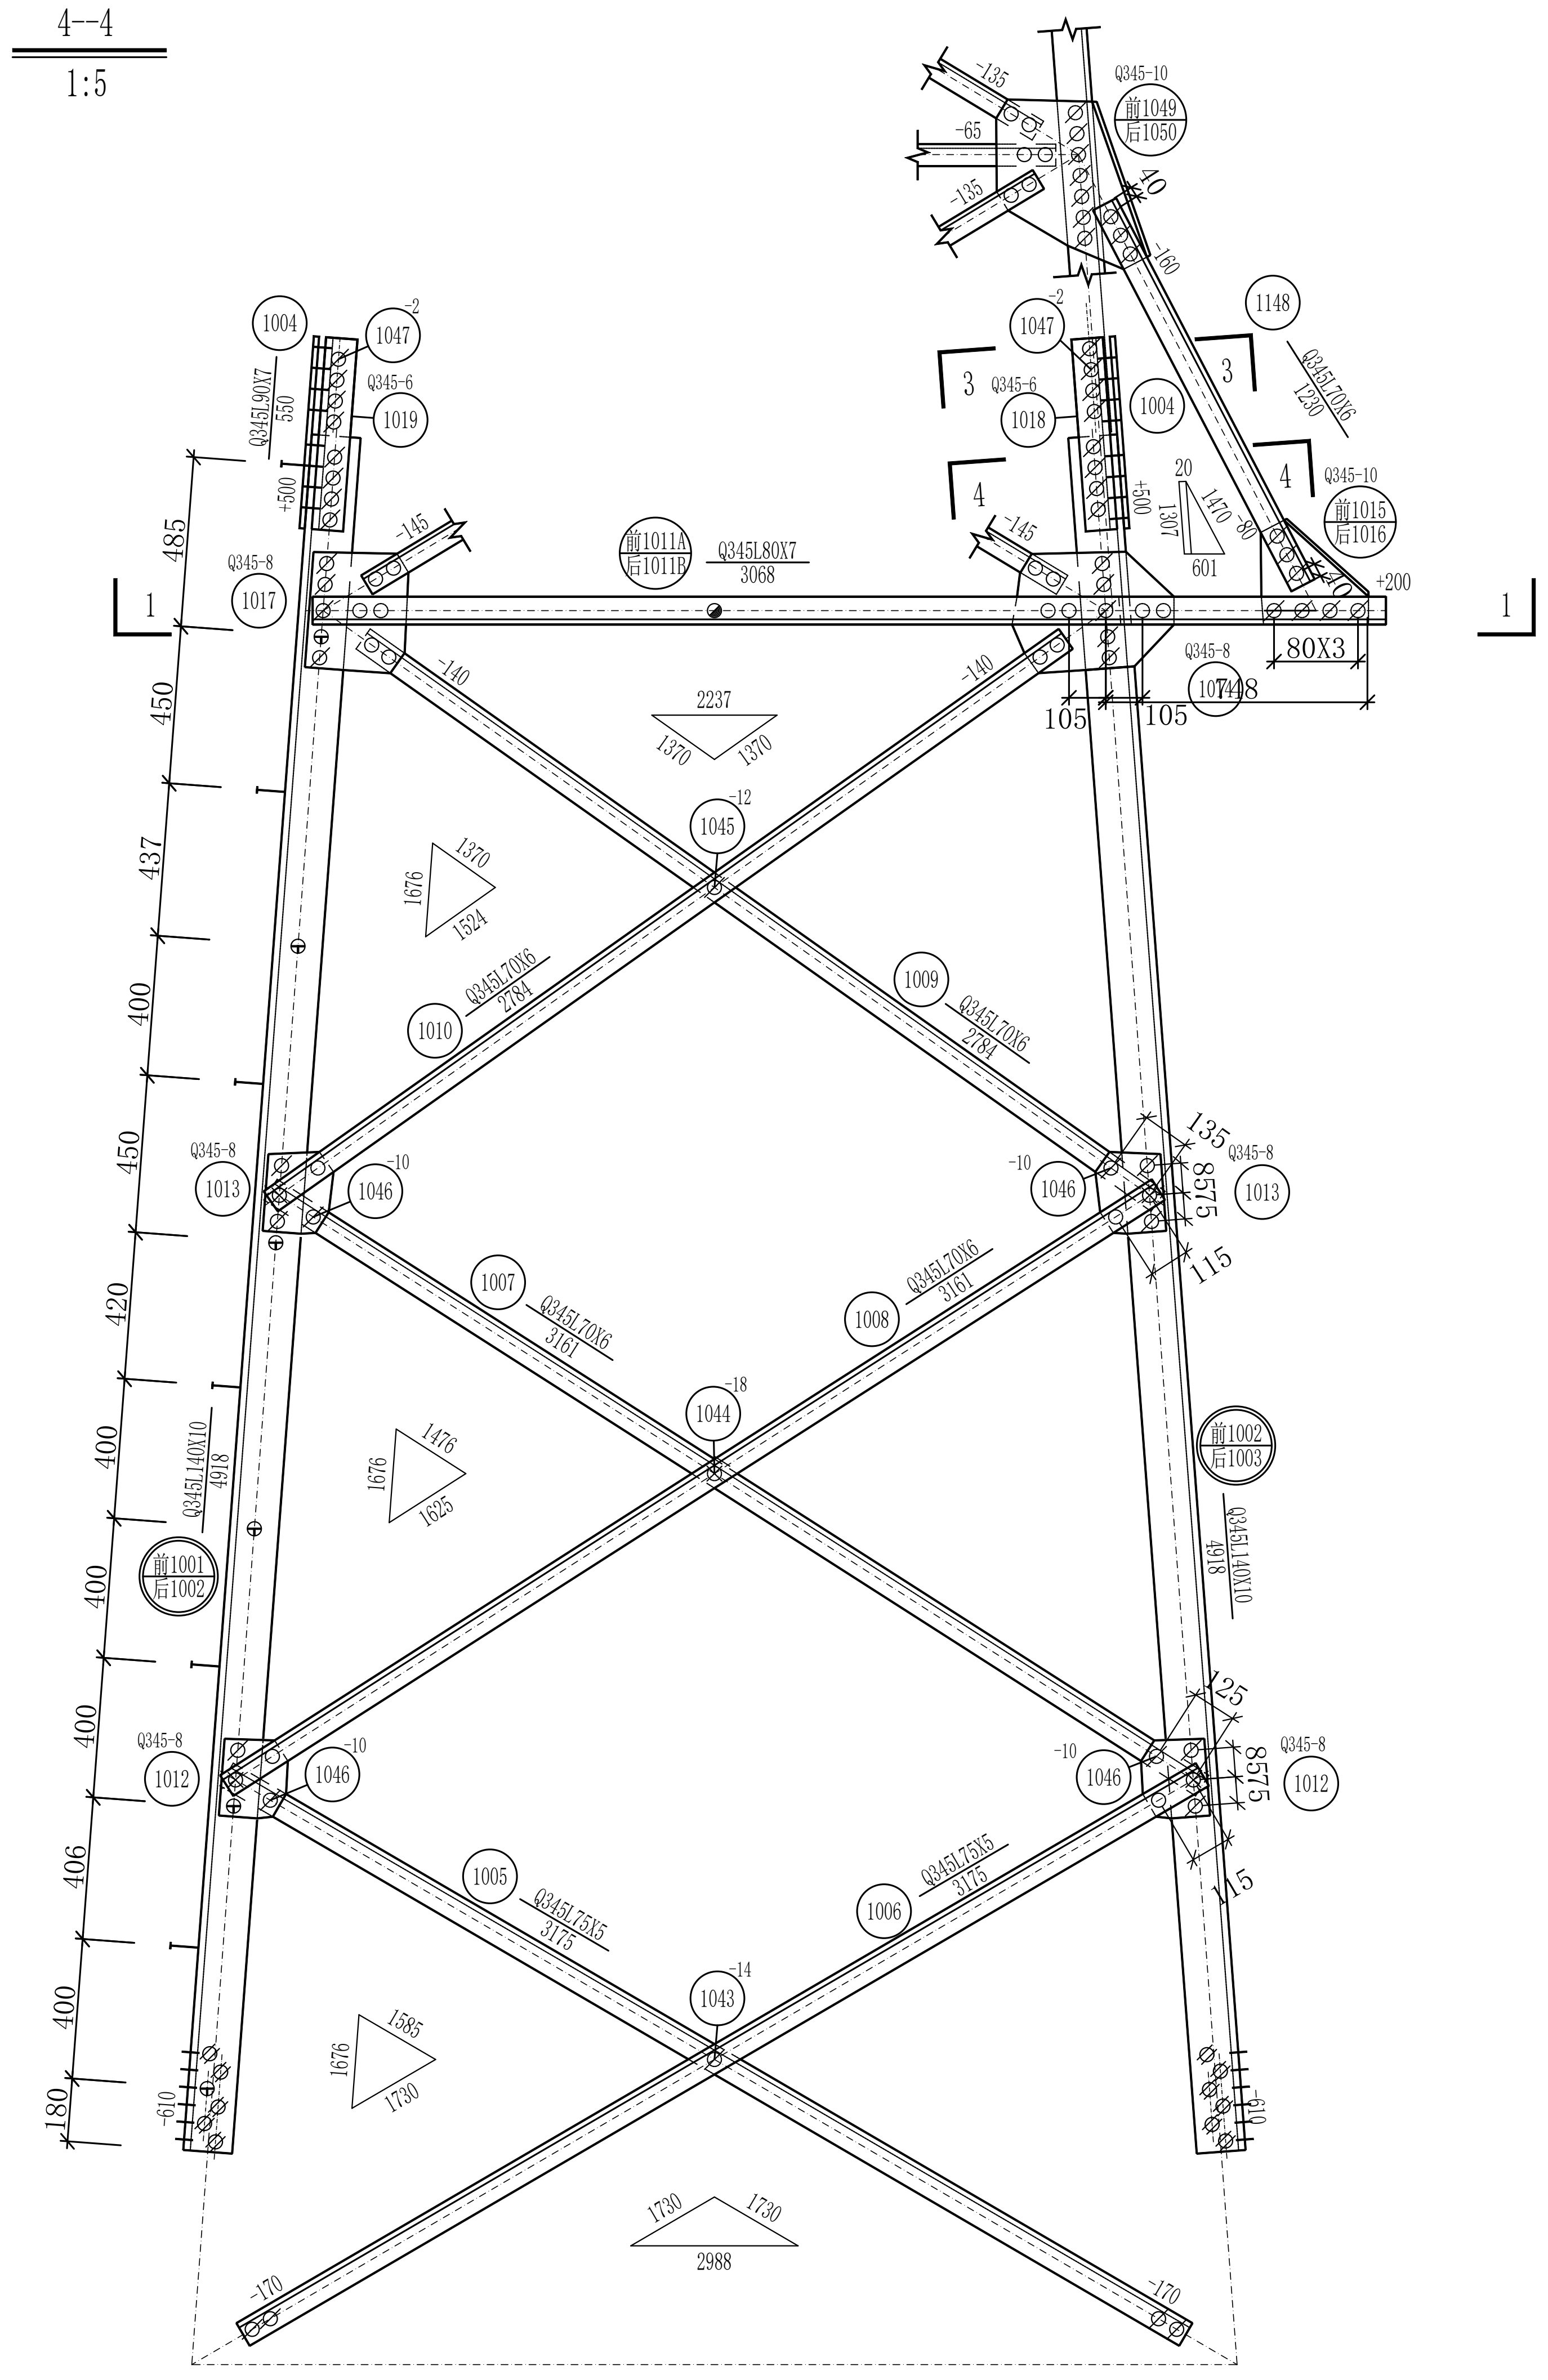

正面图

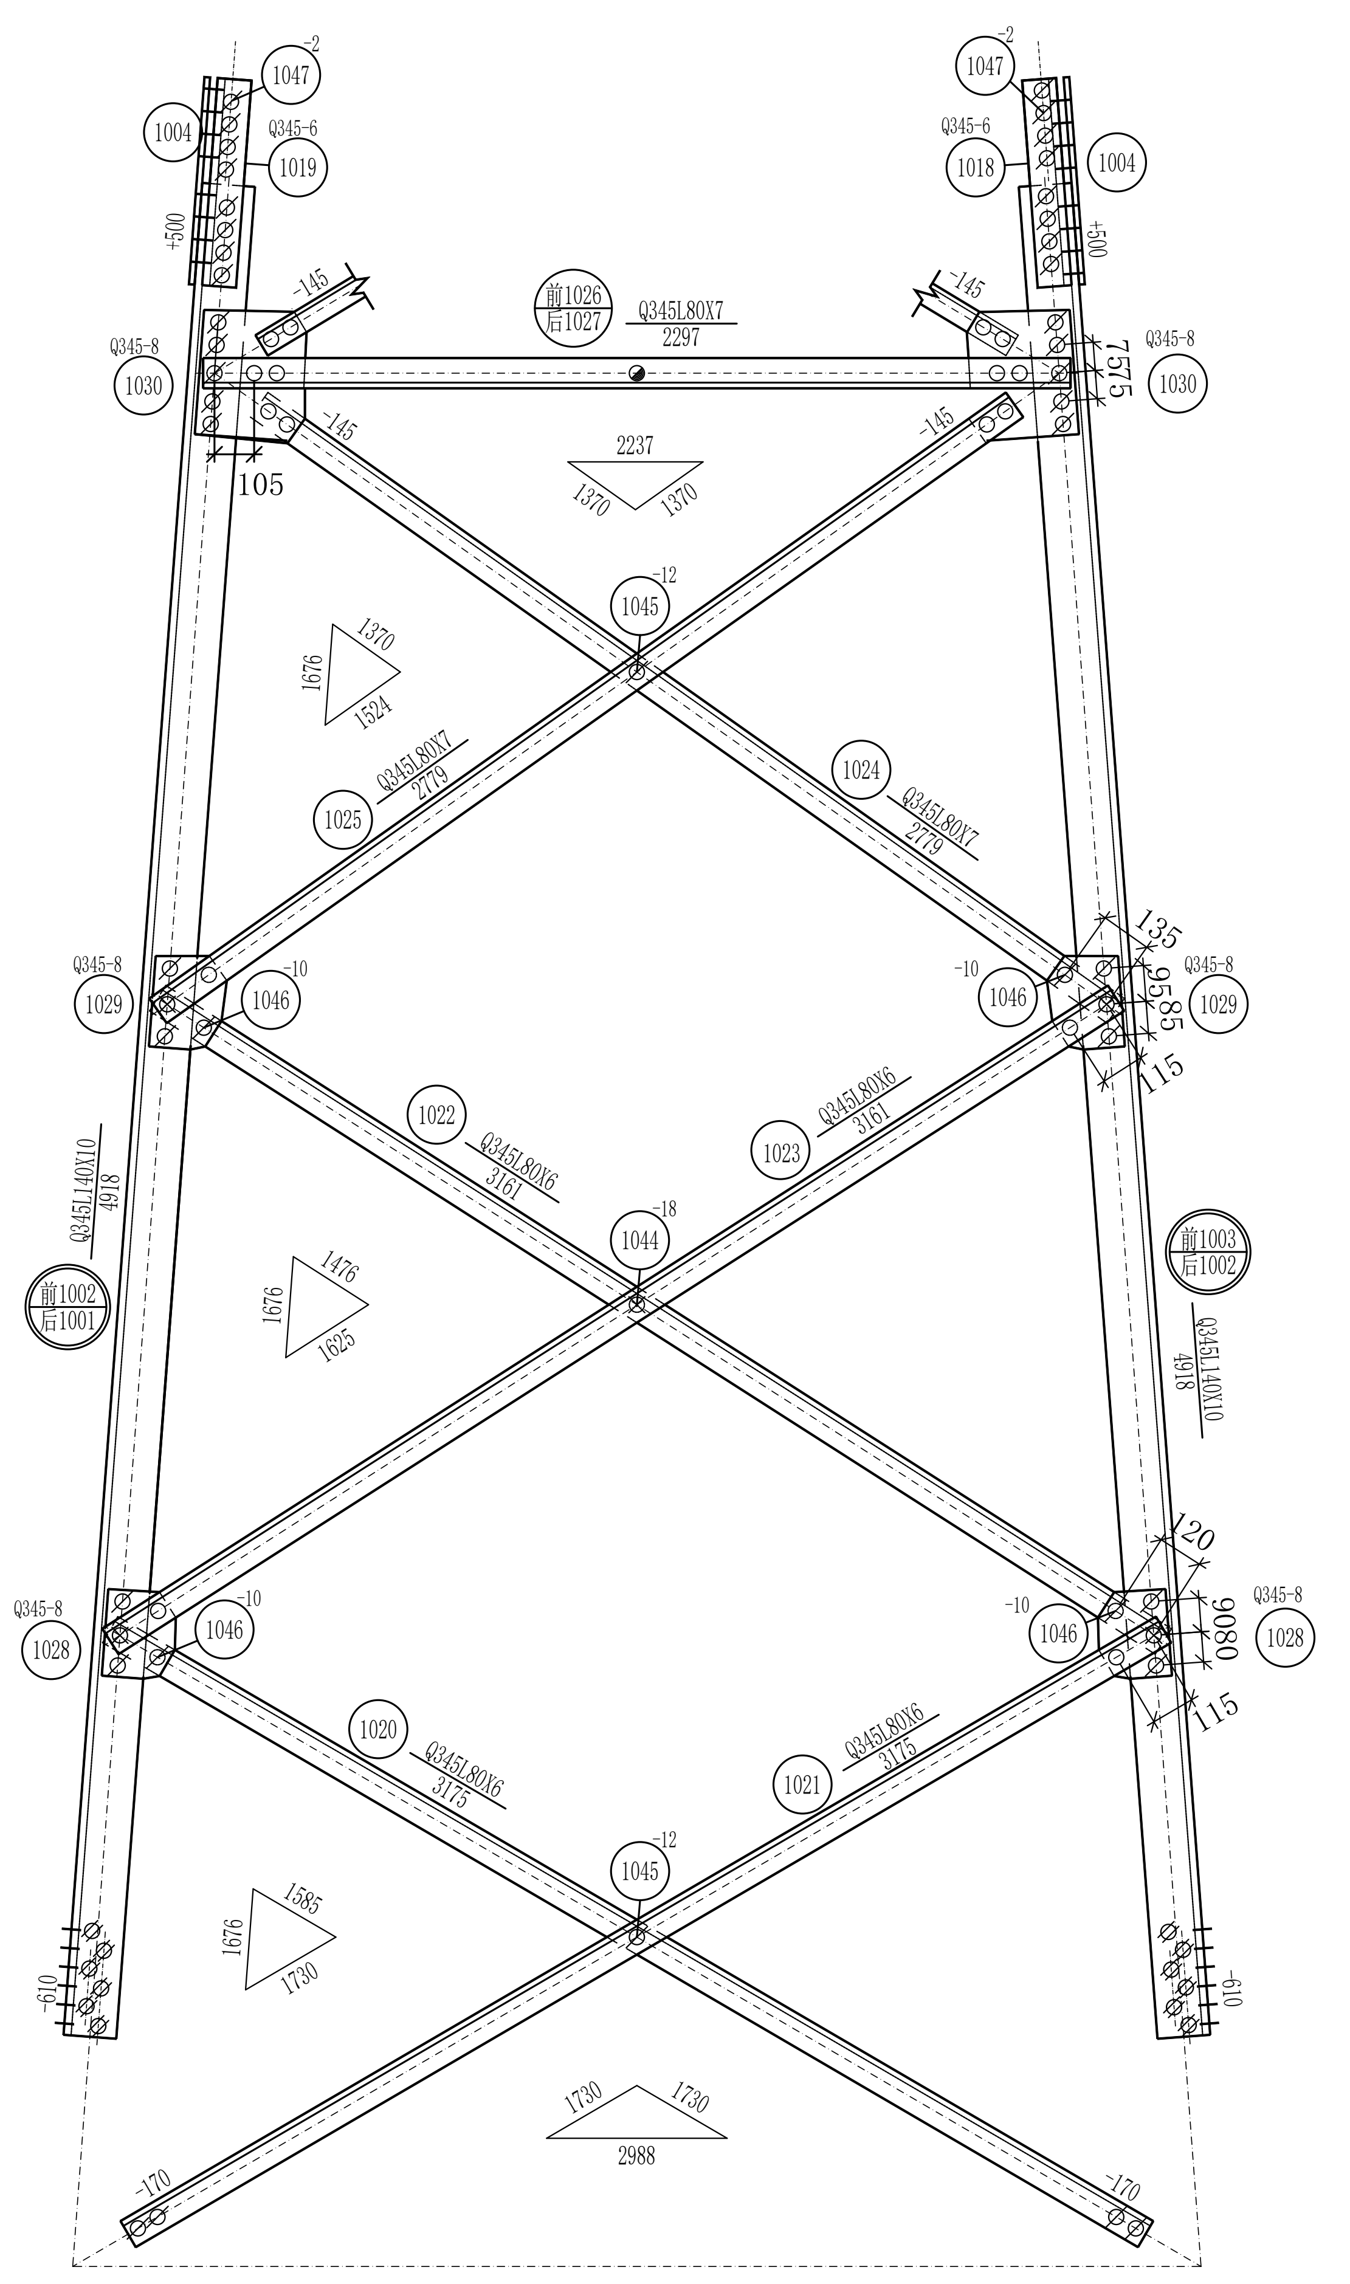

侧面图

构件明细表

编号	规格	长度(mm)	数量	重量(kg) 一件	重量(kg) 小计	备注
1001	Q345L140X10	4918	1	105.68	105.7	带脚钉
1002	Q345L140X10	4918	2	105.68	211.4	
1003	Q345L140X10	4918	1	105.68	105.7	
1004	Q345L90X7	550	4	5.31	21.2	铲背
1005	Q345L75X5	3175	2	18.47	36.9	切角
1006	Q345L75X5	3175	2	18.47	36.9	
1007	Q345L70X6	3161	2	20.25	40.5	切角
1008	Q345L70X6	3161	2	20.25	40.5	
1009	Q345L70X6	2784	2	17.83	35.7	切角
1010	Q345L70X6	2784	2	17.83	35.7	
1011A	Q345L80X7	3068	1	26.15	26.2	
1011B	Q345L80X7	3068	1	26.15	26.2	
1012	Q345-8X188	235	4	2.77	11.1	
1013	Q345-8X191	291	4	3.49	14.0	
1014	Q345-8X335	450	2	9.47	18.9	
1015	Q345-10X235	310	1	5.72	5.7	卷边60mm
1016	Q345-10X235	310	1	5.72	5.7	卷边60mm
1017	Q345-8X295	335	2	6.21	12.4	
1018	Q345-6X100	550	4	2.59	10.4	
1019	Q345-6X100	550	4	2.59	10.4	
1020	Q345L80X6	3175	2	23.42	46.8	切角
1021	Q345L80X6	3175	2	23.42	46.8	
1022	Q345L80X6	3161	2	23.32	46.6	切角
1023	Q345L80X6	3161	2	23.32	46.6	
1024	Q345L80X7	2779	2	23.69	47.4	切角
1025	Q345L80X7	2779	2	23.69	47.4	
1026	Q345L80X7	2297	1	19.58	19.6	
1027	Q345L80X7	2297	1	19.58	19.6	
1028	Q345-8X187	223	4	2.62	10.5	
1029	Q345-8X190	237	4	2.83	11.3	
1030	Q345-8X333	381	4	7.97	31.9	
1031	L63X5	1553	4	7.49	30.0	
1032	L50X4	2369	2	7.25	14.5	
1033	Q345L75X5	2369	1	13.78	13.8	
1034	Q345L63X5	1049	2	5.06	10.1	
1035	-6X207	358	2	3.49	7.0	
1036	Q345-6X329	509	1	7.89	7.9	卷边50mm
1037	-6X207	358	1	3.49	3.5	
1038	Q345-22X390	450	1	30.31	30.3	火曲 焊接
1039	Q345-22X390	450	1	30.31	30.3	火曲 焊接
1040	Q345-22X390	420	1	28.29	28.3	火曲 焊接
1041	Q345-22X390	420	1	28.29	28.3	火曲 焊接
1042	Q345Ø60/Ø38	34	4	0.45	1.8	焊接
1043	-14X60	60	2	0.40	0.8	垫块
1044	-18X60	60	4	0.51	2.0	垫块
1045	-12X60	60	6	0.34	2.0	垫块
1046	-10X60	60	16	0.28	4.5	垫块
1047	-2X60	240	8	0.23	1.8	垫板
1048	Q345L70X6	1230	2	7.88	15.8	
1049	Q345-10X430	457	1	15.43	15.4	卷边60mm
1050	Q345-10X430	457	1	15.43	15.4	卷边60mm
合计		1449.2 kg				

螺栓、脚钉、垫圈明细表

名称	级别	规格	符号	数量	重量(kg)	备注
螺栓	6.8级	M16X40	◍	4	0.6	
		M16X50	⊘	1	0.2	
		M20X45	○	118	31.9	
		M20X55	⊘	194	57.3	
		M20X65	⊗	20	6.4	
		M20X80	○	36	14.8	带双帽
脚钉	6.8级	M16X180	⊖ ⊥	8	2.6	
		M20X200		3	1.9	
垫圈	Q235	-3(Ø17.5)	规格X个数	2	0.0	
合计			115.7 kg			

甘肃电通电力工程设计咨询有限公司

甘肃庆阳能化电厂330千伏送出工程 工程		施工图	设计阶段
批准	曹晓青	曹晓青	330-KC22D-DJ终端塔 (0°-40°)中导及塔身结构图 ⑩
审核	王公阳	王公阳	
	丁国鹏	丁国鹏	
校核	王文军		
设计	段增强	段增强	
CAD 制图	段增强	段增强	
比例			
日期	2026年7月	图号	330-KC22D-DJ-11