

上接⑨段

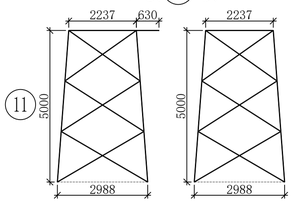

⑪

单线图


1:100

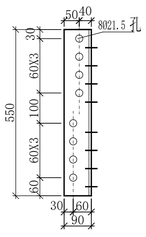

1104 Q345J 90X7 350

连接角钢大样图


1:10

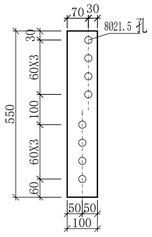

Q345-6 1118

包钢板大样图


1:10

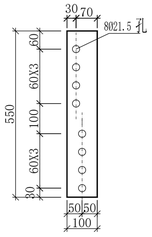

Q345-6 1119

包钢板大样图


1:10

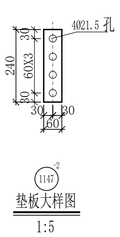

1147 -2


垫板大样图

1:5

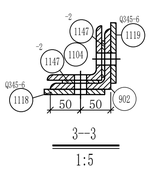


3—3

1:5

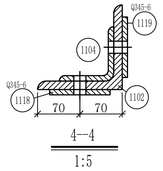


4—4

1:5

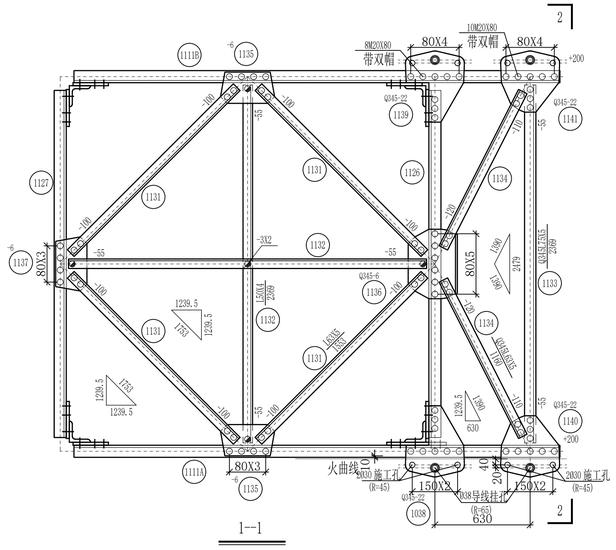


1--1

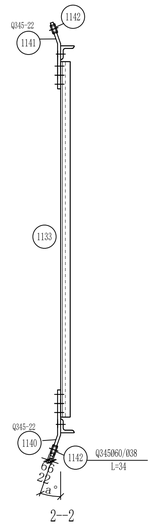


2—2


说明:挂线板倾角"a°"详见〈杆塔明细表〉

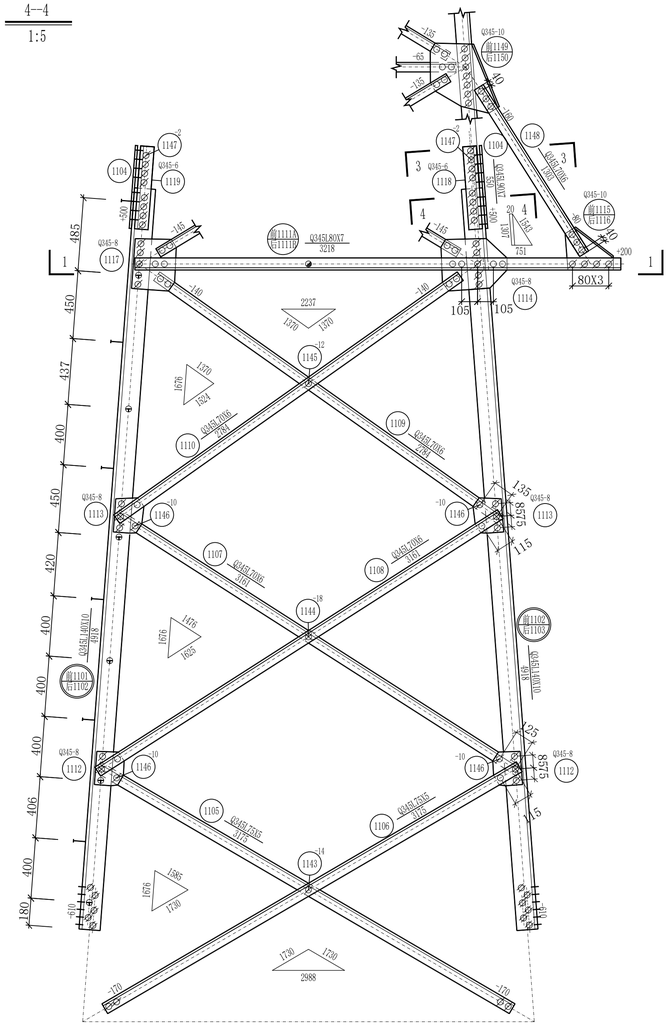

正面图

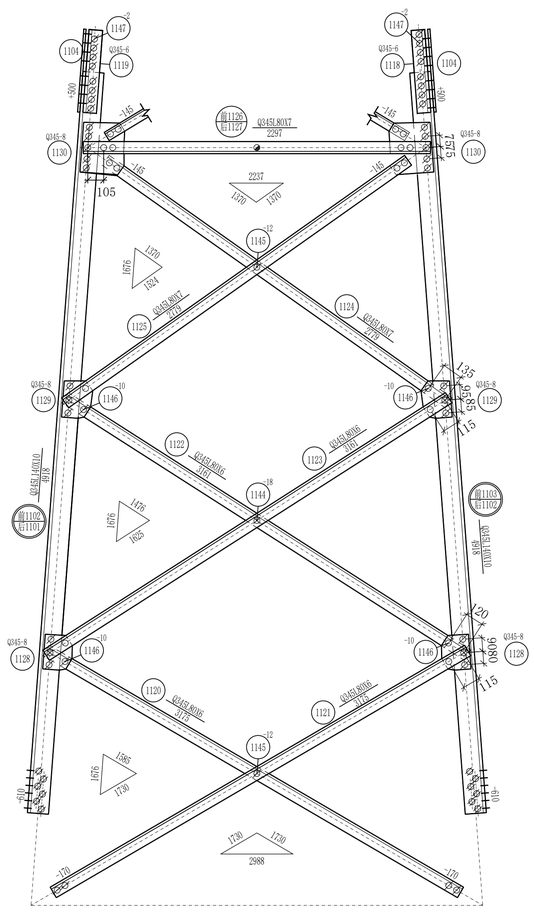

侧面图

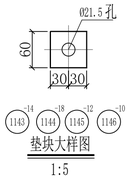

垫块大样图

1:5

构件明细表

编号	规格	长度(mm)	数量	重量(kg) 一件	重量(kg) 小计	备注
1101	Q345L140X10	4918	1	105.68	105.7	带脚钉
1102	Q345L140X10	4918	2	105.68	211.4	
1103	Q345L140X10	4918	1	105.68	105.7	
1104	Q345L90X7	550	4	5.31	21.2	铲背
1105	Q345L75X5	3175	2	18.47	36.9	切角
1106	Q345L75X5	3175	2	18.47	36.9	
1107	Q345L70X6	3161	2	20.25	40.5	切角
1108	Q345L70X6	3161	2	20.25	40.5	
1109	Q345L70X6	2784	2	17.83	35.7	切角
1110	Q345L70X6	2784	2	17.83	35.7	
1111A	Q345L80X7	3218	1	27.43	27.4	
1111B	Q345L80X7	3218	1	27.43	27.4	
1112	Q345-8X188	235	4	2.77	11.1	
1113	Q345-8X191	291	4	3.49	14.0	
1114	Q345-8X335	450	2	9.47	18.9	
1115	Q345-10X235	310	1	5.72	5.7	卷边60mm
1116	Q345-10X235	310	1	5.72	5.7	卷边60mm
1117	Q345-8X295	335	2	6.21	12.4	
1118	Q345-6X100	550	4	2.59	10.4	
1119	Q345-6X100	550	4	2.59	10.4	
1120	Q345L80X6	3175	2	23.42	46.8	切角
1121	Q345L80X6	3175	2	23.42	46.8	
1122	Q345L80X6	3161	2	23.32	46.6	切角
1123	Q345L80X6	3161	2	23.32	46.6	
1124	Q345L80X7	2779	2	23.69	47.4	切角
1125	Q345L80X7	2779	2	23.69	47.4	
1126	Q345L80X7	2297	1	19.58	19.6	
1127	Q345L80X7	2297	1	19.58	19.6	
1128	Q345-8X187	223	4	2.62	10.5	
1129	Q345-8X190	237	4	2.83	11.3	
1130	Q345-8X333	381	4	7.97	31.9	
1131	L63X5	1553	4	7.49	30.0	
1132	L50X4	2369	2	7.25	14.5	
1133	Q345L75X5	2369	1	13.78	13.8	
1134	Q345L63X5	1160	2	5.59	11.2	
1135	-6X207	358	2	3.49	7.0	
1136	Q345-6X329	509	1	7.89	7.9	卷边50mm
1137	-6X207	358	1	3.49	3.5	
1138	Q345-22X390	450	1	30.31	30.3	火曲 焊接
1139	Q345-22X390	450	1	30.31	30.3	火曲 焊接
1140	Q345-22X390	420	1	28.29	28.3	火曲 焊接
1141	Q345-22X390	420	1	28.29	28.3	火曲 焊接
1142	Q345060/038	34	4	0.45	1.8	焊接
1143	-14X60	60	2	0.40	0.8	垫块
1144	-18X60	60	4	0.51	2.0	垫块
1145	-12X60	60	6	0.34	2.0	垫块
1146	-10X60	60	16	0.28	4.5	垫块
1147	-2X60	240	8	0.23	1.8	垫板
1148	Q345L70X6	1303	2	8.35	16.7	
1149	Q345-10X430	440	1	14.85	14.8	卷边60mm
1150	Q345-10X430	440	1	14.85	14.8	卷边60mm
合计					1452.4 kg	

螺栓、脚钉、垫圈明细表

名称	级别	规格	符号	数量	重量(kg)	备注
螺栓	6.8级	M16X40		4	0.6	
		M16X50		1	0.2	
		M20X45		118	31.9	
		M20X55		194	57.3	
		M20X65		20	6.4	
		M20X80		36	14.8	带双帽
脚钉	6.8级	M16X180		8	2.6	
		M20X200		3	1.9	
垫圈	Q235	-3(Ø17.5)	规格X个数	2	0.0	
合计					115.7 kg	

甘肃电通电力工程设计咨询有限公司			
甘肃庆阳能化电厂330千伏送出工程	工程	施工图	设计阶段
批准	曹晓青		330-KC22D-DJ终端塔 ⑪
审核	王公阳		(40°-90°)中导及塔身结构图
	丁国鹏		
校核	王文军		
设计	段增强		
CAD制图	段增强		
比例			
日期	2026年7月	图号	330-KC22D-DJ-12