


上接⑩⑪段

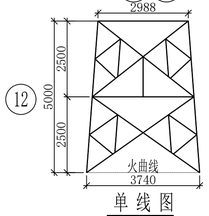



单线图


1:100

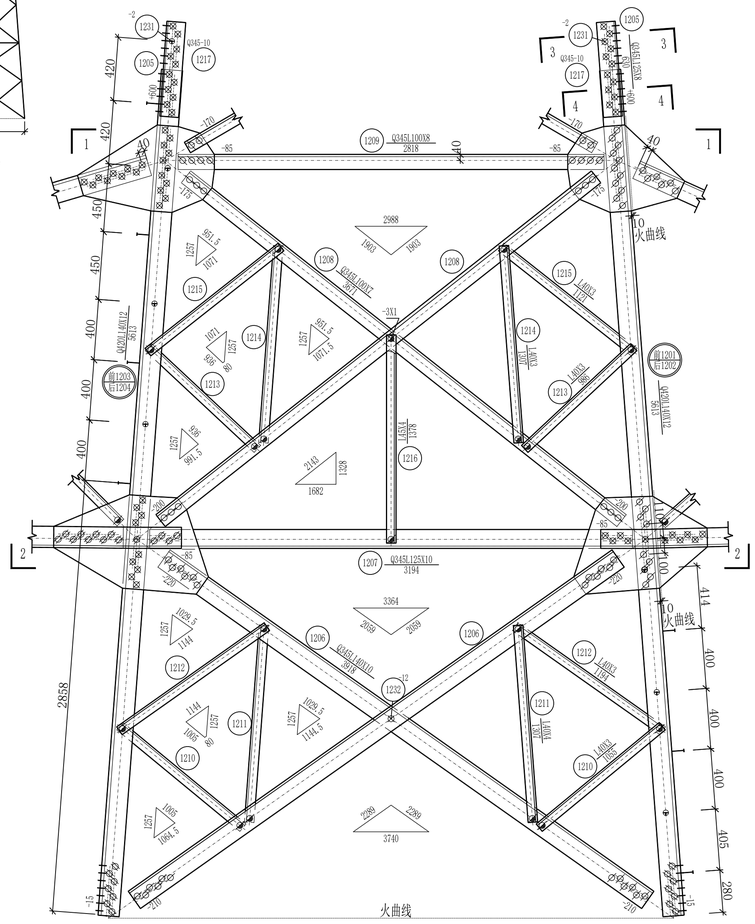


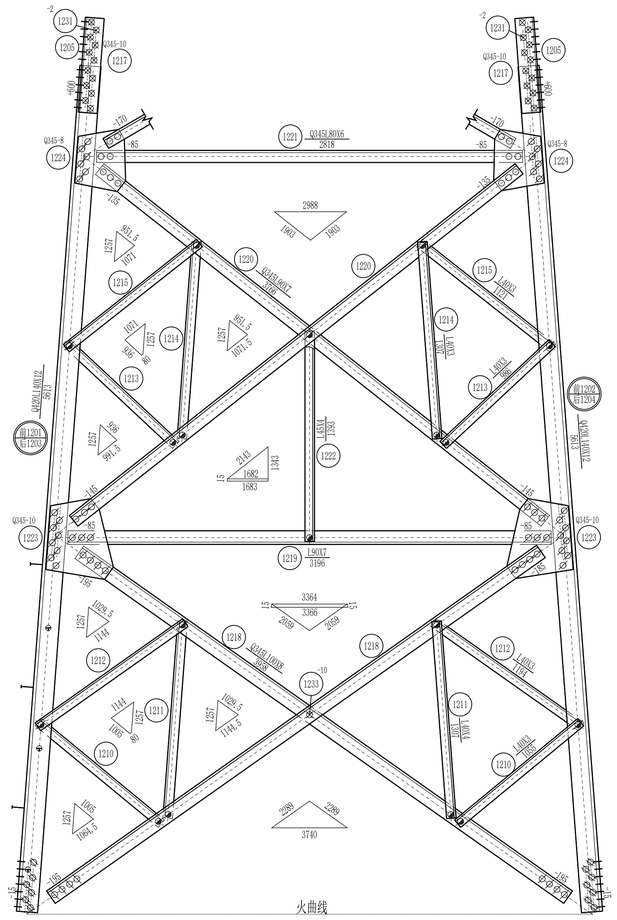


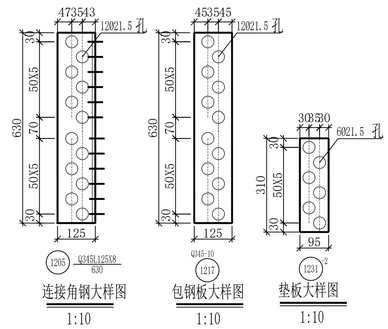

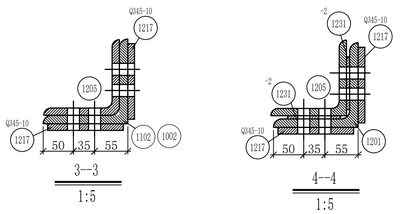

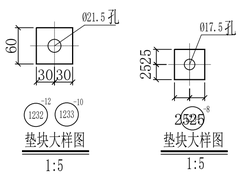

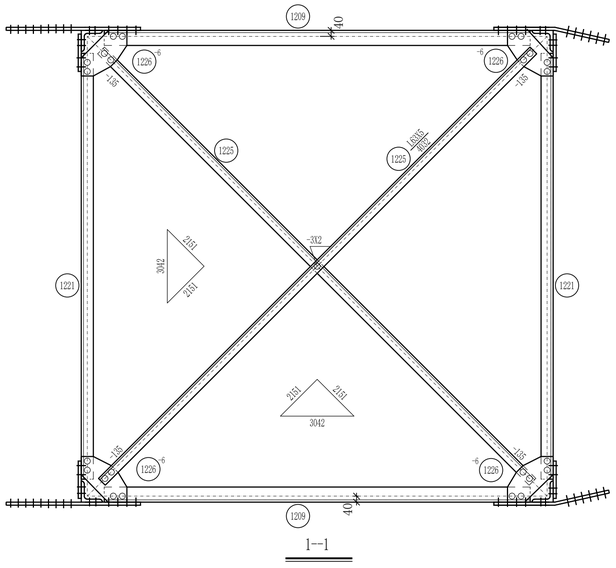

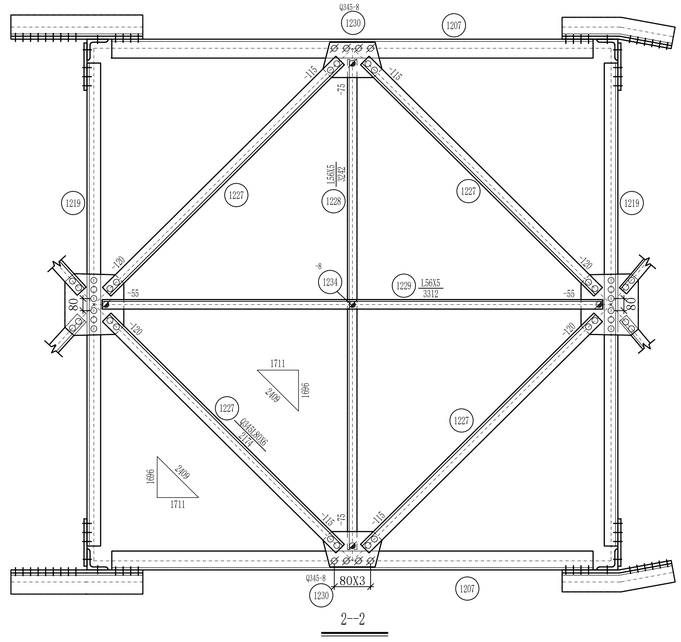

构件明细表

编号	规格	长度(mm)	数量	重量(kg) 一件	重量(kg) 小计	备注
1201	Q420L140X12	5613	1	143.25	143.2	带脚钉
1202	Q420L140X12	5613	1	143.25	143.2	
1203	Q420L140X12	5613	1	143.25	143.2	带脚钉
1204	Q420L140X12	5613	1	143.25	143.2	
1205	Q345L125X8	630	4	9.77	39.1	铲背
1206	Q345L140X10	3918	4	84.16	336.6	
1207	Q345L125X10	3194	2	61.11	122.2	
1208	Q345L100X7	3671	4	45.04	180.2	
1209	Q345L100X8	2818	2	34.59	69.2	
1210	L40X3	1055	8	1.95	15.6	
1211	L40X4	1307	8	3.17	25.4	切角
1212	L40X3	1194	8	2.21	17.7	
1213	L40X3	986	8	1.83	14.6	
1214	L40X3	1307	8	2.42	19.4	切角
1215	L40X3	1121	8	2.08	16.6	
1216	L45X4	1378	2	3.77	7.5	一端压扁
1217	Q345-10X125	630	8	6.18	49.4	
1218	Q345L100X8	3958	4	48.56	194.2	
1219	L90X7	3196	2	30.86	61.7	
1220	Q345L90X7	3766	4	36.36	145.4	
1221	Q345L80X6	2818	2	20.79	41.6	
1222	L45X4	1393	2	3.81	7.6	一端压扁
1223	Q345-10X450	544	4	19.22	76.9	
1224	Q345-8X327	406	4	8.34	33.4	
1225	L63X5	4032	2	19.44	38.9	
1226	-6X302	302	4	4.30	17.2	
1227	Q345L80X6	2174	4	16.04	64.2	
1228	L56X5	3242	1	13.78	13.8	
1229	L56X5	3312	1	14.08	14.1	
1230	Q345-8X234	391	2	5.75	11.5	
1231	-2X95	310	8	0.46	3.7	垫板
1232	-12X60	60	2	0.34	0.7	垫块
1233	-10X60	60	2	0.28	0.6	垫块
1234	-8X50	50	1	0.16	0.2	垫块
合计				2212.0 kg		

螺栓、脚钉、垫圈明细表

名称	级别	规格	符号	数量	重量(kg)	备注
螺栓	6.8级	M16X40		26	3.7	
		M16X50		47	7.5	
		M16X60		2	0.4	
		M20X45		60	16.1	
		M20X55		105	31.0	
		M20X65		100	32.1	
脚钉	6.8级	M16X180		9	2.9	
		M20X200		4	2.5	
垫圈	Q235	-3(Ø17.5)	规格X个数	2	0.0	
		-3(Ø22)		2	0.0	
合计				96.2 kg		

甘肃电通电力工程设计咨询有限公司

甘肃庆阳能化电厂330千伏送出工程		工程	施工图	设计阶段
批准	曹晓青		330-KC22D-DJ终端塔	
审核	王公阳		塔身结构图	12
	丁国鹏			
校核	王文军			
设计	段增强			
CAD制图	段增强			
比例				
日期	2026年7月	图号	330-KC22D-DJ-13	