


上接⑫段

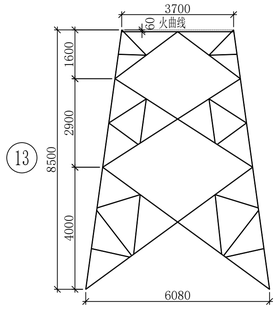

单线图


1:100

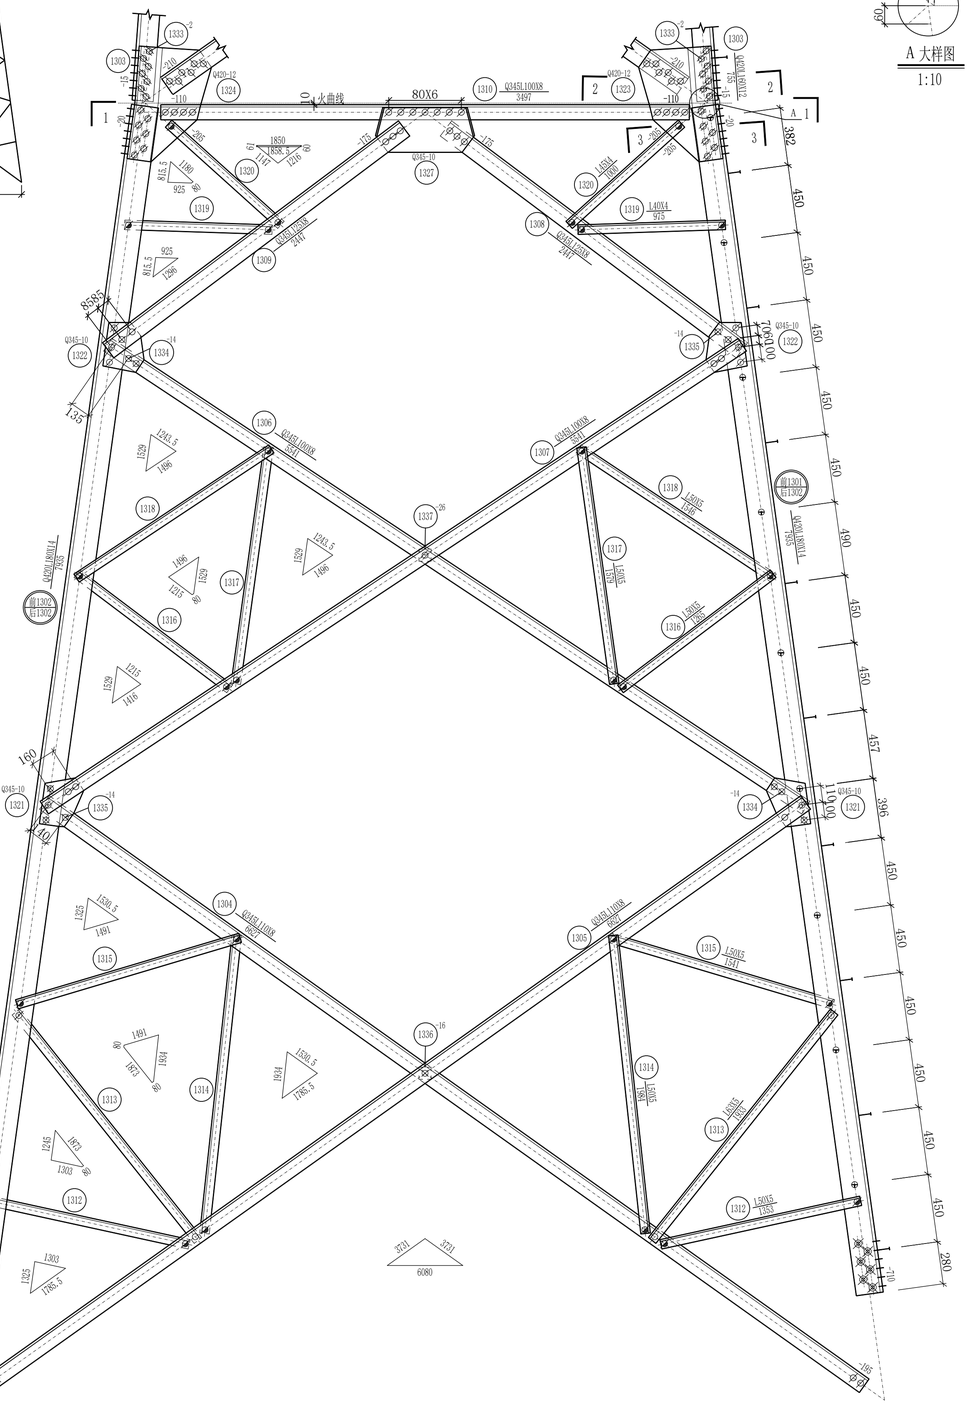

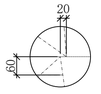


A 大样图

1:10

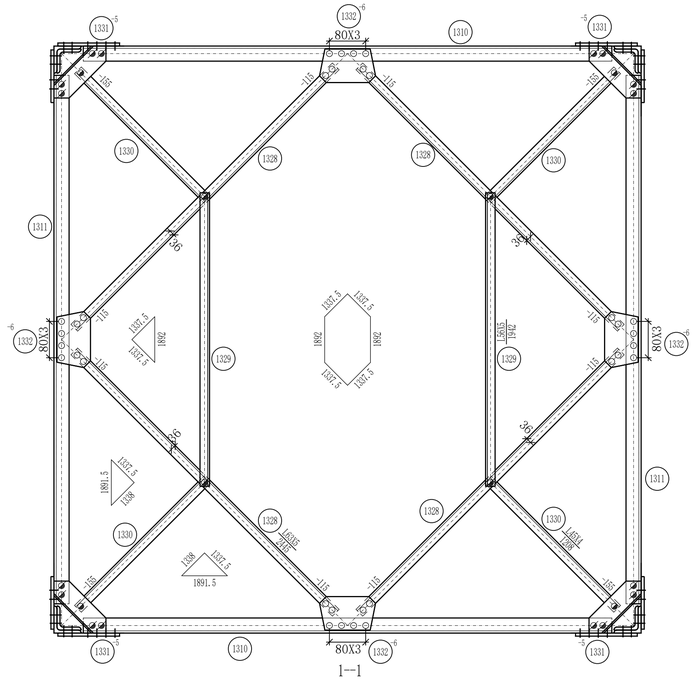


1--1

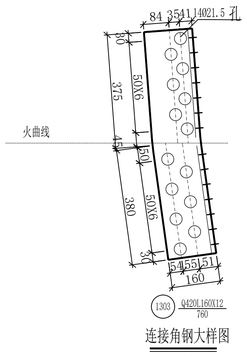


连接角钢大样图

1:10

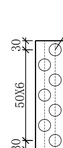


垫板大样图


1:10

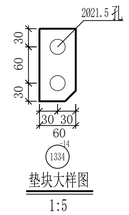


1:5

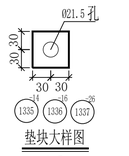

1:5

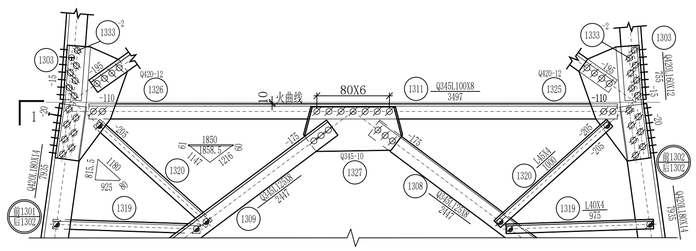


侧面图

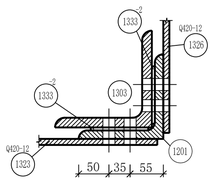

2--2

1:5

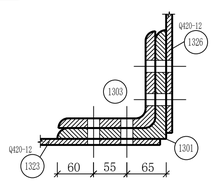

3--3

1:5

构件明细表

编号	规格	长度(mm)	数量	重量(kg) 一件	重量(kg) 小计	备注
1301	Q420L180X14	7935	1	304.57	304.6	带脚钉
1302	Q420L180X14	7935	3	304.57	913.7	
1303	Q420L160X12	755	4	22.19	88.8	铲背 火曲
1304	Q345L110X8	6627	4	89.66	358.6	切角
1305	Q345L110X8	6627	4	89.66	358.6	
1306	Q345L100X8	5541	4	67.99	272.0	切角
1307	Q345L100X8	5541	4	67.99	272.0	
1308	Q345L125X8	2447	4	37.93	151.7	切角
1309	Q345L125X8	2447	4	37.93	151.7	
1310	Q345L100X8	3497	2	42.93	85.9	
1311	Q345L100X8	3497	2	42.93	85.9	
1312	L50X5	1353	8	5.10	40.8	
1313	L63X5	1984	8	9.57	76.6	
1314	L50X5	2034	8	7.67	61.4	
1315	L50X5	1541	8	5.81	46.5	
1316	L50X5	1265	8	4.77	38.2	
1317	L50X5	1579	8	5.95	47.6	
1318	L50X5	1546	8	5.83	46.6	
1319	L40X4	975	8	2.36	18.9	
1320	L45X4	1000	8	2.74	21.9	
1321	Q345-10X263	331	8	6.83	54.6	
1322	Q345-10X266	315	8	6.58	52.6	
1323	Q420-12X487	755	2	34.64	69.3	火曲
1324	Q420-12X487	755	2	34.64	69.3	火曲
1325	Q420-12X409	755	2	29.09	58.2	火曲
1326	Q420-12X409	755	2	29.09	58.2	火曲
1327	Q345-10X287	754	4	20.38	81.5	卷边60mm
1328	L63X5	2446	4	11.79	47.2	
1329	L56X5	1942	2	8.26	16.5	
1330	L45X4	1208	4	3.31	13.2	
1331	-5X129	464	4	2.35	9.4	
1332	-6X222	371	4	3.88	15.5	
1333	-12X195	360	8	3.22	25.8	垫板
1334	-14X60	120	8	0.79	6.3	垫块
1335	-14X60	60	8	0.40	3.2	垫块
1336	-16X60	60	4	0.68	2.7	垫块
1337	-26X60	60	4	0.45	1.8	垫块
合计					4027.3 kg	

螺栓、脚钉、垫圈明细表

名称	级别	规格	符号	数量	重量(kg)	备注
螺栓	6.8级	M16X40		4	0.6	
		M16X50		116	18.6	
		M16X60		8	1.4	
		M20X45		40	10.8	
		M20X55		164	48.4	
		M20X65		52	16.7	
		M20X75		132	45.6	
脚钉	6.8级	M16X180		15	4.9	
		M20X200		3	1.9	
垫圈	Q235		规格X个数			
合计					148.9 kg	

甘肃电通电力工程设计咨询有限公司				
甘肃庆阳能化电厂330千伏送出工程	工程	施工图	设计阶段	
批准	曹晓青		330-KC22D-DJ终端塔	
审核	王公阳		塔身结构图	13
	丁国鹏			
校核	王文军			
设计	段增强			
CAD制图	段增强			
比例				
日期	2026年7月	图号	330-KC22D-DJ-14	