


上接(13)段

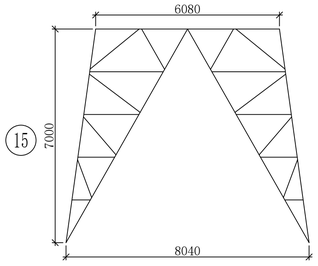


(15) 单线图 1:100

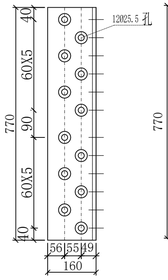


连接角钢大样图 1:10

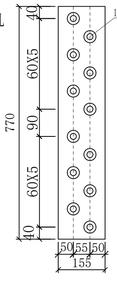


包钢板大样图 1:10

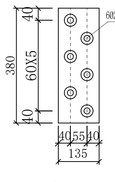


垫板大样图 1:10

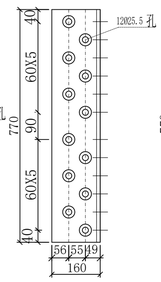


连接角钢大样图 1:10

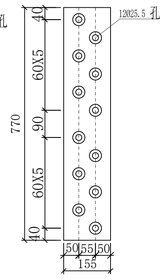


包钢板大样图 1:10

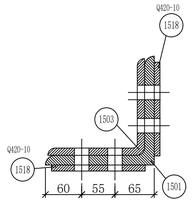


3--3 1:5

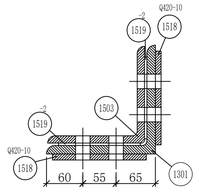

4--4 1:5

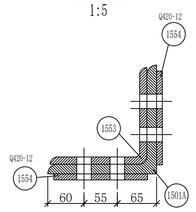


6--6 1:5

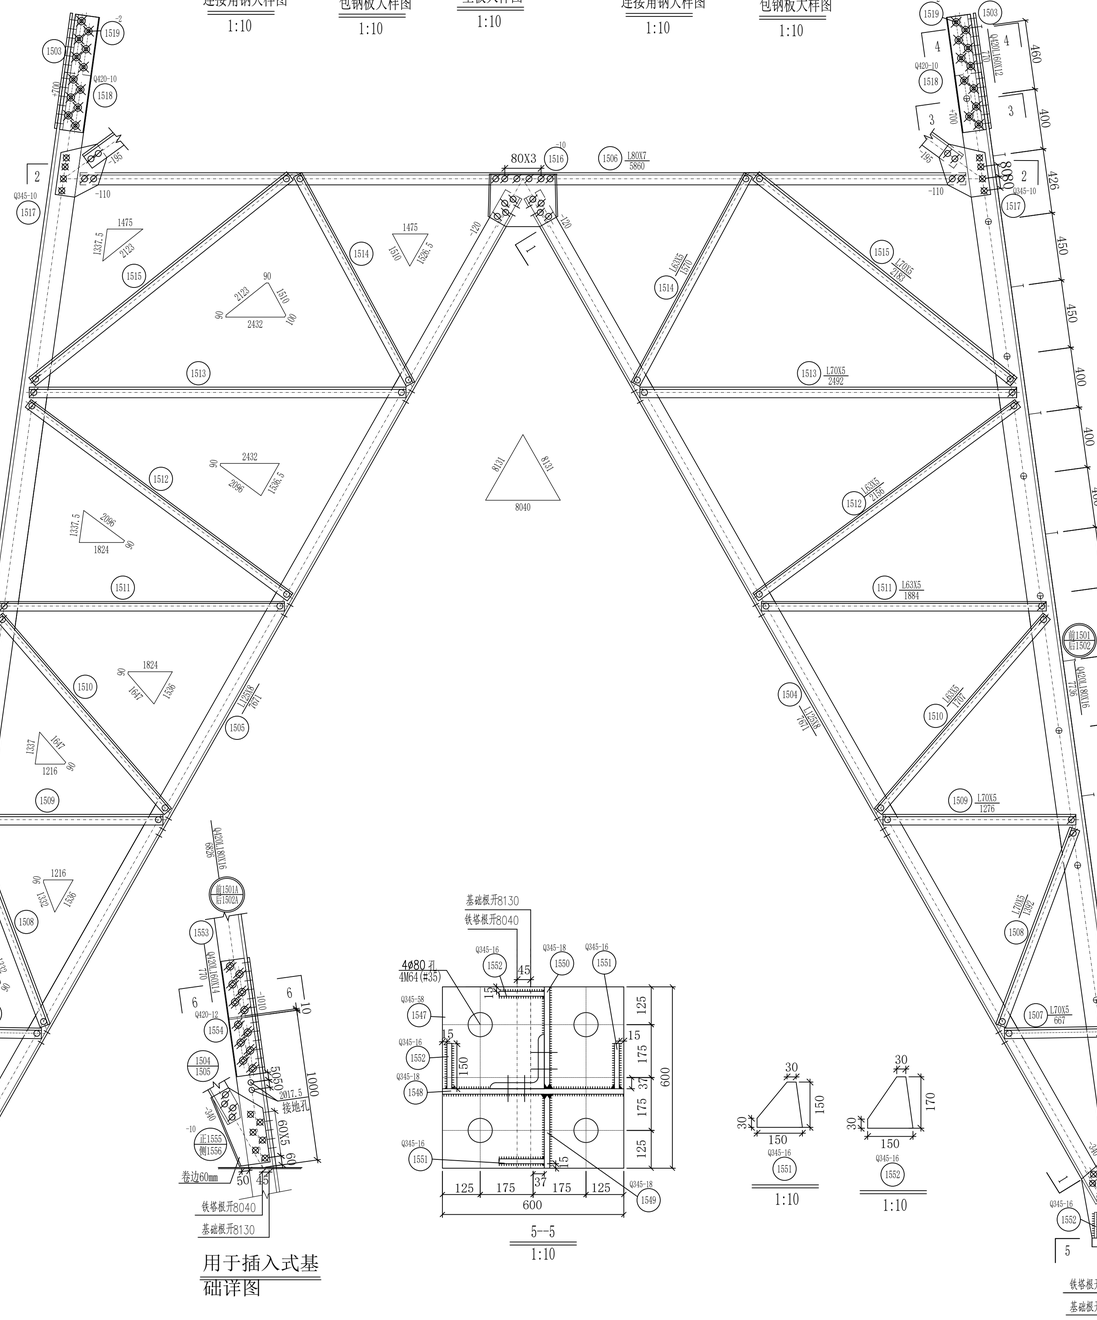

用于插入式基础详图

5--5 1:10

1:10 1:10

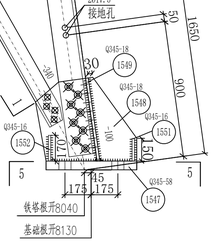

构件明细表(插入式)

编号	规格	长度(mm)	数量	重量(kg) 一件	重量(kg) 小计	备注
1501A	Q420L180X16	6826	1	297.22	297.2	带脚钉
1502A	Q420L180X16	6826	3	297.22	891.7	
1503	Q420L160X12	770	4	22.63	90.5	铲背
1504	L125X8	7671	4	118.90	475.6	切角
1505	L125X8	7671	4	118.90	475.6	切角
1506	L80X7	5860	4	49.96	199.8	
1507	L70X5	667	8	3.60	28.8	
1508	L70X5	1392	8	7.51	60.1	
1509	L70X5	1276	8	6.89	55.1	
1510	L63X5	1707	8	8.23	65.8	
1511	L63X5	1884	8	9.08	72.6	
1512	L63X5	2156	8	10.40	83.2	
1513	L70X5	2492	8	13.45	107.6	
1514	L63X5	1570	8	7.57	60.6	
1515	L70X5	2183	8	11.78	94.2	
1516	-10X373	505	4	14.79	59.2	卷边60mm
1517	Q345-10X342	351	8	9.42	75.4	
1518	Q420-10X155	770	8	9.37	75.0	
1519	-2X135	380	8	0.81	6.5	垫板
1520	L50X4	3402	2	10.41	20.8	切角
1521	L50X4	3402	2	10.41	20.8	切角
1522	L50X4	3402	2	10.41	20.8	
1523	L50X4	3402	2	10.41	20.8	
1524	L50X4	2078	4	6.36	25.4	
1525	L40X3	512	4	0.95	3.8	
1526	L40X4	1291	4	3.13	12.5	一端压扁
1527	L40X3	710	4	1.31	5.2	
1528	L40X3	710	2	1.31	2.6	切角
1529	L40X3	710	2	1.31	2.6	切角
1530	-5X330	330	4	4.27	17.1	卷边50mm
1531	L40X4	837	4	2.03	8.1	
1532	L40X3	1924	8	3.56	28.5	
1533	L40X4	2610	8	6.32	50.6	
1534	L45X4	4446	8	12.16	97.3	
1535	L40X4	1731	8	4.19	33.5	
1536	L40X3	817	8	1.51	12.1	
1537	-6X154	189	4	1.37	5.5	火曲
1538	-6X154	189	4	1.37	5.5	火曲
1539	-6X180	205	4	1.74	7.0	火曲
1540	-6X180	205	4	1.74	7.0	火曲
1541	-6X173	176	4	1.43	5.7	火曲
1542	-6X173	176	4	1.43	5.7	火曲
1543	-6X146	187	4	1.29	5.2	火曲
1544	-6X146	187	4	1.29	5.2	火曲
1545	-6X130	198	4	1.21	4.8	火曲
1546	-6X152	185	4	1.32	5.3	火曲
1553	Q420L160X14	770	4	26.17	104.7	铲背
1554	Q420-12X155	770	8	11.24	89.9	
1555	-10X453	459	4	16.32	65.3	卷边60mm
1556	-10X453	459	4	16.32	65.3	卷边60mm
合计				4039.1 kg		

螺栓、脚钉、垫圈明细表

名称	级别	规格	符号	数量	重量(kg)	备注
螺栓	6.8级	M16X40		160	23.8	
		M16X50		100	16.0	
		M20X45		80	21.6	
		M20X55		184	54.3	
		M20X65		80	25.7	
	8.8级	M24X75		96	51.5	
		M24X85		96	55.1	
脚钉	6.8级	M16X180		13	4.2	
		M20X200		1	0.6	
	8.8级	M24X240		2	1.8	
垫圈	Q235	-3(Ø17.5)	规格X个数	24	0.3	
合计				254.9 kg		

构件明细表(座板式)

编号	规格	长度(mm)	数量	重量(kg) 一件	重量(kg) 小计	备注
1501	Q420L180X16	7736	1	336.84	336.8	带脚钉
1502	Q420L180X16	7736	3	336.84	1010.5	
1503	Q420L160X12	770	4	22.63	90.5	铲背
1504	L125X8	7671	4	118.90	475.6	切角
1505	L125X8	7671	4	118.90	475.6	切角
1506	L80X7	5860	4	49.96	199.8	
1507	L70X5	667	8	3.60	28.8	
1508	L70X5	1392	8	7.51	60.1	
1509	L70X5	1276	8	6.89	55.1	
1510	L63X5	1707	8	8.23	65.8	
1511	L63X5	1884	8	9.08	72.6	
1512	L63X5	2156	8	10.40	83.2	
1513	L70X5	2492	8	13.45	107.6	
1514	L63X5	1570	8	7.57	60.6	
1515	L70X5	2183	8	11.78	94.2	
1516	-10X373	505	4	14.79	59.2	卷边60mm
1517	Q345-10X342	351	8	9.42	75.4	
1518	Q420-10X155	770	8	9.37	75.0	
1519	-2X135	380	8	0.81	6.5	垫板
1520	L50X4	3402	2	10.41	20.8	切角
1521	L50X4	3402	2	10.41	20.8	切角
1522	L50X4	3402	2	10.41	20.8	
1523	L50X4	3402	2	10.41	20.8	
1524	L50X4	2078	4	6.36	25.4	
1525	L40X3	512	4	0.95	3.8	
1526	L40X4	1291	4	3.13	12.5	一端压扁
1527	L40X3	710	4	1.31	5.2	
1528	L40X3	710	2	1.31	2.6	切角
1529	L40X3	710	2	1.31	2.6	切角
1530	-5X330	330	4	4.27	17.1	卷边50mm
1531	L40X4	837	4	2.03	8.1	
1532	L40X3	1924	8	3.56	28.5	
1533	L40X4	2610	8	6.32	50.6	
1534	L45X4	4446	8	12.16	97.3	
1535	L40X4	1731	8	4.19	33.5	
1536	L40X3	817	8	1.51	12.1	
1537	-6X154	189	4	1.37	5.5	火曲
1538	-6X154	189	4	1.37	5.5	火曲
1539	-6X180	205	4	1.74	7.0	火曲
1540	-6X180	205	4	1.74	7.0	火曲
1541	-6X173	176	4	1.43	5.7	火曲
1542	-6X173	176	4	1.43	5.7	火曲
1543	-6X146	187	4	1.29	5.2	火曲
1544	-6X146	187	4	1.29	5.2	火曲
1545	-6X130	198	4	1.21	4.8	火曲
1546	-6X152	185	4	1.32	5.3	火曲
1547	Q345-58X600	600	4	163.91	655.6	焊接
2248	Q345-18X542	600	4	45.95	183.8	坡口焊
1549	Q345-18X245	542	4	18.76	75.0	坡口焊
1550	Q345-18X337	542	4	25.81	103.2	坡口焊
1551	Q345-16X150	150	8	2.83	22.6	坡口焊
1552	Q345-16X150	170	8	3.20	25.6	坡口焊
合计				4938.1 kg		

螺栓、脚钉、垫圈明细表

名称	级别	规格	符号	数量	重量(kg)	备注
螺栓	6.8级	M16X40		160	23.1	
		M16X50		100	16.0	
		M20X45		80	21.6	
		M20X55		152	44.9	
		M20X65		64	21.2	
	8.8级	M24X75		160	85.9	
脚钉	6.8级	M16X180		13	4.2	
		M20X200		1	0.6	
	8.8级	M24X240		2	1.8	
垫圈	Q235	-3(Ø17.5)	规格X个数	24	0.3	
合计				219.6 kg		

甘肃电通电力工程设计咨询有限公司

甘肃庆阳能化电厂330千伏送出工程	工程	施工图	设计阶段	
批准	曹晓青		330-KC22D-DJ终端塔	
审核	王公阳		18.0m 腿部结构图	(15)
	丁国鹏			
校核	王文军			
设计	段增强			
CAD制图	段增强			
比例				
日期	2026年7月	图号	330-KC22D-DJ-16(1/2)	