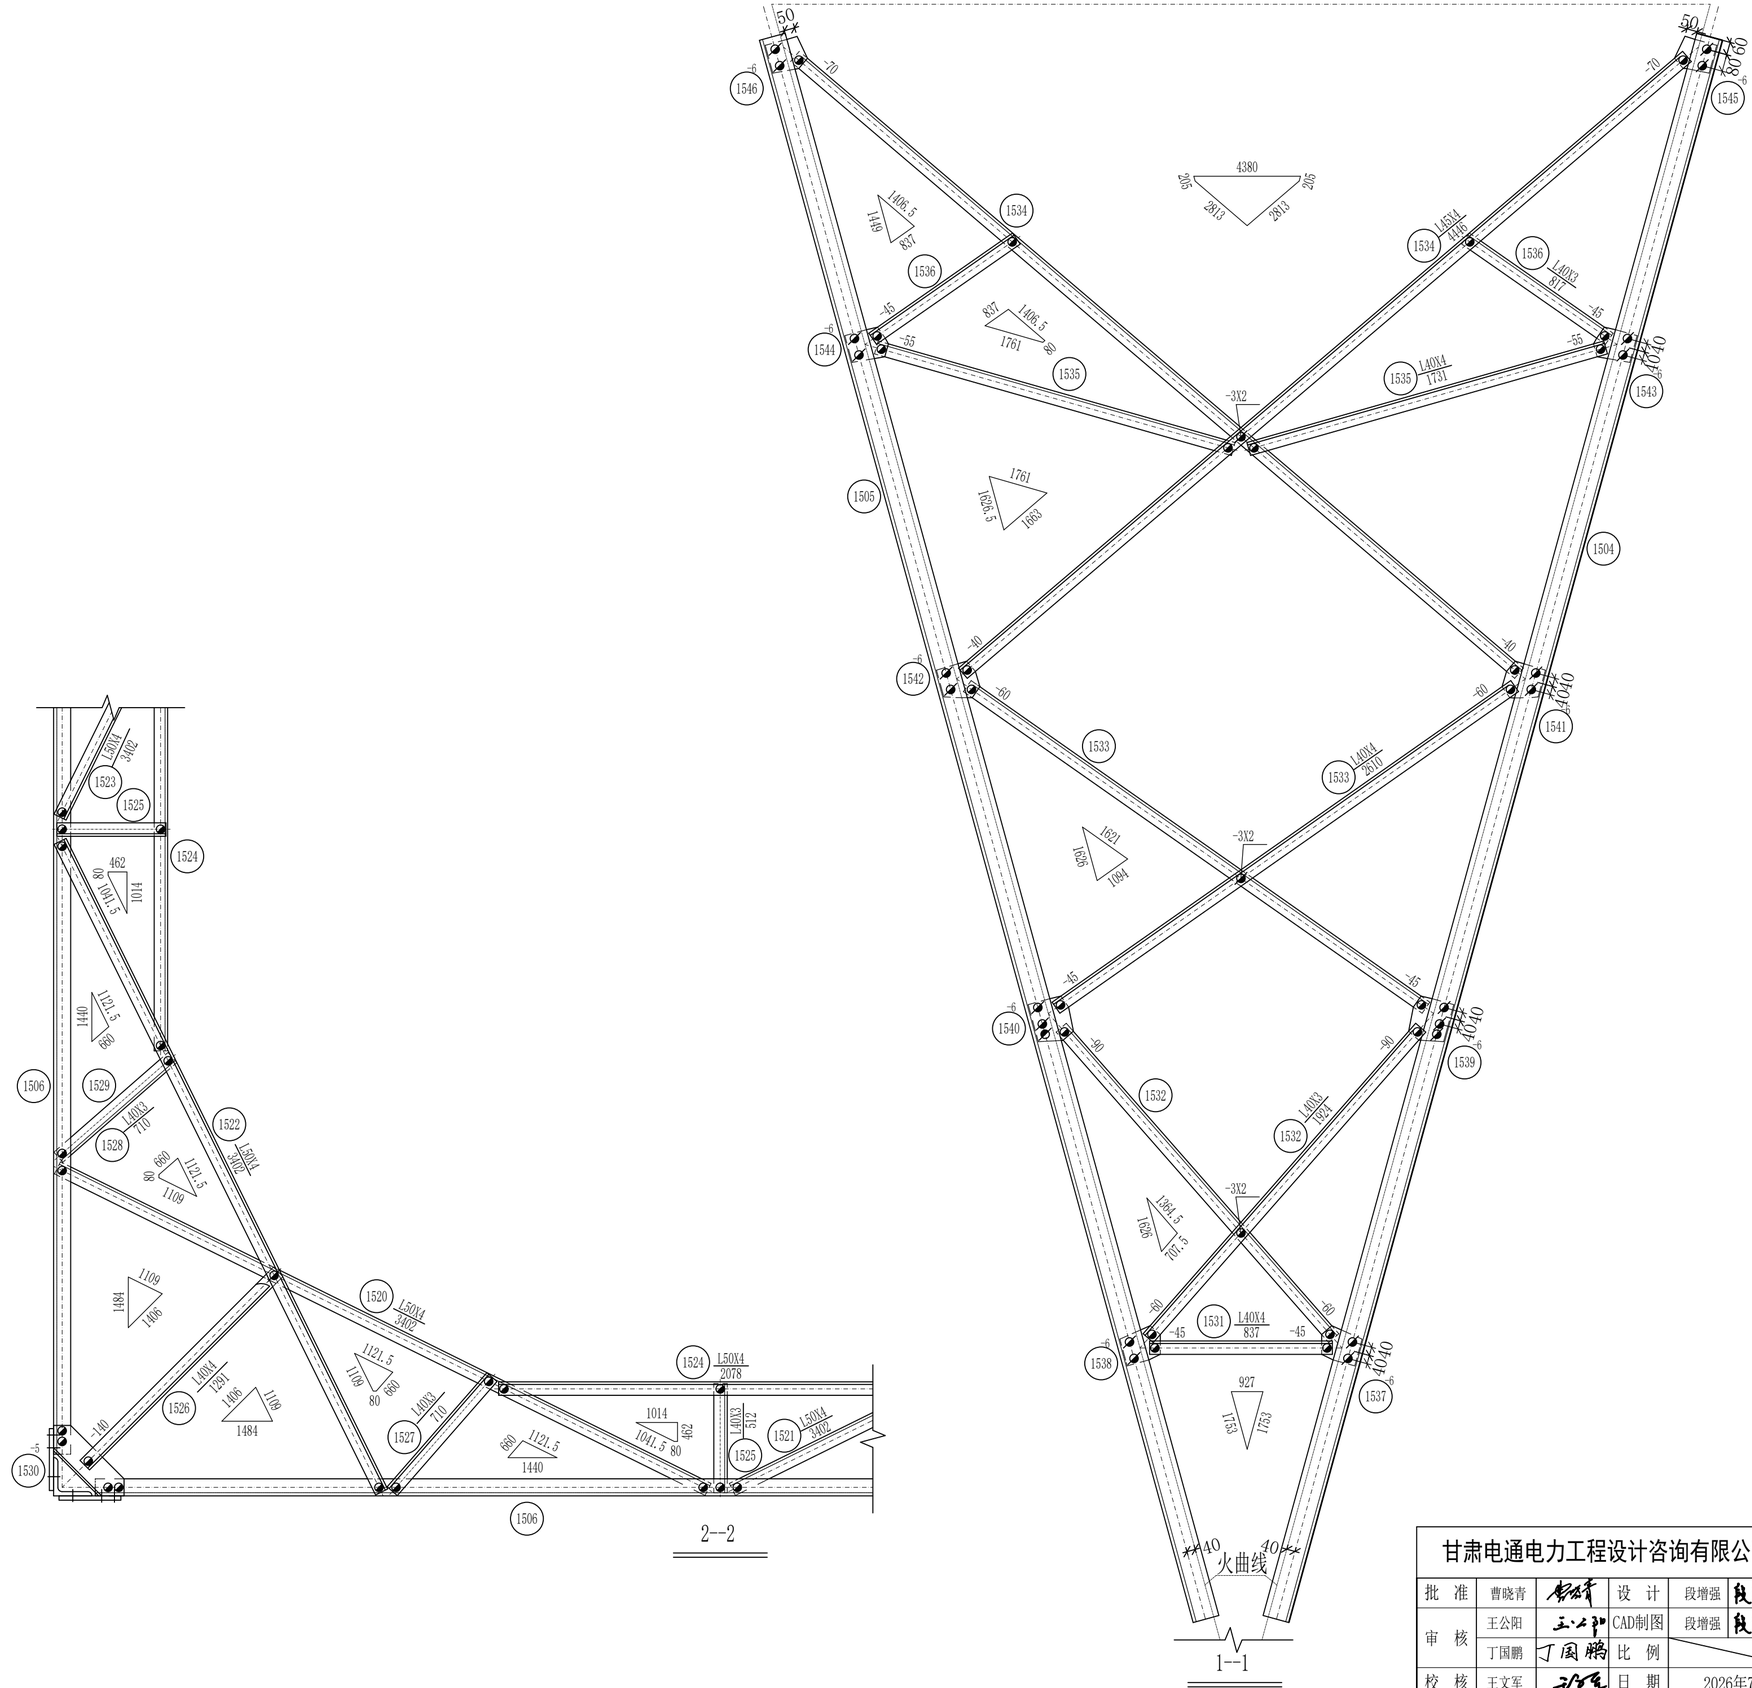


甘肃电通电力工程设计咨询有限公司					甘肃庆阳能化电厂330千伏送出工程	工程	施工图 设计阶段
批 准	曹晓青		设 计	段增强	330-KC22D-DJ终端塔 18.0m腿部结构图		15
审 核	王公阳		CAD制图	段增强			
	丁国鹏		比 例				
校 核	王文军		日 期	2026年7月	图 号	330-KC22D-DJ-16(2/2)	