


上接(13)段

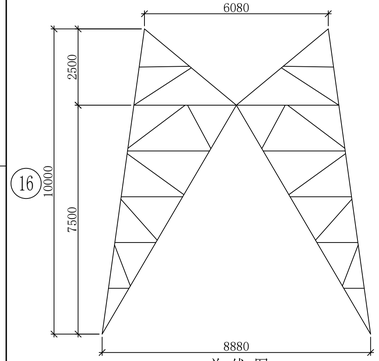


单线图
1:100

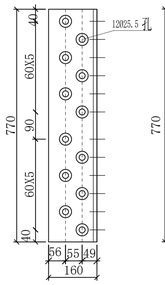


连接角钢大样图
1:10

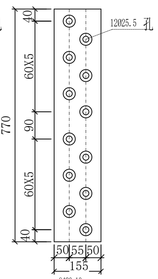


包钢板大样图
1:10

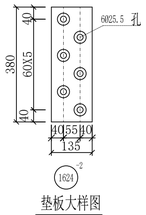

垫板大样图
1:10

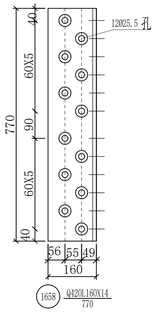

连接角钢大样图
1:10

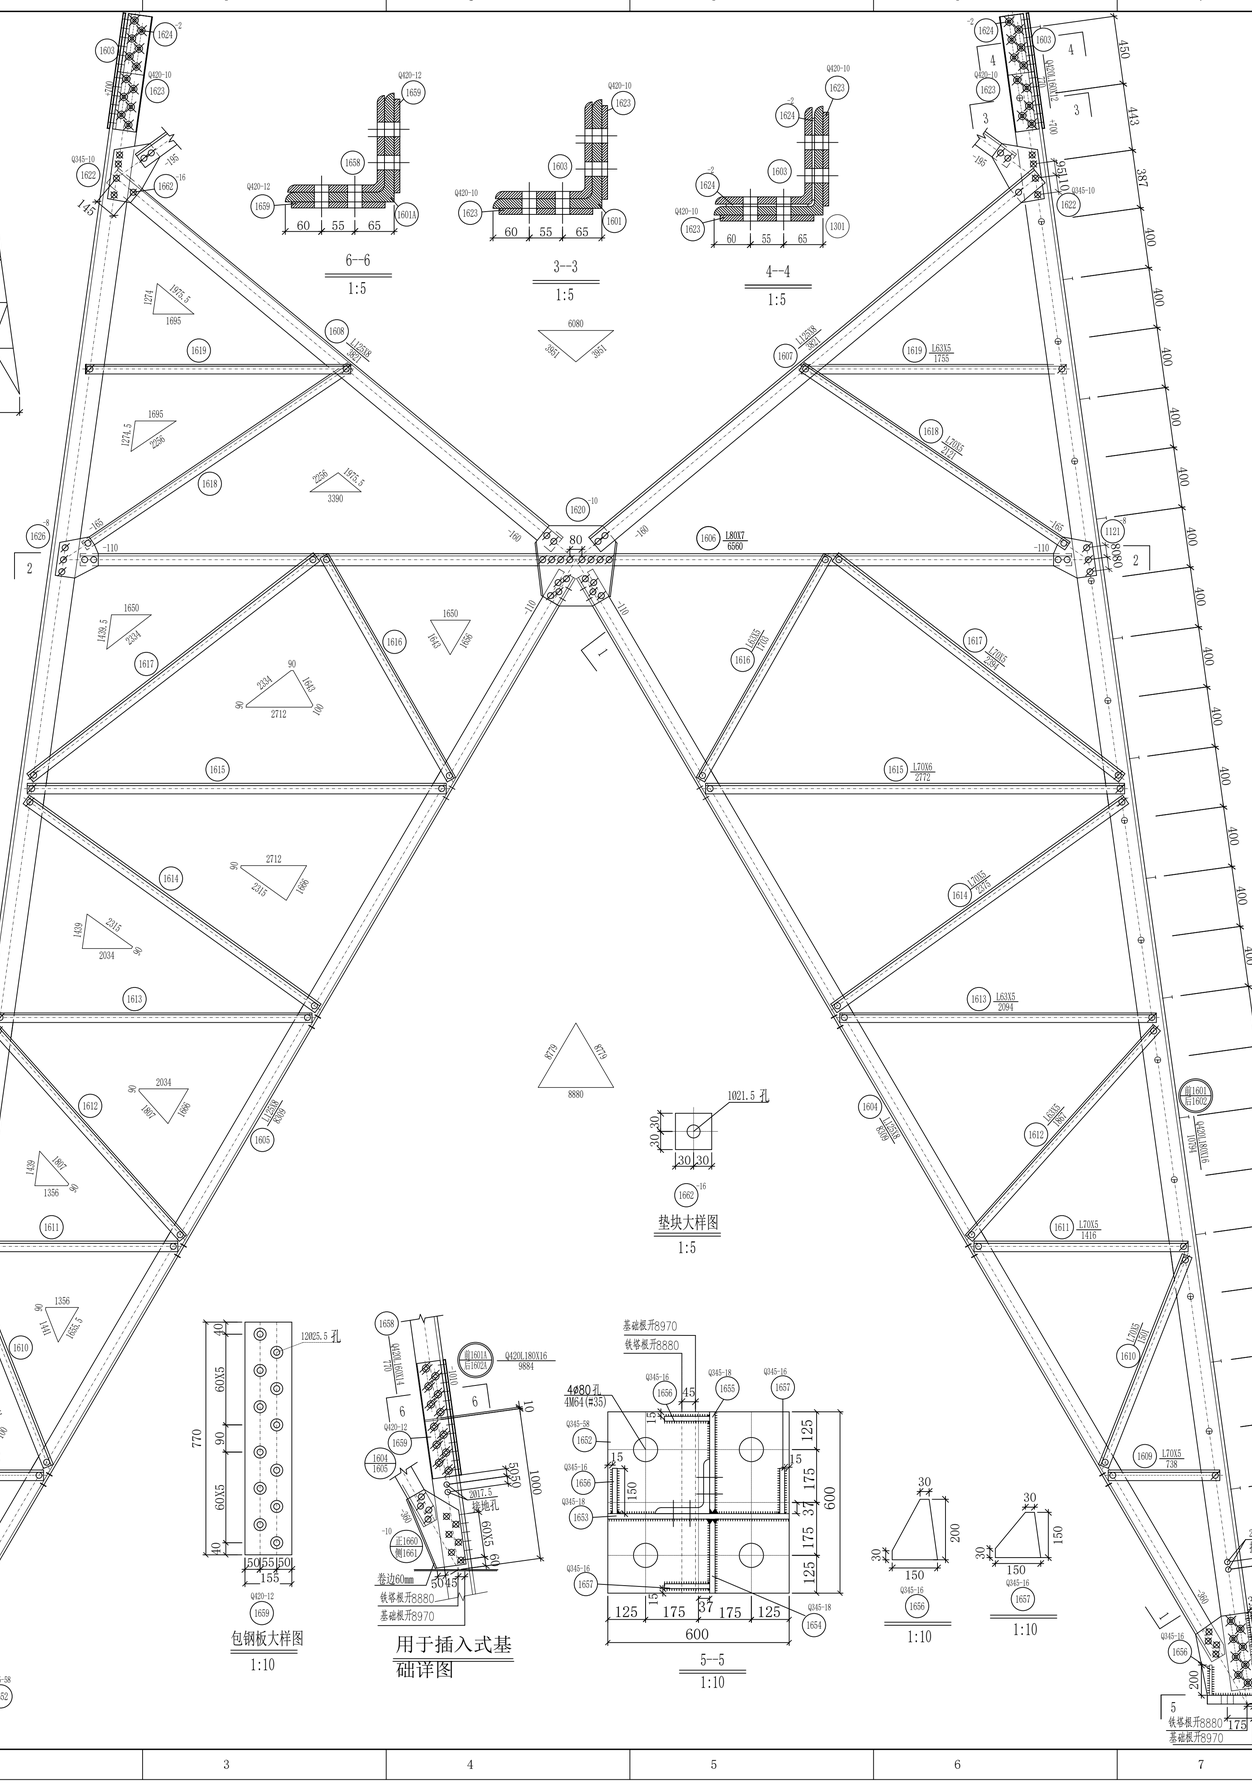

构件明细表(插入式)

编号	规格	长度(mm)	数量	重量(kg) 一件	重量(kg) 小计	备注
1601A	Q420L180X16	9884	1	430.37	430.4	带脚钉
1602A	Q420L180X16	9884	3	430.37	1291.1	
1603	Q420L160X12	770	4	22.63	90.5	铲背
1604	L125X8	8309	4	128.79	515.2	切角
1605	L125X8	8309	4	128.79	515.2	切角
1606	L80X7	6560	4	55.92	223.7	
1607	L125X8	3821	4	59.24	237.0	
1608	L125X8	3821	4	59.24	237.0	
1609	L70X5	738	8	3.98	31.8	
1610	L70X5	1501	8	8.10	64.8	
1611	L70X5	1416	8	7.64	61.1	
1612	L63X5	1867	8	9.00	72.0	
1613	L63X5	2094	8	10.10	80.8	
1614	L70X5	2375	8	12.82	102.6	
1615	L70X6	2772	8	17.76	142.1	
1616	L63X5	1703	8	8.21	65.7	
1617	L70X5	2394	8	12.92	103.4	
1618	L70X5	2121	8	11.45	91.6	
1619	L63X5	1755	8	8.46	67.7	
1620	-10X570	745	4	33.34	133.4	卷边60mm
1621	-8X274	277	8	4.77	38.2	
1622	Q345-10X346	429	8	11.65	93.2	
1623	Q420-10X155	770	8	9.37	75.0	
1624	-2X135	380	8	0.81	6.5	
1625	L56X4	3794	2	13.07	26.1	切角
1626	L56X4	3794	2	13.07	26.1	切角
1627	L56X4	3794	2	13.07	26.1	
1628	L56X4	3794	2	13.07	26.1	
1629	L50X4	2311	4	7.07	28.3	
1630	L40X3	570	4	1.06	4.2	
1631	L45X4	1456	4	3.98	15.9	一端压扁
1632	L40X3	792	4	1.47	5.9	
1633	L40X3	792	2	1.47	2.9	切角
1634	L40X3	792	2	1.47	2.9	切角
1635	-5X330	330	4	4.27	17.1	卷边50mm
1636	L40X4	935	4	2.26	9.0	
1637	L40X3	2113	8	3.91	31.3	
1638	L45X4	2882	8	7.89	63.1	
1639	L45X4	4889	8	13.38	107.0	
1640	L45X4	1930	8	5.28	42.2	
1641	L40X3	902	8	1.67	13.4	
1642	-6X152	189	4	1.36	5.4	火曲
1643	-6X152	189	4	1.36	5.4	火曲
1644	-6X180	204	4	1.73	6.9	火曲
1645	-6X180	204	4	1.73	6.9	火曲
1646	-6X173	179	4	1.46	5.8	火曲
1647	-6X173	179	4	1.46	5.8	火曲
1648	-6X145	187	4	1.28	5.1	火曲
1649	-6X145	187	4	1.28	5.1	火曲
1650	-6X172	199	4	1.61	6.4	火曲
1651	-6X172	199	4	1.61	6.4	火曲
1658	Q420L160X14	770	4	26.17	104.7	铲背
1659	Q420-12X155	770	8	11.24	89.9	
1660	-10X592	597	4	27.74	111.0	卷边60mm
1661	-10X592	597	4	27.74	111.0	卷边60mm
1662	-16X60	60	4	0.45	1.8	垫块
合计				5695.2 kg		

螺栓、脚钉、垫圈明细表

名称	级别	规格	符号	数量	重量(kg)	备注
螺栓	6.8级	M16X40		160	23.1	
		M16X50		92	14.7	
		M20X45		104	28.1	
		M20X55		228	67.3	
		M20X65		84	26.9	
	8.8级	M24X75		96	51.5	
		M24X85		96	55.1	
脚钉	6.8级	M16X180		22	7.2	
		M20X200		1	0.6	
	8.8级	M24X240		2	1.8	
垫圈	Q235	-3(Ø17.5)	规格X个数	24	0.3	
合计				276.6 kg		

构件明细表(座板式)

编号	规格	长度(mm)	数量	重量(kg) 一件	重量(kg) 小计	备注
1601	Q420L180X16	10794	1	469.99	470.0	带脚钉
1602	Q420L180X16	10794	3	469.99	1410.0	
1603	Q420L160X12	770	4	22.63	90.5	铲背
1604	L125X8	8309	4	128.79	515.2	切角
1605	L125X8	8309	4	128.79	515.2	切角
1606	L80X7	6560	4	55.92	223.7	
1607	L125X8	3821	4	59.24	237.0	
1608	L125X8	3821	4	59.24	237.0	
1609	L70X5	738	8	3.98	31.8	
1610	L70X5	1501	8	8.10	64.8	
1611	L70X5	1416	8	7.64	61.1	
1612	L63X5	1867	8	9.00	72.0	
1613	L63X5	2094	8	10.10	80.8	
1614	L70X5	2375	8	12.82	102.6	
1615	L70X6	2772	8	17.76	142.1	
1616	L63X5	1703	8	8.21	65.7	
1617	L70X5	2394	8	12.92	103.4	
1618	L70X5	2121	8	11.45	91.6	
1619	L63X5	1755	8	8.46	67.7	
1620	-10X570	745	4	33.34	133.4	卷边60mm
1621	-8X274	277	8	4.77	38.2	
1622	Q345-10X346	429	8	11.65	93.2	
1623	Q420-10X155	770	8	9.37	75.0	
1624	-2X135	380	8	0.81	6.5	
1625	L56X4	3794	2	13.07	26.1	切角
1626	L56X4	3794	2	13.07	26.1	切角
1627	L56X4	3794	2	13.07	26.1	
1628	L56X4	3794	2	13.07	26.1	
1629	L50X4	2311	4	7.07	28.3	
1630	L40X3	570	4	1.06	4.2	
1631	L45X4	1456	4	3.98	15.9	一端压扁
1632	L40X3	792	4	1.47	5.9	
1633	L40X3	792	2	1.47	2.9	切角
1634	L40X3	792	2	1.47	2.9	切角
1635	-5X330	330	4	4.27	17.1	卷边50mm
1636	L40X4	935	4	2.26	9.0	
1637	L40X3	2113	8	3.91	31.3	
1638	L45X4	2882	8	7.89	63.1	
1639	L45X4	4889	8	13.38	107.0	
1640	L45X4	1930	8	5.28	42.2	
1641	L40X3	902	8	1.67	13.4	
1642	-6X152	189	4	1.35	5.4	火曲
1643	-6X152	189	4	1.35	5.4	火曲
1644	-6X180	204	4	1.73	6.9	火曲
1645	-6X180	204	4	1.73	6.9	火曲
1646	-6X173	179	4	1.46	5.8	火曲
1647	-6X173	179	4	1.46	5.8	火曲
1648	-6X145	187	4	1.28	5.1	火曲
1649	-6X145	187	4	1.28	5.1	火曲
1650	-6X172	199	4	1.61	6.4	火曲
1651	-6X172	199	4	1.61	6.4	火曲
1652	Q345-58X600	600	4	163.91	655.6	焊接
1653	Q345-18X542	600	4	45.95	183.8	坡口焊
1654	Q345-18X245	542	4	18.76	75.0	坡口焊
1655	Q345-18X337	542	4	25.81	103.2	坡口焊
1656	Q345-16X150	200	8	3.77	30.2	坡口焊
1657	Q345-16X150	150	8	2.83	22.6	坡口焊
1662	-16X60	60	4	0.45	1.8	垫块
合计				6507.5 kg		

螺栓、脚钉、垫圈明细表

名称	级别	规格	符号	数量	重量(kg)	备注
螺栓	6.8级	M16X40		160	23.1	
		M16X50		92	14.7	
		M20X45		104	28.1	
		M20X55		196	57.9	
		M20X65		68	21.8	
	8.8级	M24X75		160	85.9	
脚钉	6.8级	M16X180		22	7.2	
		M20X200		1	0.6	
	8.8级	M24X240		2	1.8	
垫圈	Q235	-3(Ø17.5)	规格X个数	24	0.3	
合计				241.4 kg		

甘肃电通电力工程设计咨询有限公司

甘肃庆阳能化电厂330千伏送出工程	工程	施工图	设计阶段

批准	曹晓青	
审核	王公阳	
	丁国鹏	
校核	王文军	
设计	段增强	
CAD制图	段增强	
比例		
日期	2026年7月	

330-KC22D-DJ终端塔 (16)
21.0m 腿部结构图

图号 330-KC22D-DJ-17(1/2)