


铁塔根开及基础根开表				
呼高	铁塔根开 2Lt	基础根开 2Lj	底脚螺栓根开 Ld	底脚板螺栓直径及个数
15.0m	7200	7290	370	4M64
18.0m	8040	8130		
21.0m	8880	8970		
24.0m	9720	9810		
27.0m	10540	10640		
30.0m	11380	11480		

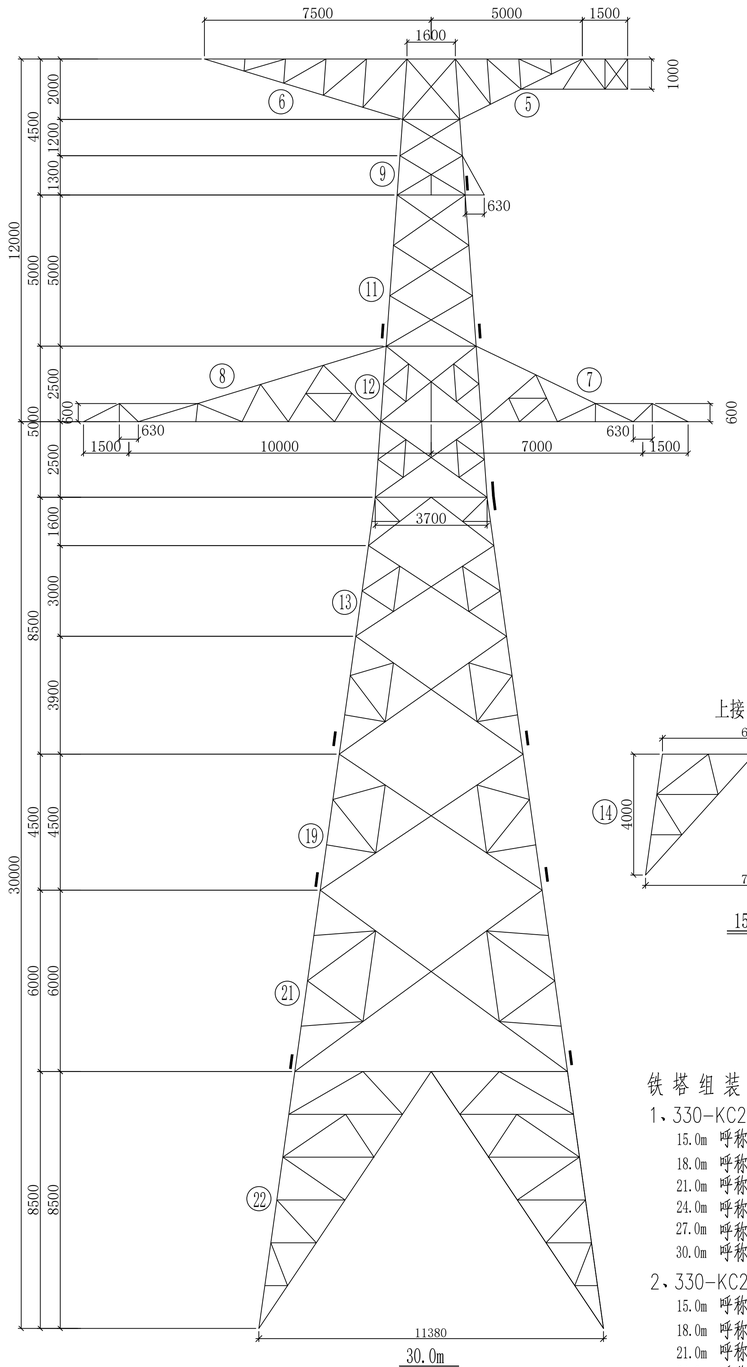


30.0m

330-KC22D-DJ (40°-90°)

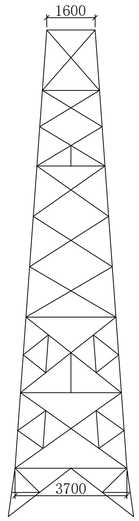


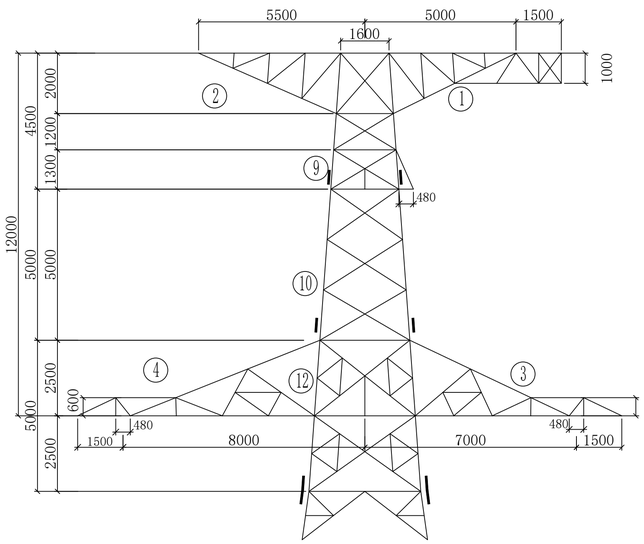

330-KC22D-DJ (0°-40°)

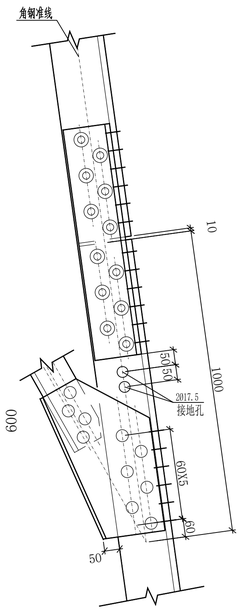


用于插入式基础详图

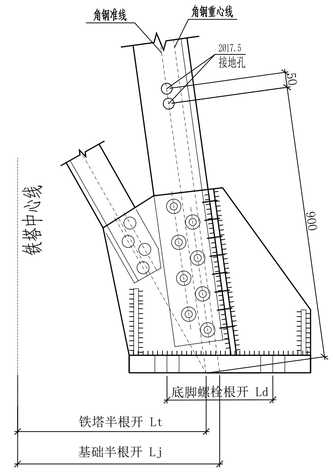


用于座板式基础详图

上接⑬段

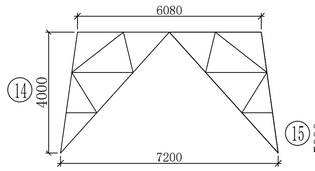


15.0m

上接⑬段

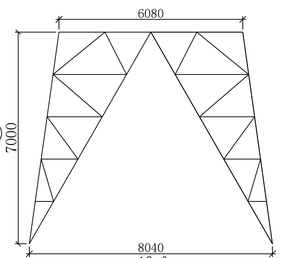


18.0m

上接⑬段

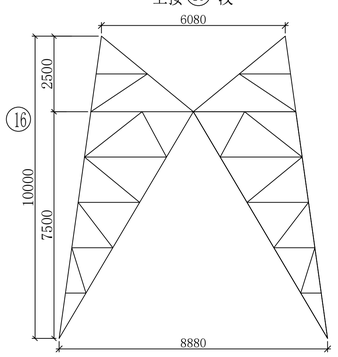


21.0m

上接⑬段

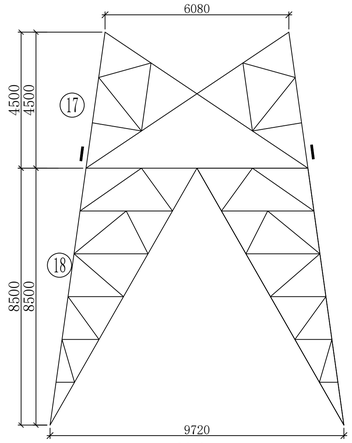

24.0m

上接⑬段

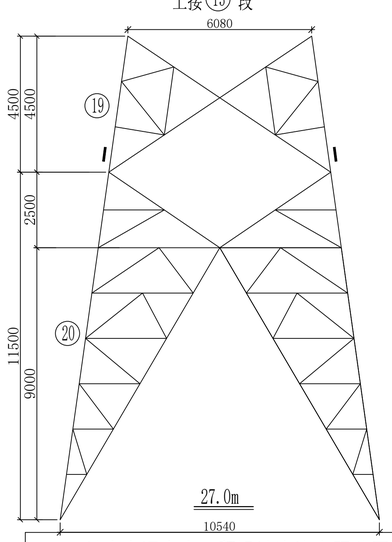

27.0m


铁塔组装说明:

1、330-KC22D-DJ (0°-40°)各呼高的组成如图所示:


15.0m 呼称高包括 ①、④段和⑨⑩⑫⑬⑭段.
18.0m 呼称高包括 ①、④段和⑨⑩⑫⑬⑮段.
21.0m 呼称高包括 ①、④段和⑨⑩⑫⑬⑯段.
24.0m 呼称高包括 ①、④段和⑨⑩⑫⑬⑰⑱段.
27.0m 呼称高包括 ①、④段和⑨⑩⑫⑬⑲⑳段.
30.0m 呼称高包括 ①、④段和⑨⑩⑫⑬⑲㉑㉒段.

2、330-KC22D-DJ (40°-90°))各呼高的组成如图所示:

15.0m 呼称高包括 ⑤、⑨段和⑪⑫⑬⑭段.
18.0m 呼称高包括 ⑤、⑨段和⑪⑫⑬⑮段.
21.0m 呼称高包括 ⑤、⑨段和⑪⑫⑬⑯段.
24.0m 呼称高包括 ⑤、⑨段和⑪⑫⑬⑰⑱段.
27.0m 呼称高包括 ⑤、⑨段和⑪⑫⑬⑲⑳段.
30.0m 呼称高包括 ⑤、⑨段和⑪⑫⑬⑲㉑㉒段.

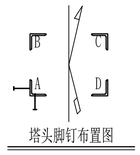

塔头脚钉布置图

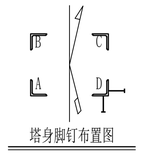

塔身脚钉布置图

甘肃电通电力工程设计咨询有限公司

甘肃庆阳能化电厂330千伏送出工程	工程	施工图	设计阶段
批准	曹晓青		330-KC22D-DJ转角塔 总图及材料汇总表
审核	王公阳		
	丁国鹏		
校核	王文军		
设计	段增强		
CAD制图	段增强		
比例			
日期	2026年7月	图号	330-KC22D-DJ-01(1/2)