各呼称高塔段组合表
（本体及等长接腿重量合计表）

呼称高(m)	90.0			93.0			96.0			99.0		
基本塔身段号	①~⑰㉓(Z1)~(Z6)(P1)(P2)			①~⑰㉓(Z1)~(Z6)(P1)(P2)			①~⑰㉓(Z1)~(Z6)(P1)(P2)			①~⑲㉔(Z1)~(Z6)(P1)(P2)		
	接腿	段号	重量	接腿	段号	重量	接腿	段号	重量	接腿	段号	重量
	90.0-4.5	㉗X4	231486.5	93.0-4.5	㉙X4	236455.3	96.0-4.5	㉛X4	242090.9	99.0-4.5	㉟X4	259044.5
	90.0-3.0	㉘X4	234082.8	93.0-3.0	㉚X4	239479.2	96.0-3.0	㉜X4	246495.0	99.0-3.0	㊱X4	261023.4
	90.0-1.5	㉙X4	236455.3	93.0-1.5	㉛X4	242090.9	96.0-1.5	㉝X4	250262.4	99.0-1.5	㊲X4	264369.3
	90.0-0.0	㉚X4	239479.2	93.0-0.0	㉜X4	246495.0	96.0-0.0	㉞X4	252568.0	99.0-0.0	㊳X4	269278.5

呼称高(m)	102.0			105.0			108.0			111.0		
基本塔身段号	①~⑲㉔(Z1)~(Z6)(P1)(P2)			①~⑲㉔(Z1)~(Z6)(P1)(P2)			①~⑲㉕(Z1)~(Z6)(P1)(P2)			①~⑲㉕(Z1)~(Z6)(P1)(P2)		
	接腿	段号	重量	接腿	段号	重量	接腿	段号	重量	接腿	段号	重量
	102.0-4.5	㊲X4	264369.3	105.0-4.5	㊴X4	272346.5	108.0-4.5	㊸X4	280915.2	111.0-4.5	㊺X4	286197.6
	102.0-3.0	㊳X4	269278.5	105.0-3.0	㊵X4	274889.8	108.0-3.0	㊹X4	283799.1	111.0-3.0	㊻X4	291729.6
	102.0-1.5	㊴X4	272346.5	105.0-1.5	㊶X4	277114.4	108.0-1.5	㊺X4	286197.6	111.0-1.5	㊼X4	294868.3
	102.0-0.0	㊵X4	274889.8	105.0-0.0	㊷X4	282231.1	108.0-0.0	㊻X4	291729.6	111.0-0.0	㊽X4	297836.2

呼称高(m)	114.0			117.0			120.0			123.0		
基本塔身段号	①~⑲㉕(Z1)~(Z6)(P1)(P2)			①~⑲㉕(Z1)~(Z6)(P1)(P2)			①~㉑㉖(Z1)~(Z6)(P1)(P3)			①~㉑㉖(Z1)~(Z6)(P1)(P3)		
	接腿	段号	重量	接腿	段号	重量	接腿	段号	重量	接腿	段号	重量
	114.0-4.5	㊼X4	294868.3	117.0-4.5	㊾X4	300287.0	120.0-4.5	(53)X4	330431.2	123.0-4.5	(55)X4	337138.4
	114.0-3.0	㊽X4	297836.2	117.0-3.0	㊿X4	304162.3	120.0-3.0	(54)X4	332936.1	123.0-3.0	(56)X4	343378.6
	114.0-1.5	㊾X4	300287.0	117.0-1.5	(51)X4	307435.6	120.0-1.5	(55)X4	337138.4	123.0-1.5	(57)X4	346203.2
	114.0-0.0	㊿X4	304162.3	117.0-0.0	(52)X4	310601.2	120.0-0.0	(56)X4	343378.6	123.0-0.0	(58)X4	349165.0

呼称高(m)	126.0			129.0			132.0			135.0		
基本塔身段号	①~㉑㉖(Z1)~(Z6)(P1)(P3)			①~㉑㉖(Z1)~(Z6)(P1)(P3)			①~㉑㉒(Z1)~(Z6)(P1)(P3)			①~㉑㉒(Z1)~(Z6)(P1)(P3)		
	接腿	段号	重量	接腿	段号	重量	接腿	段号	重量	接腿	段号	重量
	126.0-4.5	(57)X4	346203.2	129.0-4.5	(59)X4	353055.4	132.0-4.5	(63)X4	367000.1	135.0-4.5	(65)X4	374383.1
	126.0-3.0	(58)X4	349165.0	129.0-3.0	(60)X4	357814.3	132.0-3.0	(64)X4	370611.3	135.0-3.0	(66)X4	380084.1
	126.0-1.5	(59)X4	353055.4	129.0-1.5	(61)X4	361315.2	132.0-1.5	(65)X4	374383.1	135.0-1.5	(67)X4	383971.5
	126.0-0.0	(60)X4	357814.3	129.0-0.0	(62)X4	364523.3	132.0-0.0	(66)X4	380084.1	135.0-0.0	(68)X4	389396.7

说明: 此表格1个主材带爬梯和3个主材带脚钉的重量。

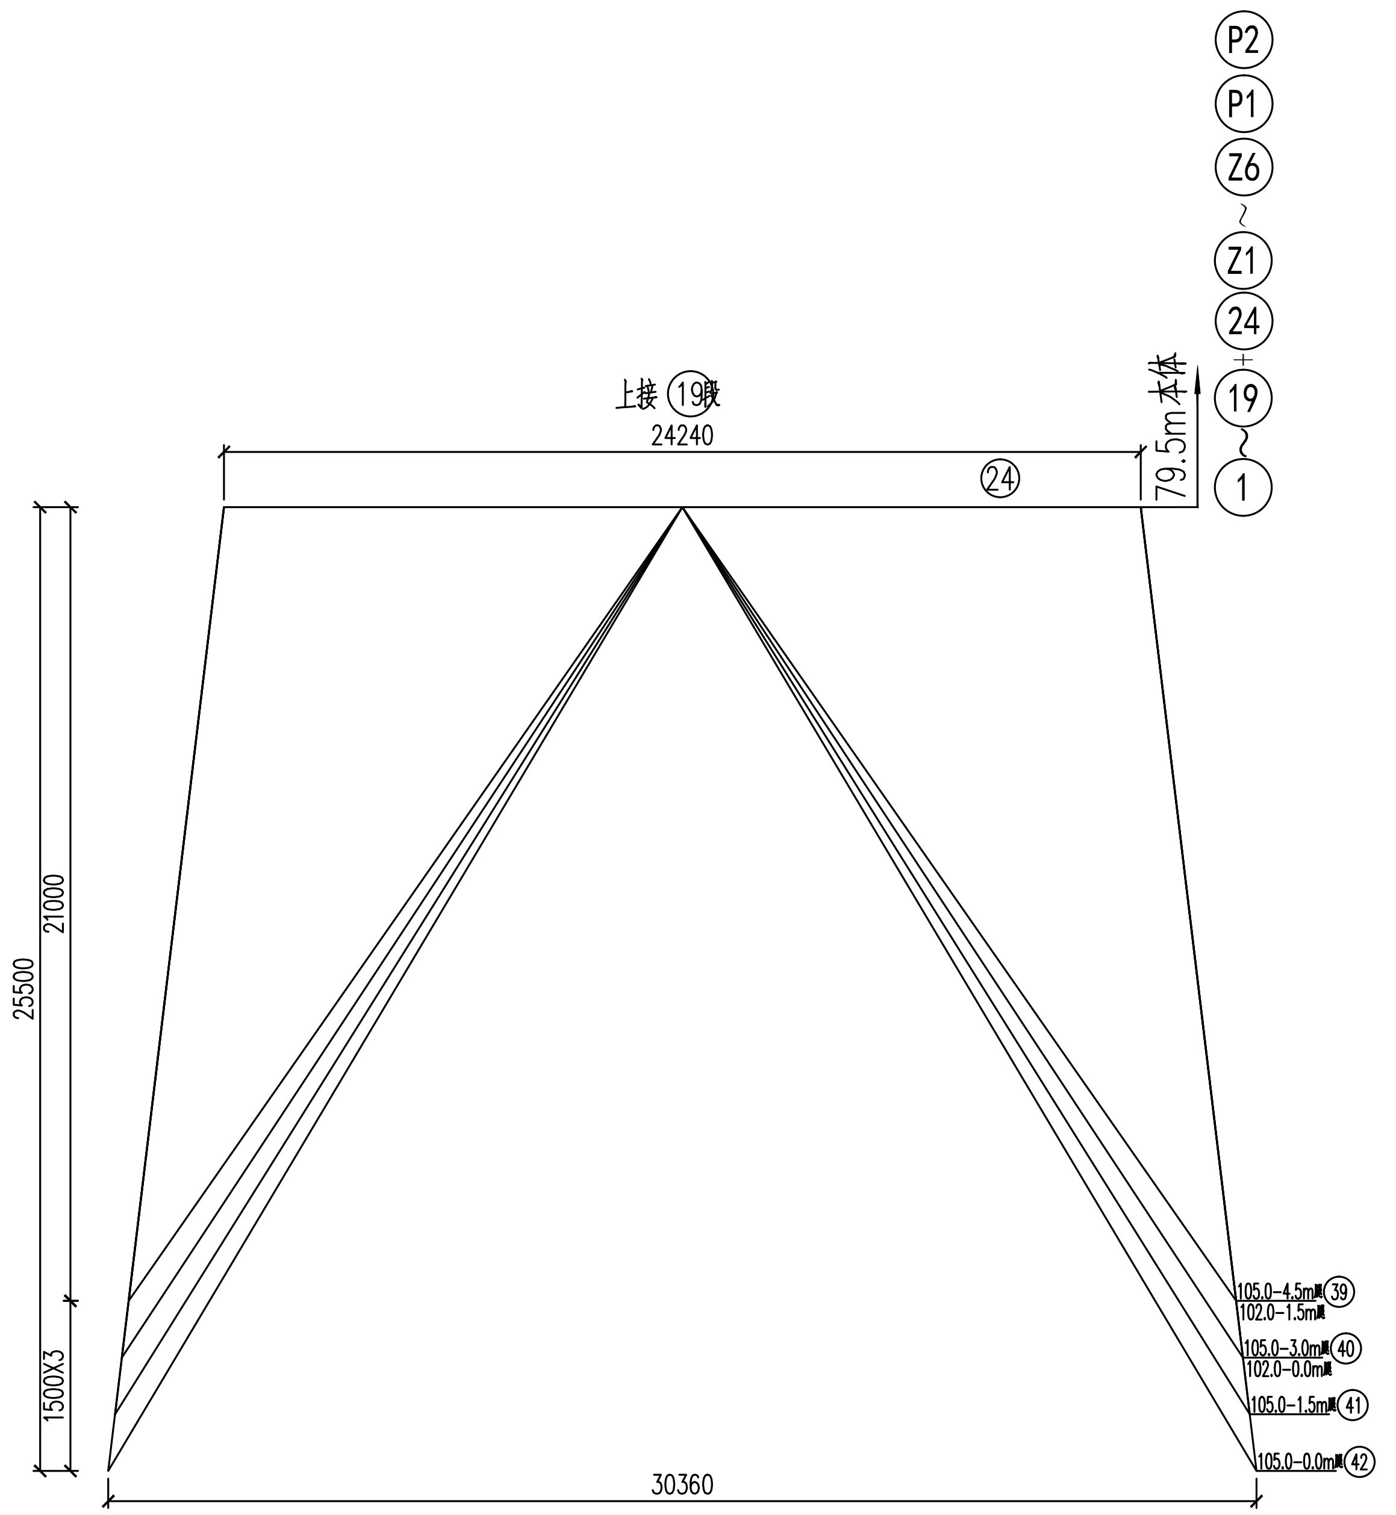

105.0m呼高

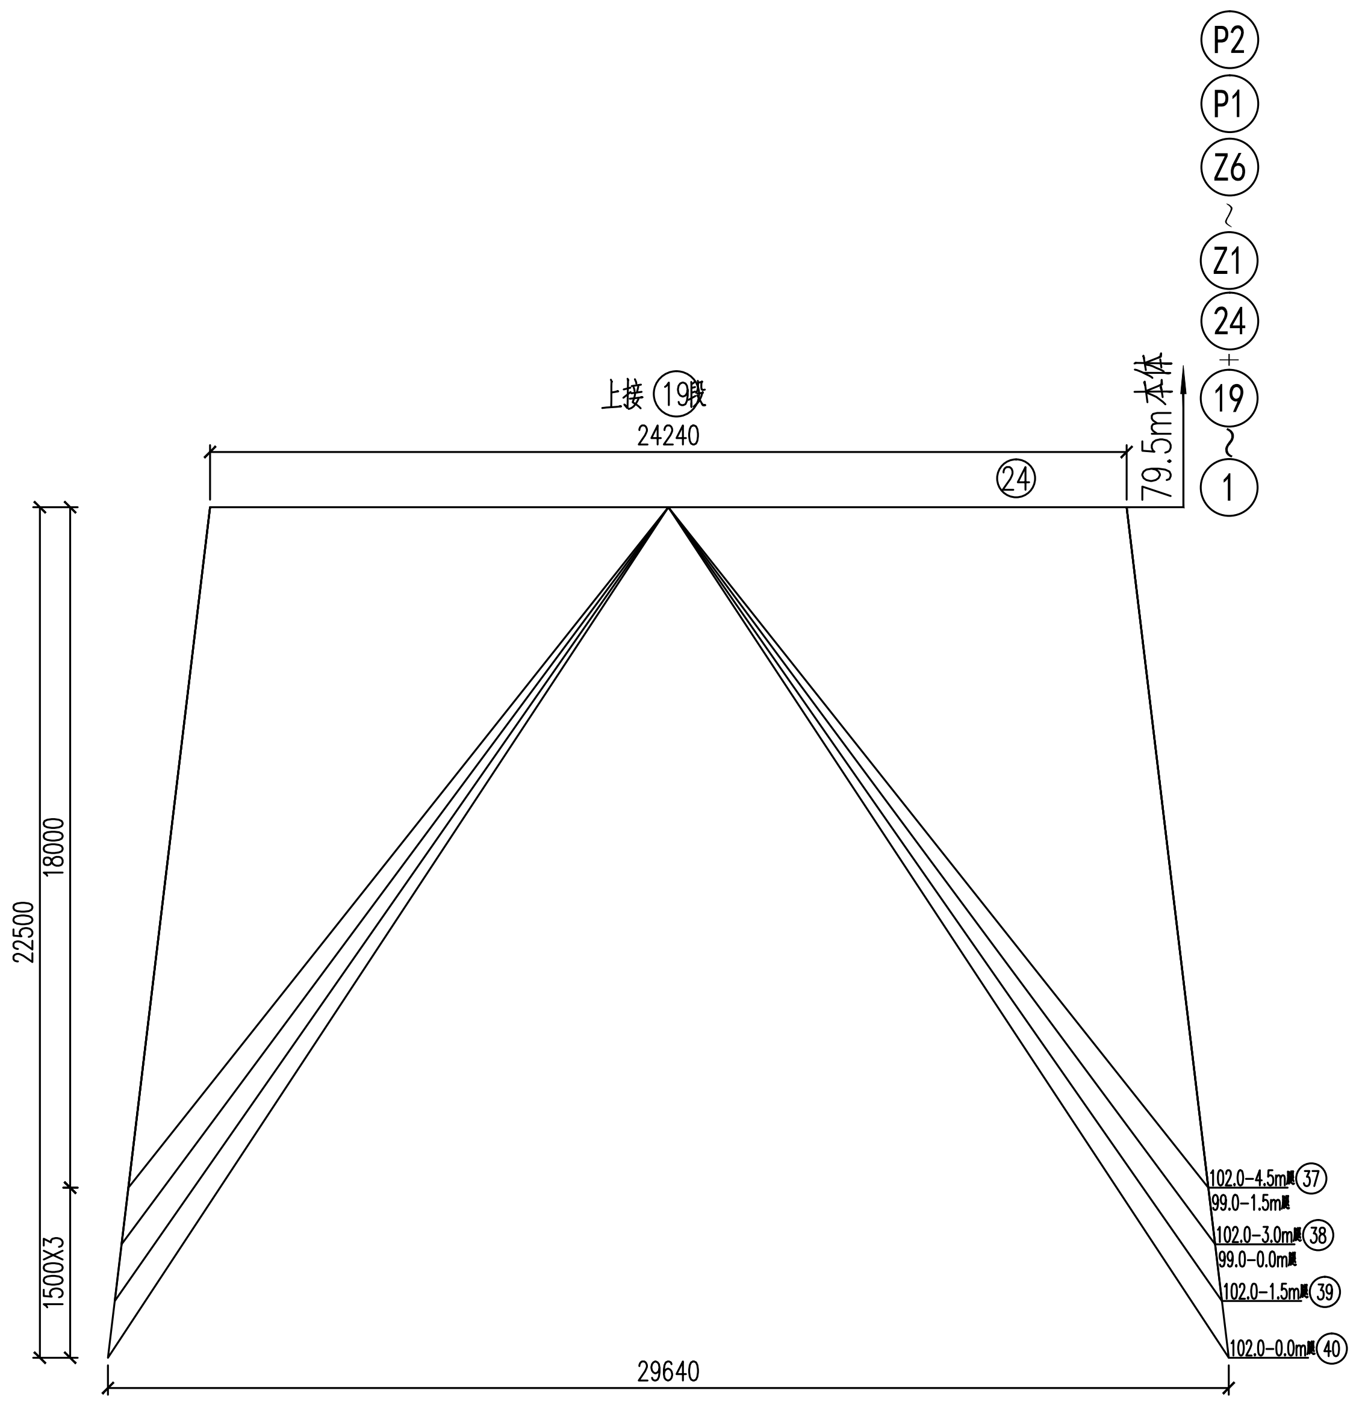

102.0m呼高

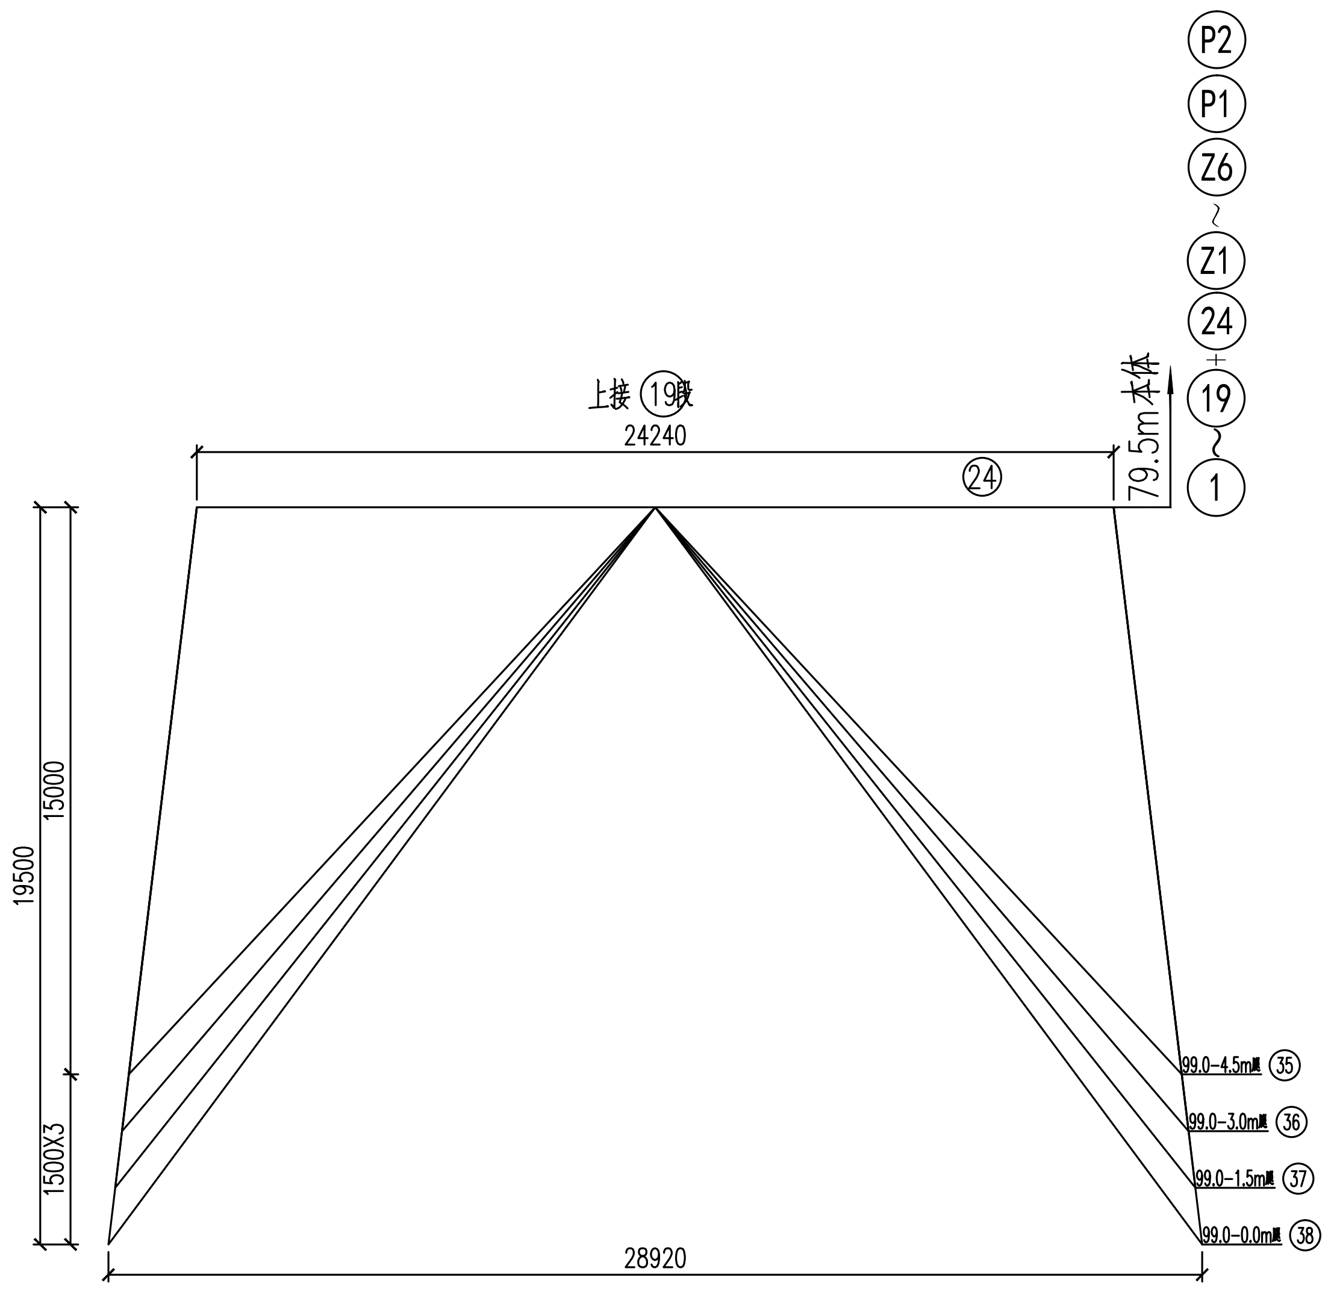

99.0m呼高

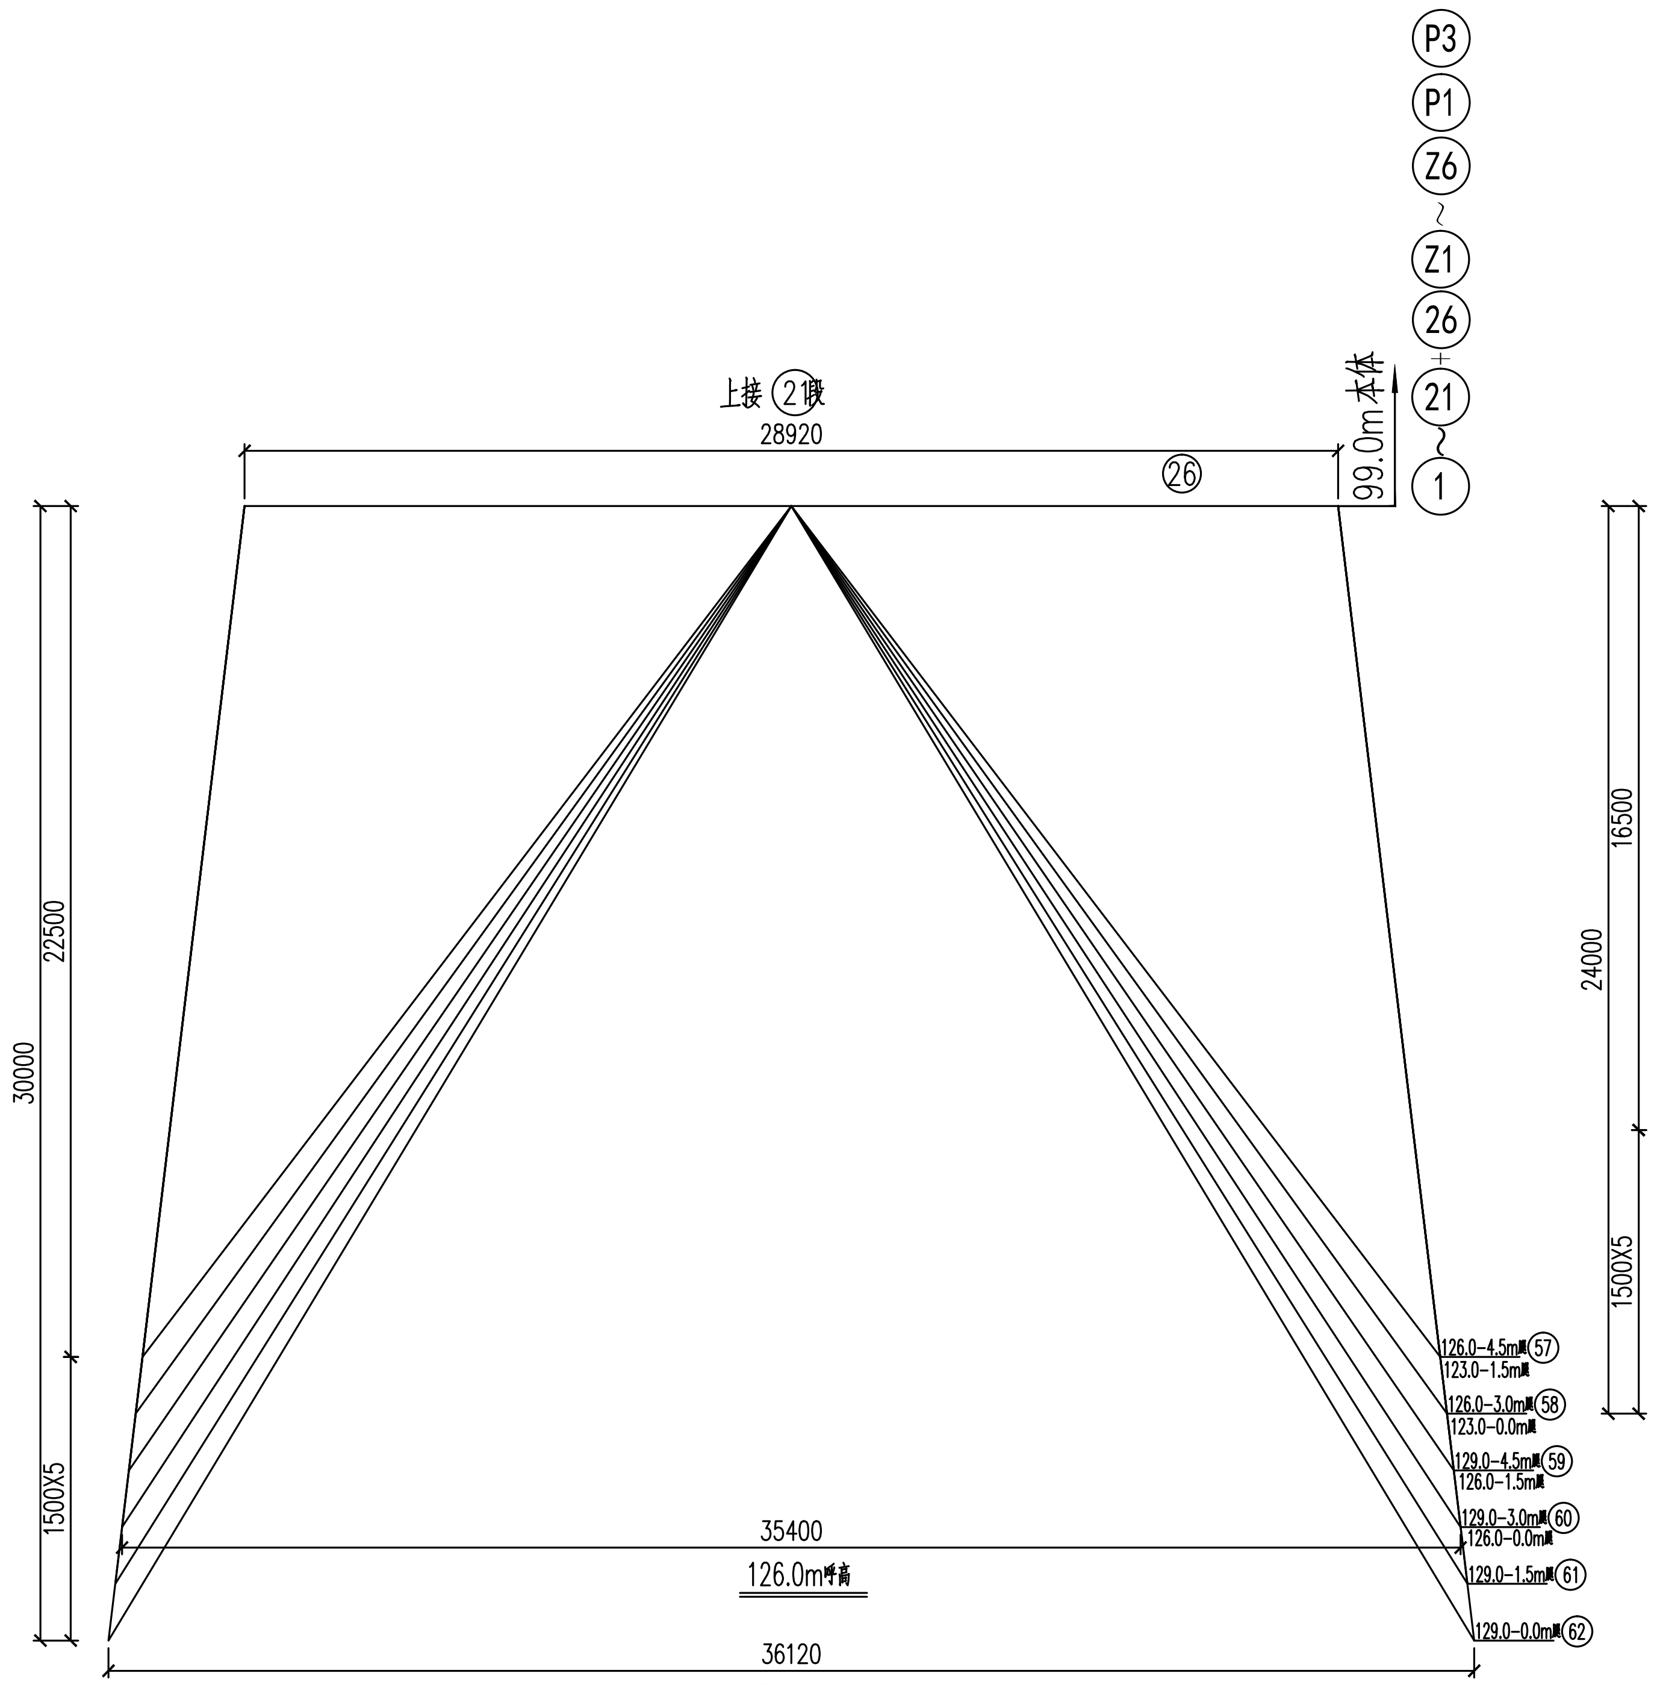

126.0m呼高

129.0m呼高

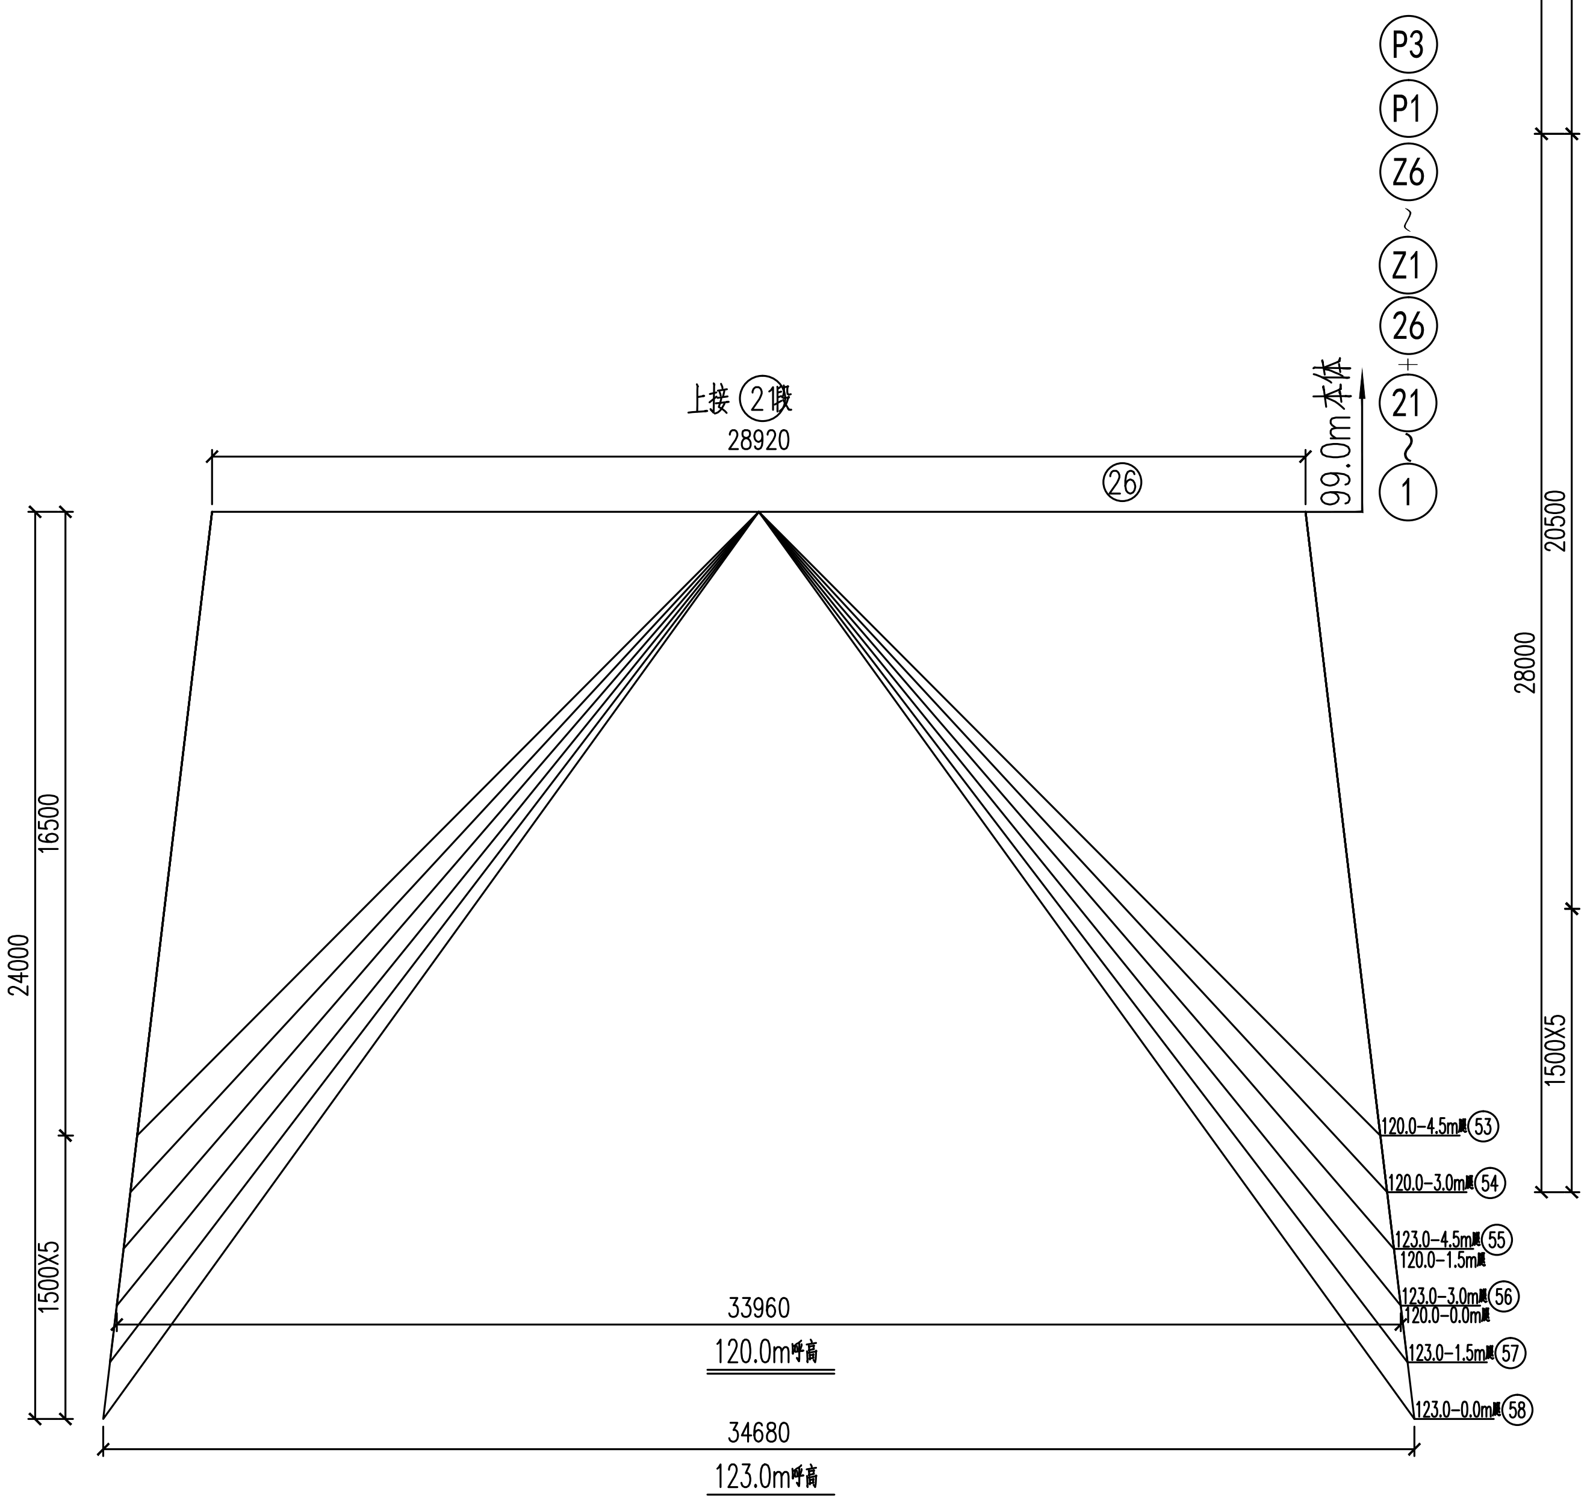

120.0m呼高

123.0m呼高

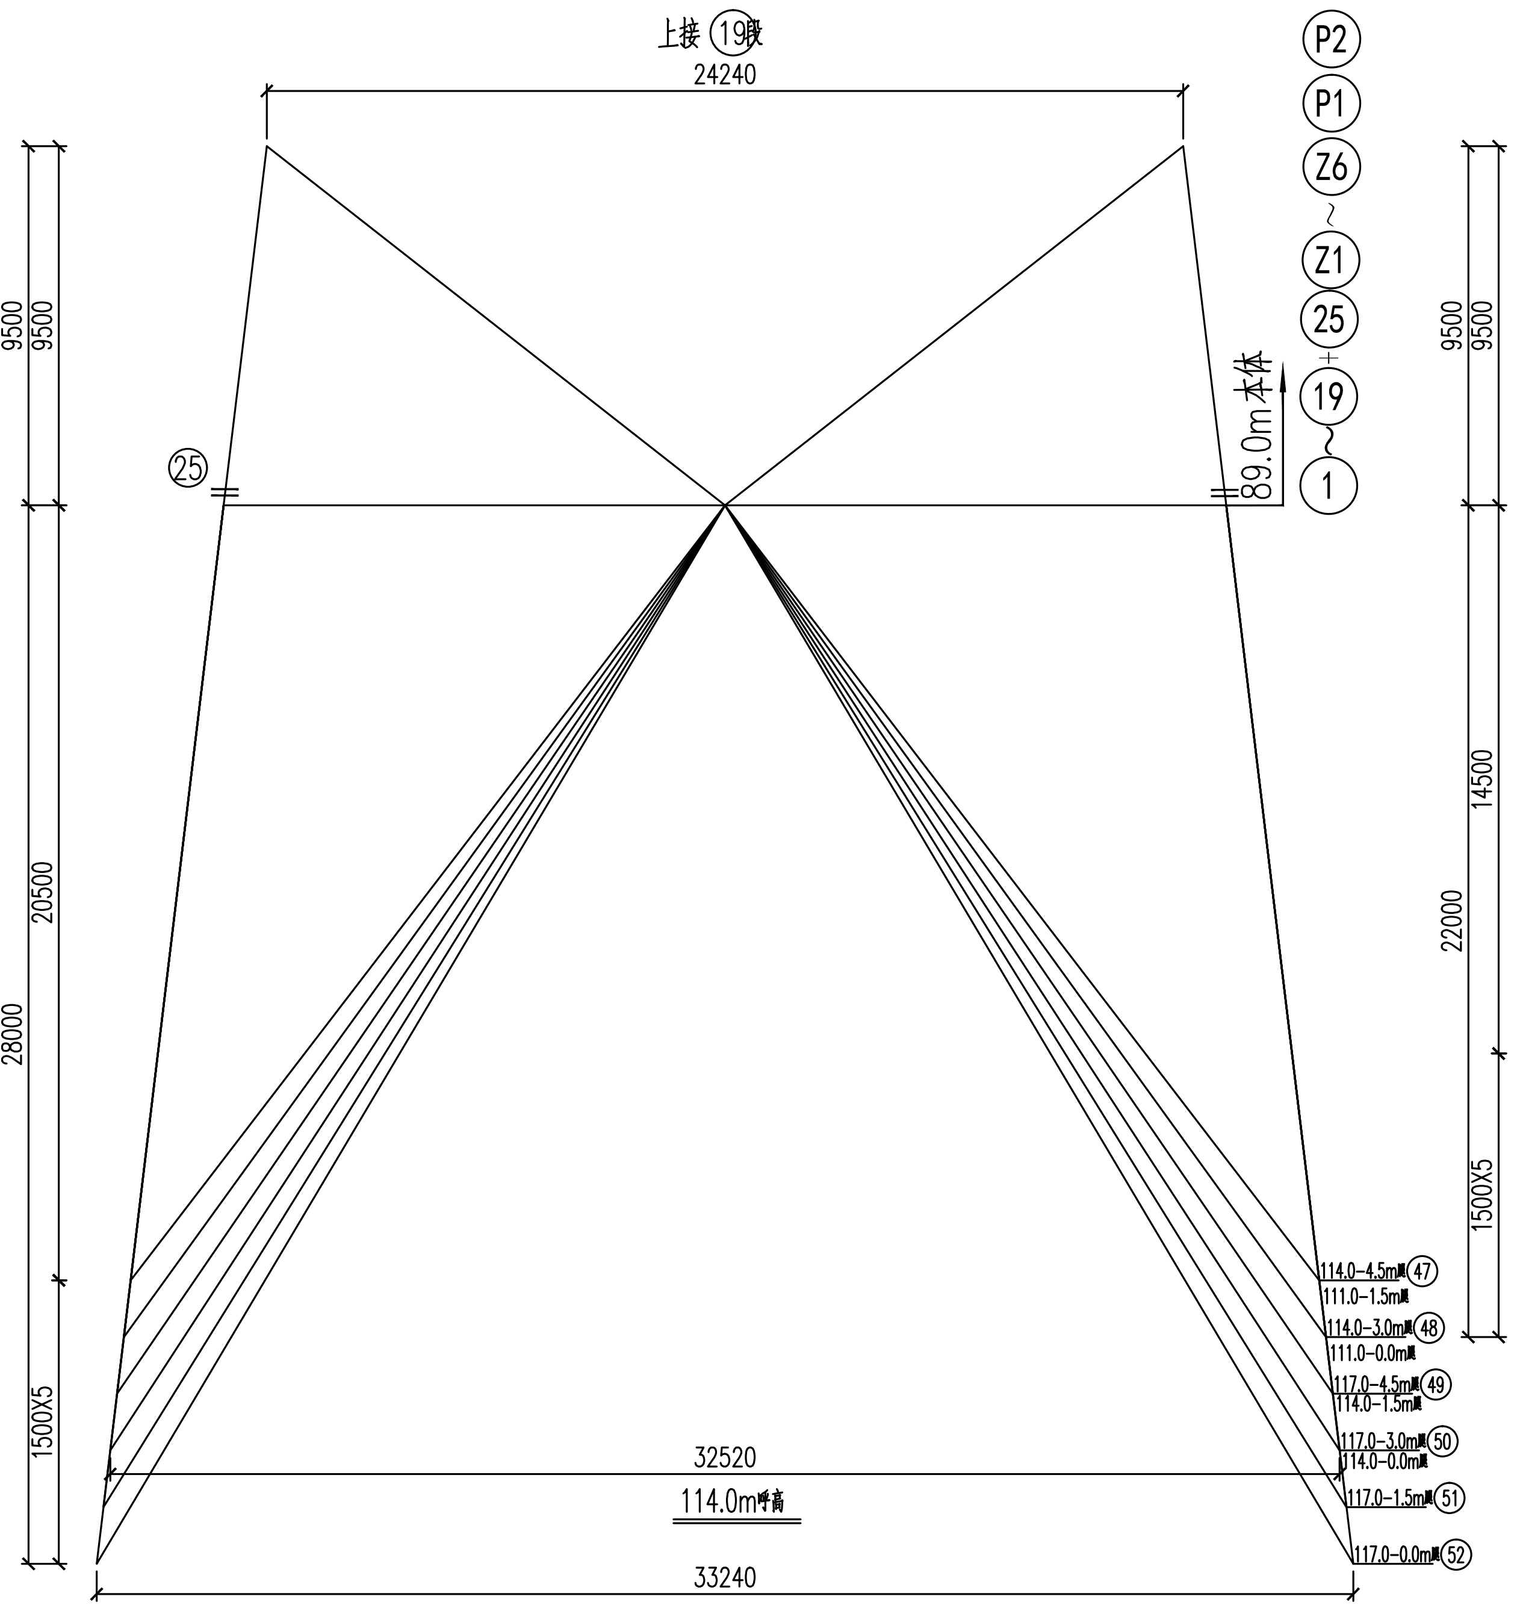

114.0m呼高

117.0m呼高

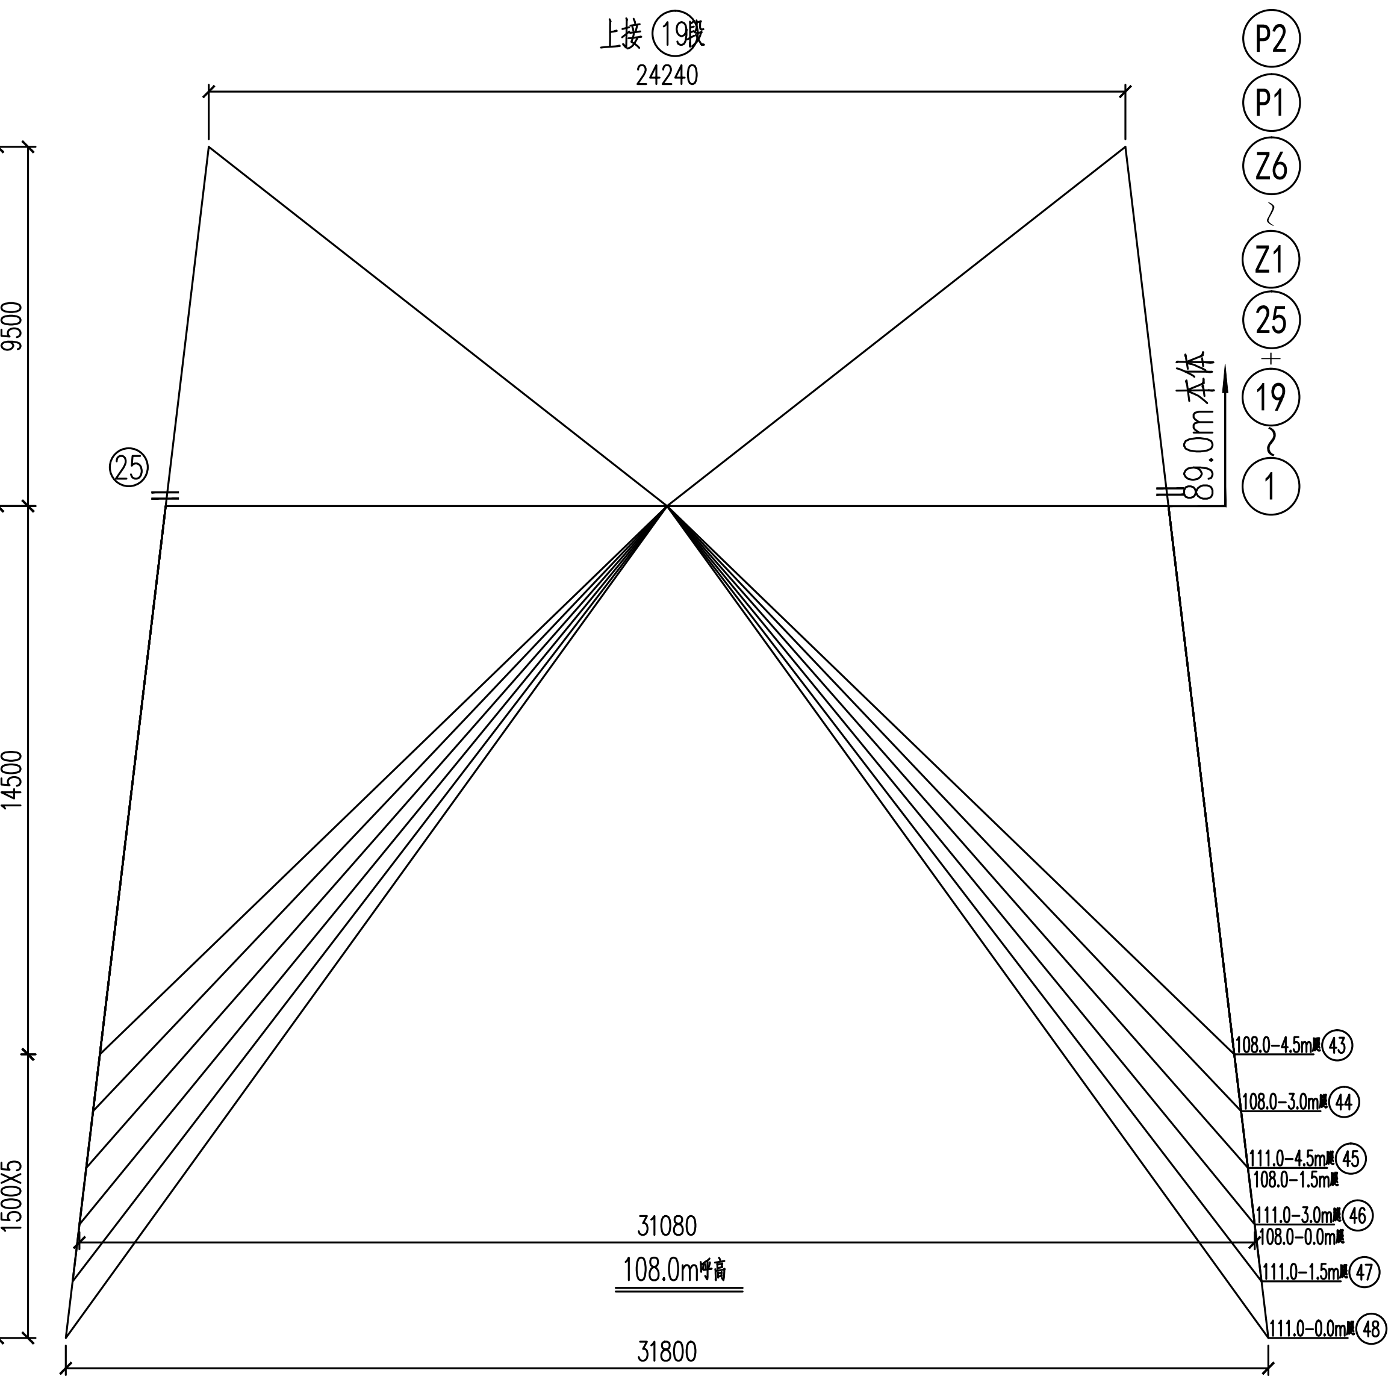

108.0m呼高

111.0m呼高

山东电力工程咨询院有限公司
浙江特高压交流环网工程线路 工程
施工图 设计阶段
批 准 雷强
审 核 高锡鹏
校 核 马一丹
设计/勘测
比 例 1:200
日 期 2026年 08月
SZK31102A双回路直线塔
总图及材料汇总表(2/3)
图 号 37-SA36901S-T0121-002
版本
电 气 赵庆周 2026.08
专 业 会 签 日 期