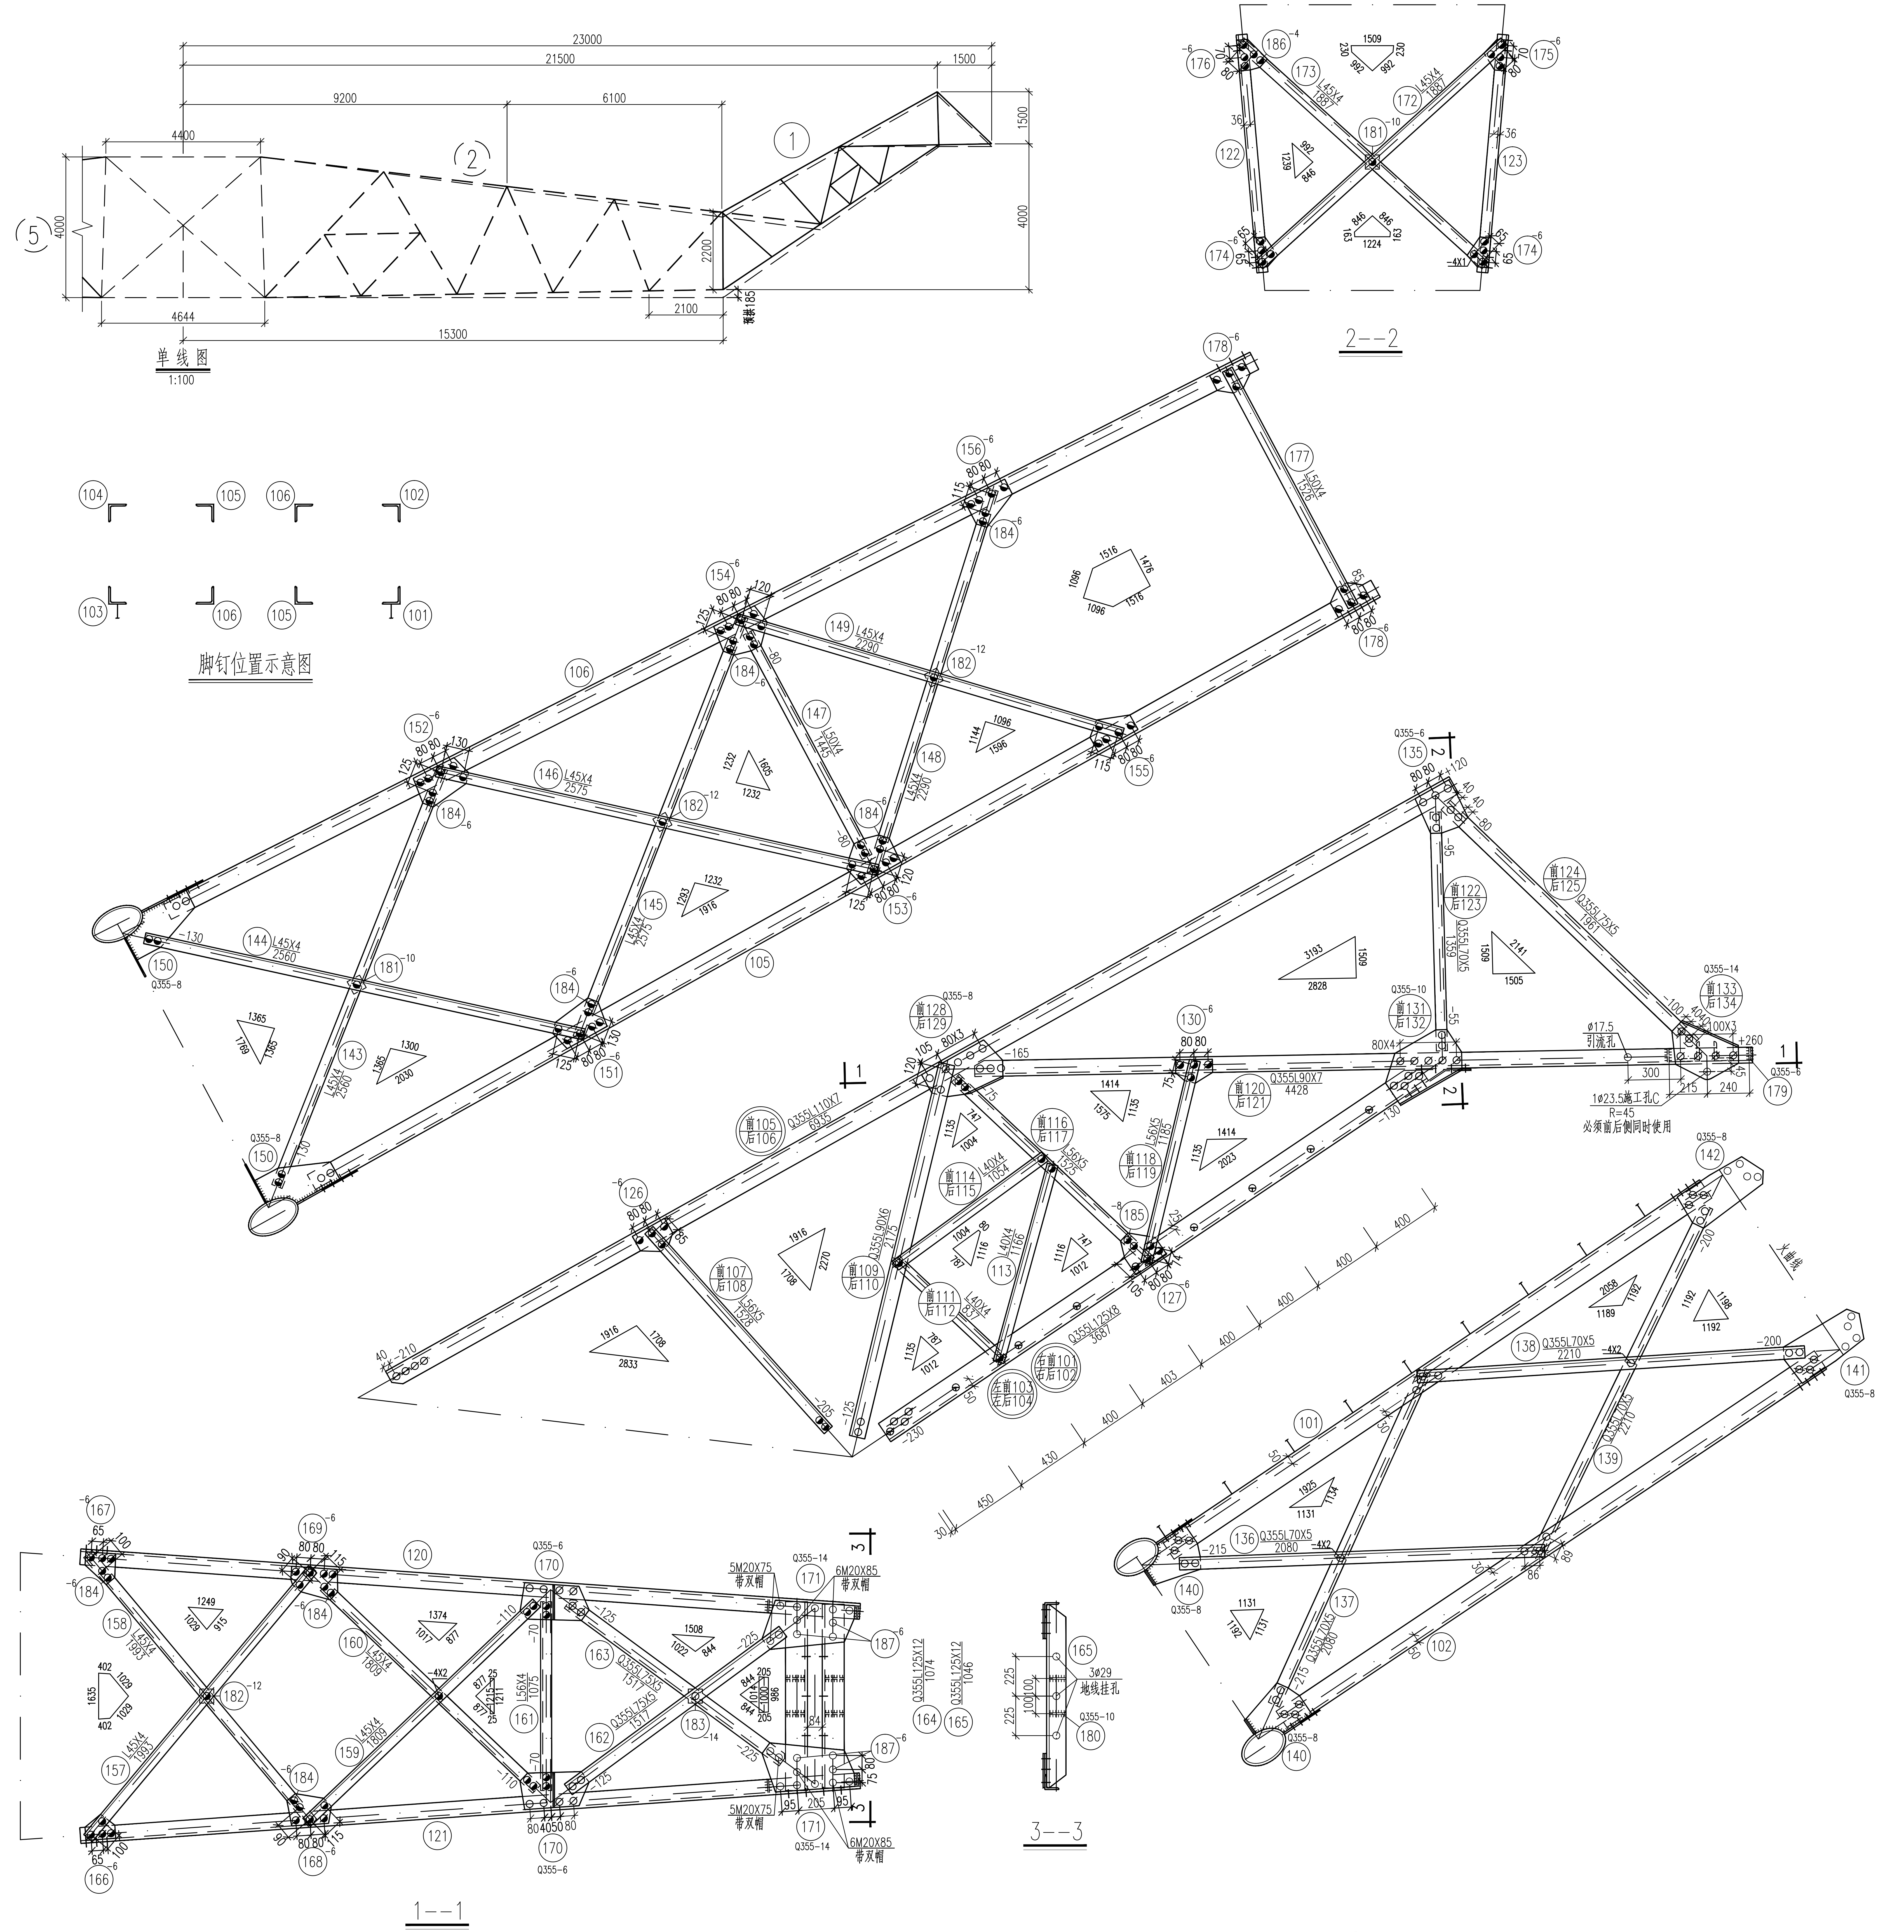

单线图 1:100

2--2

脚钉位置示意图

1--1

3--3

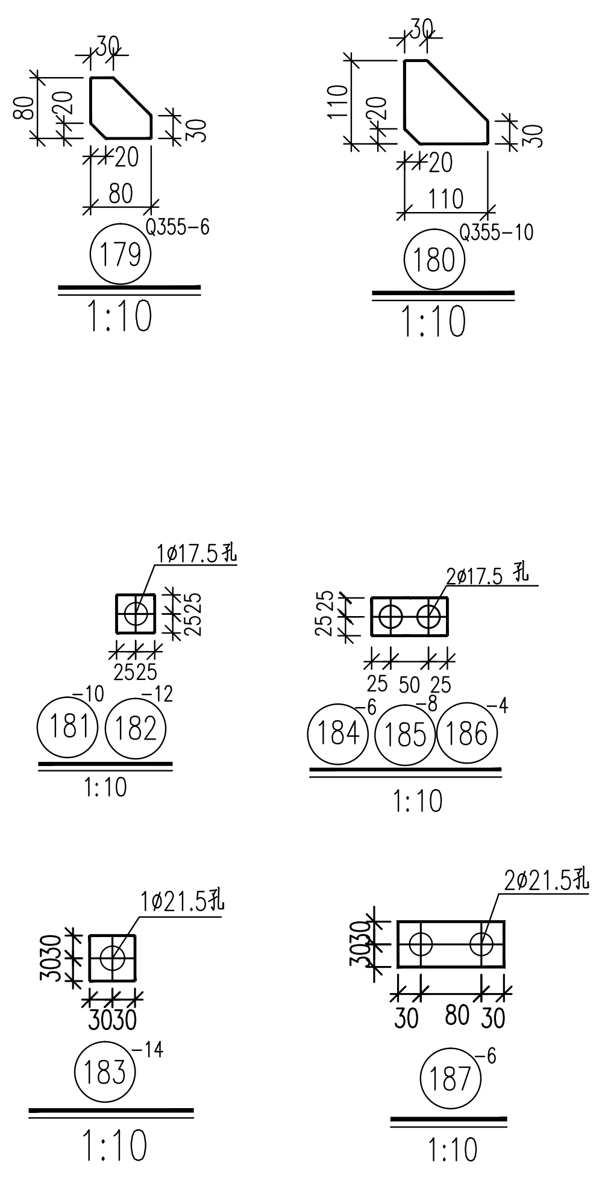

1:10

1:10

1:10

1:10

1:10

1:10

构 件 明 细 表

编号	规 格	长 度 (mm)	数量	重 量 (kg) 一 件	重 量 (kg) 小 计	备 注
180	Q355-10X110	110	8	0.95	7.6	电焊
181	-10X50	50	4	0.20	0.8	垫块
182	-12X50	50	6	0.24	1.4	垫块
183	-14X60	60	2	0.34	0.7	垫块
184	-6X50	100	16	0.24	3.8	垫块
185	-8X50	100	4	0.31	1.2	垫块
186	-4X50	100	2	0.16	0.3	垫块
187	-6X60	140	8	0.40	3.2	垫块
合 计		1808.4 kg				

螺栓、脚钉、垫圈明细表

名称	级别	规 格	符 号	数量	重量(kg)	备 注
螺栓	6.8级	M16X45	⊘	84	14.2	
		M16X55	⊘	202	37.3	
		M16X65	⊗	4	0.8	
		M20X55	○	108	35.4	
		M20X65	∅	114	40.2	
		M20X75S	○	20	8.0	带双帽
		M20X85S	○	24	10.2	带双帽
脚钉	6.8级	M16X185	⊖	16	6.6	
垫圈	Q235	-4(ø17.5)	规格X个数	6	0.1	
		-4(ø22)		8	0.2	
合 计			153.0 kg			

注：材料表为2个地线支架的重量
　　1 2 段需同时预拱。

构 件 明 细 表

编号	规 格	长 度 (mm)	数量	重 量 (kg) 一 件	重 量 (kg) 小 计	备 注
101	Q355L125X8	3687	1	57.16	57.2	局部合角 切角 带脚钉
102	Q355L125X8	3687	1	57.16	57.2	局部合角 切角
103	Q355L125X8	3687	1	57.16	57.2	局部合角 切角 带脚钉
104	Q355L125X8	3687	1	57.16	57.2	局部合角 切角
105	Q355L110X7	6935	2	82.72	165.4	局部开角 切角
106	Q355L110X7	6935	2	82.72	165.4	局部开角 切角
107	L56X5	1528	2	6.50	13.0	
108	L56X5	1528	2	6.50	13.0	
109	Q355L90X6	2175	2	18.16	36.3	
110	Q355L90X6	2175	2	18.16	36.3	
111	L40X4	837	2	2.03	4.1	切角
112	L40X4	837	2	2.03	4.1	切角
113	L40X4	1166	4	2.83	11.3	
114	L40X4	1054	2	2.55	5.1	切角
115	L40X4	1054	2	2.55	5.1	切角
116	L56X5	1525	2	6.48	13.0	切角
117	L56X5	1525	2	6.48	13.0	切角
118	L56X5	1185	2	5.04	10.1	
119	L56X5	1185	2	5.04	10.1	
120	Q355L90X7	4428	2	42.76	85.5	局部合角 切角 电焊
121	Q355L90X7	4428	2	42.76	85.5	局部合角 切角 电焊
122	Q355L70X5	1359	2	6.55	13.1	局部开角
123	Q355L70X5	1359	2	6.55	13.1	局部开角
124	Q355L75X5	1961	2	11.41	22.8	切角
125	Q355L75X5	1961	2	11.41	22.8	切角
126	-6X155	210	4	1.53	6.1	
127	-6X210	223	4	2.21	8.8	
128	Q355-8X324	487	2	9.91	19.8	卷边60mm
129	Q355-8X324	487	2	9.91	19.8	卷边60mm
130	-6X135	231	4	1.47	5.9	
131	Q355-10X352	514	2	14.20	28.4	卷边60mm
132	Q355-10X352	514	2	14.20	28.4	卷边60mm
133	Q355-14X333	463	2	16.94	33.9	卷边60mm
134	Q355-14X333	463	2	16.94	33.9	卷边60mm
135	Q355-6X240	288	4	3.26	13.0	
136	Q355L70X5	2080	2	11.23	22.5	
137	Q355L70X5	2080	2	11.23	22.5	切角
138	Q355L70X5	2210	2	11.93	23.9	
139	Q355L70X5	2210	2	11.93	23.9	切角
140	Q355-8X286	358	4	6.43	25.7	
141	Q355-8X251	550	2	8.67	17.3	火曲
142	Q355-8X251	550	2	8.67	17.3	火曲
143	L45X4	2560	2	7.01	14.0	切角
144	L45X4	2560	2	7.01	14.0	
145	L45X4	2575	2	7.05	14.1	切角
146	L45X4	2575	2	7.05	14.1	
147	L50X4	1445	2	4.42	8.8	
148	L45X4	2290	2	6.27	12.5	切角
149	L45X4	2290	2	6.27	12.5	
150	Q355-8X244	472	4	7.23	28.9	
151	-6X195	312	2	2.87	5.7	
152	-6X197	311	2	2.89	5.8	
153	-6X221	297	2	3.09	6.2	
154	-6X221	297	2	3.09	6.2	
155	-6X163	260	2	2.00	4.0	
156	-6X199	260	2	2.44	4.9	
157	L45X4	1993	2	5.45	10.9	
158	L45X4	1993	2	5.45	10.9	切角
159	L45X4	1809	2	4.95	9.9	
160	L45X4	1809	2	4.95	9.9	切角
161	L56X4	1075	2	3.70	7.4	
162	Q355L75X5	1517	2	8.83	17.7	
163	Q355L75X5	1517	2	8.83	17.7	
164	Q355L125X12	1074	2	20.55	41.1	切角 电焊
165	Q355L125X12	1046	2	20.01	40.0	切角 电焊
166	-6X143	170	2	1.15	2.3	
167	-6X174	179	2	1.47	2.9	
168	-6X182	251	2	2.15	4.3	
169	-6X176	271	2	2.25	4.5	
170	Q355-6X227	431	4	4.61	18.4	
171	Q355-14X302	567	4	16.13	64.5	
172	L45X4	1887	2	5.16	10.3	
173	L45X4	1887	2	5.16	10.3	切角
174	-6X127	170	4	1.02	4.1	
175	-6X131	175	2	1.08	2.2	
176	-6X165	175	2	1.36	2.7	
177	L50X4	1526	2	4.67	9.3	
178	-6X151	210	4	1.49	6.0	
179	Q355-6X80	80	8	0.30	2.4	电焊

			山东电力工程咨询院有限公司				浙江特高压交流环网工程线路 工程	施工图 设计阶段
			批 准	雷强	校 核	马一丹	SZK31102A直线塔 ① 地线支架结构图	
			审 核	高锡鹏				
电 气	赵庆周	2026.08			设计/勘测	潘胜光		
专 业	会 签	日 期	比 例		日 期	2026年 08月	图 号 37-SA36901S-T0121-004	版本