





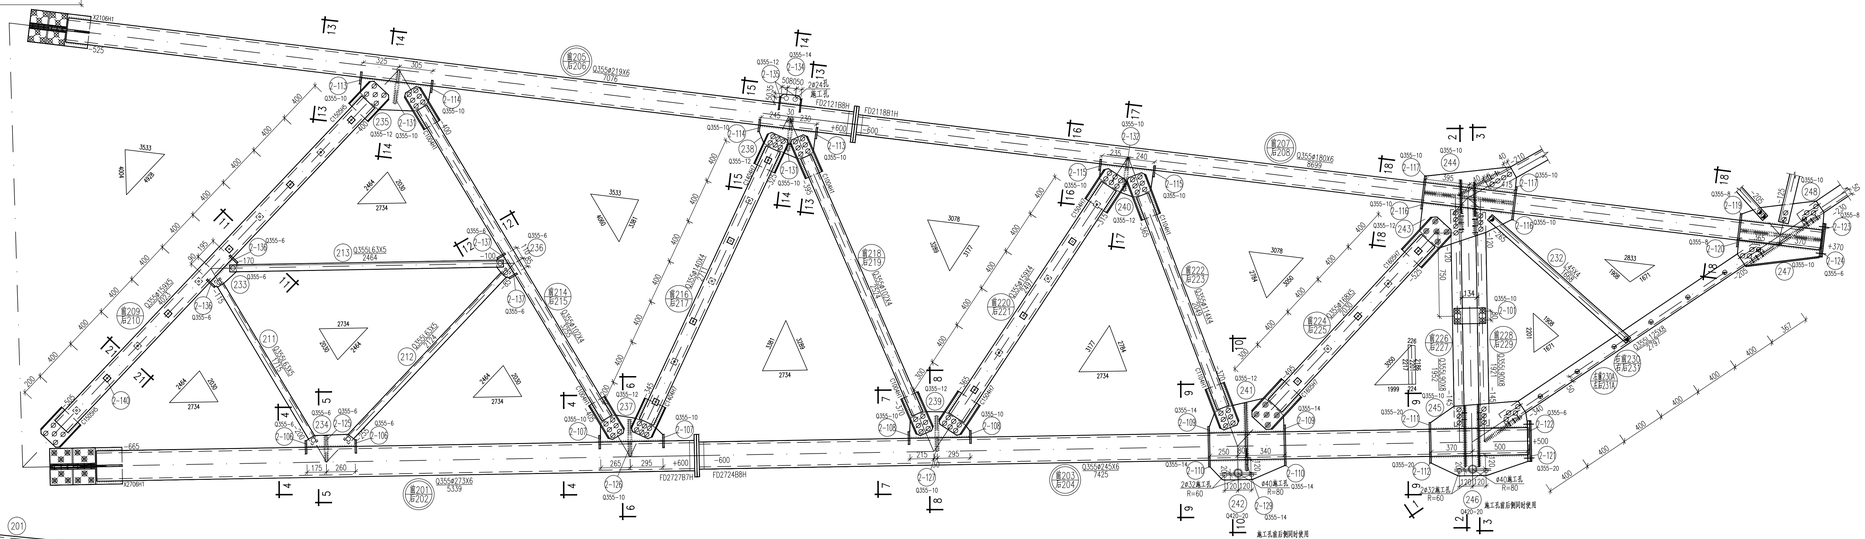

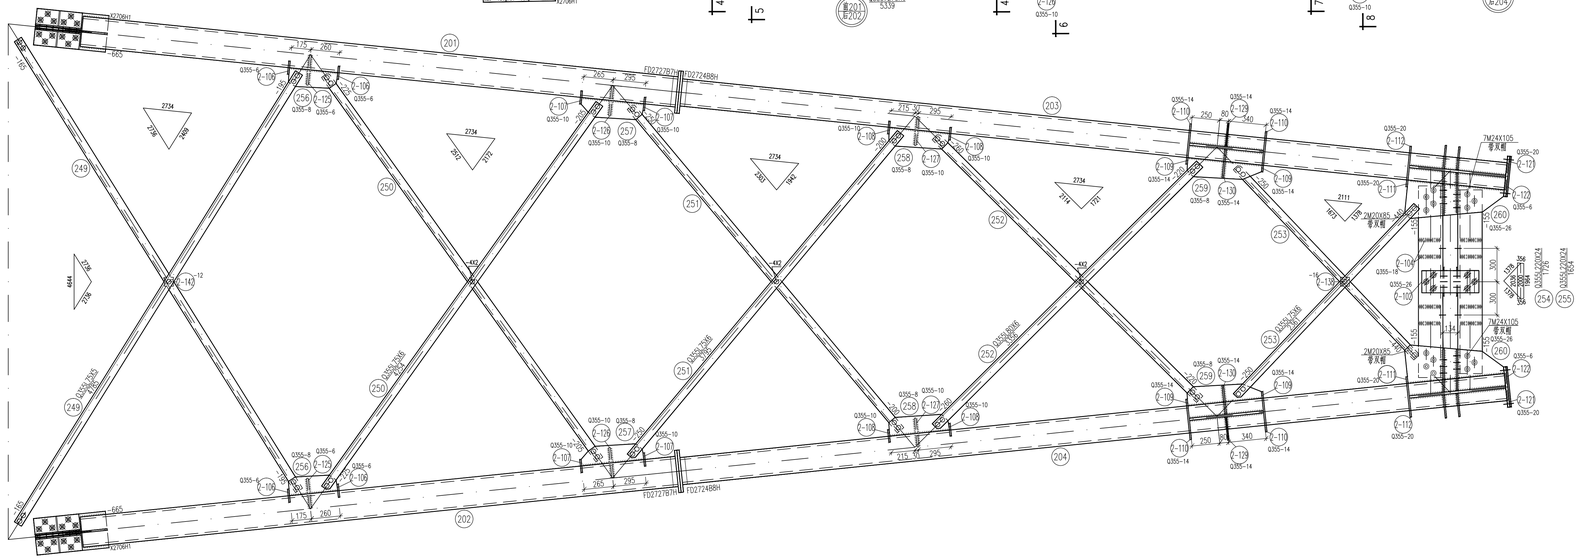

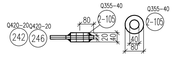

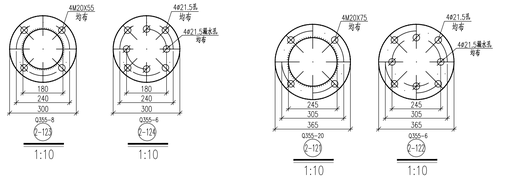

山东电力工程咨询院有限公司					浙江特高压交流环网工程线路	工程	施工图	设计阶段	
批准	审批		校核		SZK31102A直线塔				
审核	审核		设计/勘测		上导线横担结构图(1/2)				②
电气		2026.08	日期	2026年 08月	图号	37-SA36901S-T0121-005		版本	
专业	会签		比例						