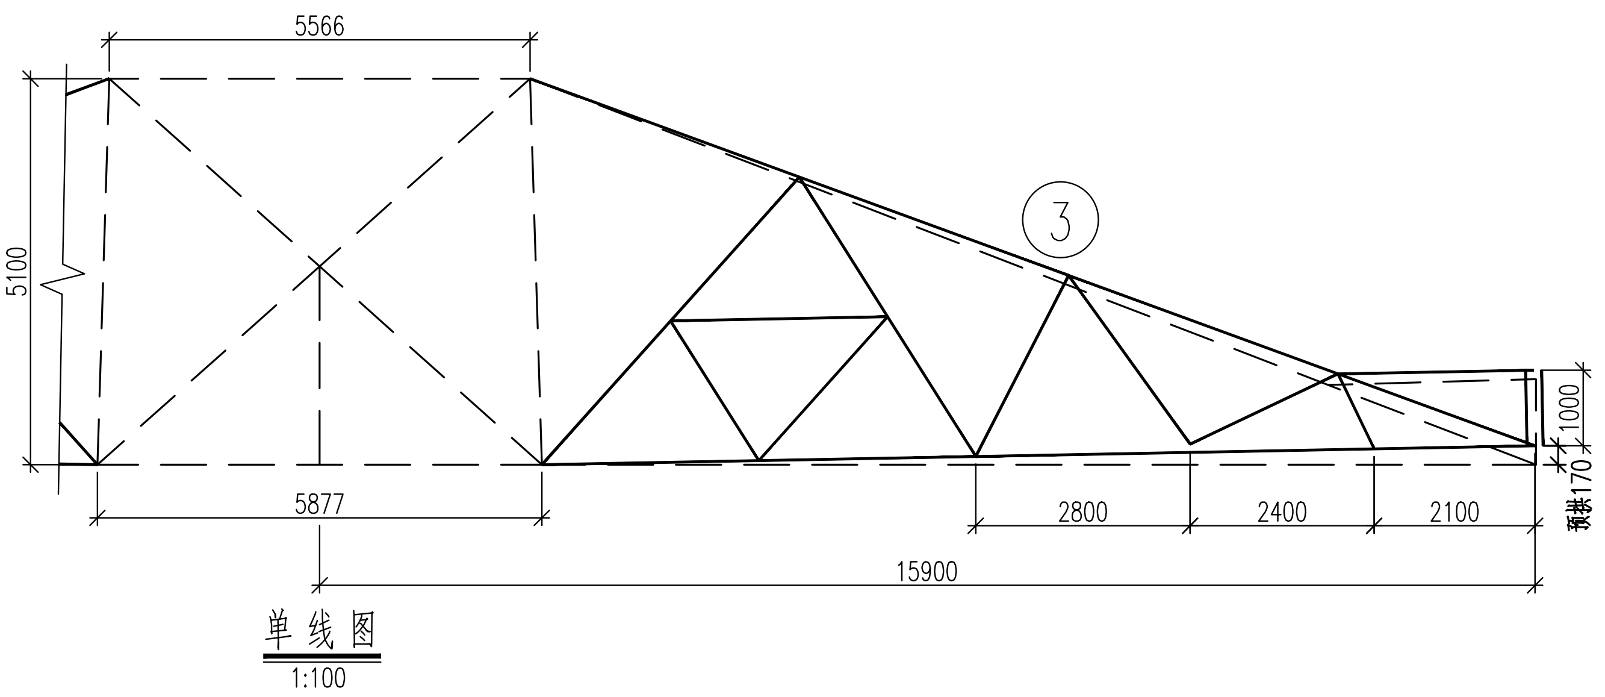
5566
5100
7
3
5877
2800
2400
2100
15900
1000
170

单线图
1:100

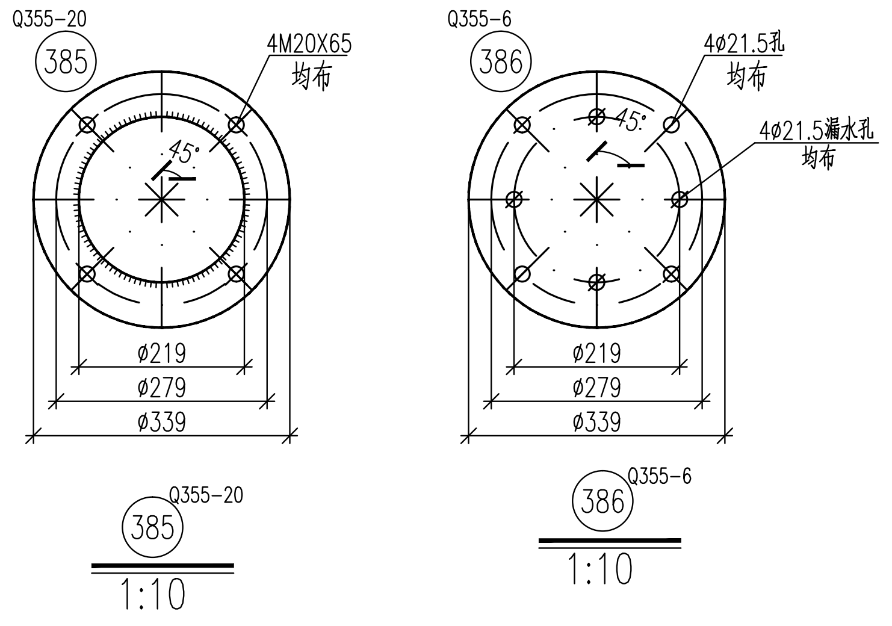
Q355-20
385
4M20X65
均布
45°
ø219
ø279
ø339
Q355-6
386
4ø21.5孔
均布
4ø21.5漏水孔
均布

385 Q355-20
1:10

386 Q355-6
1:10

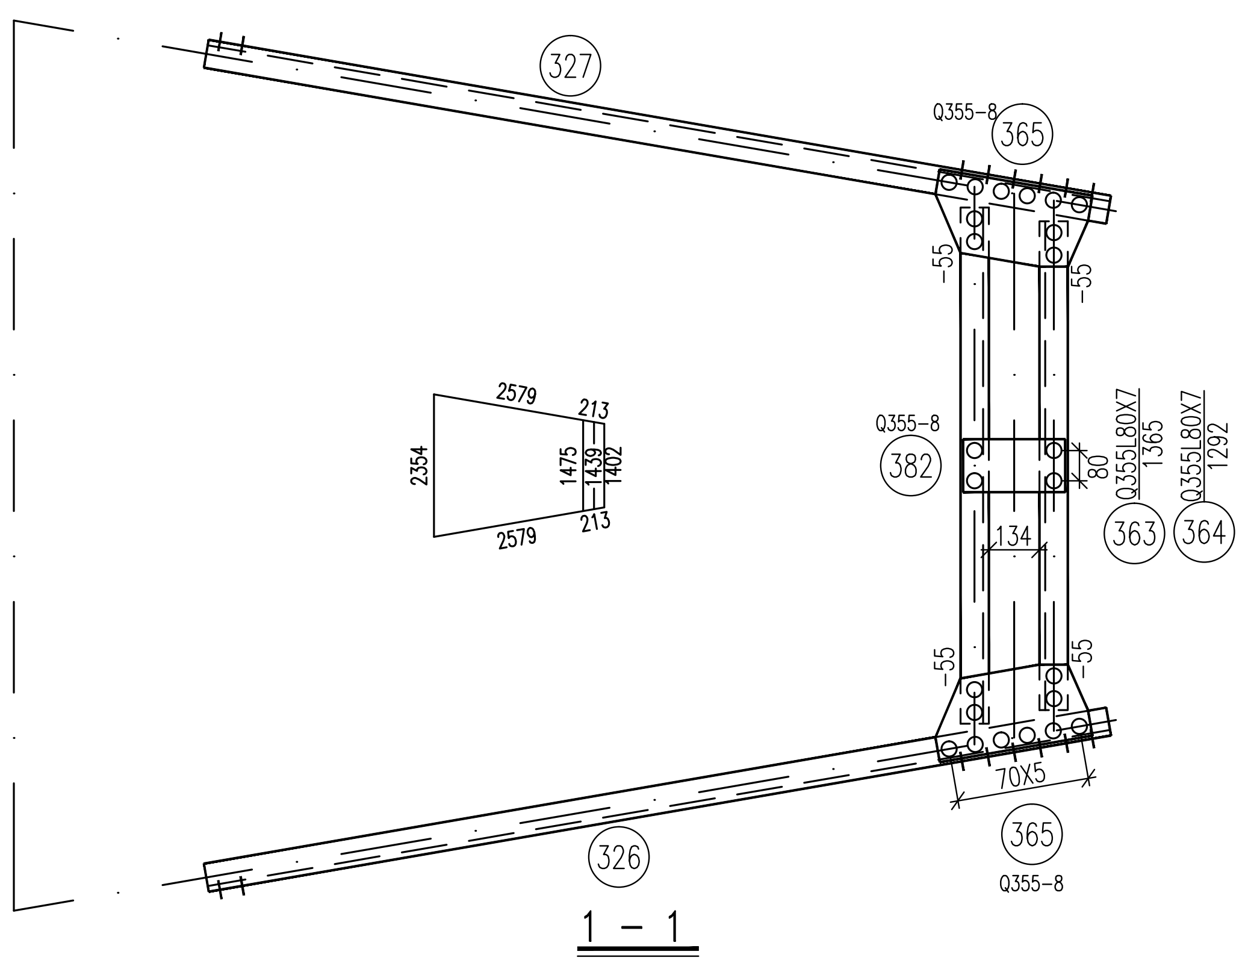
327
Q355-8
365
382
363
364
Q355L80X7
1365
Q355L80X7
1292
134
70X5
365
Q355-8
326
-55
2579
2354
213
475
402

1 - 1

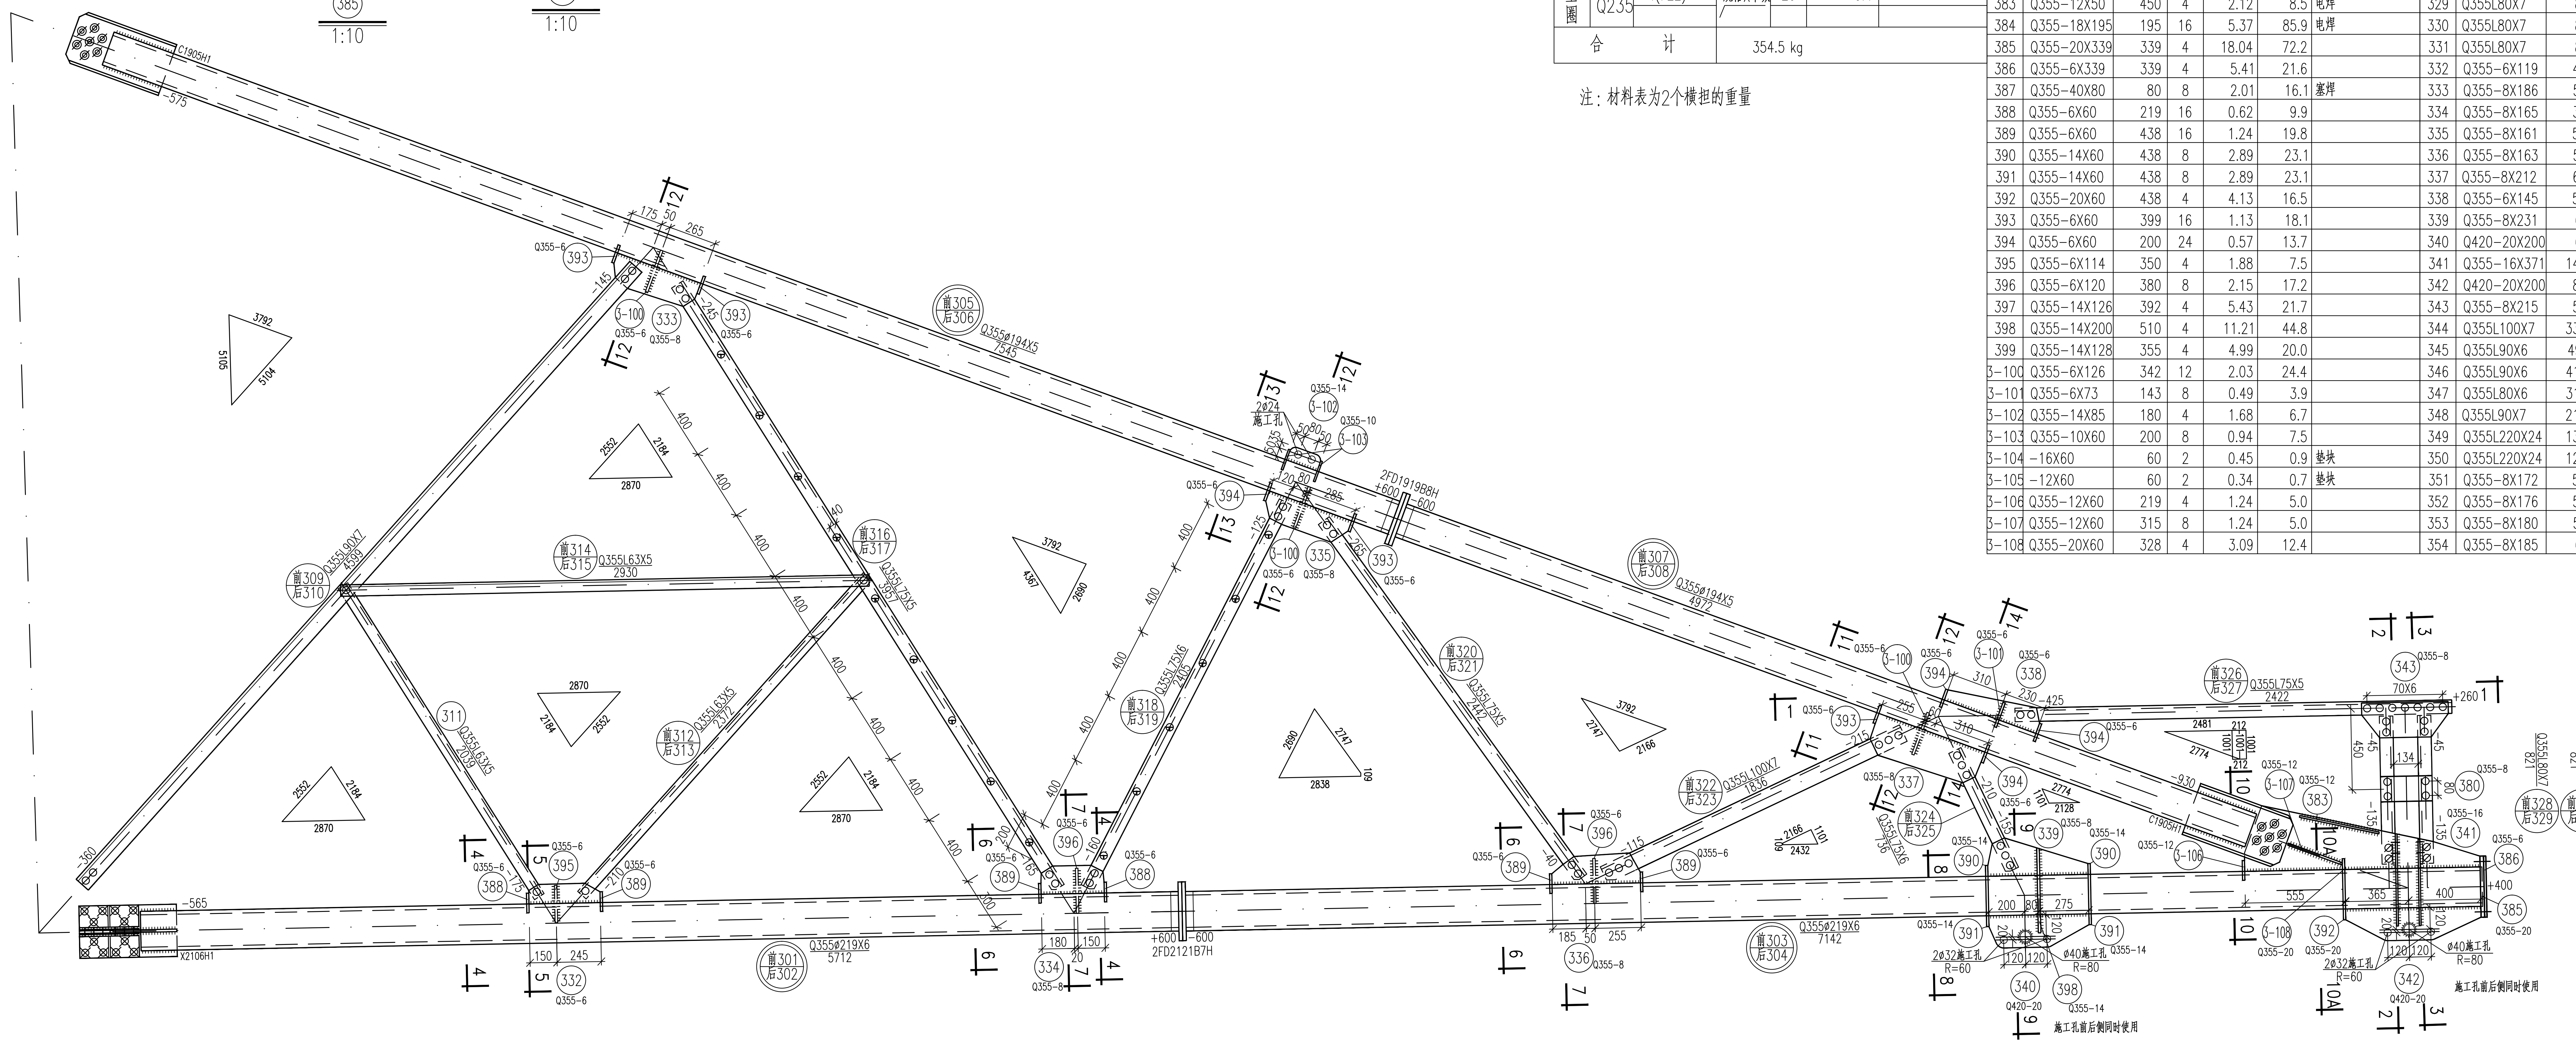
C1905H1
-575
前305 后306
Q355ø194X5
7545
前307 后308
Q355ø194X5
4972
前309 后310
Q355L90X7
4599
前314 后315
Q355L63X5
2930
前316 后317
前312 后313
前318 后319
311
前320 后321
前322 后323
Q355L100X7
前324 后325
前326 后327
Q355L75X5
2422
前328 后329
前330 后331
前301 后302
Q355ø219X6
5712
前303 后304
Q355ø219X6
7142
2FD1919B8H
+600
2FD2121B7H
X2106H1
-565
施工孔前后侧同时使用
ø40施工孔
2ø32施工孔
R=60
R=80

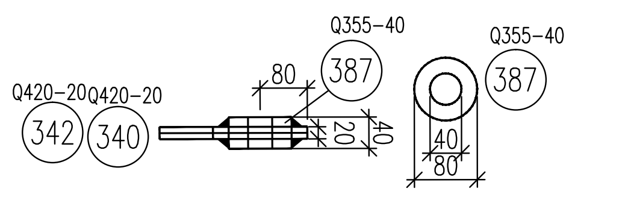
Q420-20
342
Q420-20
340
80
Q355-40
387
20
40
Q355-40
387
40
80

构　件　明　细　表

编号	规　格	长度 (mm)	数量	重量(kg) 一件	重量(kg) 小计	备　注
3-109	Q355-20X60	110	4	1.04	4.2	
	FD1919B8H		8	8.7	69.6	
	FD2121B7H		8	9.2	73.6	
	C1905H1		8	27.1	216.8	
	X2106H1		4	44.5	178.0	
合　计		7929.5 kg				

螺栓、脚钉、垫圈明细表

名称	级别	规　格	符号	数量	重量(kg)	备　注
螺栓	6.8级	M20X55	○	416	136.2	
		M20X65	∅	32	11.3	
		M20X75	⊗	44	16.6	
		M20X85	∅	2	0.8	
		M20X75S	○	24	9.6	带双帽
		M20X85S	○	52	22.1	带双帽
	8.8级	M24X75	◎	28	16.6	
		M24X95	◎	36	24.0	
		M24X105S	○	52	38.5	带双帽
		M20X90	○	56	26.4	法兰螺栓
		M20X95	○	56	27.1	法兰螺栓
脚钉	6.8级	M16X185	⊖	60	24.9	
垫圈	Q235	-4(ø22)	规格X个数	20	0.4	
合　计			354.5 kg			

注：材料表为2个横担的重量

构　件　明　细　表

编号	规　格	长度 (mm)	数量	重量(kg) 一件	重量(kg) 小计	备　注
355	Q355-26X338	825	4	56.91	227.6	
356	Q355L90X6	5937	4	49.57	198.3	
357	Q355L90X6	5097	4	42.56	170.2	切角
358	Q355L75X6	4293	4	29.65	118.6	切角
359	Q355L80X6	2157	2	15.91	31.8	
360	Q355-8X180	539	4	6.09	24.4	
361	Q355-8X180	633	4	7.16	28.6	
362	Q355-8X179	479	4	5.38	21.5	
363	Q355L80X7	1365	2	11.64	23.3	
364	Q355L80X7	1292	2	11.01	22.0	
365	Q355-8X229	451	4	6.49	26.0	
366	Q355L80X7	868	2	7.40	14.8	切角
367	Q355L80X7	868	2	7.40	14.8	切角
368	Q355-10X282	322	4	7.13	28.5	
369	Q355-20X315	365	4	18.05	72.2	
370	Q355-10X384	580	2	17.48	35.0	
371	Q355L80X7	854	2	7.28	14.6	切角
372	Q355L80X7	854	2	7.28	14.6	切角
373	Q355-10X280	326	4	7.17	28.7	
374	Q355-20X315	405	4	20.03	80.1	
375	Q355-10X399	591	2	18.51	37.0	
376	Q355-20X226	526	4	18.66	74.6	
377	Q355-20X216	425	4	14.41	57.6	
378	Q355-20X226	526	4	18.66	74.6	
379	Q355-20X216	425	4	14.41	57.6	
380	Q355-8X140	286	4	2.51	10.0	
381	Q355-26X200	514	2	20.98	42.0	
382	Q355-8X140	270	2	2.37	4.7	
383	Q355-12X50	450	4	2.12	8.5	电焊
384	Q355-18X195	195	16	5.37	85.9	电焊
385	Q355-20X339	339	4	18.04	72.2	
386	Q355-6X339	339	4	5.41	21.6	
387	Q355-40X80	80	8	2.01	16.1	塞焊
388	Q355-6X60	219	16	0.62	9.9	
389	Q355-6X60	438	16	1.24	19.8	
390	Q355-14X60	438	8	2.89	23.1	
391	Q355-14X60	438	8	2.89	23.1	
392	Q355-20X60	438	4	4.13	16.5	
393	Q355-6X60	399	16	1.13	18.1	
394	Q355-6X60	200	24	0.57	13.7	
395	Q355-6X114	350	4	1.88	7.5	
396	Q355-6X120	380	8	2.15	17.2	
397	Q355-14X126	392	4	5.43	21.7	
398	Q355-14X200	510	4	11.21	44.8	
399	Q355-14X128	355	4	4.99	20.0	
3-100	Q355-6X126	342	12	2.03	24.4	
3-101	Q355-6X73	143	8	0.49	3.9	
3-102	Q355-14X85	180	4	1.68	6.7	
3-103	Q355-10X60	200	8	0.94	7.5	
3-104	-16X60	60	2	0.45	0.9	垫块
3-105	-12X60	60	2	0.34	0.7	垫块
3-106	Q355-12X60	219	4	1.24	5.0	
3-107	Q355-12X60	315	8	1.24	5.0	
3-108	Q355-20X60	328	4	3.09	12.4	

构　件　明　细　表

编号	规　格	长度 (mm)	数量	重量(kg) 一件	重量(kg) 小计	备　注
301	Q355ø219X6	5712	2	180.03	360.1	
302	Q355ø219X6	5712	2	180.03	360.1	
303	Q355ø219X6	7142	2	225.09	450.2	
304	Q355ø219X6	7142	2	225.09	450.2	
305	Q355ø194X5	7545	2	175.84	351.7	
306	Q355ø194X5	7545	2	175.84	351.7	
307	Q355ø194X5	4972	2	115.87	231.7	
308	Q355ø194X5	4972	2	115.87	231.7	
309	Q355L90X7	4599	2	44.41	88.8	
310	Q355L90X7	4599	2	44.41	88.8	
311	Q355L63X5	2039	4	9.83	39.3	
312	Q355L63X5	2372	2	11.44	22.9	切角
313	Q355L63X5	2372	2	11.44	22.9	切角
314	Q355L63X5	2930	2	14.13	28.3	切角
315	Q355L63X5	2930	2	14.13	28.3	切角
316	Q355L75X5	3957	2	23.02	46.0	带脚钉
317	Q355L75X5	3957	2	23.02	46.0	带脚钉
318	Q355L75X6	2405	2	16.61	33.2	带脚钉
319	Q355L75X6	2405	2	16.61	33.2	带脚钉
320	Q355L75X5	2442	2	14.21	28.4	切角
321	Q355L75X5	2442	2	14.21	28.4	切角
322	Q355L100X7	1836	2	19.89	39.8	切角
323	Q355L100X7	1836	2	19.89	39.8	切角
324	Q355L75X6	736	2	5.08	10.2	切角
325	Q355L75X6	736	2	5.08	10.2	切角
326	Q355L75X5	2422	2	14.09	28.2	局部开角
327	Q355L75X5	2422	2	14.09	28.2	局部开角
328	Q355L80X7	821	2	7.00	14.0	局部开角
329	Q355L80X7	821	2	7.00	14.0	局部开角
330	Q355L80X7	821	2	7.00	14.0	局部合角
331	Q355L80X7	821	2	7.00	14.0	局部合角
332	Q355-6X119	435	4	2.44	9.8	
333	Q355-8X186	539	4	6.30	25.2	
334	Q355-8X165	385	4	3.99	16.0	
335	Q355-8X161	534	4	5.40	21.6	
336	Q355-8X163	539	4	5.52	22.1	
337	Q355-8X212	688	4	9.16	36.6	
338	Q355-6X145	594	4	4.06	16.2	
339	Q355-8X231	611	4	8.86	35.4	
340	Q420-20X200	611	4	19.19	76.8	
341	Q355-16X371	1436	4	66.91	267.6	电焊
342	Q420-20X200	825	4	25.90	103.6	
343	Q355-8X215	528	4	7.13	28.5	
344	Q355L100X7	3396	4	36.80	147.2	切角
345	Q355L90X6	4941	4	41.26	165.0	切角
346	Q355L90X6	4129	4	34.48	137.9	切角
347	Q355L80X6	3189	4	23.53	94.1	切角
348	Q355L90X7	2178	4	21.03	84.1	切角
349	Q355L220X24	1348	2	106.36	212.7	电焊
350	Q355L220X24	1232	2	97.21	194.4	电焊
351	Q355-8X172	534	4	5.77	23.1	
352	Q355-8X176	506	4	5.59	22.4	
353	Q355-8X180	539	4	6.09	24.4	
354	Q355-8X185	611	4	7.10	28.4	

山东电力工程咨询院有限公司

浙江特高压交流环网工程线路	工程	施工图	设计阶段		
批　准	雷强	校　核	马一丹	SZK31102A直线塔 中导线横担结构图(1/3) ③	
审　核	高锡鹏	设计/勘测	潘胜光		
比　例		日　期	2026年 08月	图　号	37-SA36901S-T0121-007
版本					

电　气	赵庆周	2026.08
专　业	会　签	日　期