




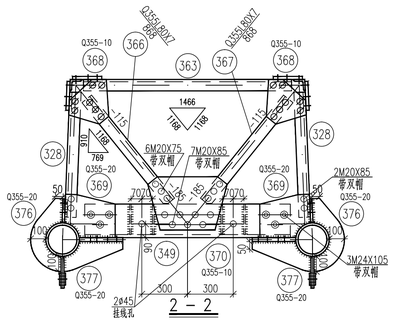


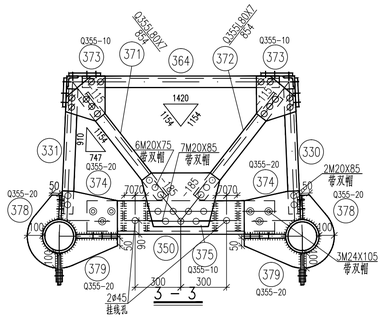


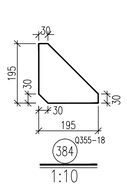

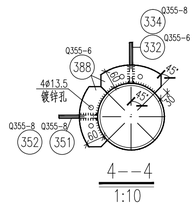

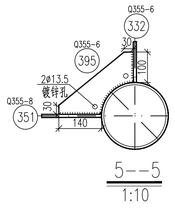

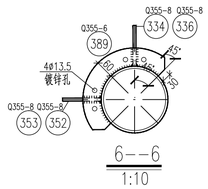

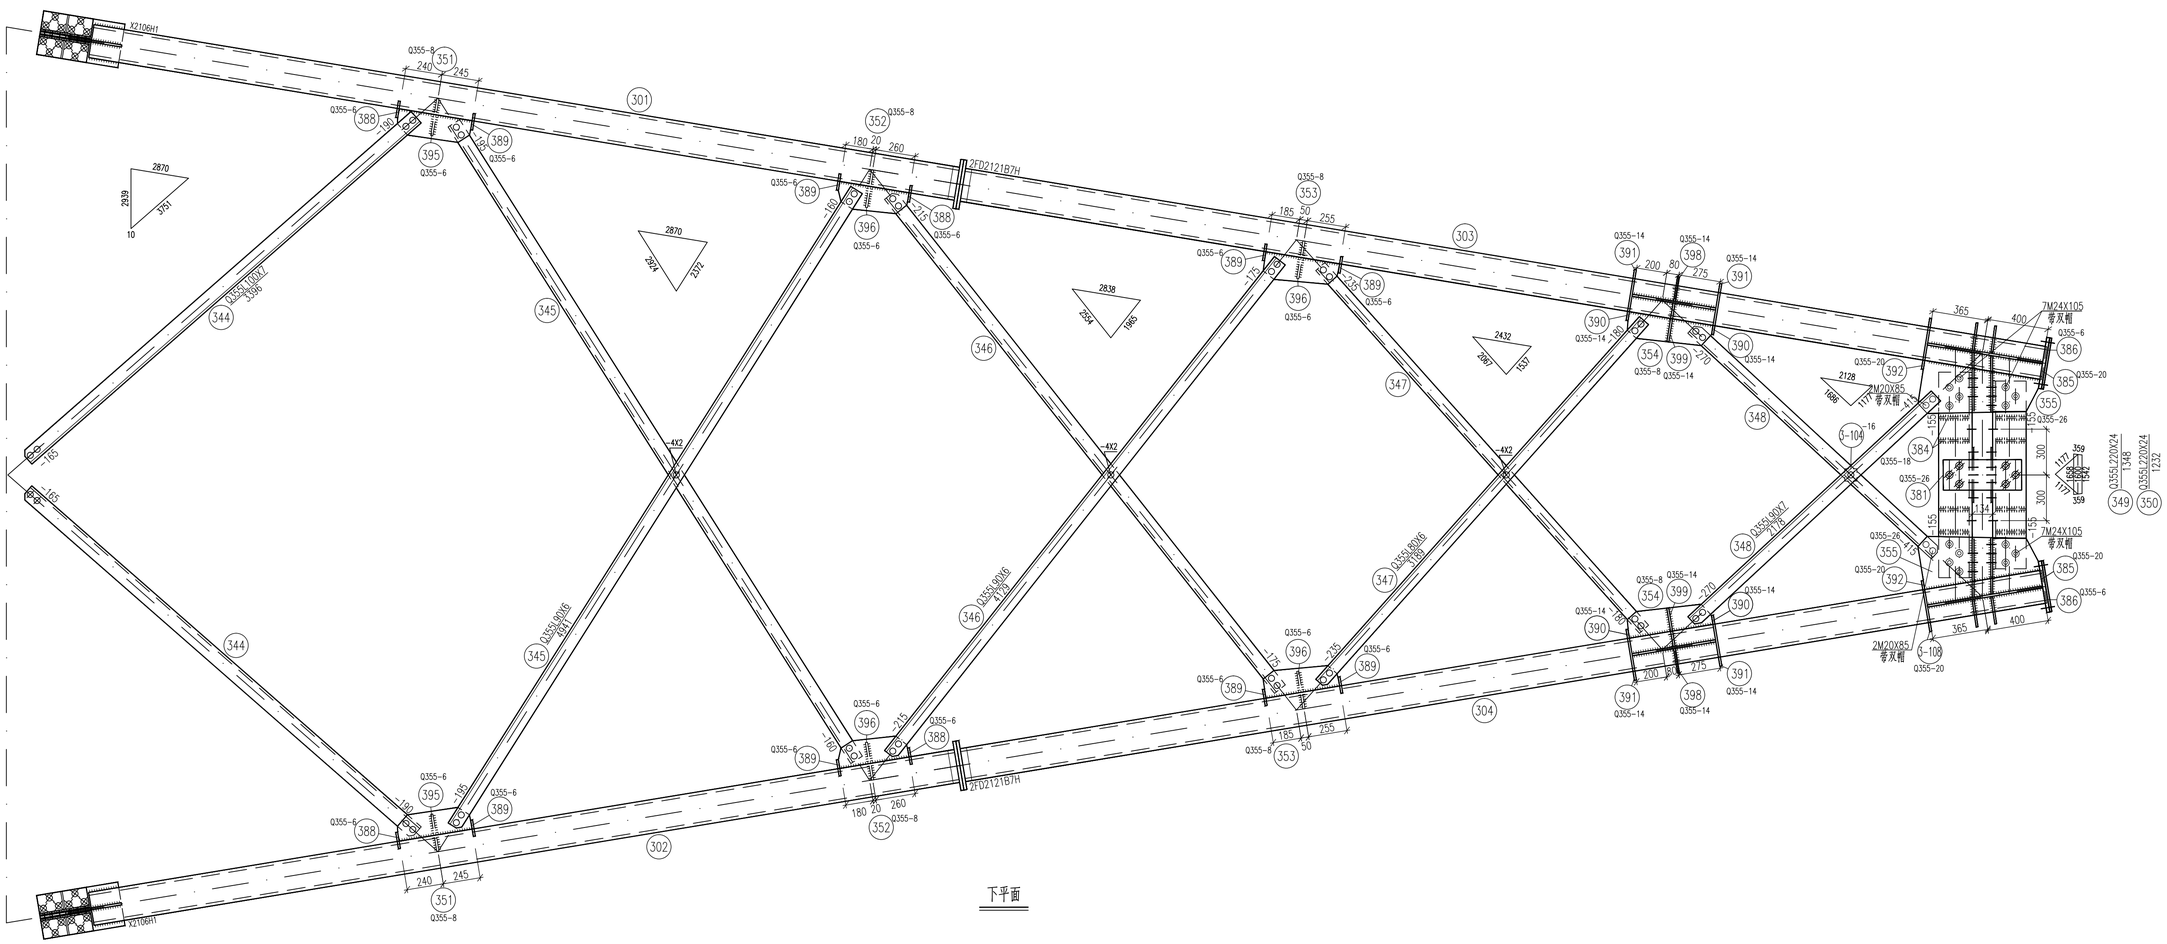

				山东电力工程咨询院有限公司		浙江特高压交流环网工程线路 工程	施工图 设计阶段
				批 准		校 核	
				审 核		设计/勘测	
电气	赵文用	2026.08		比 例		日 期	2026年 08月
专业	会签	日期					

SZK31102A直线塔
中导线横担结构图(2/3) ③

图 号 37-SA36901S-T0121-008 版本