




7--7
1:10

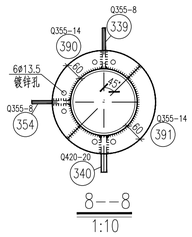


8--8
1:10

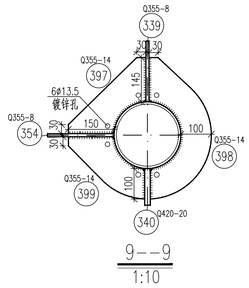


9--9
1:10

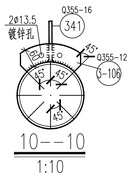


10--10
1:10

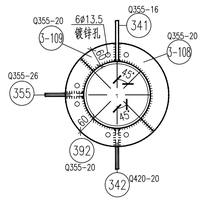


10A--10A
1:10

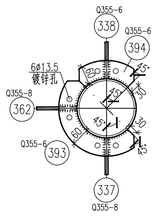


11--11
1:10

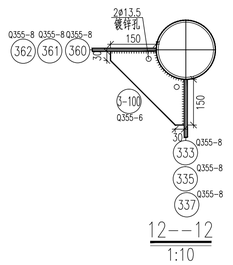


12--12
1:10

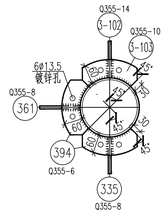


13--13
1:10

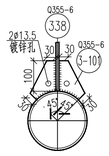

14--14
1:10

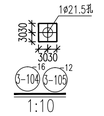

1:10

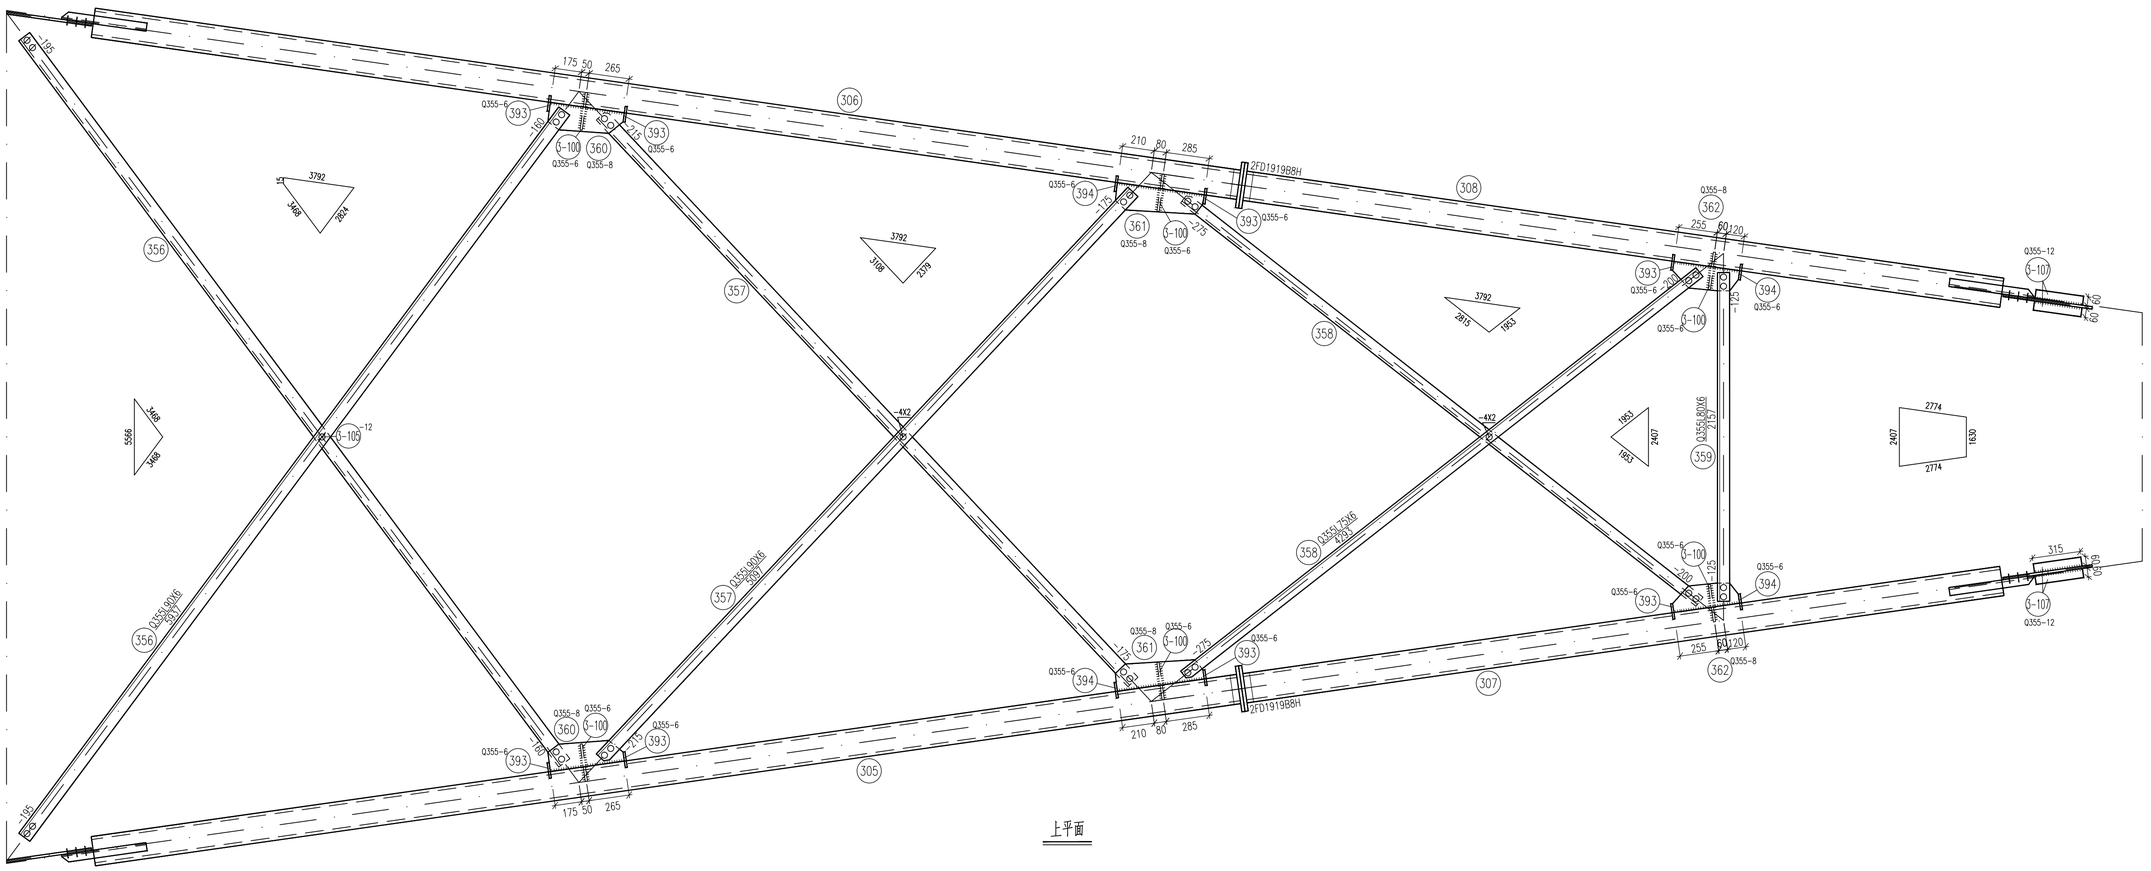

上平面

				山东电力工程咨询院有限公司		浙江特高压交流环网工程线路 工程	施工图 设计阶段
				批 准		SZK31102A直线塔 中导线横担结构图(3/3) ③	
				审 核	高鹏鹏	校 核	
电气	赵庆用	2026.08				设计/勘测	
专业	会签	日期		比 例		日 期 2026年 08月	图 号 37-SA36901S-T0121-009 版本