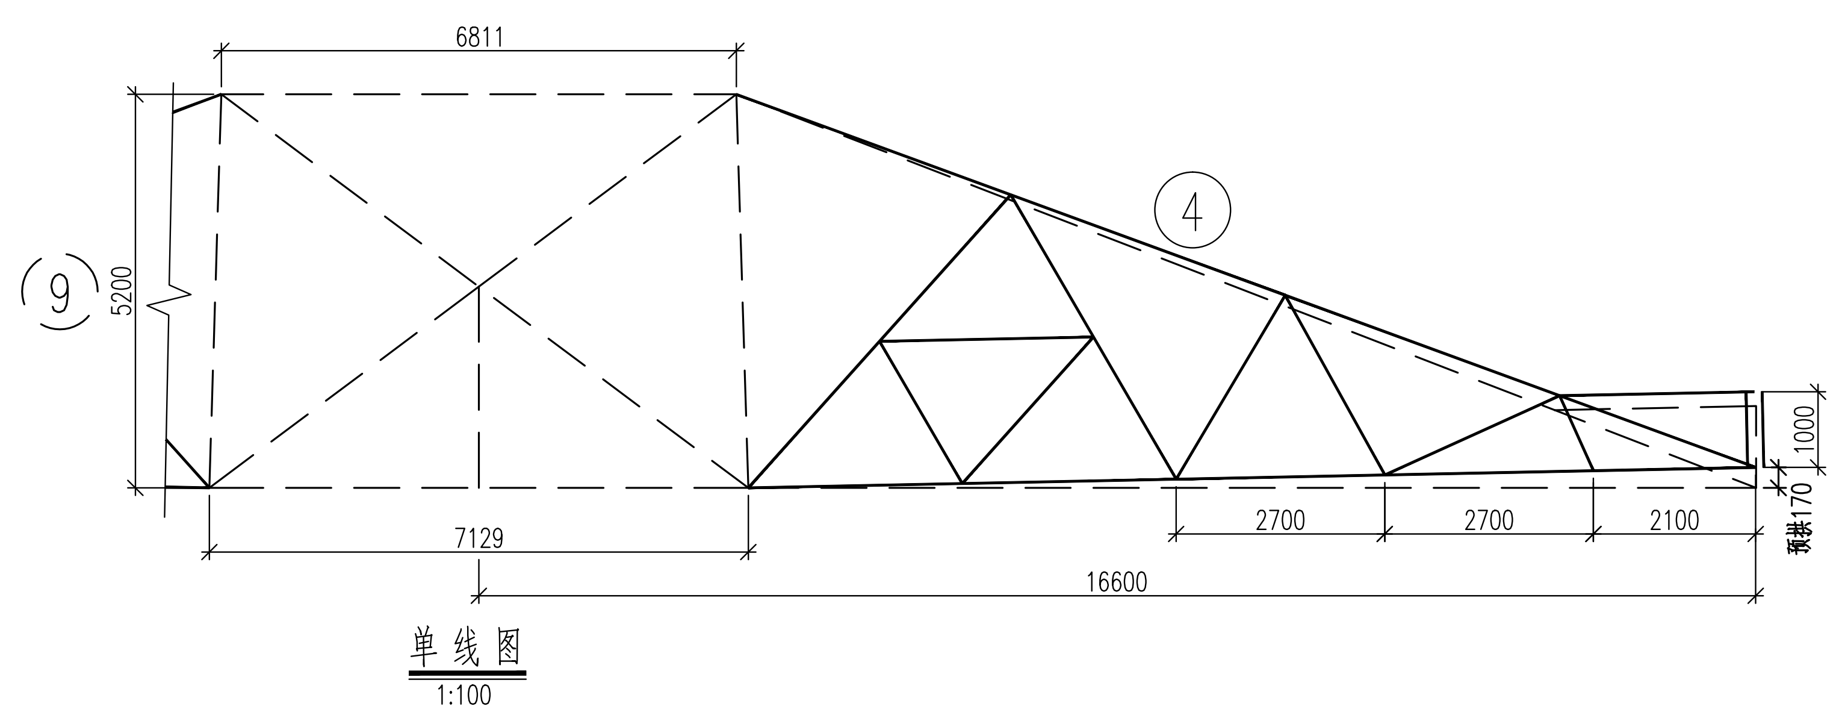

单线图
1:100

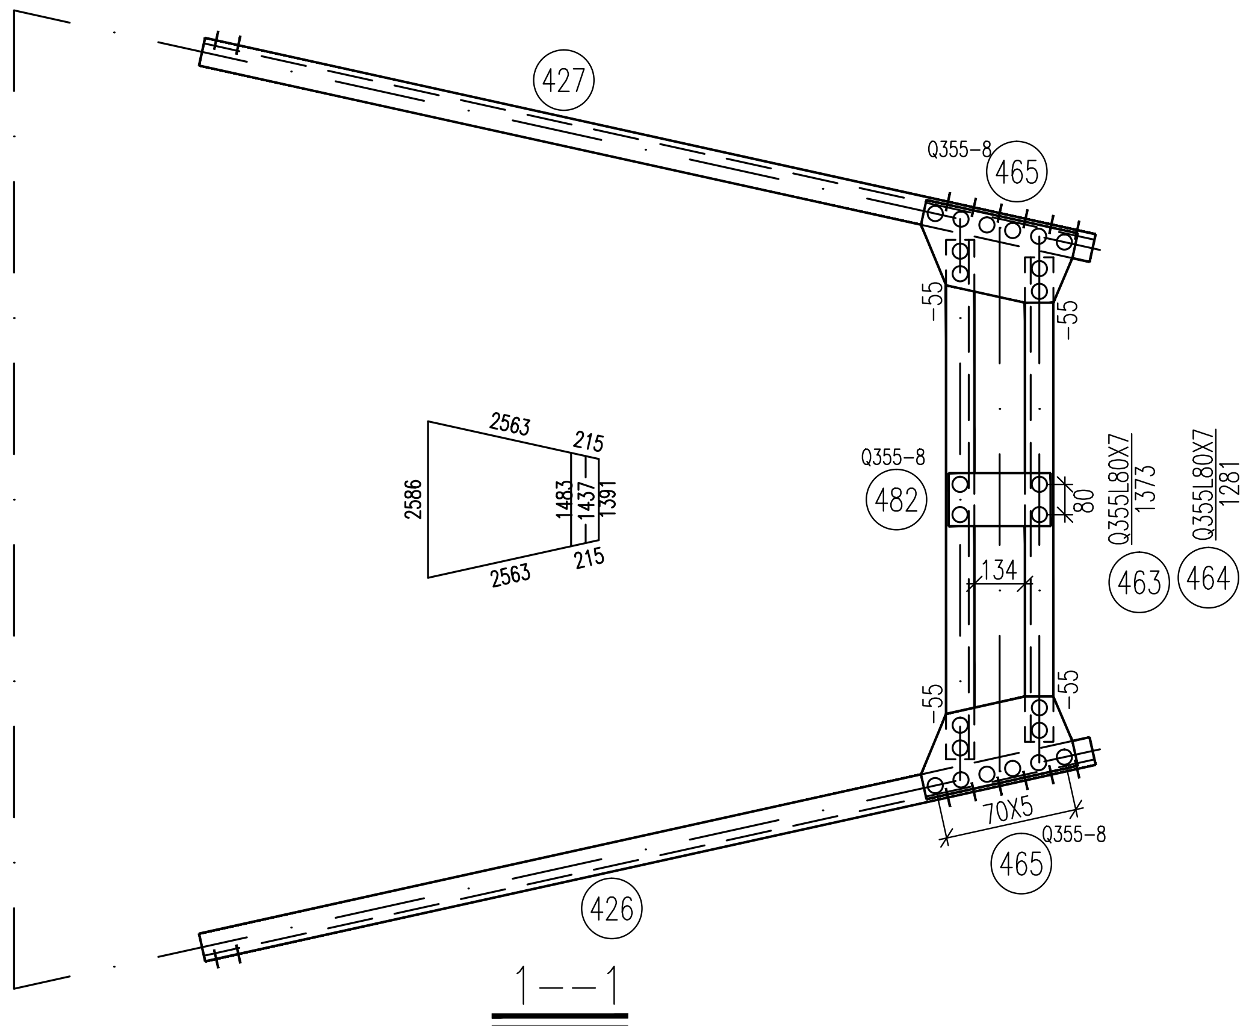

1--1

螺栓、脚钉、垫圈明细表

名称	级别	规格	符号	数量	重量(kg)	备注
螺栓	6.8级	M20X55	○	416	136.2	
		M20X65	∅	32	11.3	
		M20X75	⊗	44	16.6	
		M20X85	⊘	2	0.8	
		M20X75S	○	24	9.6	带双帽
		M20X85S	○	52	22.1	带双帽
	8.8级	M24X75	◎	28	16.6	
		M24X95	◎	36	24.0	
		M24X105S	○	52	38.5	带双帽
		M20X90	○	56	26.4	法兰螺栓
		M20X95	○	56	27.1	法兰螺栓
脚钉	6.8级	M16X185	⊖ ⊥	60	24.9	
垫圈	Q235	-4(ø22)	规格X个数	20	0.4	
合计			354.5 kg			

注：材料表为2个横担的重量

构件明细表

编号	规格	长度(mm)	数量	重量(kg) 一件	重量(kg) 小计	备注
458	Q355L90X6	4601	4	38.42	153.7	切角
459	Q355L90X6	2372	2	19.81	39.6	
460	Q355-8X194	495	4	6.03	24.1	
461	Q355-8X198	611	4	7.60	30.4	
462	Q355-8X190	380	4	4.53	18.1	
463	Q355L80X7	1373	2	11.70	23.4	
464	Q355L80X7	1281	2	10.92	21.8	
465	Q355-8X229	451	4	6.49	26.0	
466	Q355L80X7	870	2	7.42	14.8	切角
467	Q355L80X7	870	2	7.42	14.8	切角
468	Q355-10X293	322	4	7.41	29.6	
469	Q355-20X315	365	4	18.05	72.2	
470	Q355-10X369	553	2	16.02	32.0	
471	Q355L80X7	857	2	7.31	14.6	切角
472	Q355L80X7	857	2	7.31	14.6	切角
473	Q355-10X282	326	4	7.22	28.9	
474	Q355-20X305	416	4	19.92	79.7	
475	Q355-10X399	590	2	18.48	37.0	
476	Q355-20X200	526	4	16.52	66.1	
477	Q355-20X196	424	4	13.05	52.2	
478	Q355-20X200	526	4	16.52	66.1	
479	Q355-20X196	424	4	13.05	52.2	
480	Q355-8X140	316	4	2.78	11.1	
481	Q355-26X200	565	2	23.06	46.1	
482	Q355-8X140	297	2	2.61	5.2	
483	Q355-12X60	495	4	2.80	11.2	电焊
484	Q355-18X195	215	16	5.92	94.7	电焊
485	Q355-20X339	373	4	19.85	79.4	
486	Q355-6X339	373	4	5.96	23.8	
487	Q355-40X80	80	8	2.01	16.1	塞焊
488	Q355-6X60	438	24	1.24	29.8	
489	Q355-14X60	438	8	2.89	23.1	
490	Q355-14X60	438	8	2.89	23.1	
491	Q355-20X60	438	4	4.13	16.5	
492	Q355-6X60	399	8	1.13	9.0	
493	Q355-6X60	200	40	0.57	22.8	
494	Q355-6X116	327	4	1.79	7.2	
495	Q355-6X124	346	8	2.02	16.2	
496	Q355-14X127	393	4	5.49	22.0	
497	Q355-14X203	510	4	11.38	45.5	
498	Q355-14X128	355	4	4.99	20.0	
499	Q355-6X126	342	12	2.03	24.4	
4-100	Q355-6X73	143	8	0.49	3.9	
4-101	Q355-14X85	180	4	1.68	6.7	
4-102	Q355-10X60	200	8	0.94	7.5	
4-103	-16X60	60	2	0.45	0.9	垫块
4-104	-12X60	60	2	0.34	0.7	垫块
4-105	Q355-12X60	219	4	1.24	5.0	
4-106	Q355-12X60	315	8	1.24	5.0	
4-107	Q355-20X60	328	4	3.09	12.4	
4-108	Q355-20X60	110	4	1.04	4.2	
	FD1919B8H		8	8.7	69.6	
	FD2121B7H		8	9.2	73.6	
	C1905H1		8	27.1	216.8	
	X2106H1		4	44.5	178.0	
合计		8268.0 kg				

构件明细表

编号	规格	长度(mm)	数量	重量(kg) 一件	重量(kg) 小计	备注
401	Q355ø219X6	5568	2	175.49	351.0	
402	Q355ø219X6	5568	2	175.49	351.0	
403	Q355ø219X6	7415	2	233.70	467.4	
404	Q355ø219X6	7415	2	233.70	467.4	
405	Q355ø194X5	7597	2	177.05	354.1	
406	Q355ø194X5	7597	2	177.05	354.1	
407	Q355ø194X5	5032	2	117.27	234.5	
408	Q355ø194X5	5032	2	117.27	234.5	
409	Q355L90X6	4597	2	38.38	76.8	
410	Q355L90X6	4597	2	38.38	76.8	
411	Q355L63X5	2035	4	9.81	39.2	
412	Q355L63X5	2421	2	11.67	23.3	切角
413	Q355L63X5	2421	2	11.67	23.3	切角
414	Q355L63X5	2890	2	13.94	27.9	切角
415	Q355L63X5	2890	2	13.94	27.9	切角
416	Q355L75X5	3959	2	23.03	46.1	切角 带脚钉
417	Q355L75X5	3959	2	23.03	46.1	切角 带脚钉
418	Q355L80X6	2538	2	18.72	37.4	切角 带脚钉
419	Q355L80X6	2538	2	18.72	37.4	切角 带脚钉
420	Q355L75X5	2345	2	13.64	27.3	
421	Q355L75X5	2345	2	13.64	27.3	
422	Q355L110X7	2079	2	24.80	49.6	切角
423	Q355L110X7	2079	2	24.80	49.6	切角
424	Q355L75X6	737	2	5.09	10.2	切角
425	Q355L75X6	737	2	5.09	10.2	切角
426	Q355L75X5	2412	2	14.03	28.1	局部开角
427	Q355L75X5	2412	2	14.03	28.1	局部开角
428	Q355L80X7	821	2	7.00	14.0	局部开角
429	Q355L80X7	821	2	7.00	14.0	局部开角
430	Q355L80X7	821	2	7.00	14.0	局部合角
431	Q355L80X7	821	2	7.00	14.0	局部合角
432	Q355-6X128	479	4	2.89	11.6	
433	Q355-8X186	495	4	5.78	23.1	
434	Q355-8X170	473	4	5.05	20.2	
435	Q355-8X176	424	4	4.69	18.8	
436	Q355-8X183	534	4	6.14	24.6	
437	Q355-8X224	671	4	9.44	37.8	
438	Q355-6X184	589	4	5.10	20.4	
439	Q355-8X224	627	4	8.82	35.3	
440	Q420-20X180	627	4	17.72	70.9	电焊
441	Q355-16X362	1436	4	65.29	261.2	电焊
442	Q420-20X180	825	4	23.31	93.2	
443	Q355-8X195	528	4	6.47	25.9	
444	Q355L110X7	3694	4	44.07	176.3	切角
445	Q355L90X6	5704	4	47.63	190.5	切角
446	Q355L90X6	4635	4	38.70	154.8	切角
447	Q355L80X6	3663	4	27.02	108.1	切角
448	Q355L90X7	2221	4	21.45	85.8	切角
449	Q355L220X24	1355	2	106.91	213.8	电焊
450	Q355L220X24	1205	2	95.08	190.2	电焊
451	Q355-8X201	479	4	6.05	24.2	
452	Q355-8X173	473	4	5.14	20.6	
453	Q355-8X168	534	4	5.63	22.5	
454	Q355-8X187	627	4	7.36	29.4	
455	Q355-26X344	825	4	57.92	231.7	
456	Q355L110X7	6788	4	80.98	323.9	
457	Q355L100X7	5703	4	61.80	247.2	切角

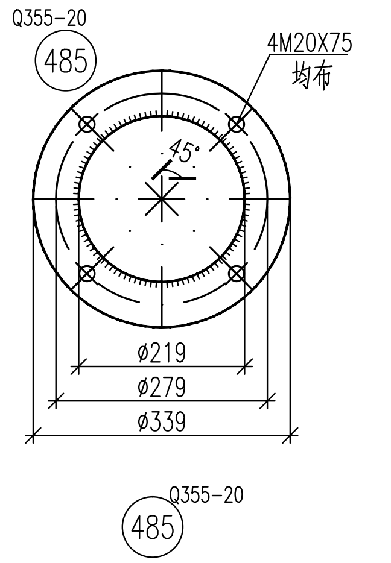

485 Q355-20
1:10

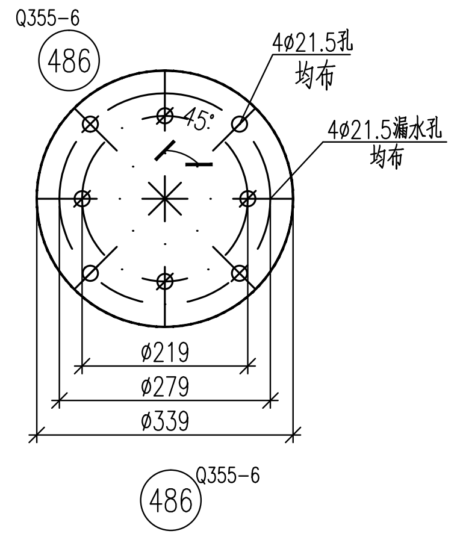

486 Q355-6
1:10

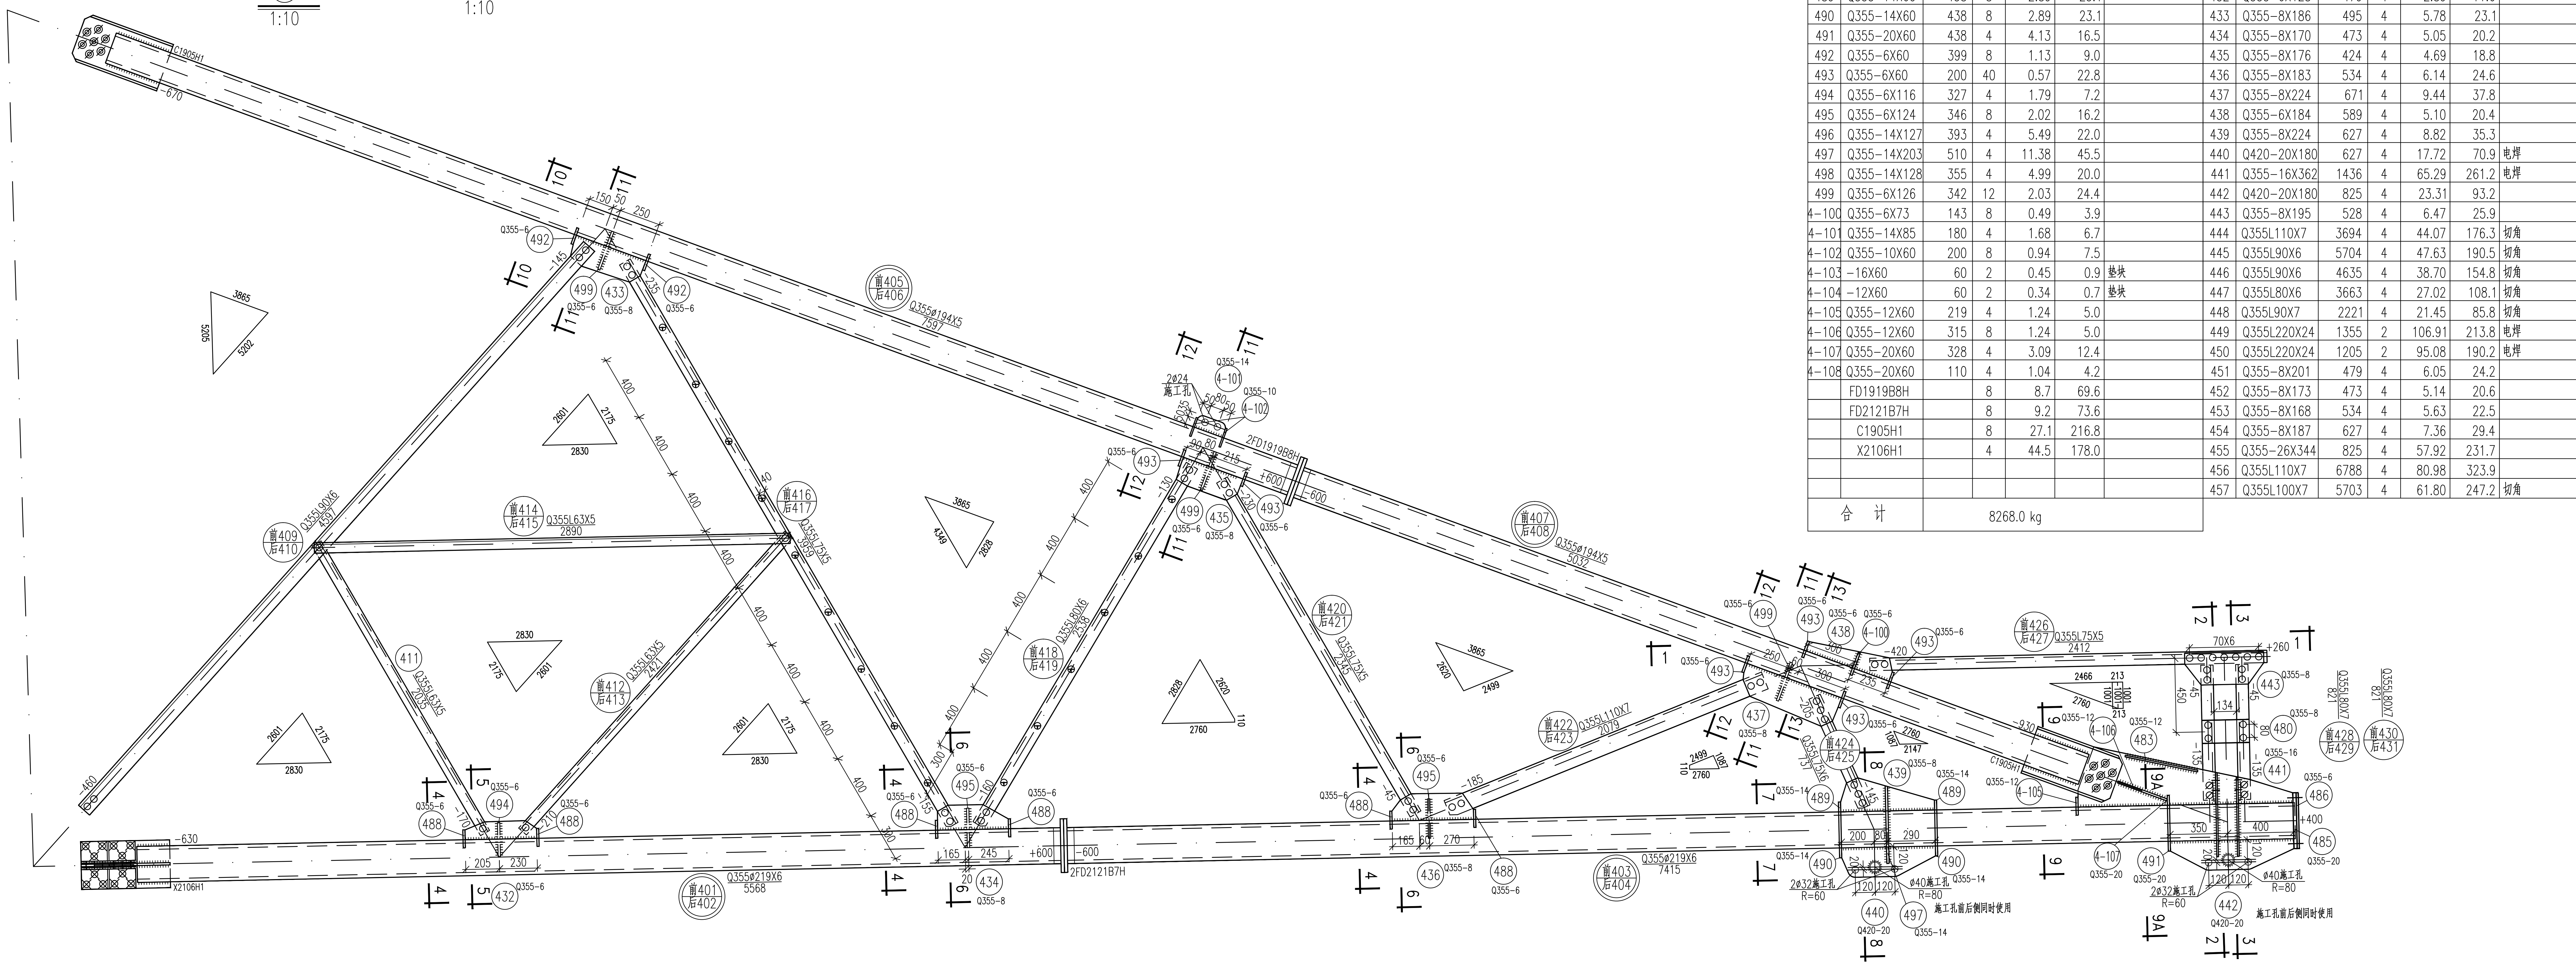
C1905H1
X2106H1
2FD1919B8H
2FD2121B7H
前405 后406 Q355ø194X5 7597
前407 后408 Q355ø194X5 5032
前401 后402 Q355ø219X6 5568
前403 后404 Q355ø219X6 7415
前409 后410 Q355L90X6 4597
前414 后415 Q355L63X5 2890
前412 后413 Q355L63X5 2421
411 Q355L63X5 2035
前416 后417 Q355L75X5
前418 后419 Q355L80X6 2538
前420 后421 Q355L75X5
前422 后423 Q355L110X7 2079
前424 后425
前426 后427 Q355L75X5 2412
前428 后429 Q355L80X7 821
前430 后431 Q355L80X7 821
70X6
+600
-600
+260
+400
ø40施工孔 R=80
2ø32施工孔 R=60
施工孔前后侧同时使用
2ø24 施工孔
1 2 4 5 6 8 9A 10 11 12 13

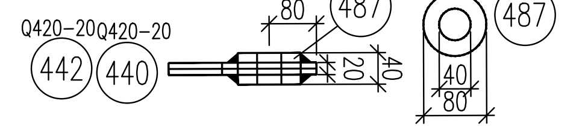

			山东电力工程咨询院有限公司			浙江特高压交流环网工程线路 工程	施工图 设计阶段
			批准	雷强	校核	马一丹	SZK31102A直线塔 下导线横担结构图(1/3) ④
			审核	高锡鹏			
电气	赵庆周	2026.08			设计/勘测	潘旭光	
专业	会签	日期	比例		日期	2026年 08月	图号 37-SA36901S-T0121-010 版本