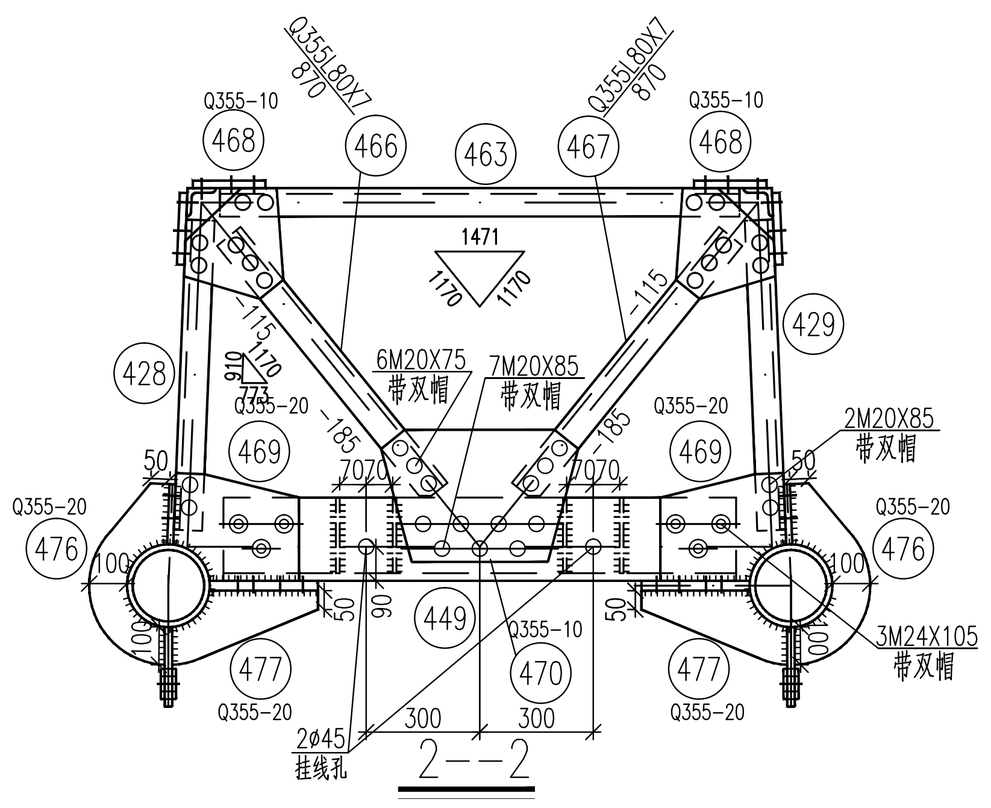

2--2

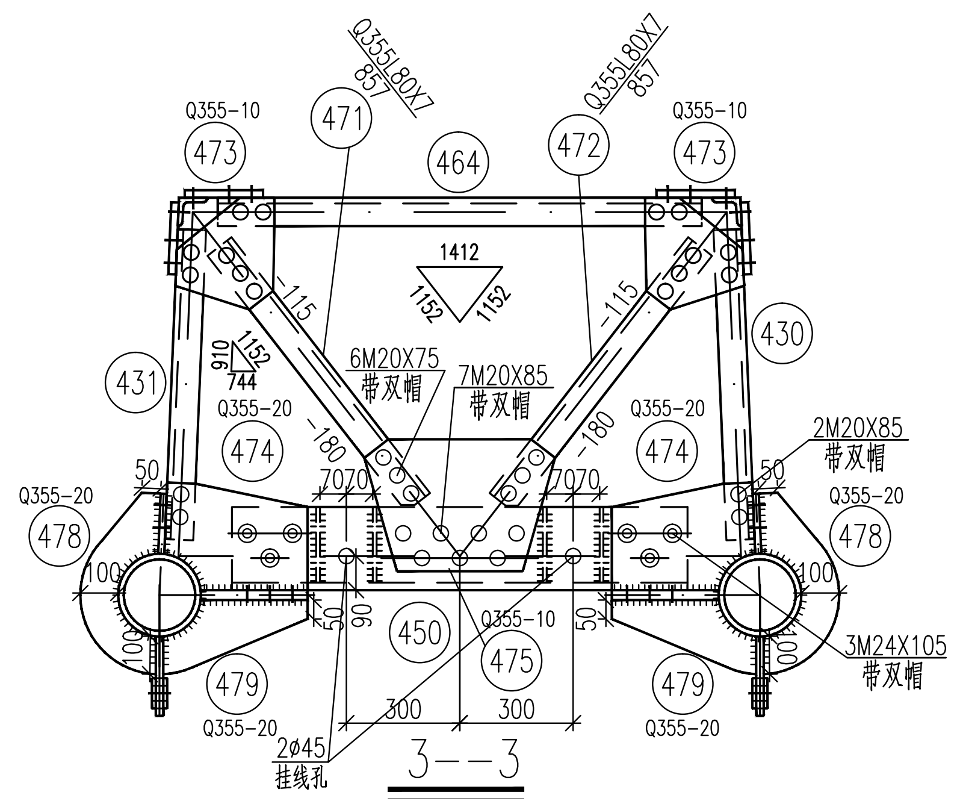

3--3

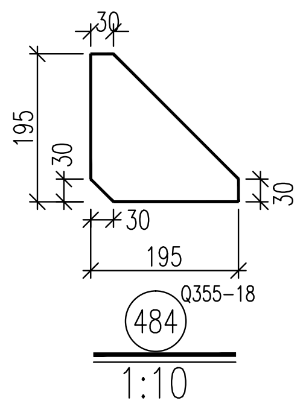

1:10

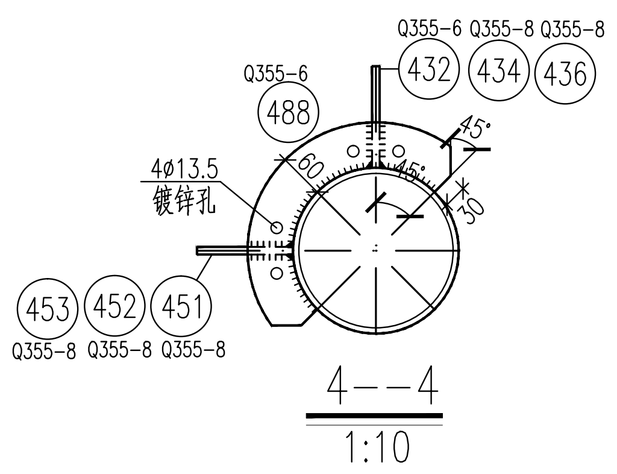

4--4

1:10

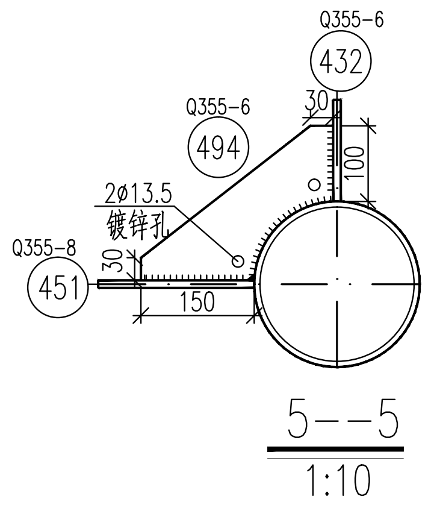

5--5

1:10

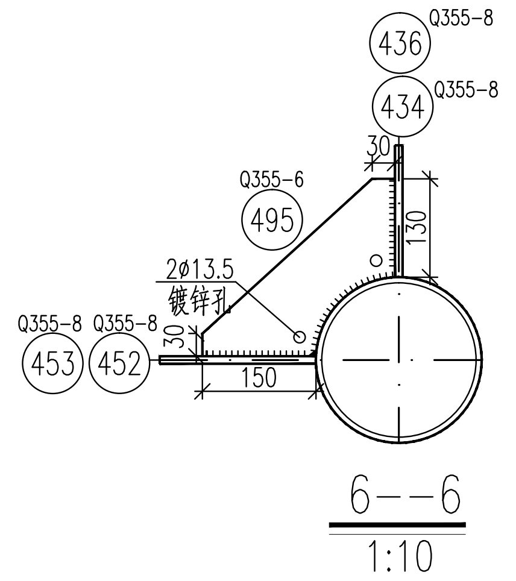

6--6

1:10

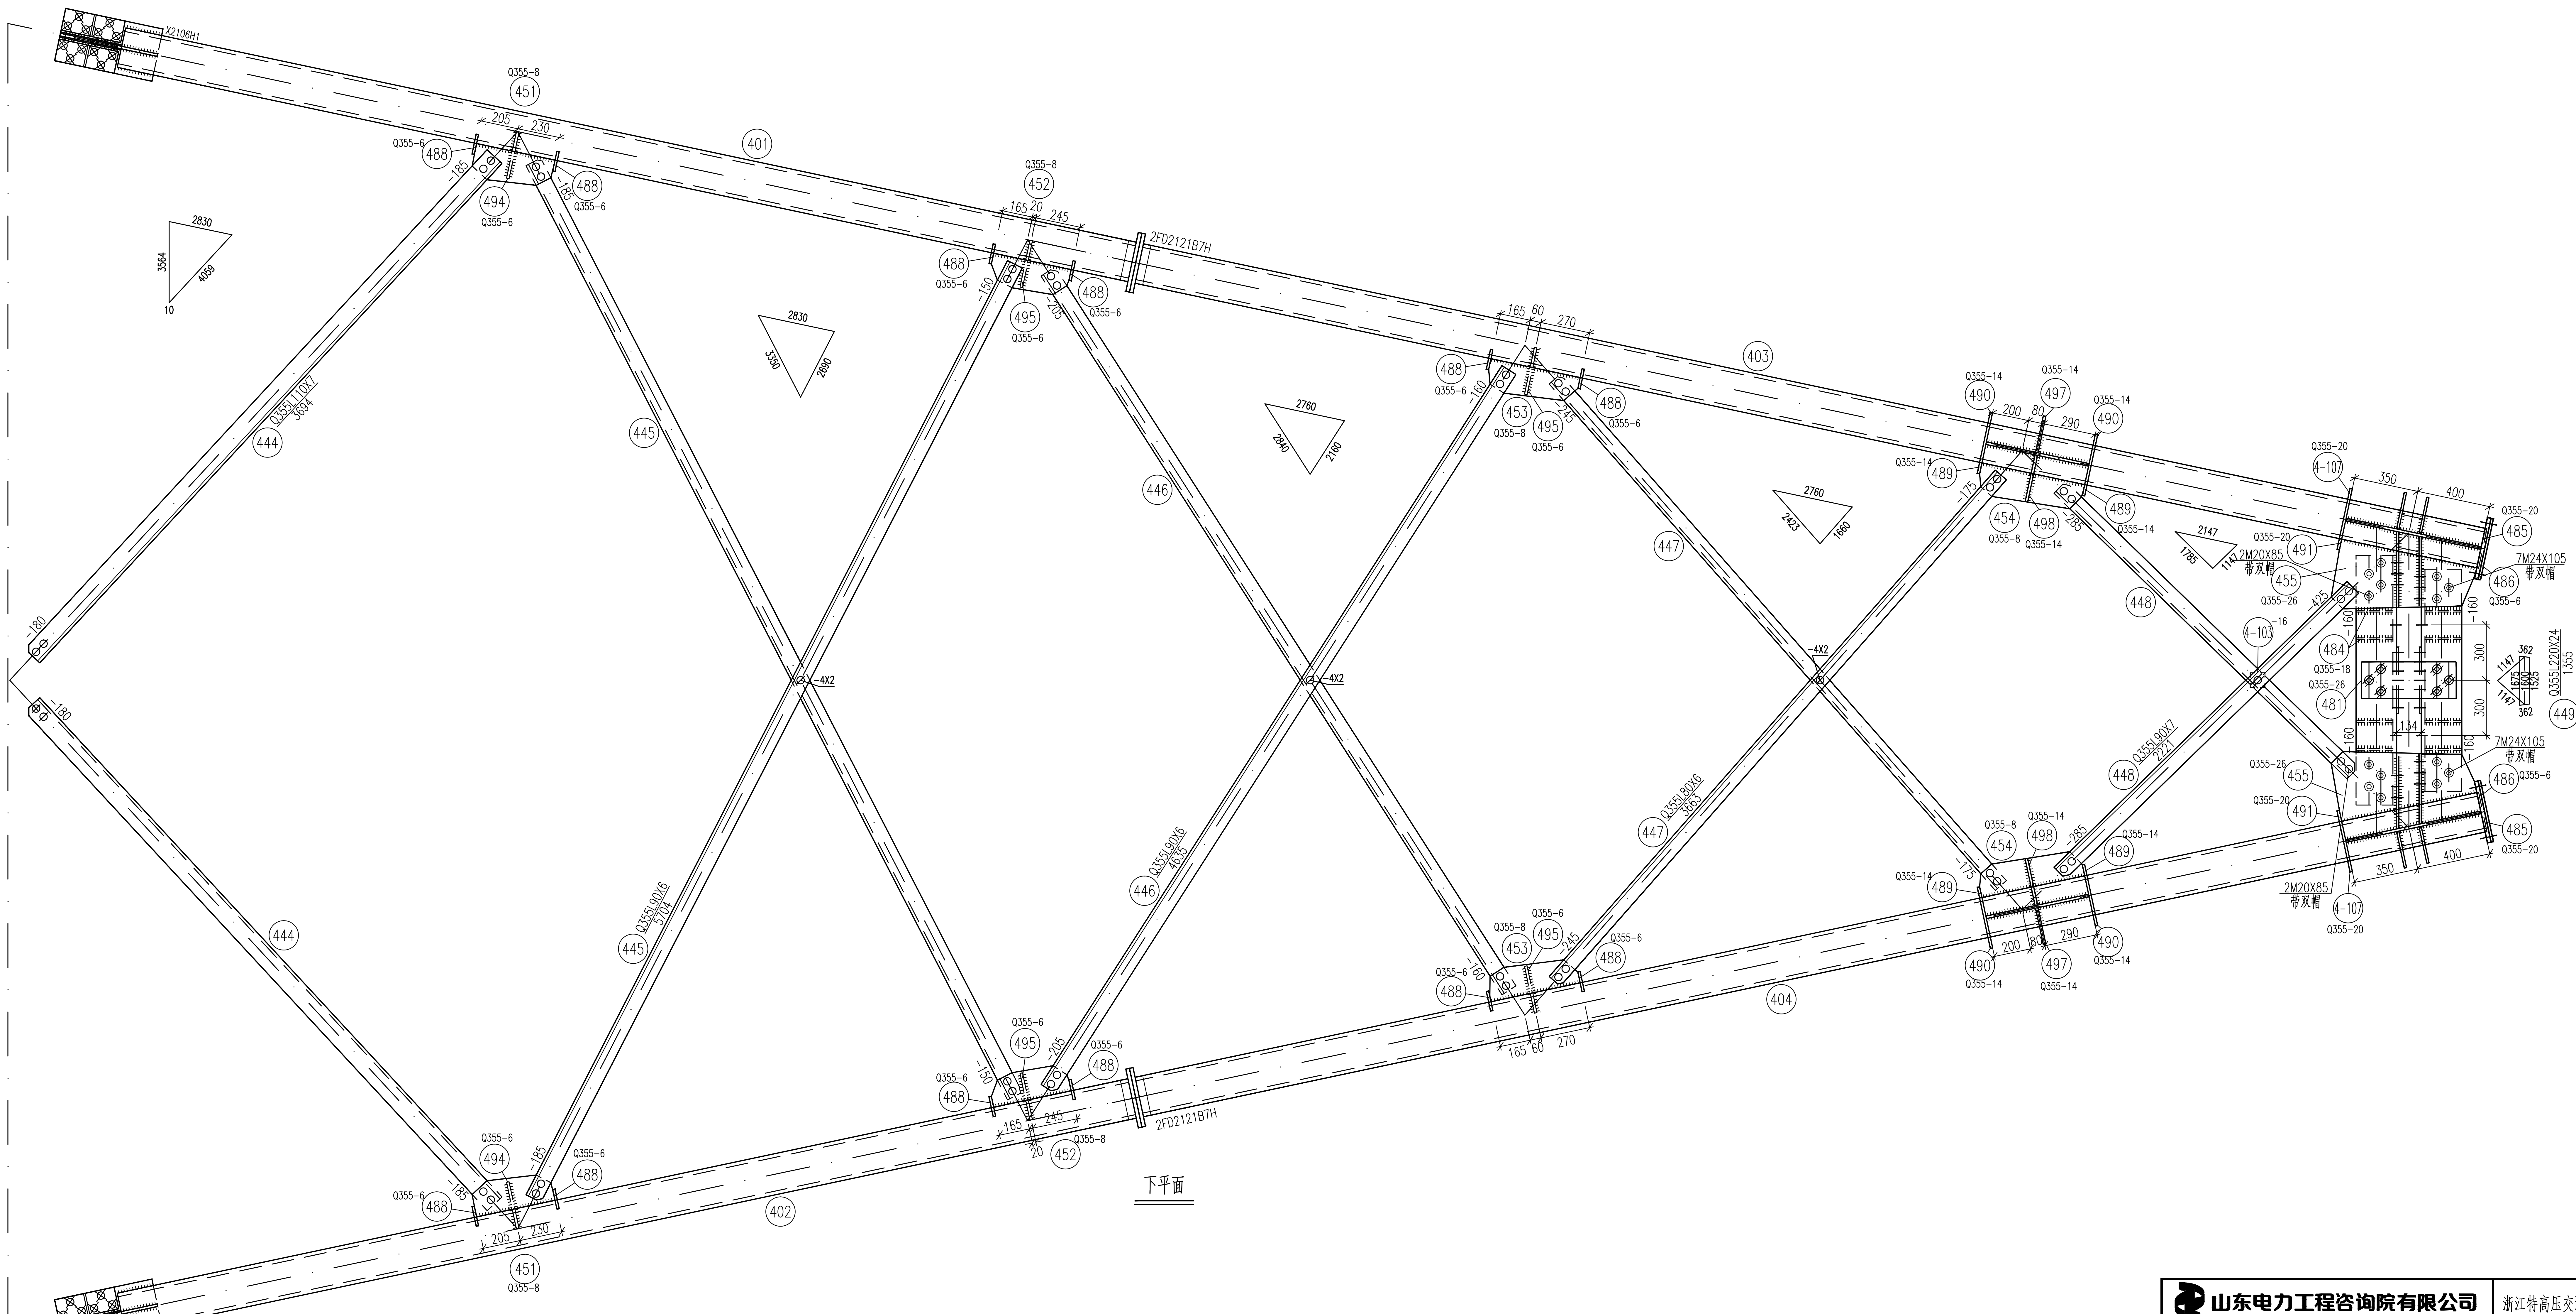

下平面

			山东电力工程咨询院有限公司				浙江特高压交流环网工程线路 工程	施工图 设计阶段
			批 准	雷强	校 核	马一丹	SZK31102A直线塔 下导线横担结构图(2/3) ④	
			审 核	高锡鹏				
电 气	赵庆周	2026.08			设计/勘测	潘胜光		
专 业	会 签	日 期	比 例		日 期	2026年 08月	图 号 37-SA36901S-T0121-011	版本