



7--7

1:10

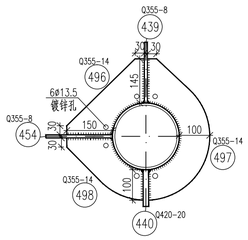


8--8

1:10

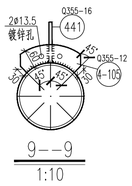


9--9

1:10

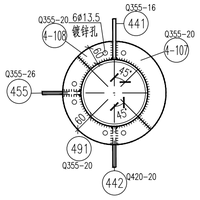


9A--9A

1:10

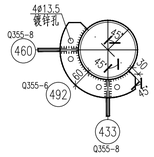


10--10

1:10

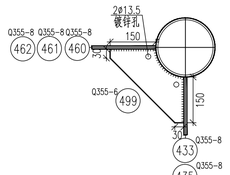


11--11

1:10

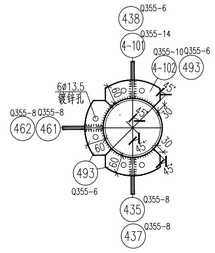


12--12

1:10

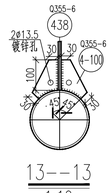


13--13

1:10

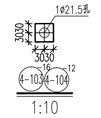

1:10

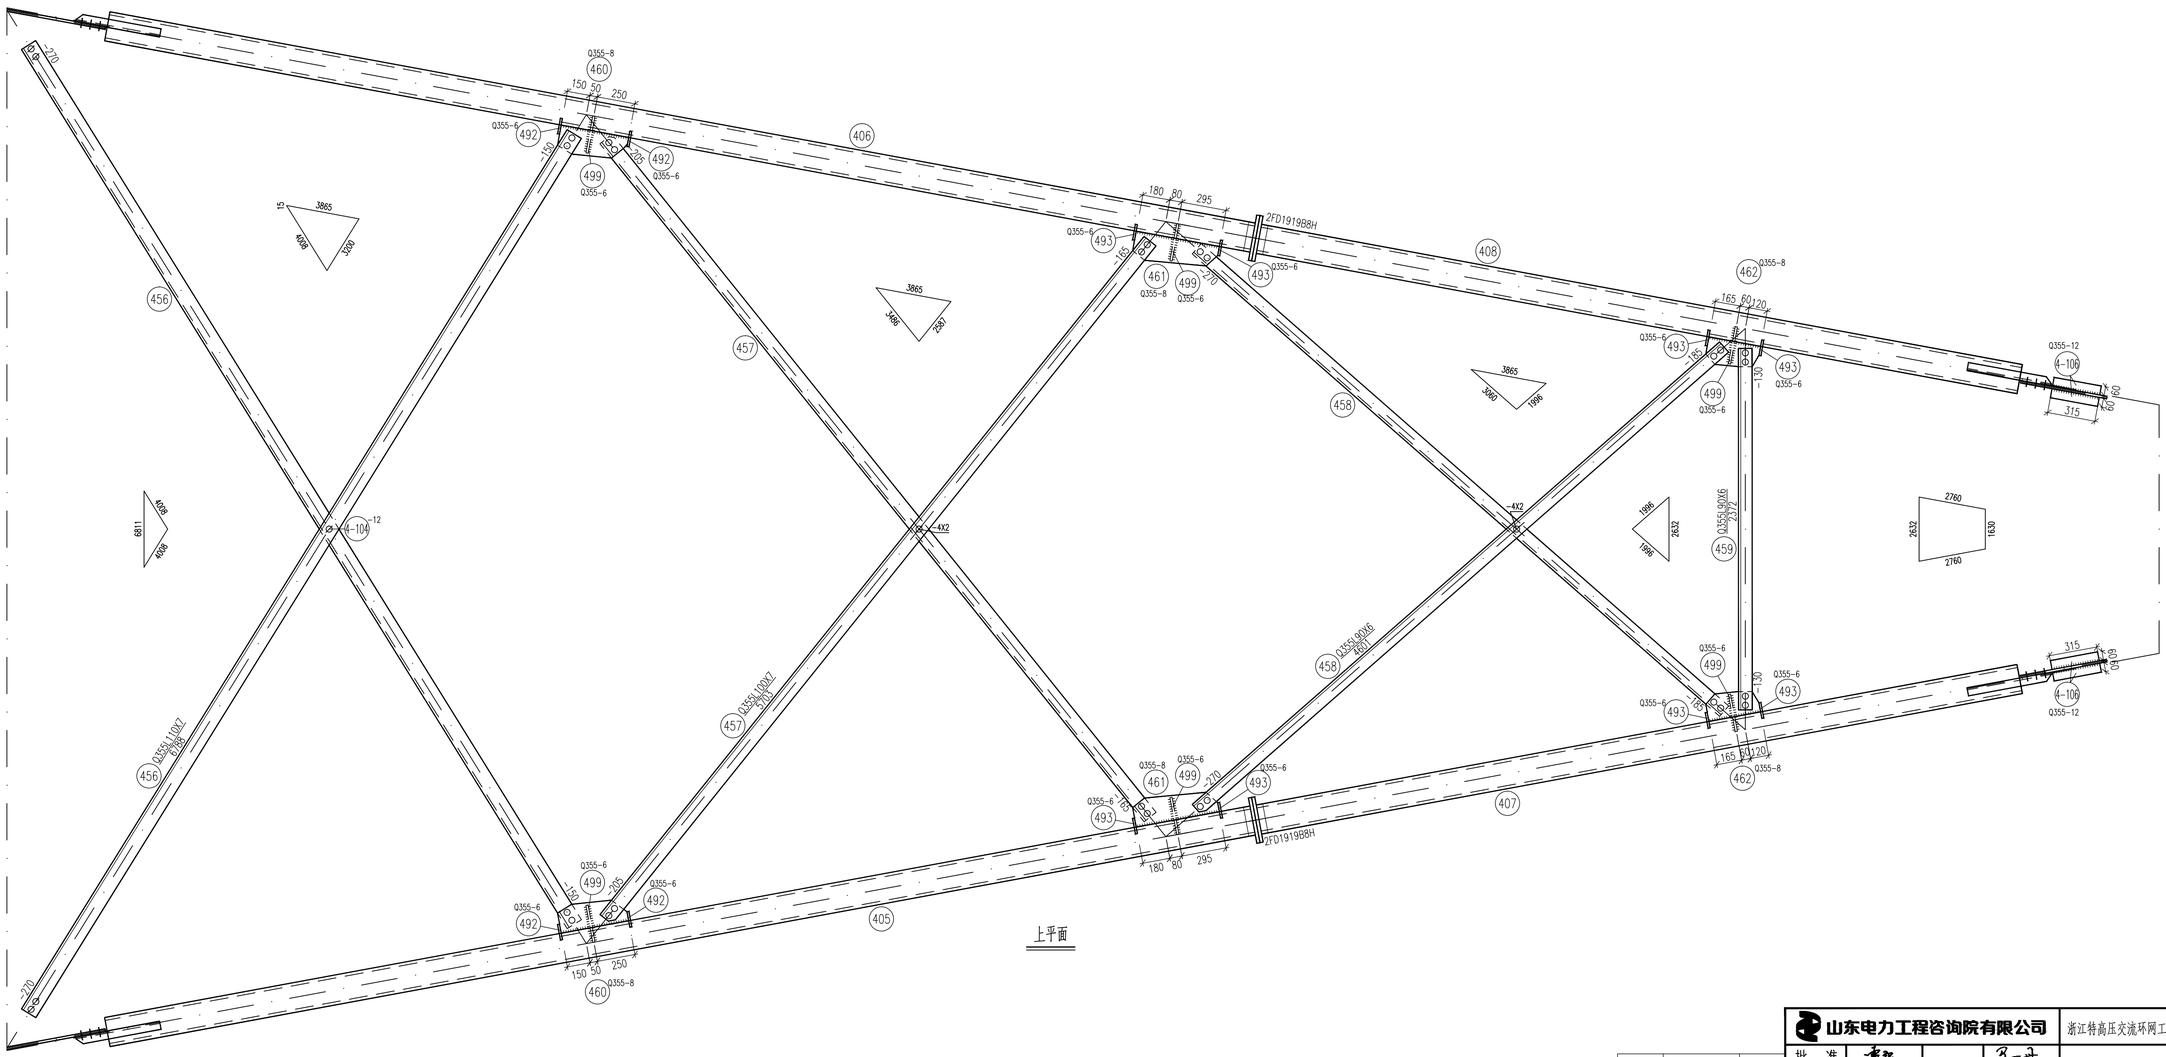

上平面

山东电力工程咨询院有限公司				浙江特高压交流环网工程线路	工程	施工图	设计阶段
批 准		校 核		SZK31102A直线塔			
审 核		设计/勘测		下导线横担结构图(3/3)		④	
电气专业	会签	日 期	2026.08	比 例		日 期	2026年 08月
				图 号	37-SA36901S-T0121-012		版本