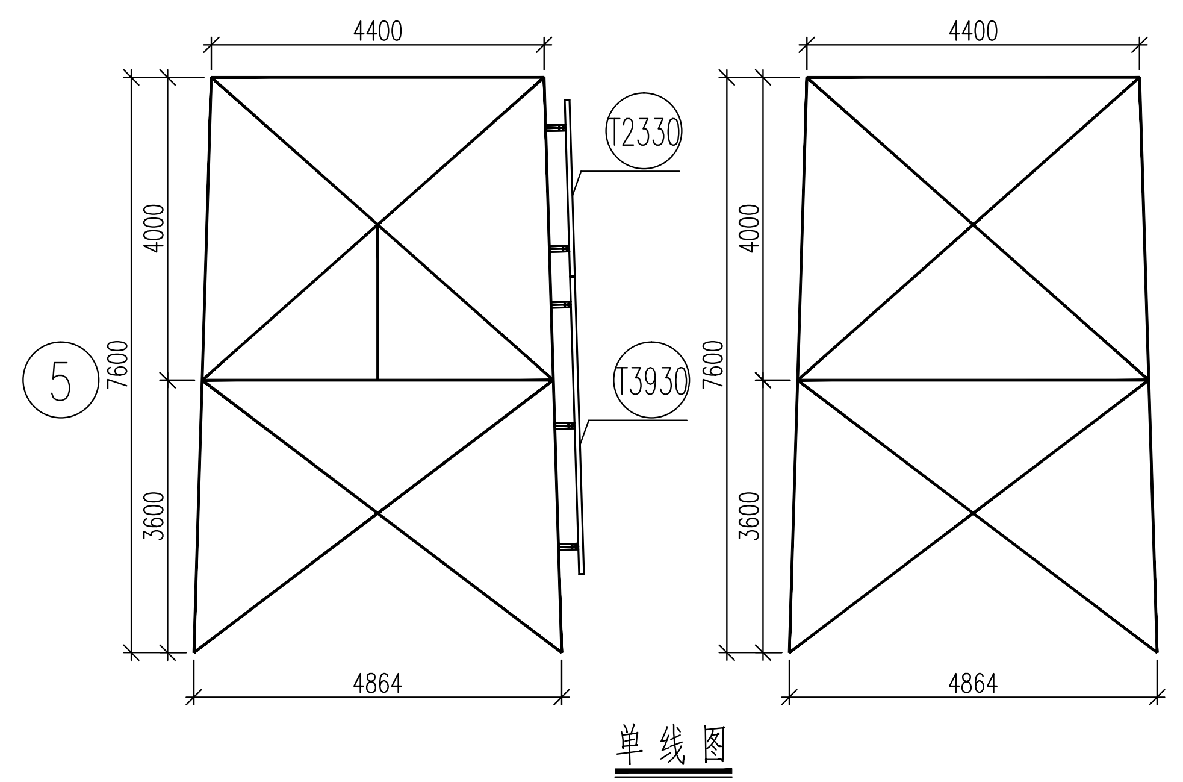

单线图
1:100

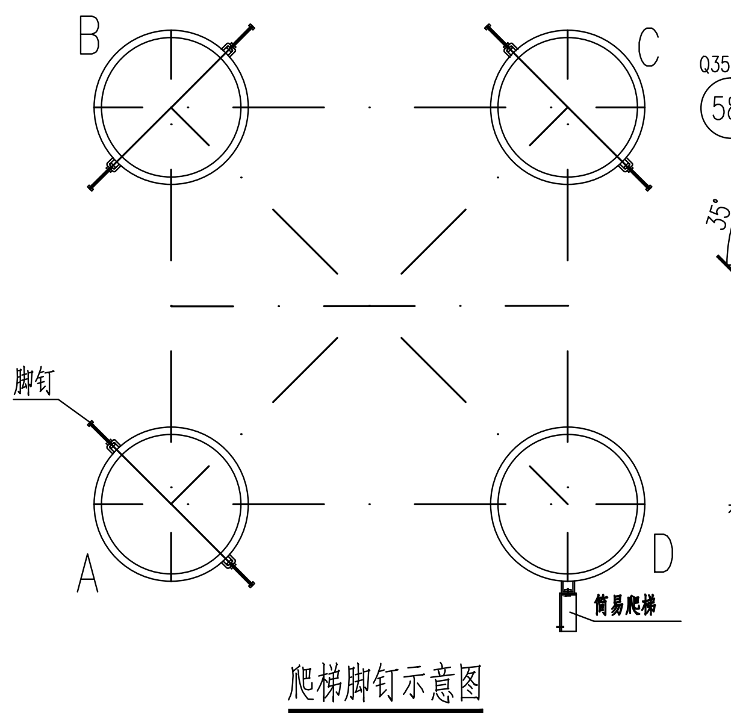

爬梯脚钉示意图

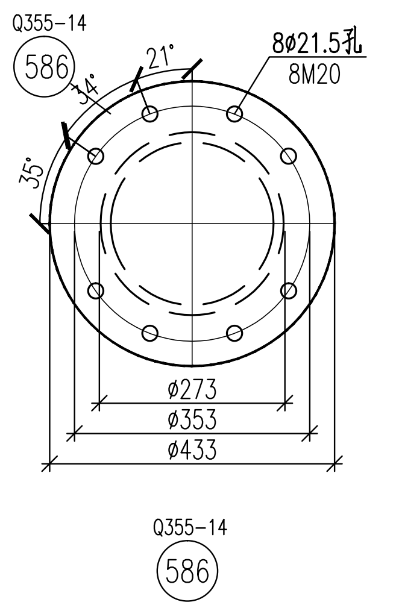

Q355-14
586
1:10

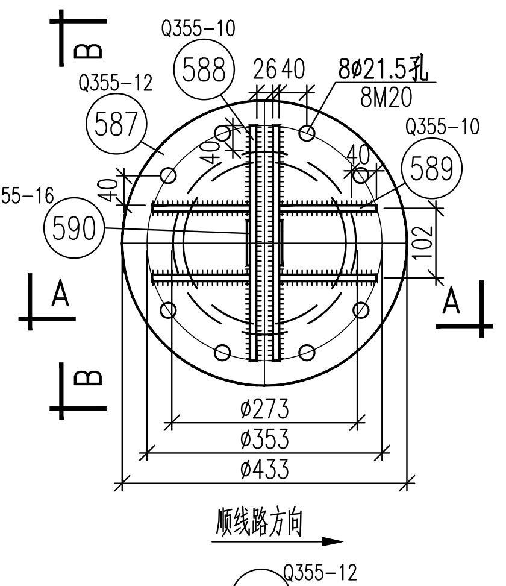

Q355-12
587
1:10

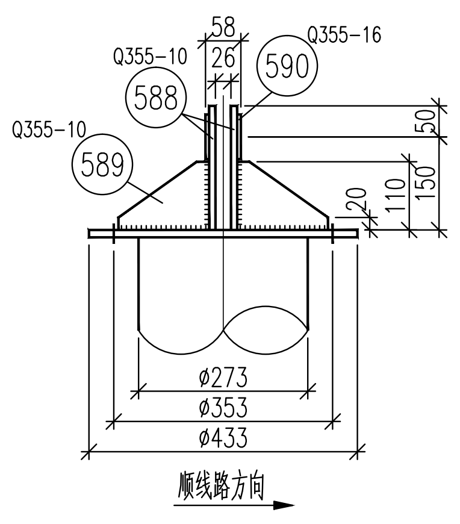

A－A

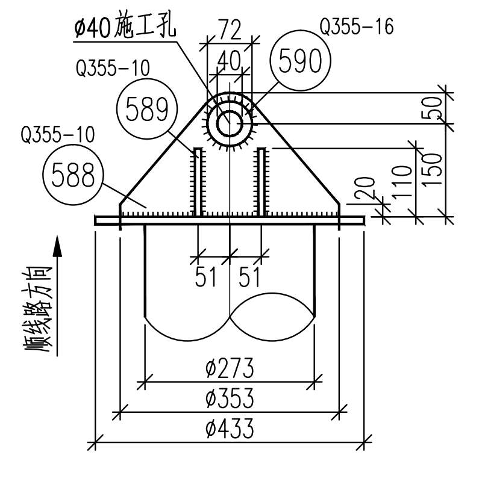

B－B

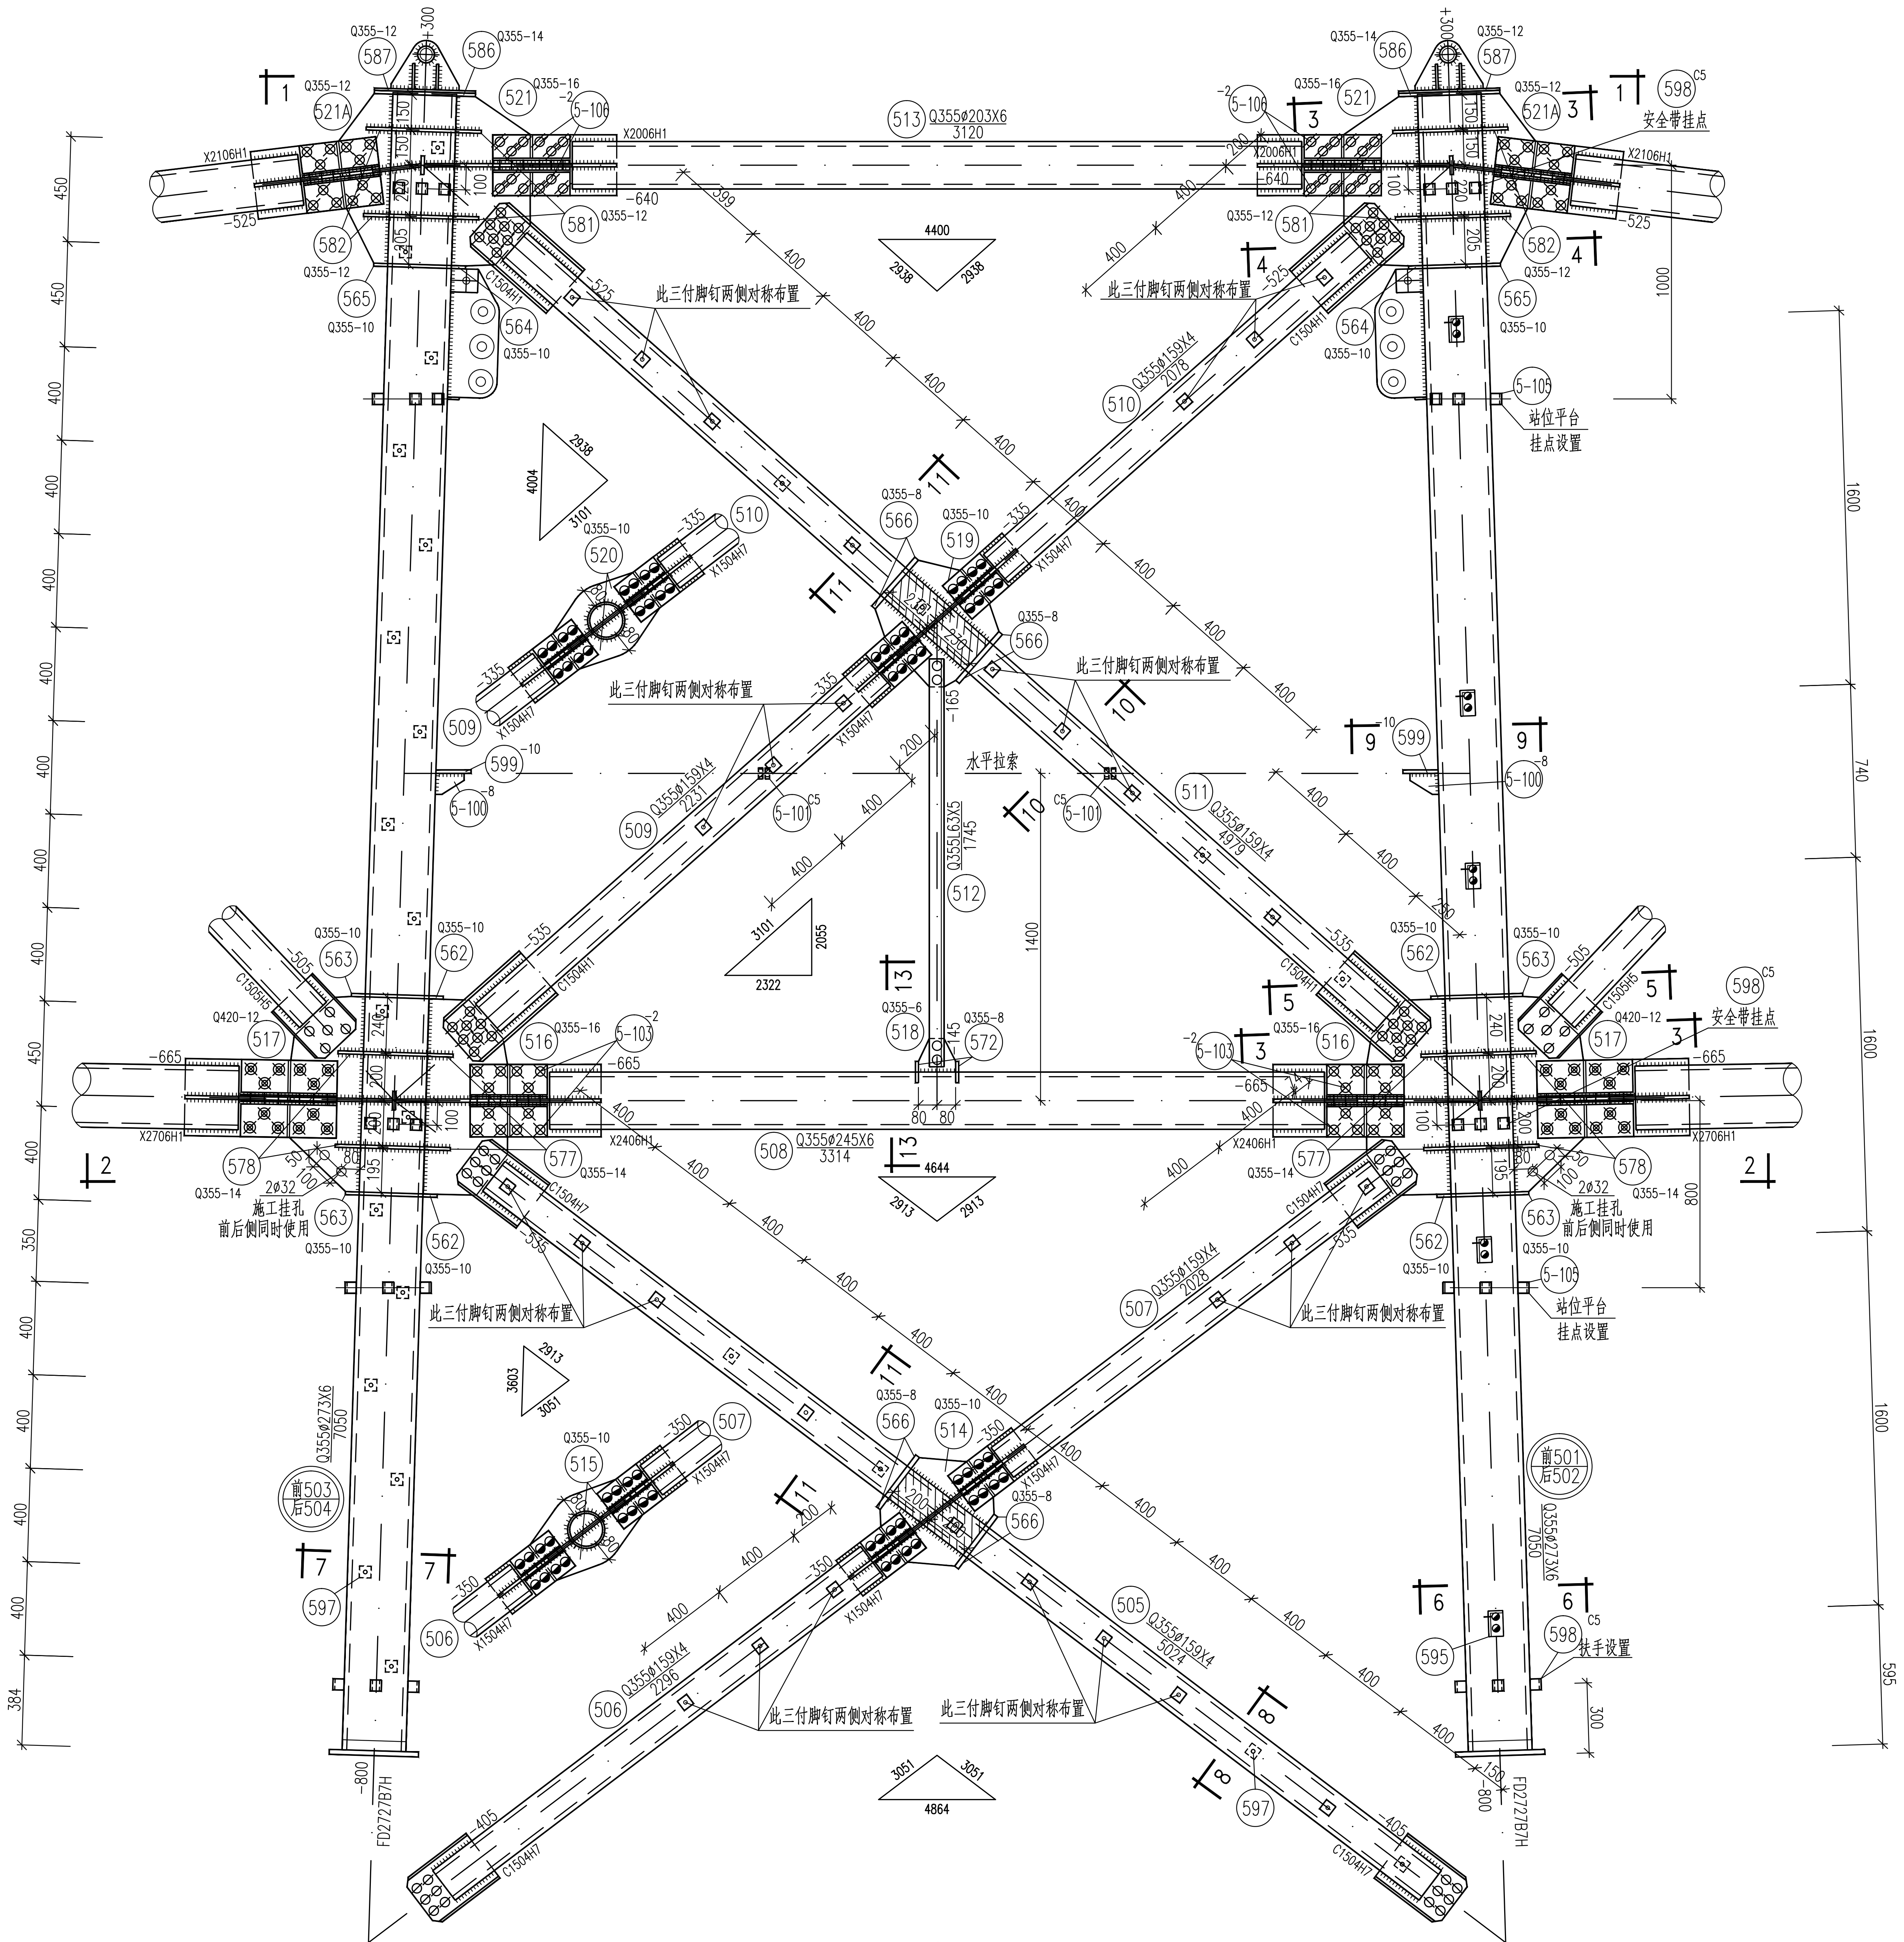

正面结构图

构 件 明 细 表

编号	规 格	长 度 (mm)	数量	重 量(kg) 一 件	重 量(kg) 小 计	备 注
579	Q355-14X110	282	8	3.41	27.3	
580	Q355-12X110	302	8	3.13	25.0	
581	Q355-12X110	302	8	3.13	25.0	
582	Q355-12X110	322	8	3.34	26.7	
583	Q355-12X110	282	4	2.92	11.7	
584	Q355-16X80	201	4	2.02	8.1	
585	Q355-14X80	191	4	1.68	6.7	
586	Q355-14X473	434	4	22.56	90.2	
587	Q355-12X473	434	4	19.34	77.4	
588	Q355-10X200	354	8	5.56	44.5	
589	Q355-10X110	177	16	1.53	24.5	
590	Q355-16X72	72	8	0.65	5.2	
591	Q355-14X210	550	4	12.69	50.8	
592	Q355-38X104	104	12	3.23	38.8	
593	Q355-10X100	115	8	0.90	7.2	
594	Q355-6X50	100	4	0.24	1.0	
595	Q355L63X5	383	5	1.85	9.3	火曲 电焊
596	-6X100	180	5	0.85	4.2	火曲
597	C5	50	295	0.27	79.6	槽钢
598	C5	25	48	0.14	6.7	槽钢
599	-10X138	190	4	2.06	8.2	拉索附件
5-100	-8X80	100	4	0.50	2.0	拉索附件
5-101	C5	50	8	0.27	2.2	槽钢
5-102	-6X50	50	8	0.12	1.0	拉索附件
5-103	-2X130	160	32	0.33	10.6	垫块
5-104	-2X150	200	16	0.47	7.5	垫块
5-105	C5	50	32	0.27	8.6	槽钢
5-106	-2X100	160	32	0.25	8.0	垫块
5-107	-2X120	160	16	0.30	4.8	垫块
	GJ-50	4700	4	7.27	29.1	拉索附件
	NUT-2		4	3.20	12.8	拉索附件
	U-10		4	0.60	2.4	拉索附件
	NX-2.1		4	2.40	9.6	拉索附件
	JK-2		8	0.32	2.6	拉索附件
	FD2727B7H		4	12.2	48.8	
	C1404H5		12	4.80	57.6	
	C1504H1		8	16.00	128.0	
	C1504H7		16	9.61	153.8	
	C1905H5		4	8.80	35.2	
	X1404H7		4	11.3	45.2	
	X1504H7		12	13.1	157.2	
	X2006H1		4	38.0	152.0	
	X2406H1		4	49.3	197.2	
	T3930		1	20.7	20.7	
	T2330		1	12.4	12.4	
合 计		6850.0 kg				

螺栓、脚钉、垫圈 明细表

名称	级别	规 格	符 号	数量	重量(kg)	备 注
螺栓	6.8级	M16X45	⊘	24	4.0	
		M16X55	⊘	260	48.0	
		M20X55	○	81	26.5	
		M20X65	∅	226	79.8	
		M20X75	⊗	336	127.1	
		M20X85	∅	48	19.4	
	8.8级	M24X85	⊗	96	60.5	
脚钉	6.8级	M16X185	⊖	295	122.3	
			⊣			
垫圈	Q235		规格X个数			
合 计			487.6 kg			

构 件 明 细 表

编号	规 格	长 度 (mm)	数量	重 量(kg) 一 件	重 量(kg) 小 计	备 注
501	Q355ø273X6	7050	1	278.53	278.5	带爬梯
502	Q355ø273X6	7050	1	278.53	278.5	带脚钉
503	Q355ø273X6	7050	1	278.53	278.5	带脚钉
504	Q355ø273X6	7050	1	278.53	278.5	带脚钉
505	Q355ø159X4	5024	2	76.82	153.6	带脚钉
506	Q355ø159X4	2296	2	35.11	70.2	带脚钉
507	Q355ø159X4	2028	2	31.01	62.0	带脚钉
508	Q355ø245X6	3314	2	117.20	234.4	
509	Q355ø159X4	2231	2	34.11	68.2	带脚钉
510	Q355ø159X4	2078	2	31.77	63.5	带脚钉
511	Q355ø159X4	4979	2	76.13	152.3	带脚钉
512	Q355L63X5	1745	2	8.41	16.8	
513	Q355ø203X6	3120	2	90.95	181.9	
514	Q355-10X400	461	2	14.44	28.9	
515	Q355-10X153	461	4	5.52	22.1	
516	Q355-16X355	836	4	37.28	149.1	
517	Q420-12X307	836	4	24.15	96.6	
518	Q355-6X160	145	2	1.09	2.2	
519	Q355-10X460	431	2	15.53	31.1	
520	Q355-10X153	431	4	5.16	20.6	
521	Q355-16X317	726	4	28.91	115.6	
521A	Q355-12X226	726	4	15.43	61.7	
522	Q355ø159X4	5044	2	77.12	154.2	带脚钉
523	Q355ø159X4	2296	2	35.11	70.2	带脚钉
524	Q355ø159X4	2048	2	31.31	62.6	带脚钉
525	Q355ø194X5	3664	2	85.39	170.8	
526	Q355ø140X4	5059	2	67.87	135.7	带脚钉
527	Q355ø140X4	2286	2	30.67	61.3	带脚钉
528	Q355ø140X4	2123	2	28.48	57.0	带脚钉
529	Q355ø140X4	3520	2	47.22	94.4	
530	Q355-10X440	461	2	15.92	31.8	
531	Q355-10X163	461	4	5.90	23.6	
532	Q355-12X377	836	4	29.69	118.8	
533	Q355-10X390	416	2	12.74	25.5	
534	Q355-10X154	416	4	5.03	20.1	
535	Q355-12X326	726	4	22.29	89.2	
536	Q355L90X6	2763	2	23.07	46.1	切角
537	Q355L90X6	2763	2	23.07	46.1	切角
538	Q355L63X5	2009	2	9.69	19.4	
539	Q355L63X5	2000	2	9.64	19.3	
540	Q355L63X5	1402	4	6.76	27.0	
541	Q355-8X176	521	2	5.76	11.5	
542	Q355-8X177	461	2	5.12	10.2	
543	Q355-6X412	374	4	7.26	29.0	
544	Q355-16X324	455	4	18.52	74.1	
545	Q355-16X326	339	4	13.88	55.5	
546	Q355-16X319	454	4	18.19	72.8	
547	Q355-16X353	338	4	14.99	60.0	
548	Q355L125X8	2856	2	44.28	88.6	切角
549	Q355L125X8	2856	2	44.28	88.6	切角
550	Q355L75X5	2132	2	12.40	24.8	
551	Q355L75X5	2122	2	12.35	24.7	
552	L45X4	926	2	2.53	5.1	
553	L45X4	931	2	2.55	5.1	
554	Q355L80X6	1488	4	10.98	43.9	
555	Q355-10X233	681	2	12.46	24.9	
556	Q355-10X235	631	2	11.64	23.3	
557	Q355-8X426	388	4	10.38	41.5	
558	Q355-16X331	480	4	19.96	79.8	
559	Q355-16X316	437	4	17.34	69.4	
560	Q355-16X329	480	4	19.83	79.3	
561	Q355-16X375	437	4	20.58	82.3	
562	Q355-10X80	555	8	3.49	27.9	
563	Q355-10X80	555	8	3.49	27.9	
564	Q355-10X80	555	4	3.49	14.0	
565	Q355-10X80	555	4	3.49	14.0	
566	Q355-8X60	345	24	1.30	31.2	
567	Q355-8X60	315	8	1.19	9.5	
568	Q355-6X60	208	4	0.59	2.4	
569	Q355-6X60	158	4	0.45	1.8	
570	Q355-8X60	241	4	0.91	3.6	
571	Q355-8X60	201	4	0.76	3.0	
572	Q355-8X145	464	4	4.23	16.9	
573	Q355-8X83	148	4	0.77	3.1	
574	Q355-6X81	193	4	0.74	3.0	
575	Q355-6X73	184	4	0.63	2.5	
576	Q355-14X110	302	8	3.65	29.2	
577	Q355-14X110	302	8	3.65	29.2	
578	Q355-14X110	322	8	3.89	31.1	

山东电力工程咨询院有限公司			浙江特高压交流环网工程线路 工程	施工图	设计阶段
批 准	雷强	校 核	马一丹	SZK31102A直线塔 身部结构图(1/3) ⑤	
审 核	高锡鹏				
		设计/勘测			
比 例		日 期	2026年 08月	图 号 37-SA36901S-T0121-013	版本