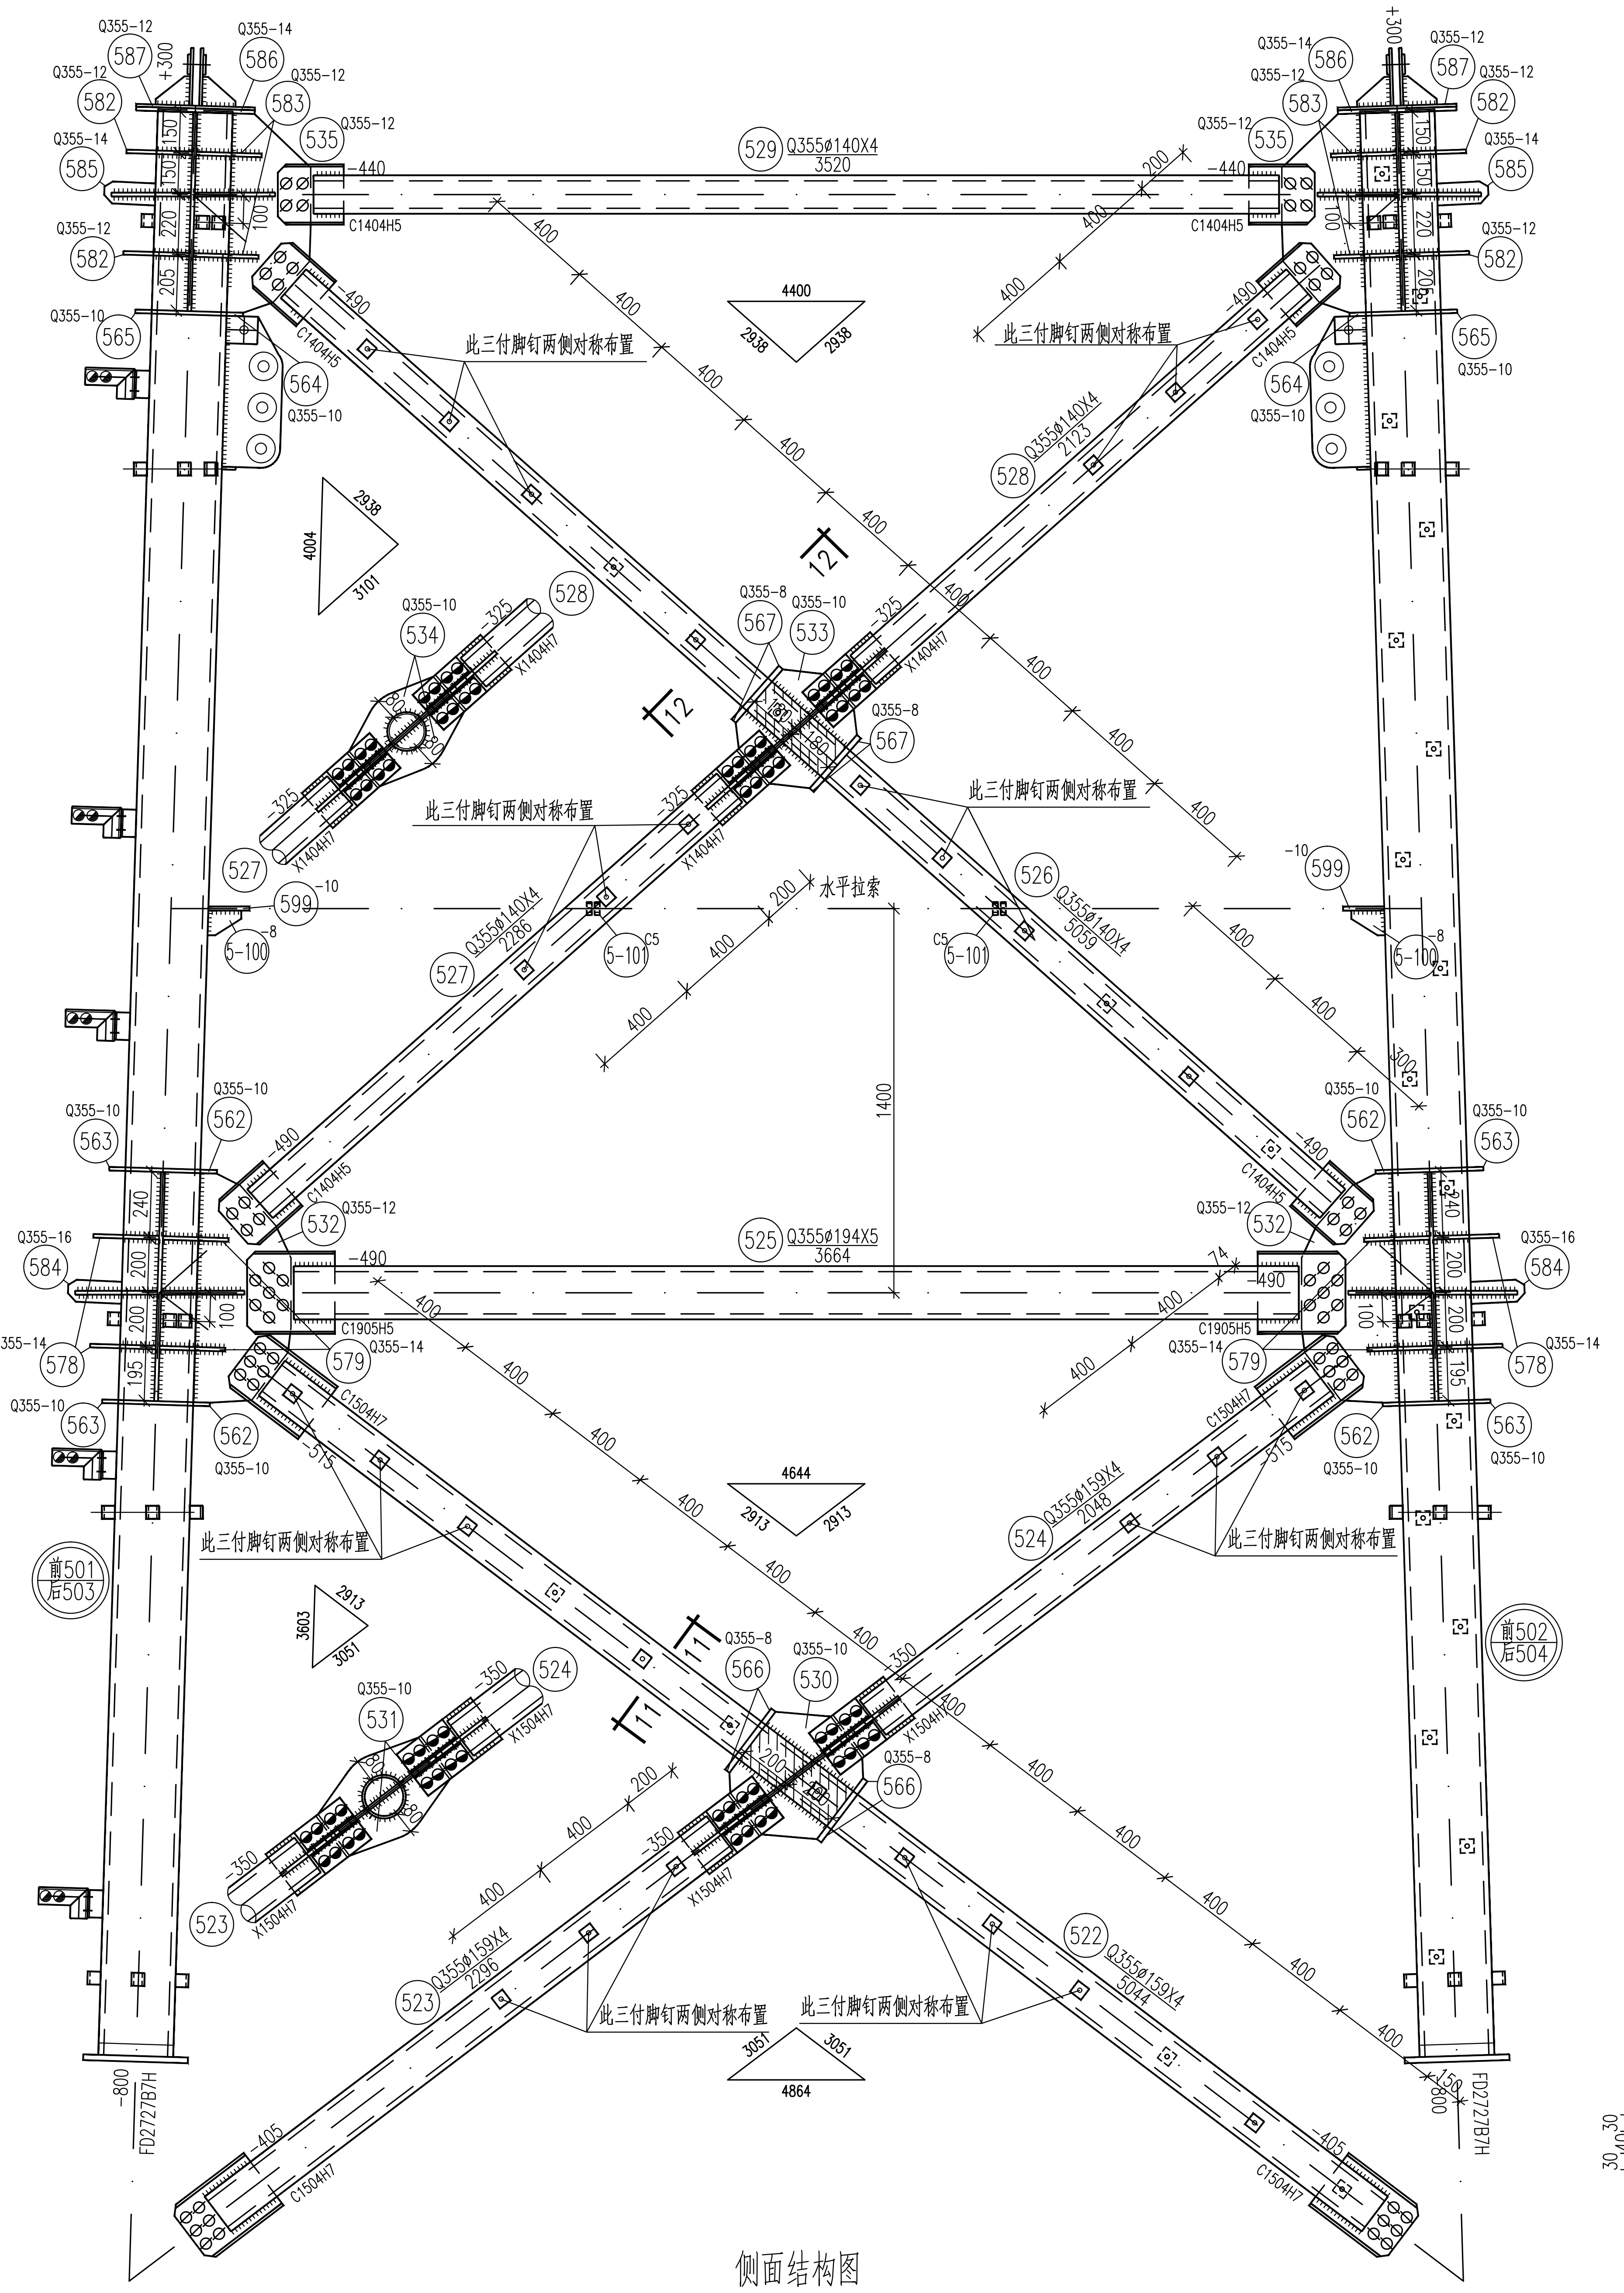

侧面结构图

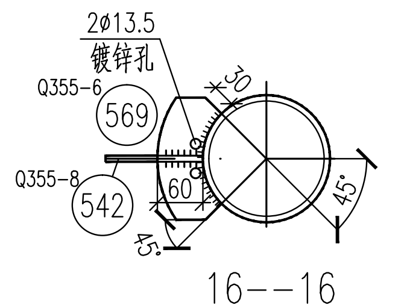

16--16
1:10

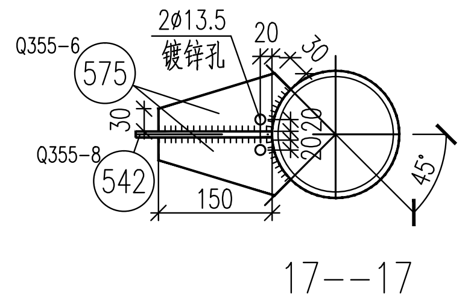

17--17
1:10

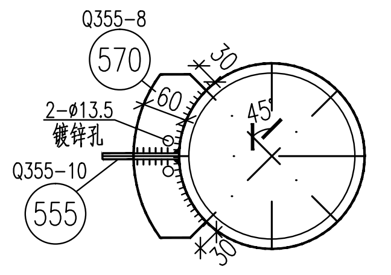

18--18
1:10

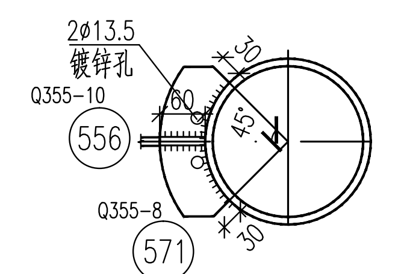

19--19
1:10

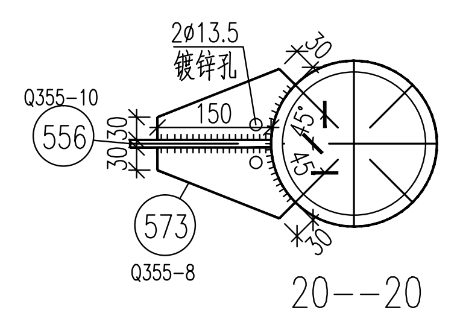

20--20
1:10

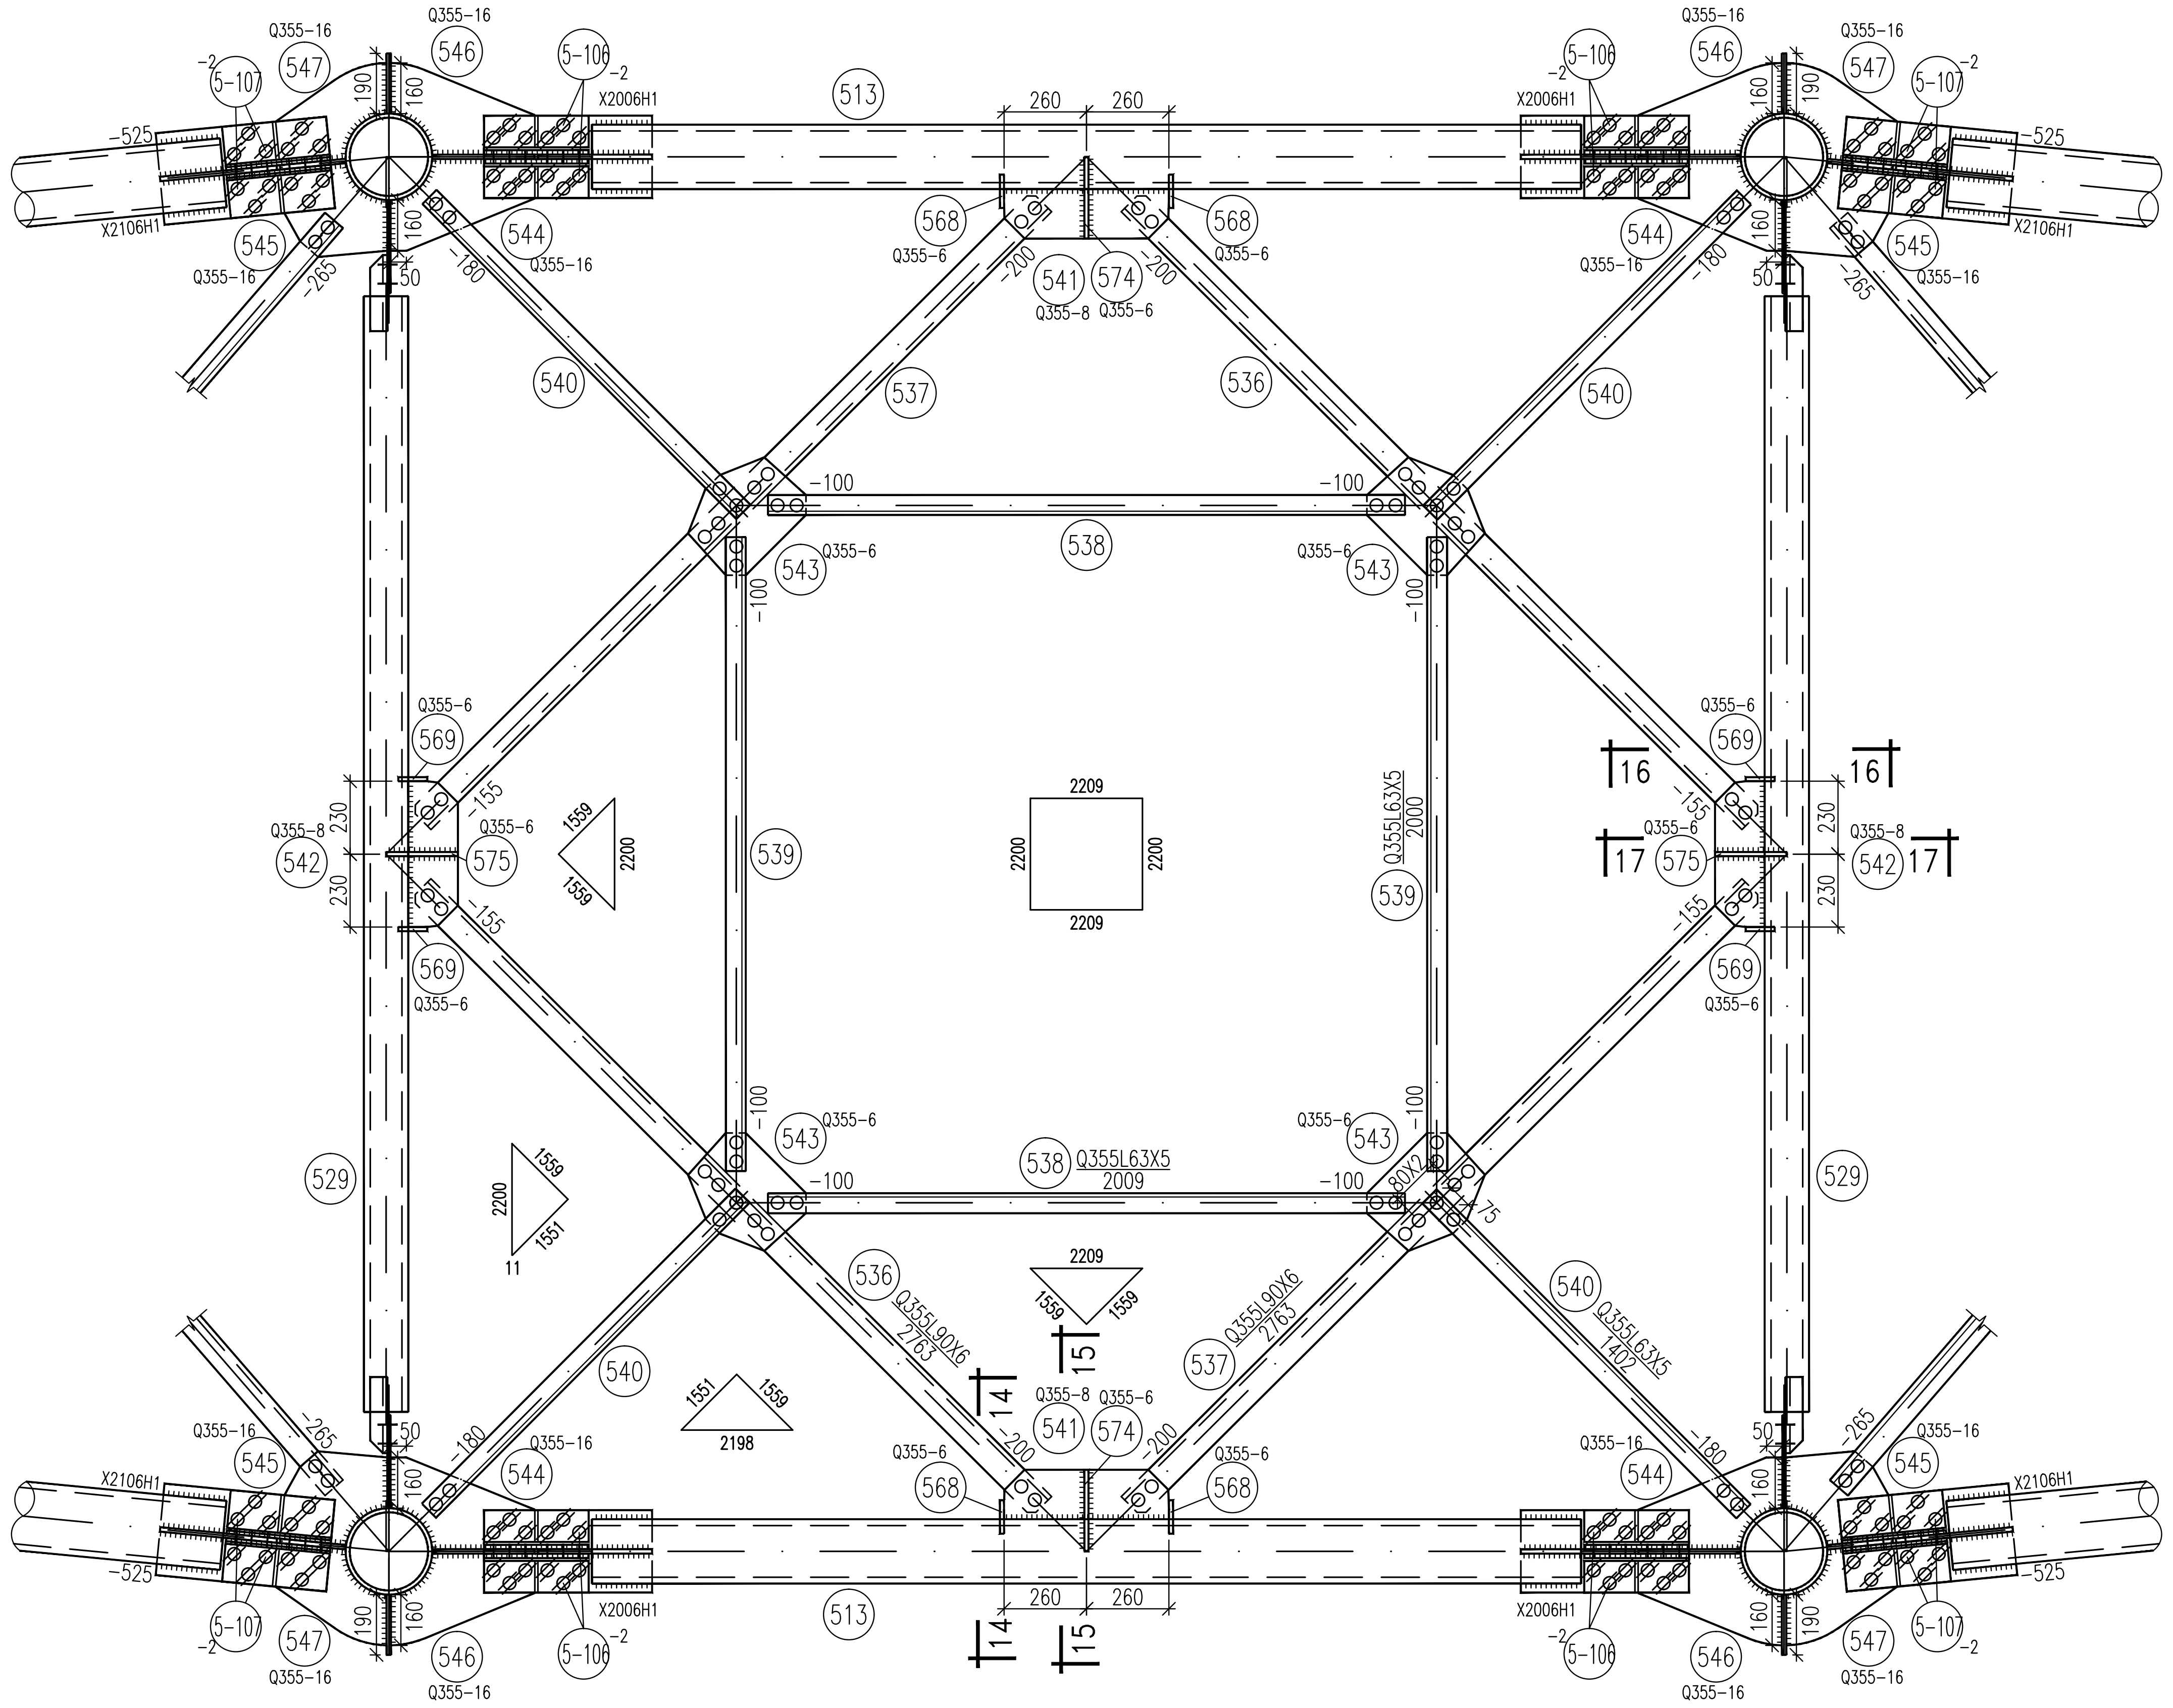

1 - 1

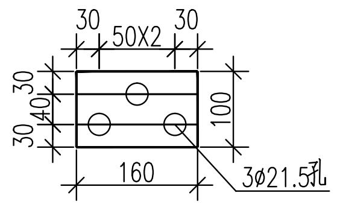

5-106 -2
1:10

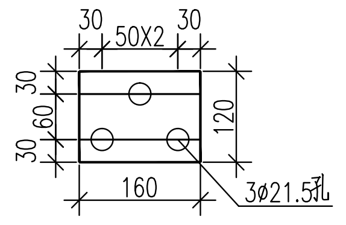

5-107 -2
1:10

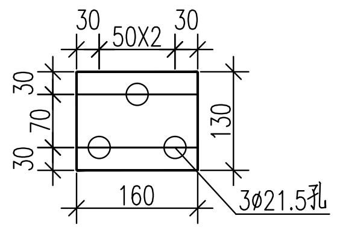

5-103 -2
1:10

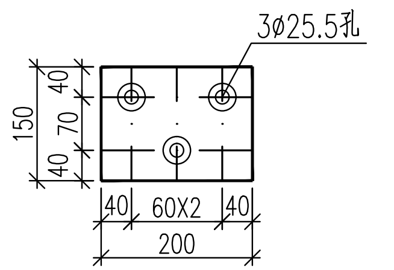

5-104 -2
1:10

山东电力工程咨询院有限公司				浙江特高压交流环网工程线路 工程	施工图	设计阶段
批准	雷强	校核	马一丹	SZK31102A直线塔 身部结构图(2/3) ⑤		
审核	高锡鹏					
		设计/勘测	潘胜光			
比例		日期	2026年 08月	图号 37-SA36901S-T0121-014	版本	