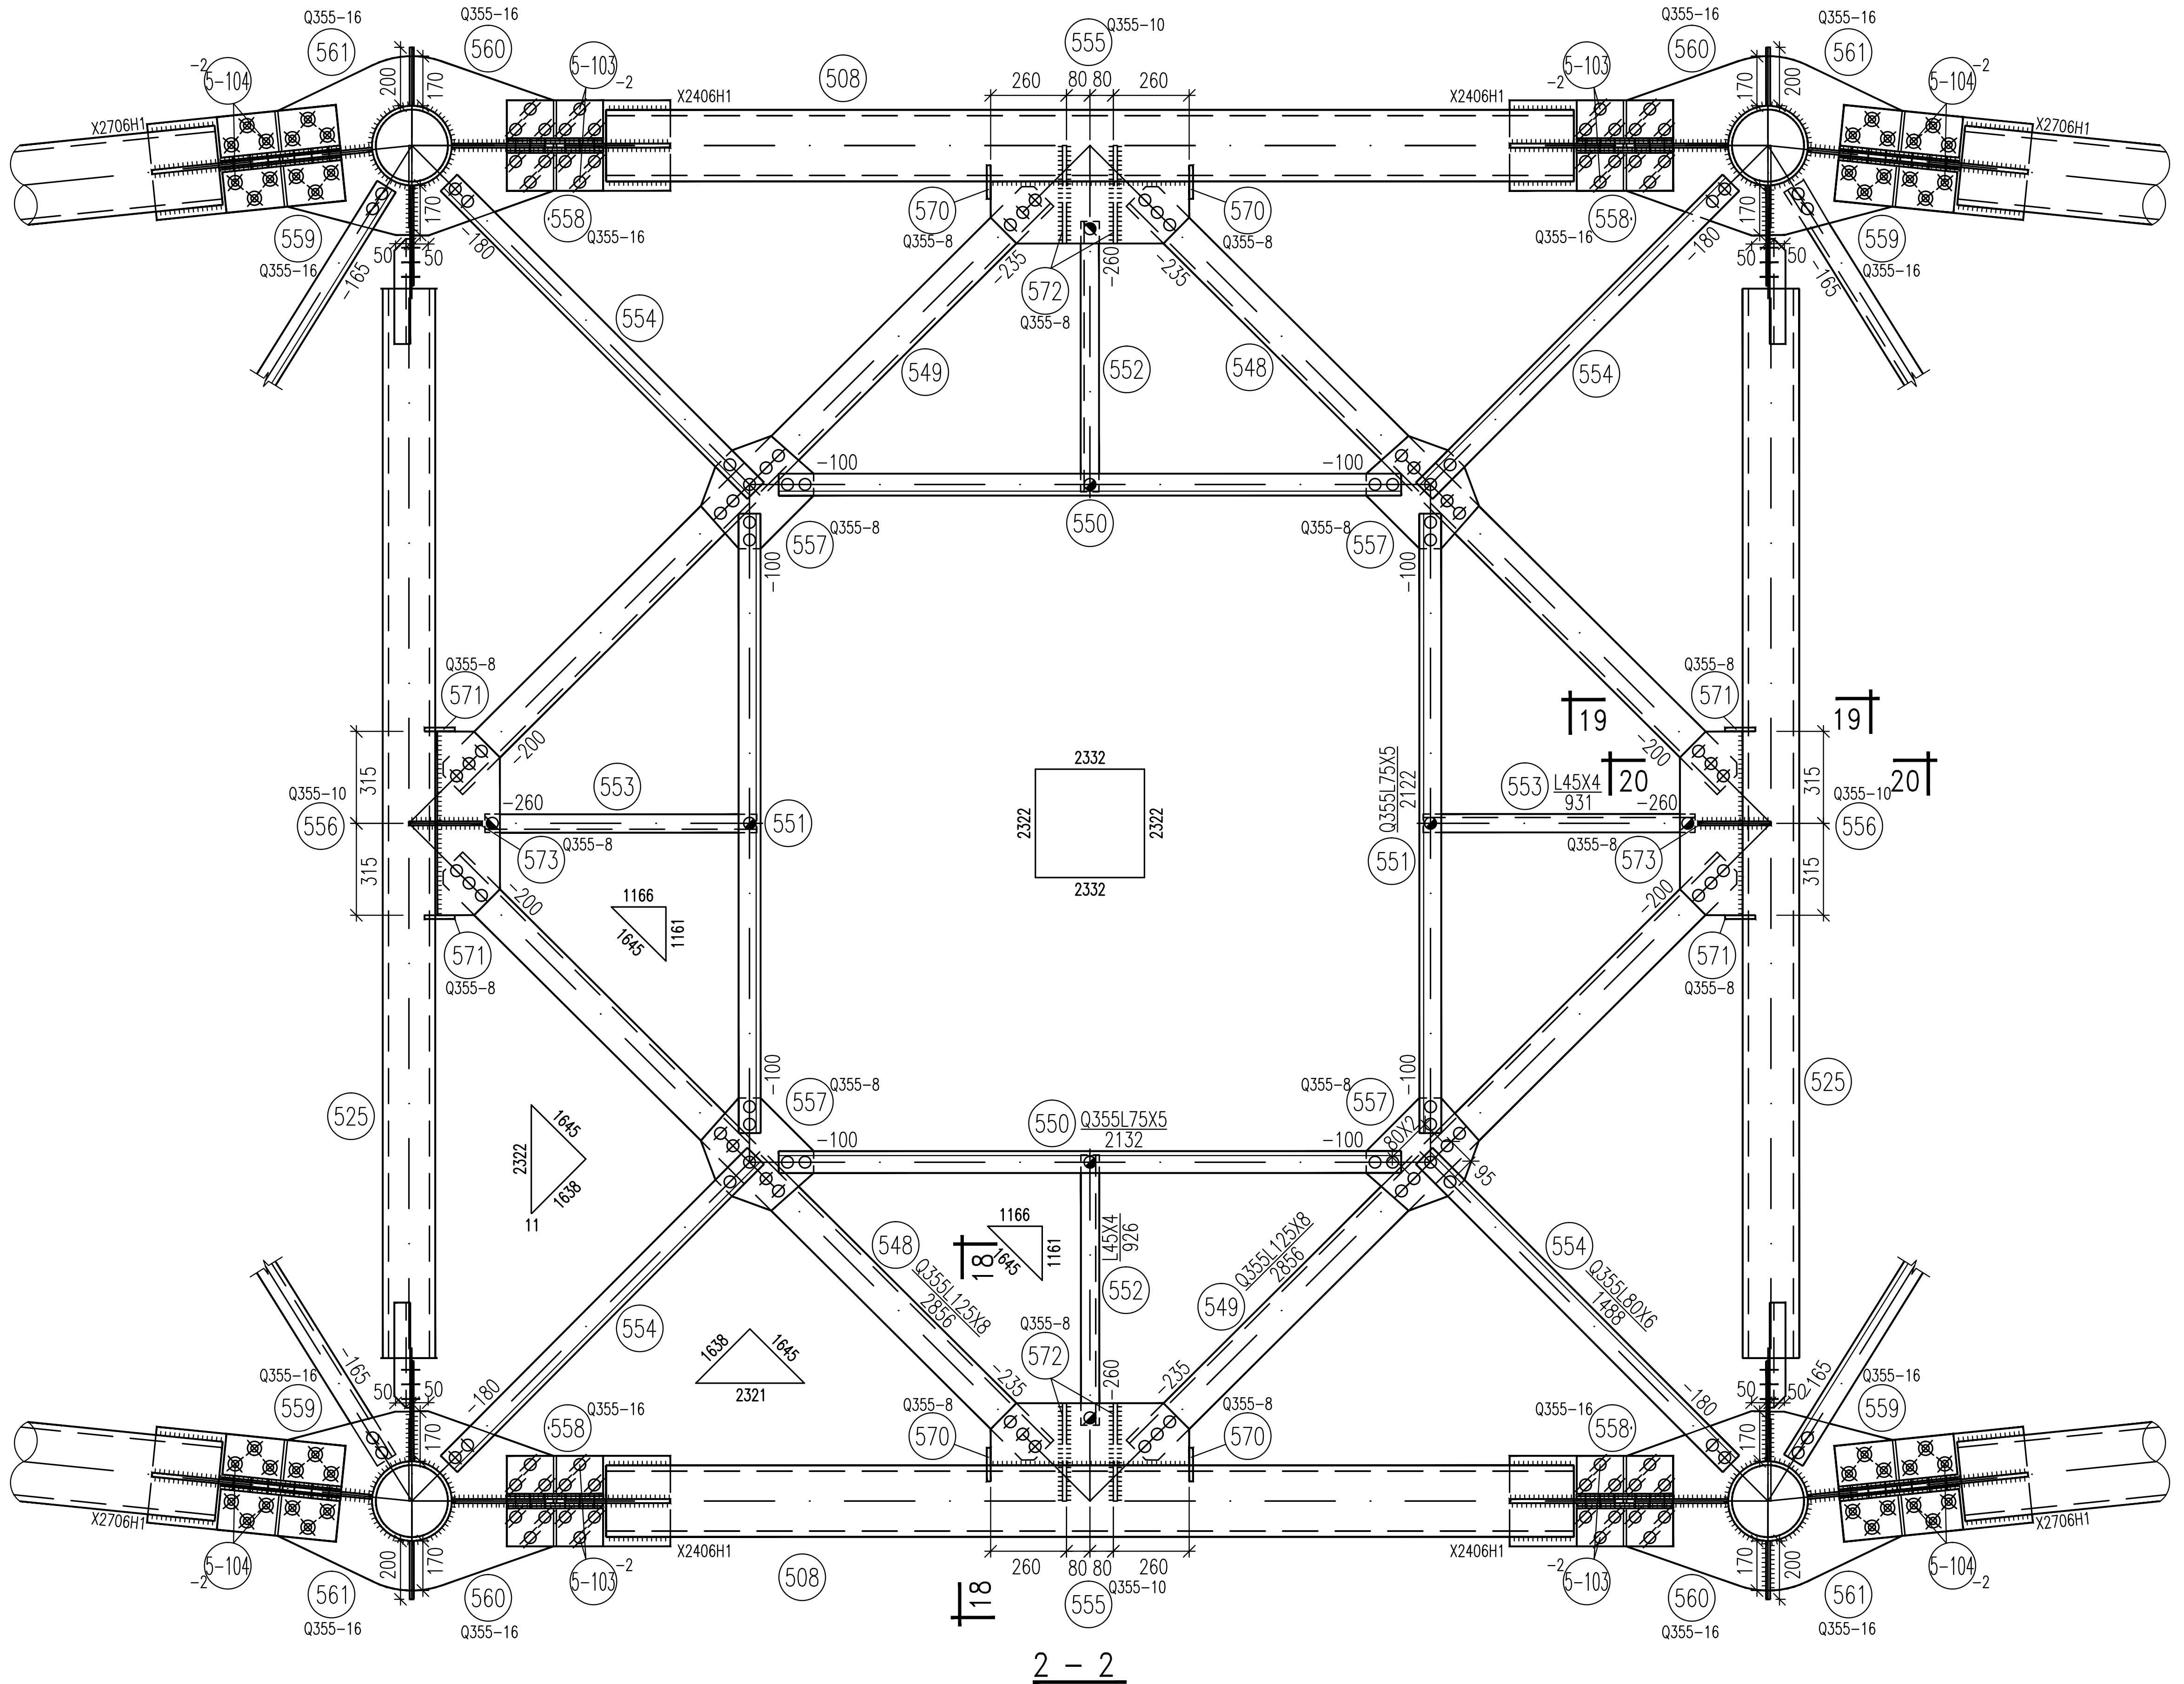

2 - 2

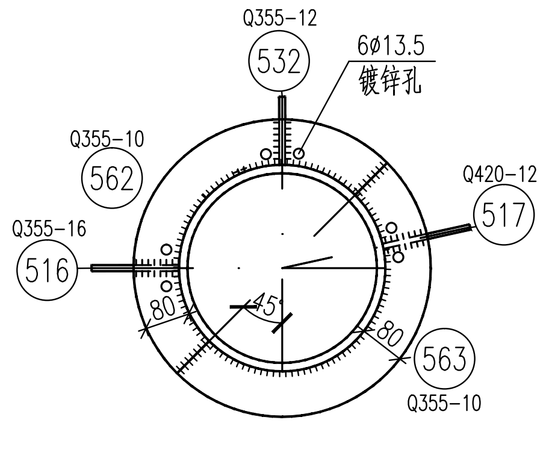

5--5
1:10

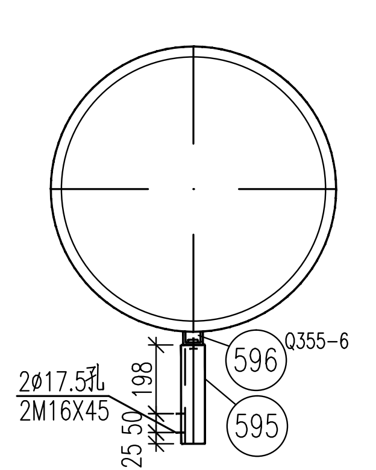

6--6
1:10

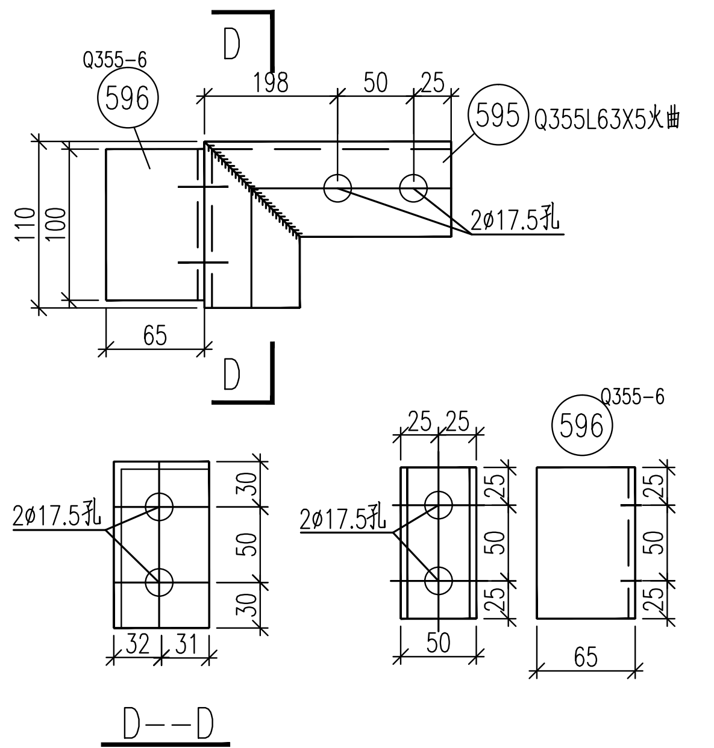

D--D
1:10

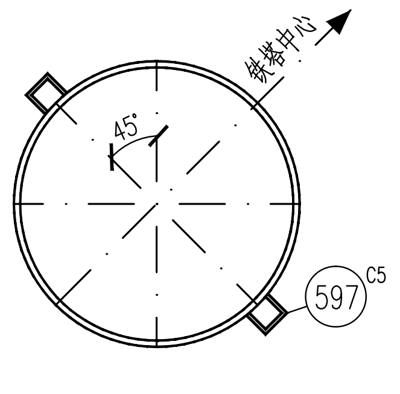

7--7
1:10

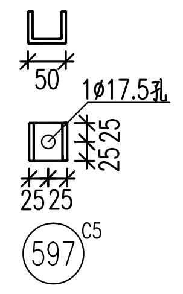

1:10

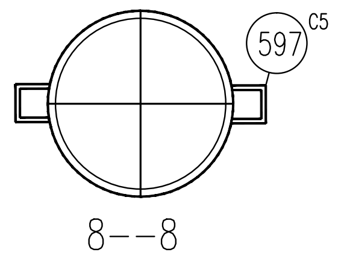

8--8
1:10

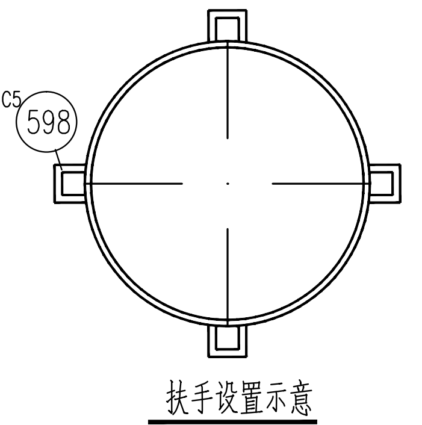

扶手设置示意

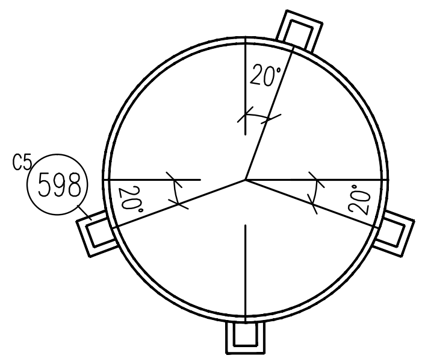

安全带挂点示意

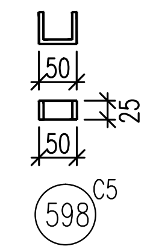

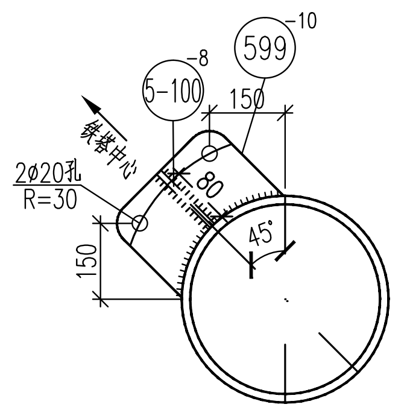

9--9
1:10

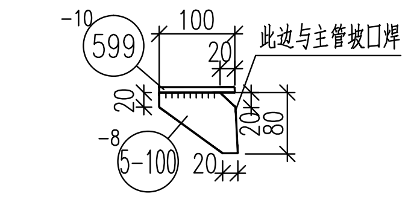

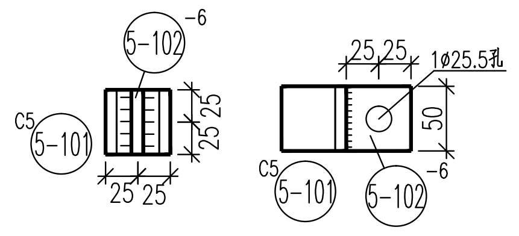

10--10
1:10

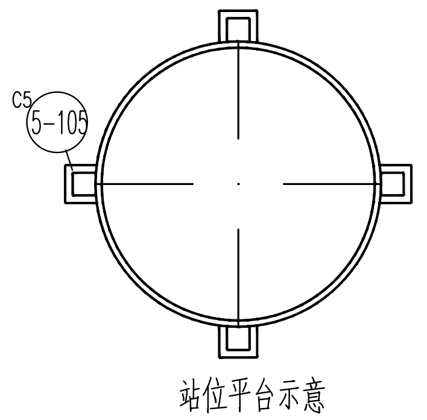

站位平台示意

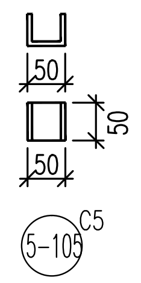

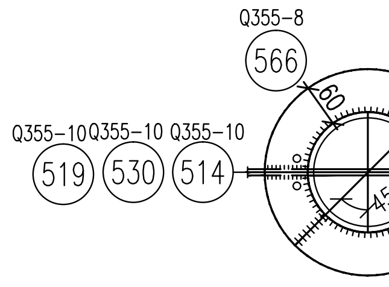

11--11
1:10

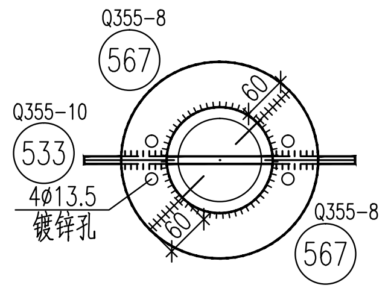

12--12
1:10

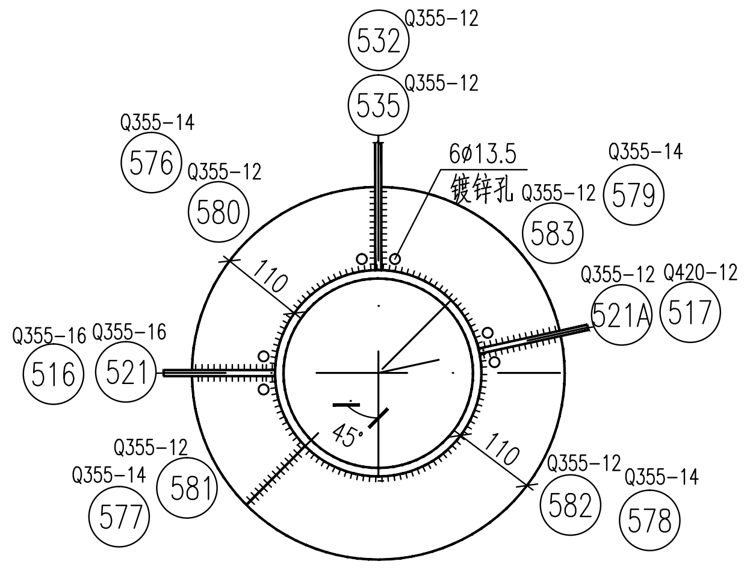

3--3
1:10

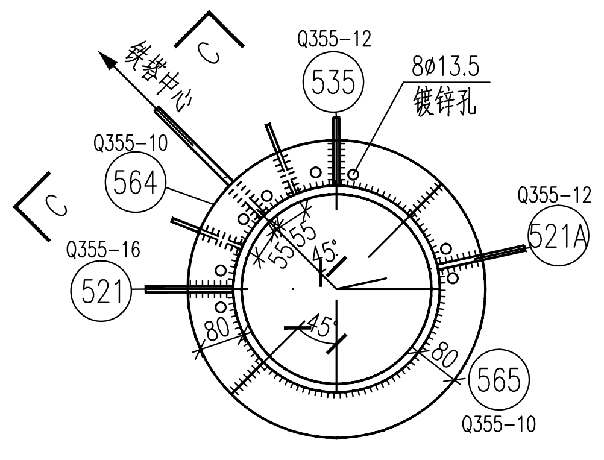

4--4
1:10

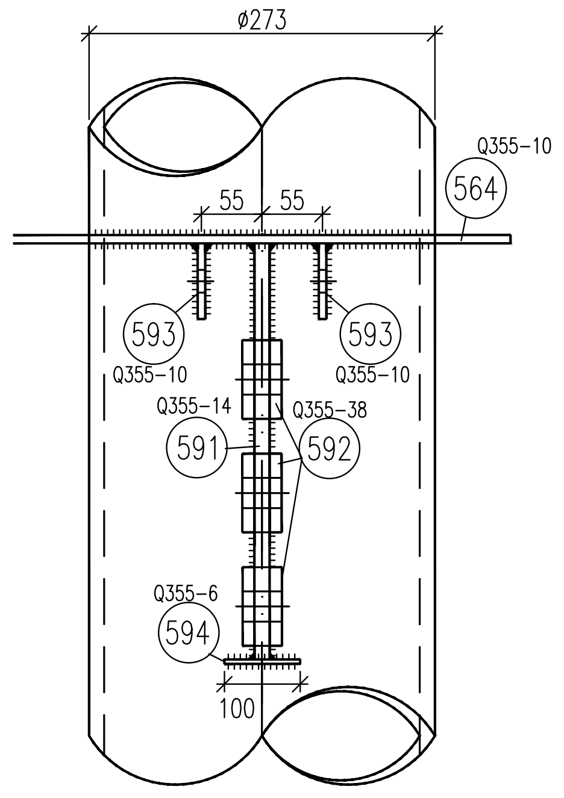

C--C
1:10

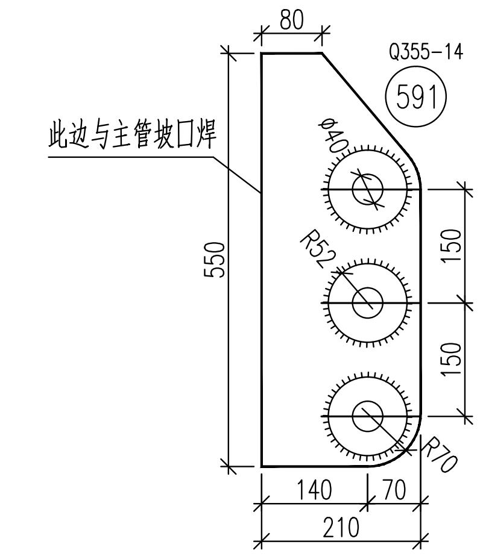

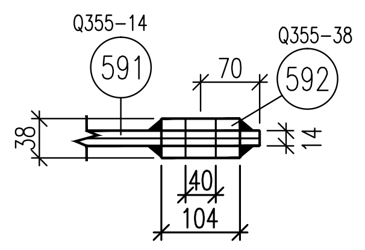

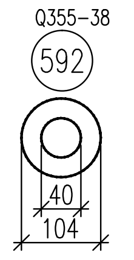

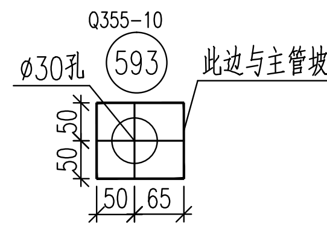

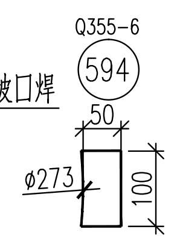

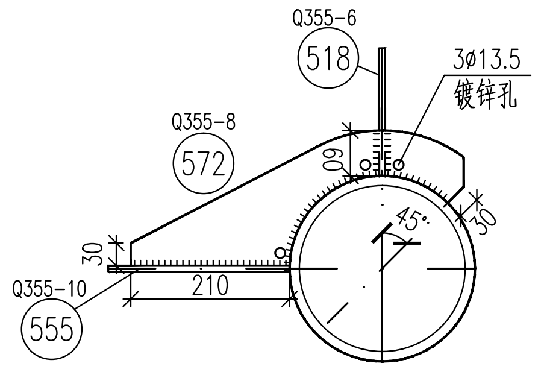

13--13
1:10

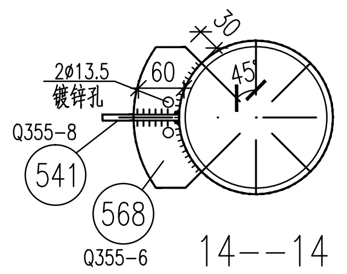

14--14
1:10

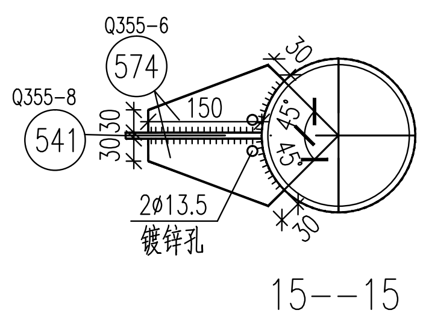

15--15
1:10

山东电力工程咨询院有限公司				浙江特高压交流环网工程线路 工程	施工图	设计阶段
批　准		校　核		SZK31102A直线塔 身部结构图(3/3) ⑤		
审　核						
		设计/勘测				
比　例		日　期	2026年 08月	图　号 37-SA36901S-T0121-015	版本	