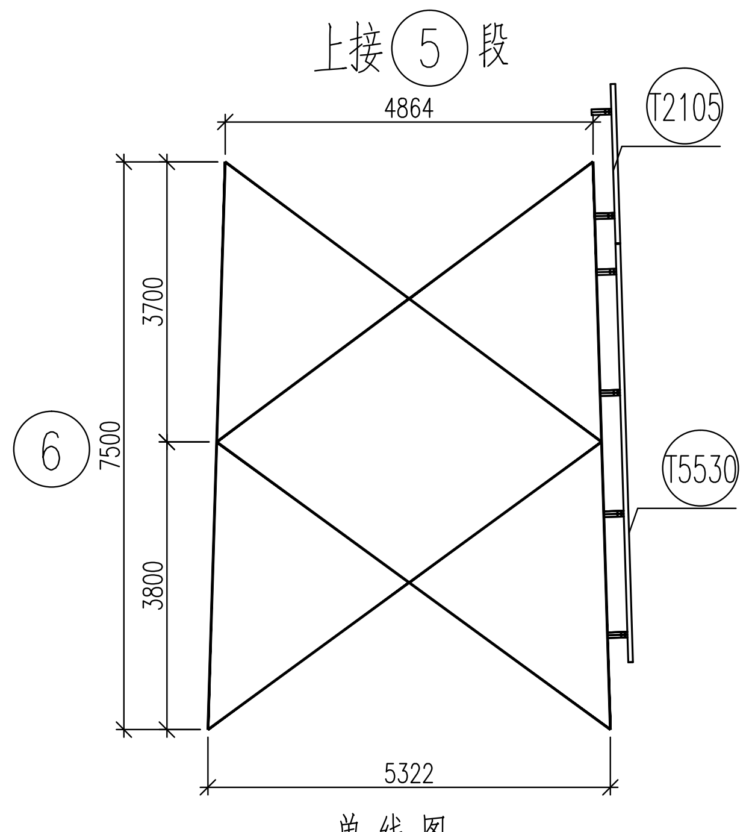

单线图
1:100

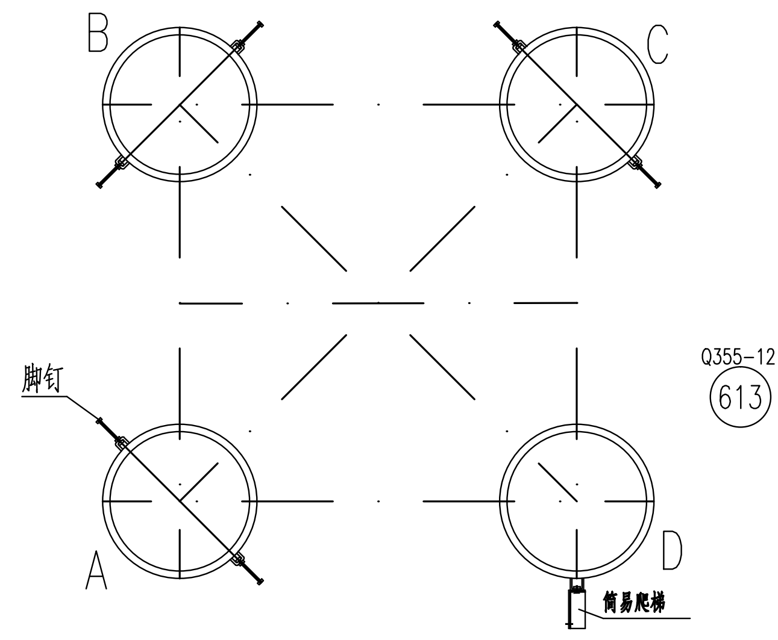

爬梯脚钉示意图

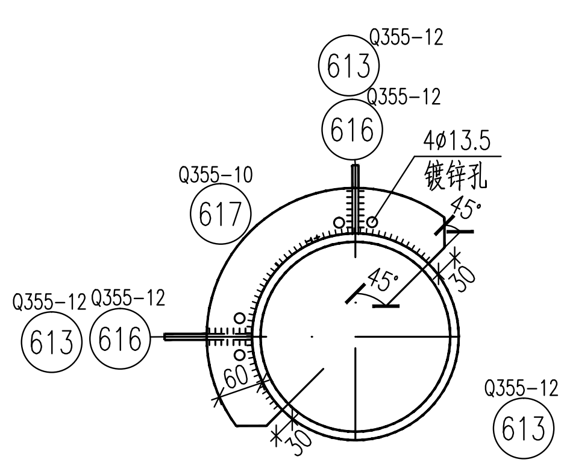

1--1
1:10

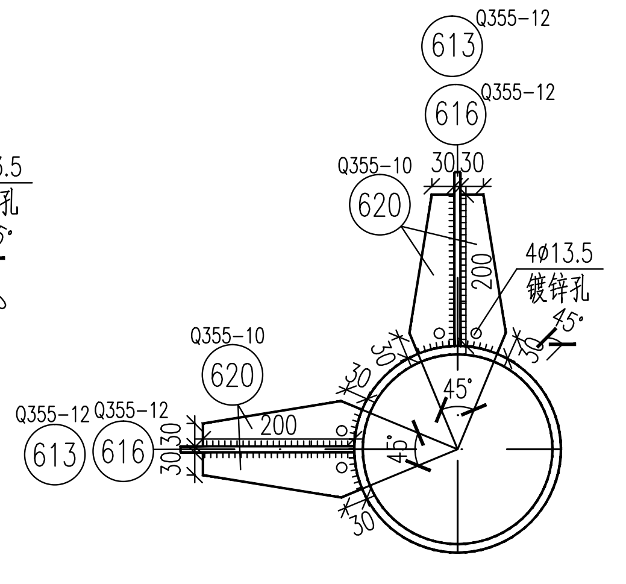

2--2
1:10

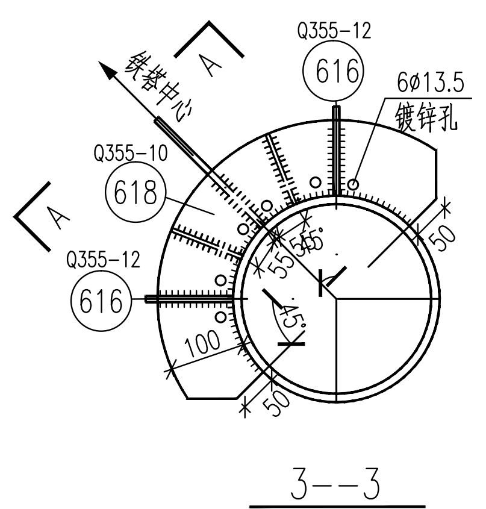

3--3
1:10

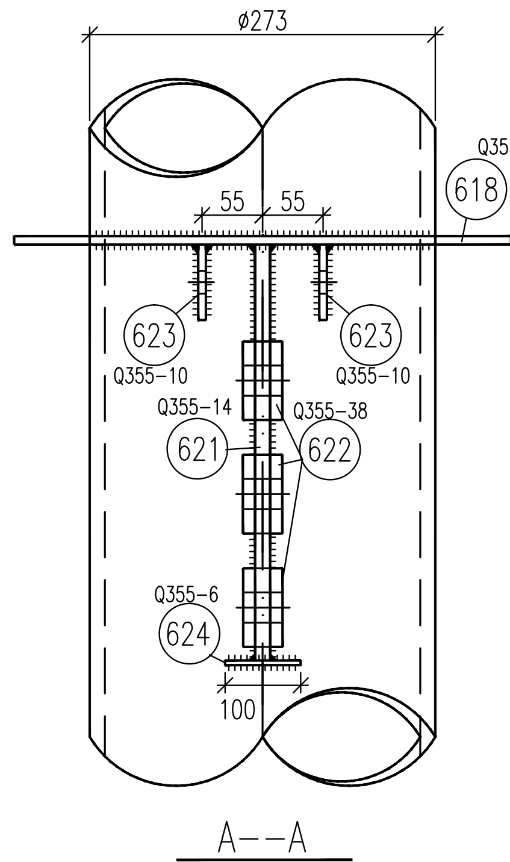

A--A
1:10

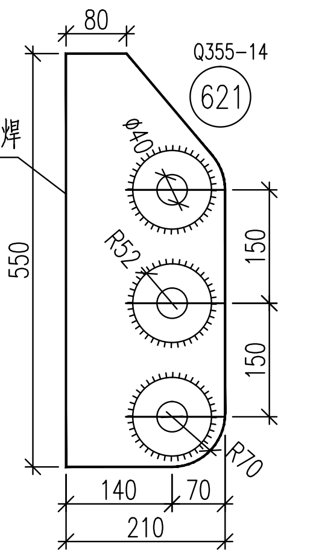

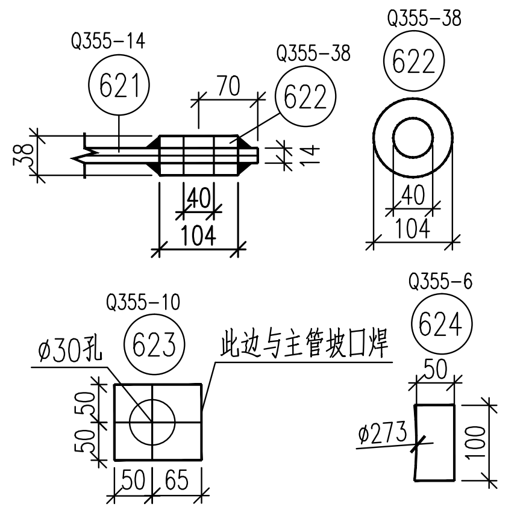

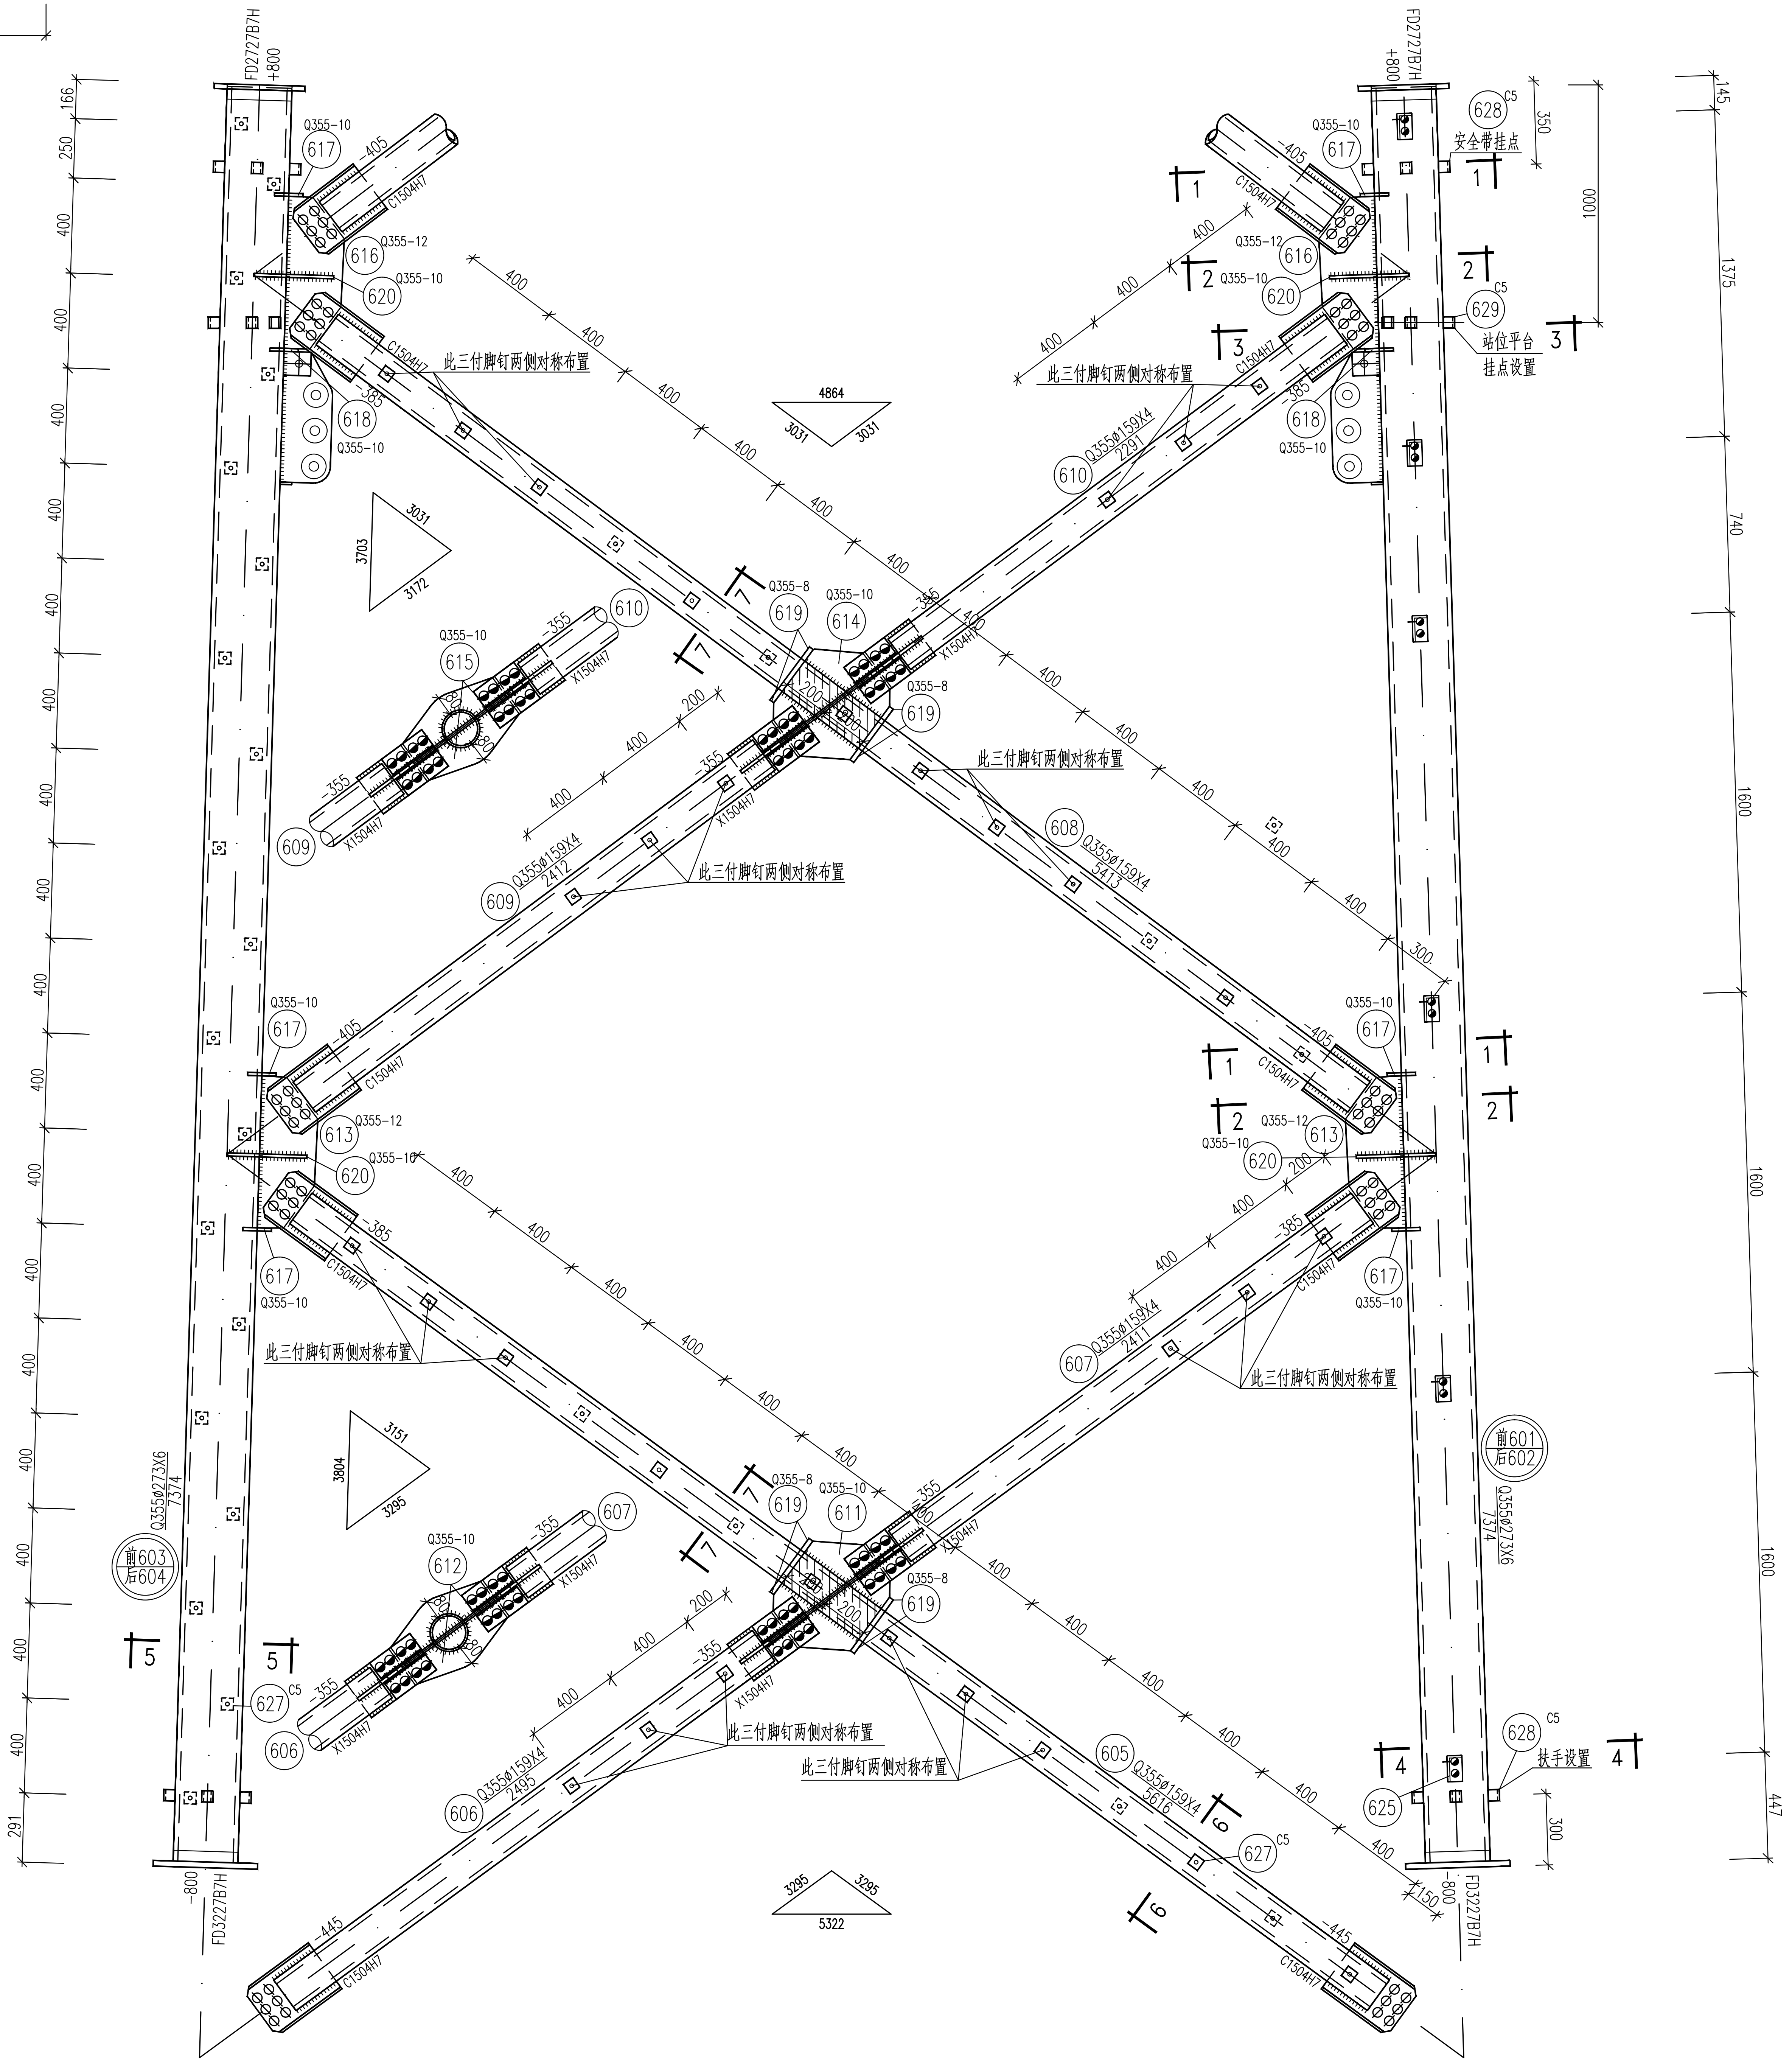

正面结构图

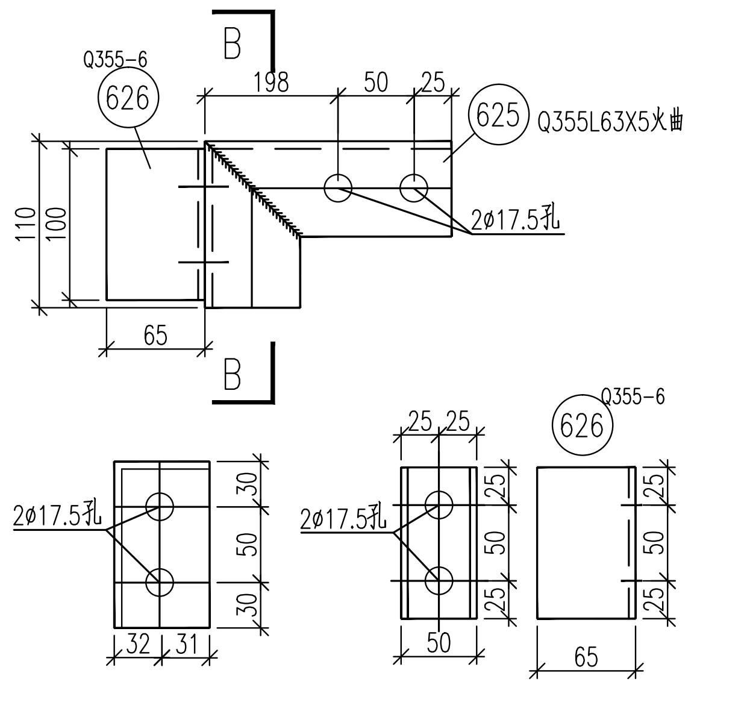

B--B
1:10

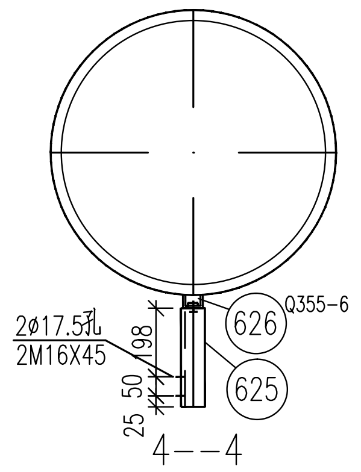

4--4
1:10

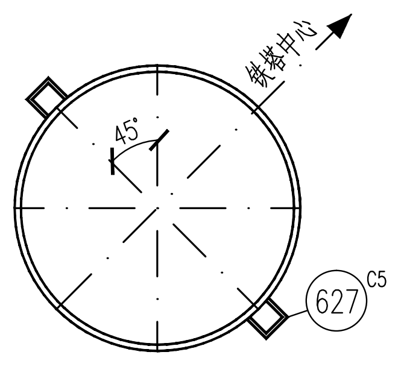

5--5
1:10

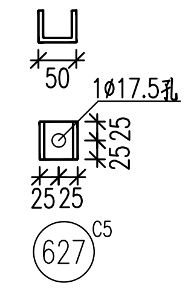

1:10

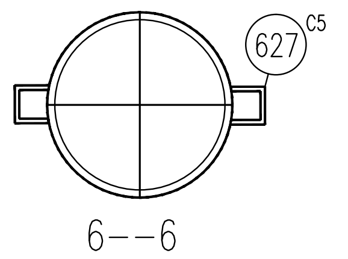

6--6
1:10

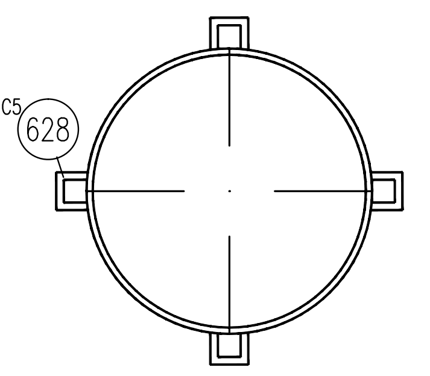

安全带挂点示意
扶手设置示意

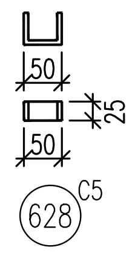

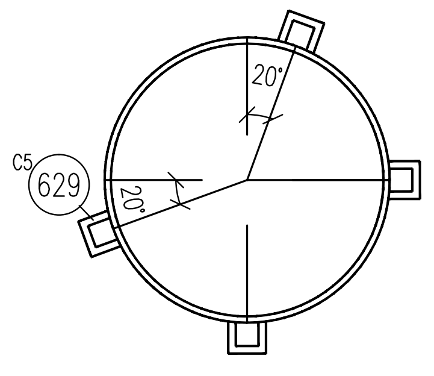

站位平台示意

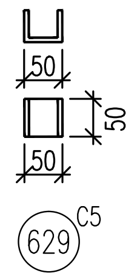

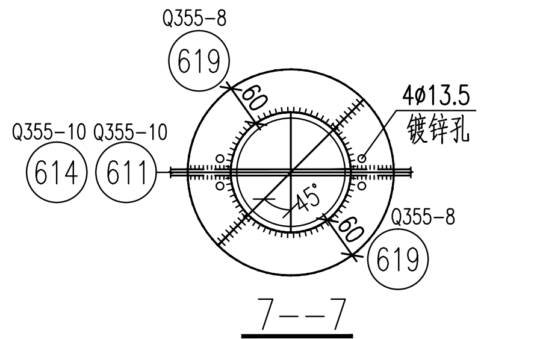

7--7
1:10

构 件 明 细 表

编号	规格	长度(mm)	数量	重量(kg) 一件	重量(kg) 小计	备注
601	Q355ø273X6	7374	1	291.33	291.3	带爬梯
602	Q355ø273X6	7374	1	291.33	291.3	带脚钉
603	Q355ø273X6	7374	1	291.33	291.3	带脚钉
604	Q355ø273X6	7374	1	291.33	291.3	带脚钉
605	Q355ø159X4	5616	4	85.87	343.5	带脚钉
606	Q355ø159X4	2495	4	38.15	152.6	带脚钉
607	Q355ø159X4	2411	4	36.86	147.4	带脚钉
608	Q355ø159X4	5413	4	82.76	331.0	带脚钉
609	Q355ø159X4	2412	4	36.88	147.5	带脚钉
610	Q355ø159X4	2291	4	35.03	140.1	带脚钉
611	Q355-10X440	517	4	17.86	71.4	
612	Q355-10X173	517	8	7.02	56.2	
613	Q355-12X261	704	8	17.31	138.5	
614	Q355-10X440	517	4	17.86	71.4	
615	Q355-10X173	517	8	7.02	56.2	
616	Q355-12X260	704	8	17.24	137.9	
617	Q355-10X60	575	12	2.71	32.5	
618	Q355-10X100	586	4	4.60	18.4	
619	Q355-8X60	378	32	1.42	45.4	
620	Q355-10X60	232	32	1.09	34.9	
621	Q355-14X210	550	4	12.69	50.8	
622	Q355-38X104	104	12	3.23	38.8	
623	Q355-10X100	115	8	0.90	7.2	
624	Q355-6X50	100	4	0.24	1.0	
625	Q355L63X5	383	6	1.85	11.1	火曲 电焊
626	-6X100	180	6	0.85	5.1	火曲
627	C5	50	309	0.27	83.4	槽钢
628	C5	25	32	0.14	4.5	槽钢
629	C5	50	16	0.27	4.3	槽钢
	FD2727B7H		4	12.2	48.8	
	FD3227B7H		4	21.9	87.6	
	C1504H7		32	9.61	307.5	
	X1504H7		16	13.1	209.6	
	T2105		1	11.5	11.5	
	T5530		1	28.8	28.8	
合计		3990.1 kg				

螺栓、脚钉、垫圈明细表

名称	级别	规格	符号	数量	重量(kg)	备注
螺栓	6.8级	M16X45	⊘	24	4.0	
		M16X55	⊘	256	47.3	
		M20X65	∅	192	67.8	
	8.8级	M20X95	○	80	38.7	法兰螺栓
脚钉	6.8级	M16X185	⊖	309	128.1	
			⊣			
垫圈	Q235		规格X个数			
合计		285.9 kg				

山东电力工程咨询院有限公司				浙江特高压交流环网工程线路 工程	施工图 设计阶段
批准	雷强	校核	马一丹	SZK31102A直线塔 ⑥ 身部结构图	
审核	高锡鹏				
		设计/勘测	潘胜光		
比例		日期	2026年 08月	图号 37-SA36901S-T0121-016	版本