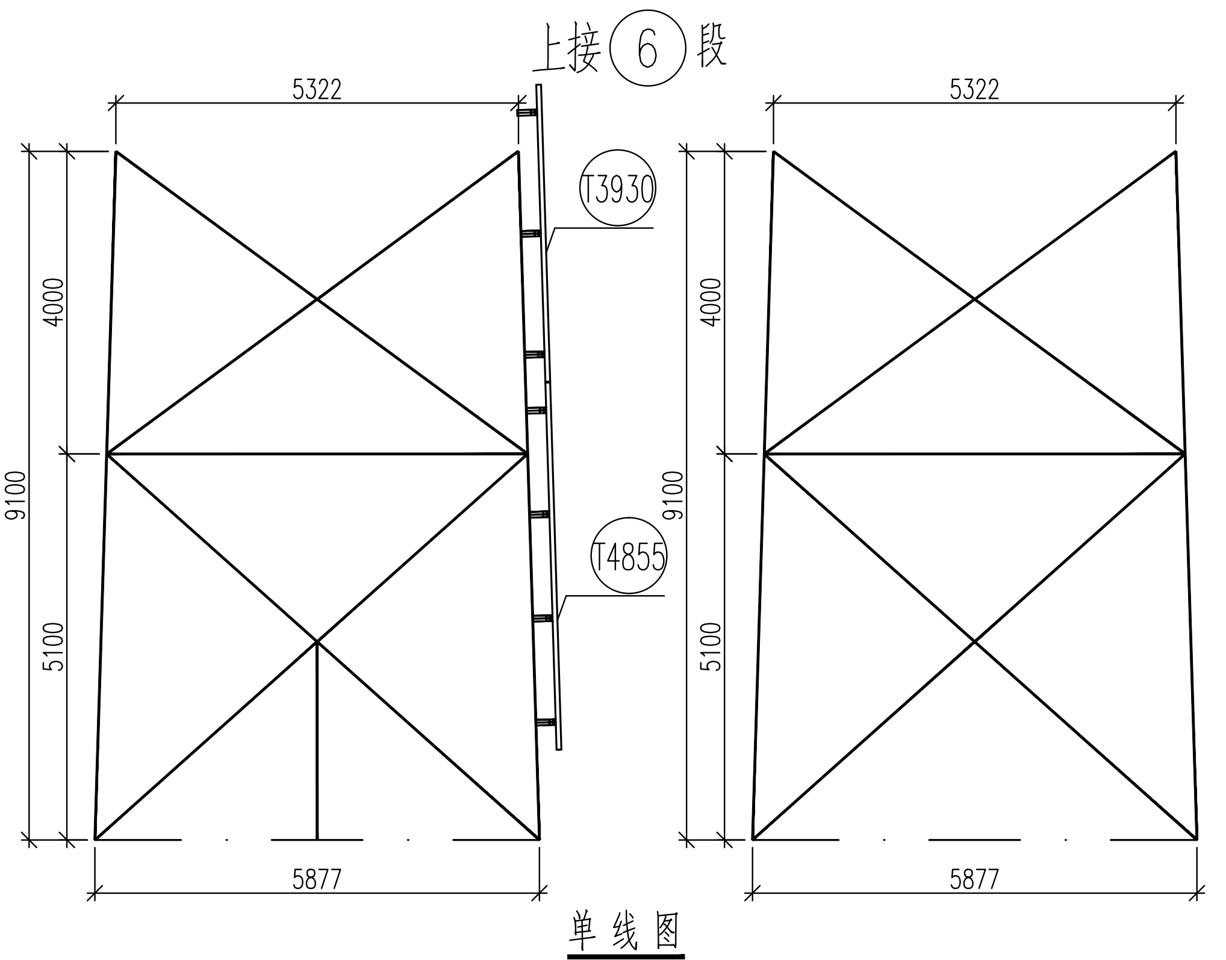
上接⑥段
5322
5322
T3930
T4855
⑦
9100
4000
5100
5877
5877

单线图
1:100

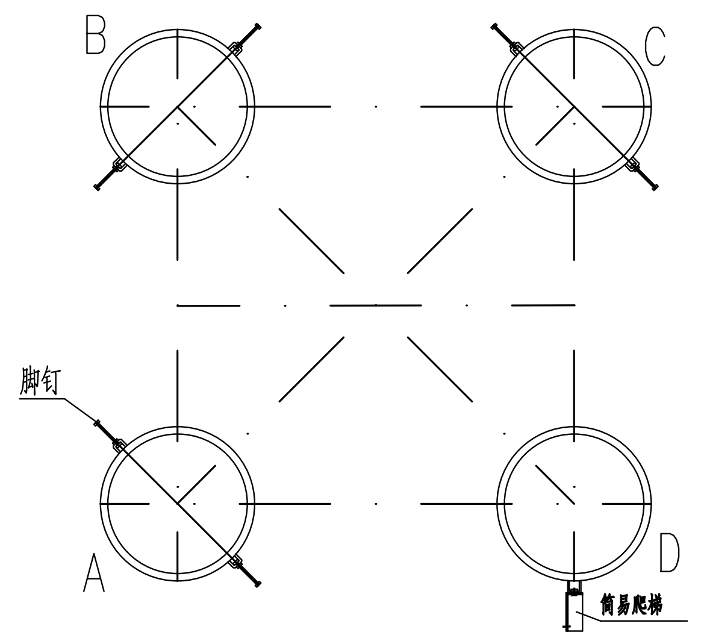
B
C
A
D
脚钉
爬梯脚钉

爬梯脚钉示意图

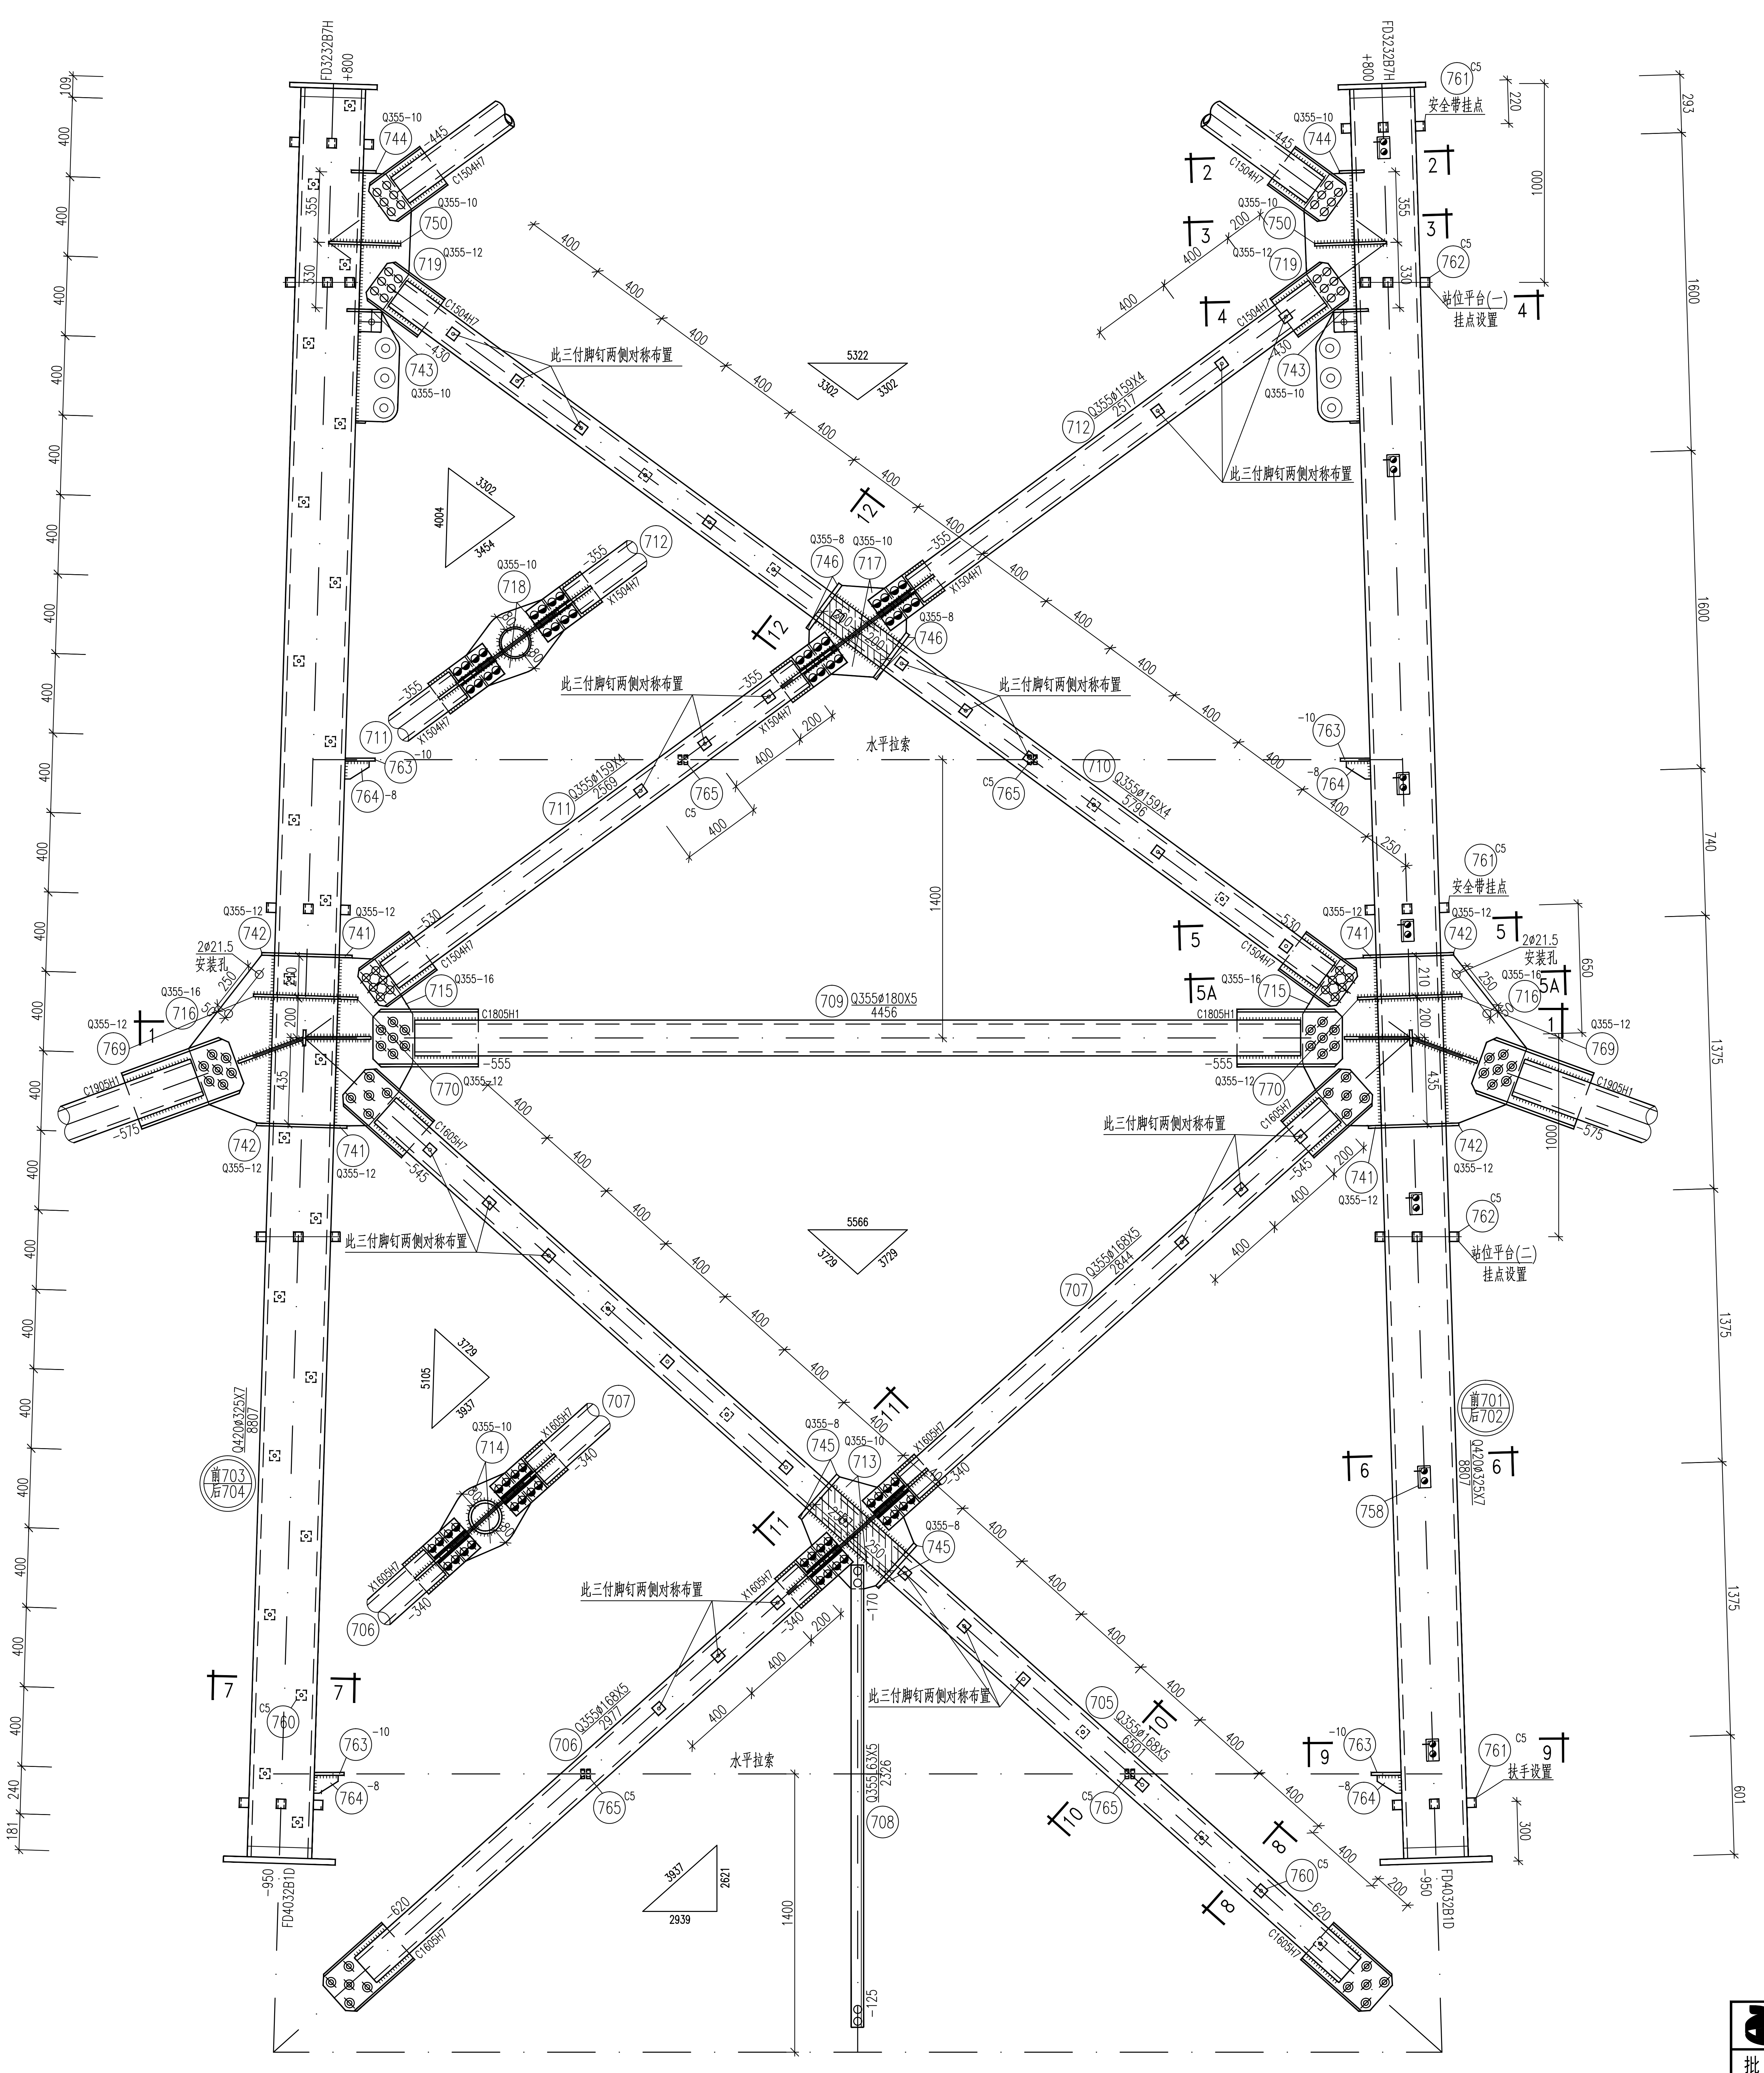
FD3232B7H
+800
Q355-10
744
750
719
743
Q355-12
C1504H7
此三付脚钉两侧对称布置
5322
3302
3302
4004
3302
3454
712
Q355ф159X4
718
711
717
746
Q355-8
710
Q355ф159X4
763
764
765
水平拉索
1400
761
安全带挂点
762
站位平台(一)
挂点设置
741
742
2ф21.5
安装孔
716
715
769
Q355-16
709
Q355ф180X5
4456
C1805H1
C1909H1
770
707
Q355ф168X5
5566
3729
3729
5105
3729
3937
714
713
745
706
705
708
Q355ф63X5
2226
Q420ф325X7
6807
简701
简702
简703
简704
758
760
站位平台(二)
扶手设置
FD4032B10
-950
2939
3937
2621
1600
1600
740
1375
1375
1375
601
283
1000
220
650
1000
300

正面结构图

山东电力工程咨询院有限公司				浙江特高压交流环网工程线路 **工程**	施工图	设计阶段
批　准	雷强	校　核	马一丹	SZK31102A直线塔 身部结构图(1/3) ⑦		
审　核	高锡鹏					
		设计/勘测	潘胜光			
比　例		日　期	2026年 08月	图　号 37-SA36901S-T0121-017	版本	