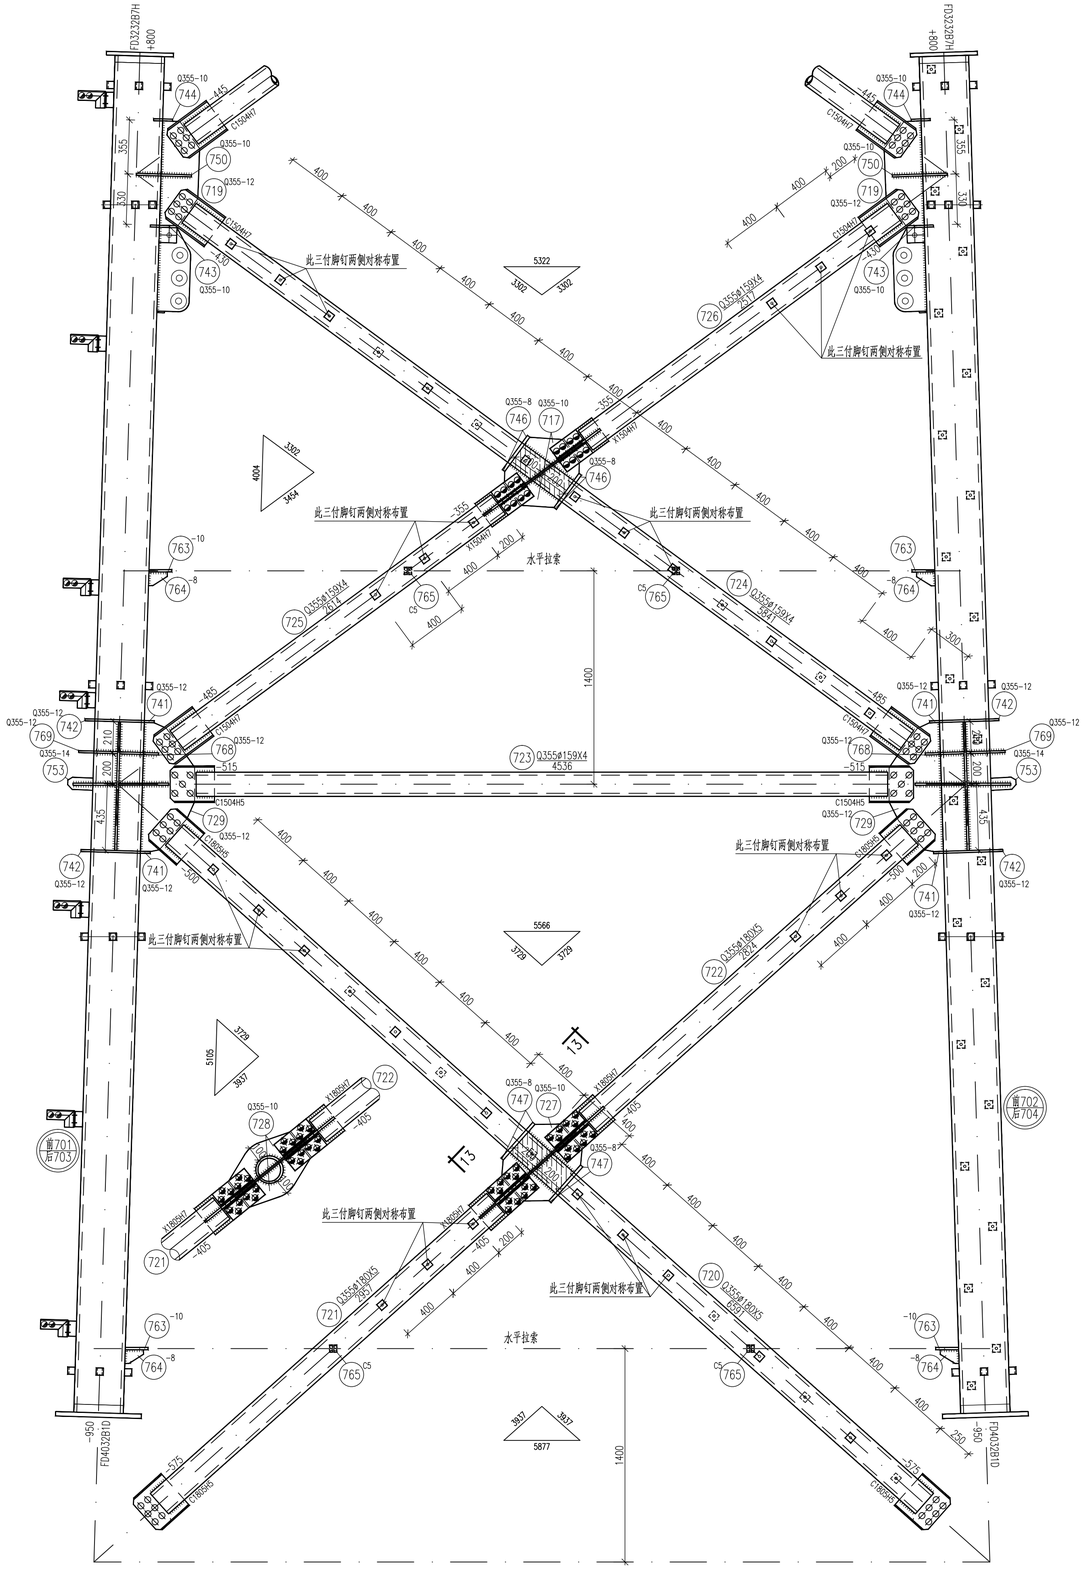
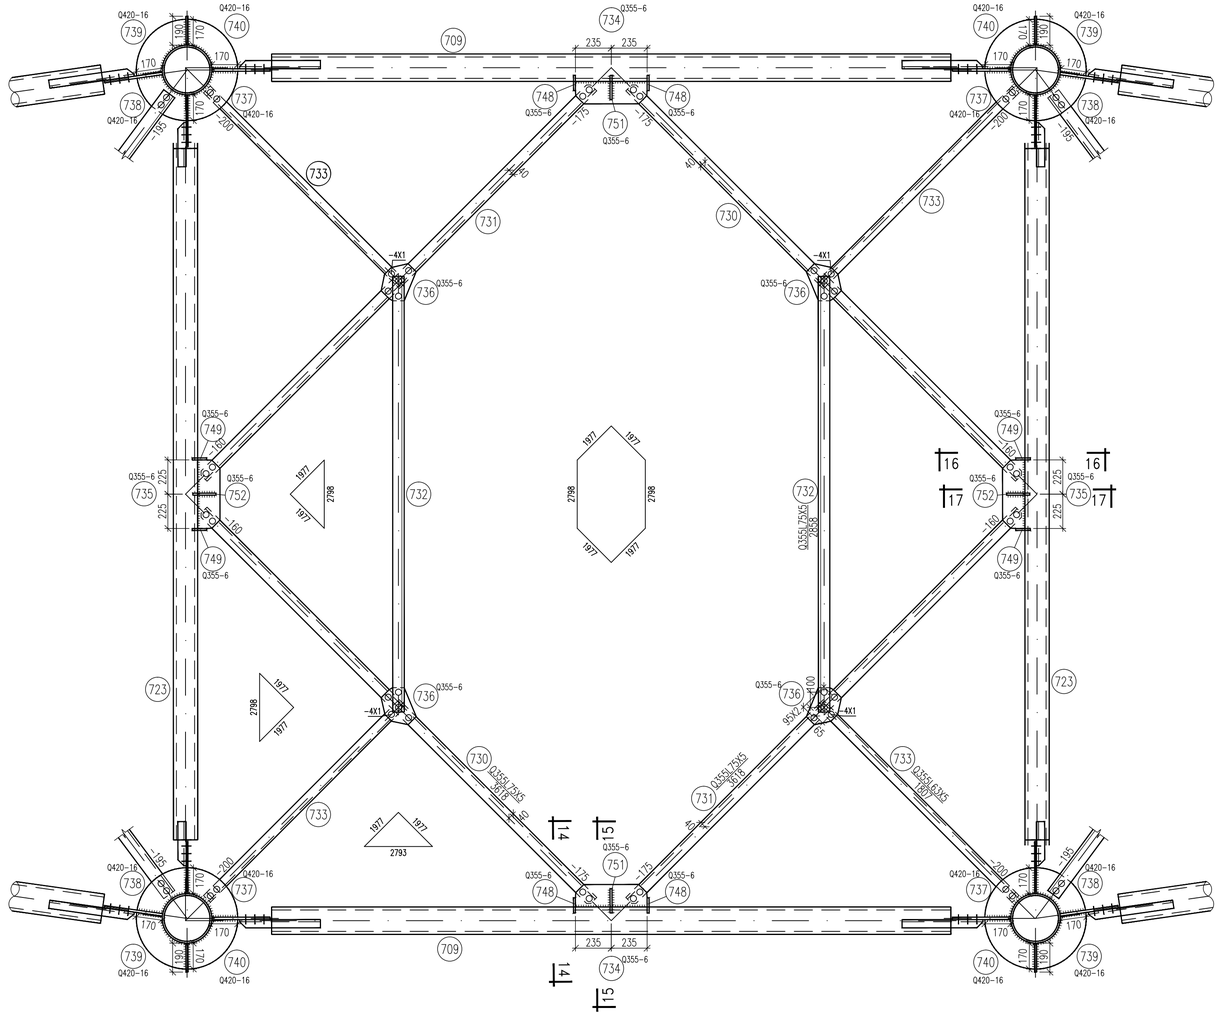



| | | | | | |
|---|---|---|---|---|---|
| 山东电力工程咨询院有限公司 | | | 浙江特高压交流环网工程线路 工程 | 施工图 | 设计阶段 |
| 批 准 | 曹强 | 校 核 | 刘一舟 | SZK31102A直线塔 身部结构图(2/3) | ⑦ |
| 审 核 | 高鹏鹏 | 设计/勘测 | 潘旭光 | | |
| 比 例 | | 日 期 | 2026年 08月 | 图 号 37-SA36901S-T0121-018 | 版本 |