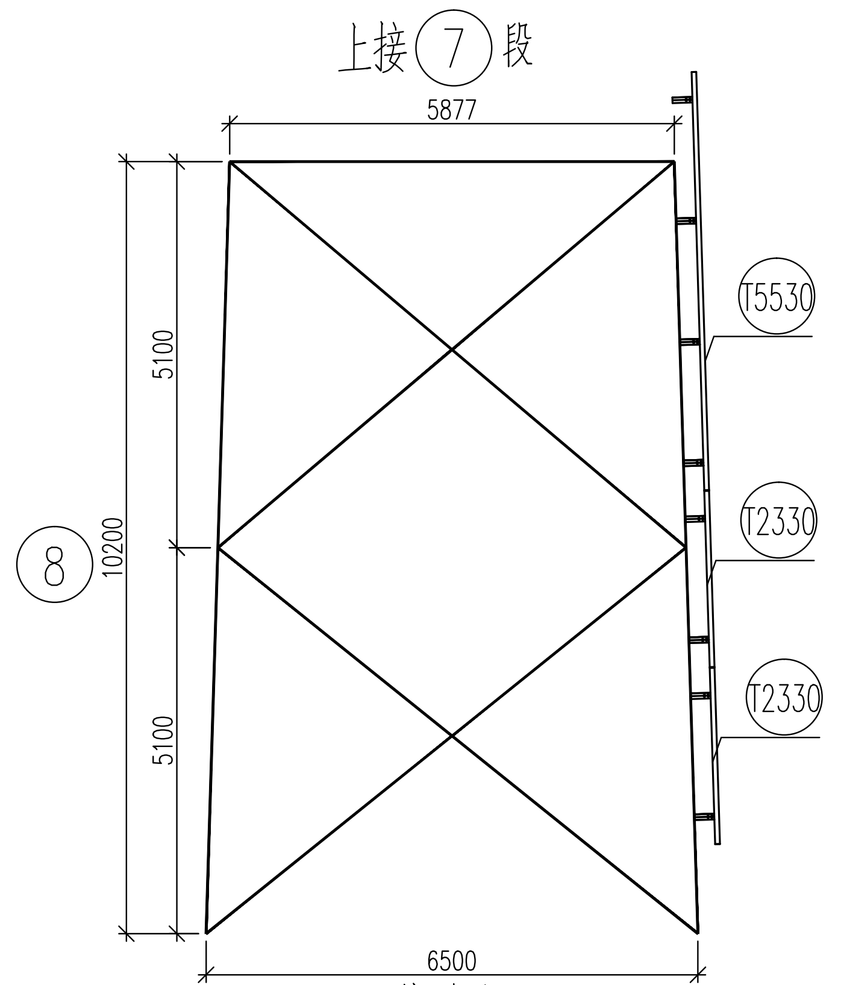
上接⑦段
5877
5100
10200
5100
⑧
T5530
T2330
T2330
6500

单线图
1:100

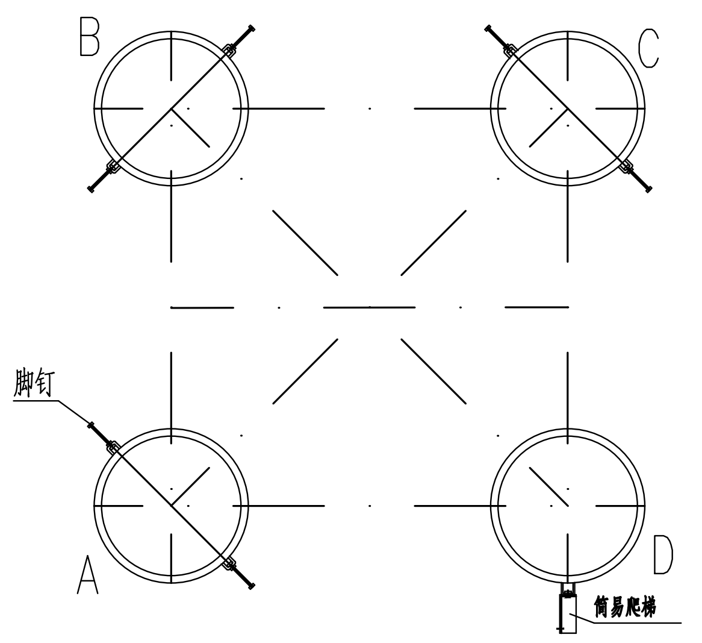
B
C
脚钉
A
D
爬梯脚钉

爬梯脚钉示意图

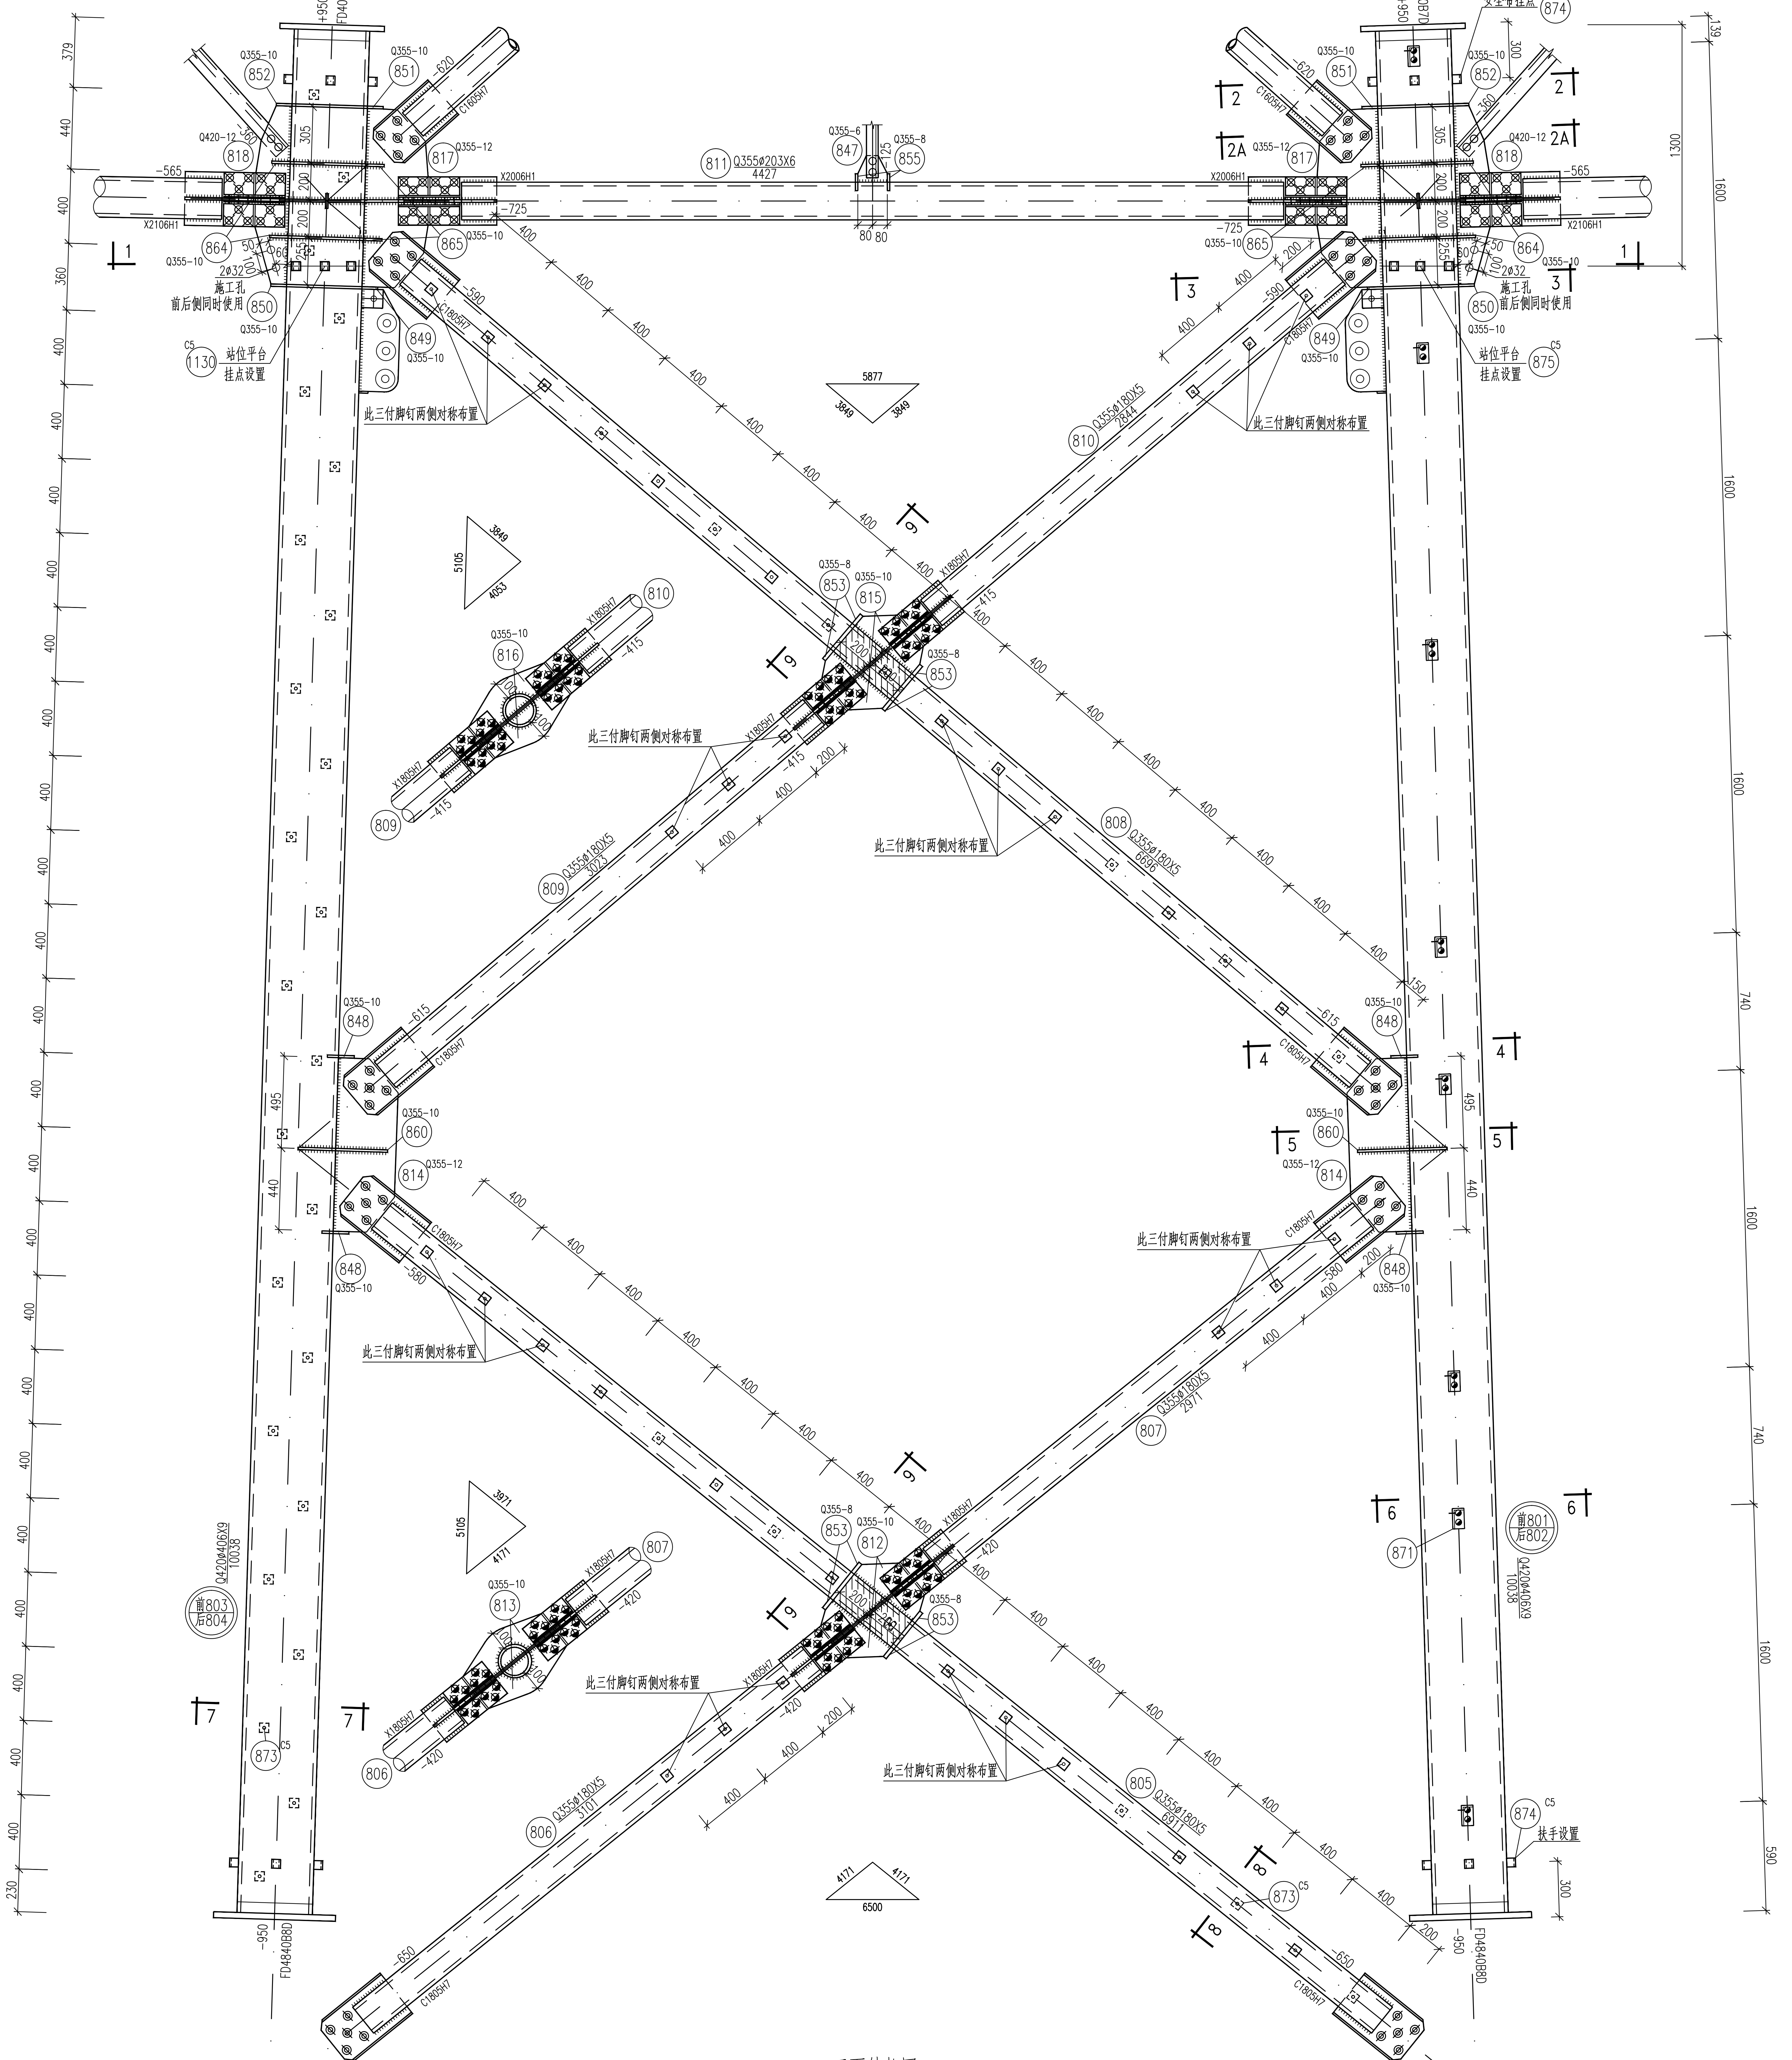
FD4040B7D
+950
安全带挂点
Q355-10
851
852
820
Q420-12
818
Q355-12
817
X2006H1
X2106H1
-565
-725
811
Q355Φ203X6
4427
Q355-6
847
Q355-8
855
864
865
2Φ32
施工孔
前后侧同时使用
850
849
1130
站位平台
挂点设置
874
875
810
Q355Φ180X5
此三付脚钉两侧对称布置
809
808
853
815
816
848
860
814
807
806
805
812
813
873
871
扶手设置
前803
后804
前801
后802
Q420Φ406X9
10038
FD4840B8D
-950
-650
5877
5105
3849
4053
3911
4171
6500
1600
740
590
1300
400

正面结构图

| **山东电力工程咨询院有限公司** | | | | 浙江特高压交流环网工程线路 | 工程 | 施工图 | 设计阶段 |
|---|---|---|---|---|---|---|---|
| 批　准 | | 校　核 | | SZK31102A直线塔<br>身部结构图(1/3) ⑧ | | | |
| 审　核 | 高锡鹏 | | | | | | |
| | | 设计/勘测 | | | | | |
| 比　例 | | 日　期 | 2026年 08月 | 图　号 | 37-SA36901S-T0121-020 | 版本 | |