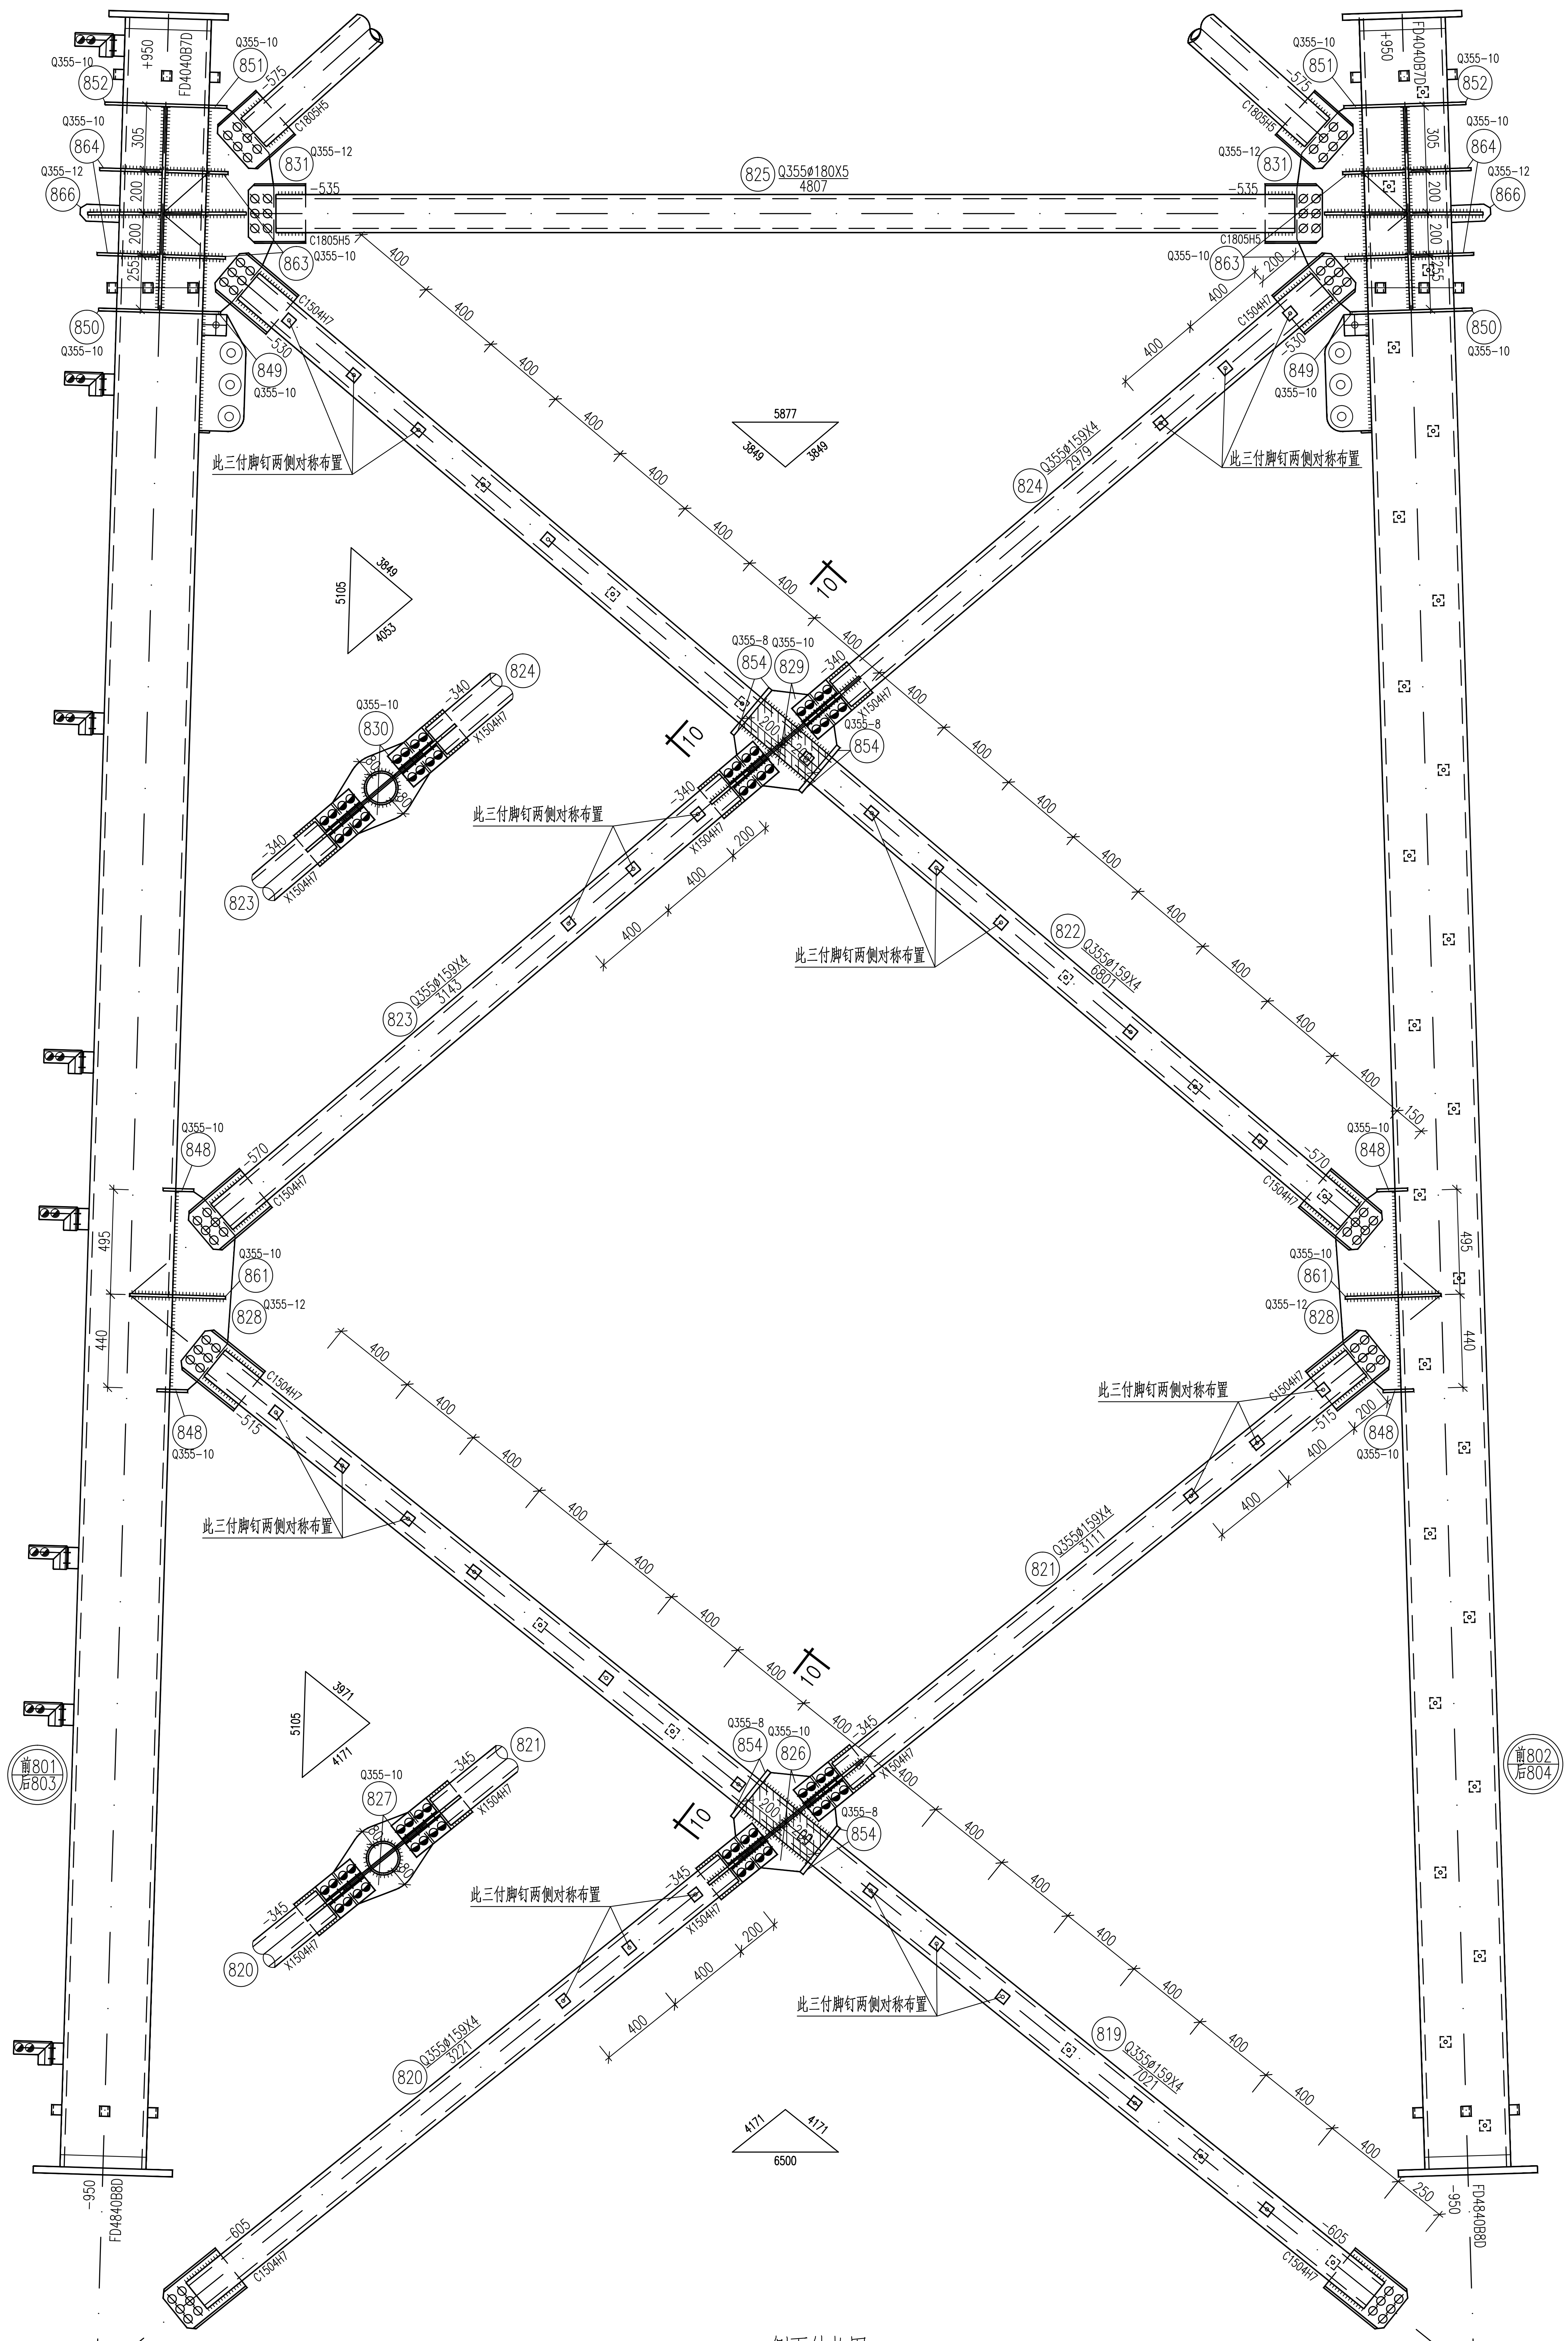
FD4040B7D
+950
Q355-10
851
852
C180S5
-575
305
200
200
255
864
866
Q355-12
831
-535
825
Q355φ180X5
4807
C180SH5
863
850
849
Q355-10
C150H7
-530
此三付脚钉两侧对称布置
5877
3849
5105
4053
824
Q355φ159X4
6079
10
854
829
Q355-8
830
-340
X150H7
823
Q355φ159X4
3142
822
Q355φ159X4
6081
400
200
848
-570
861
828
495
440
-515
821
Q355φ159X4
3117
3971
4171
827
826
-345
820
Q355φ159X4
3121
819
Q355φ159X4
6073
6500
-605
-250
-950
FD4840B8D
前801
后803
前802
后804

侧面结构图

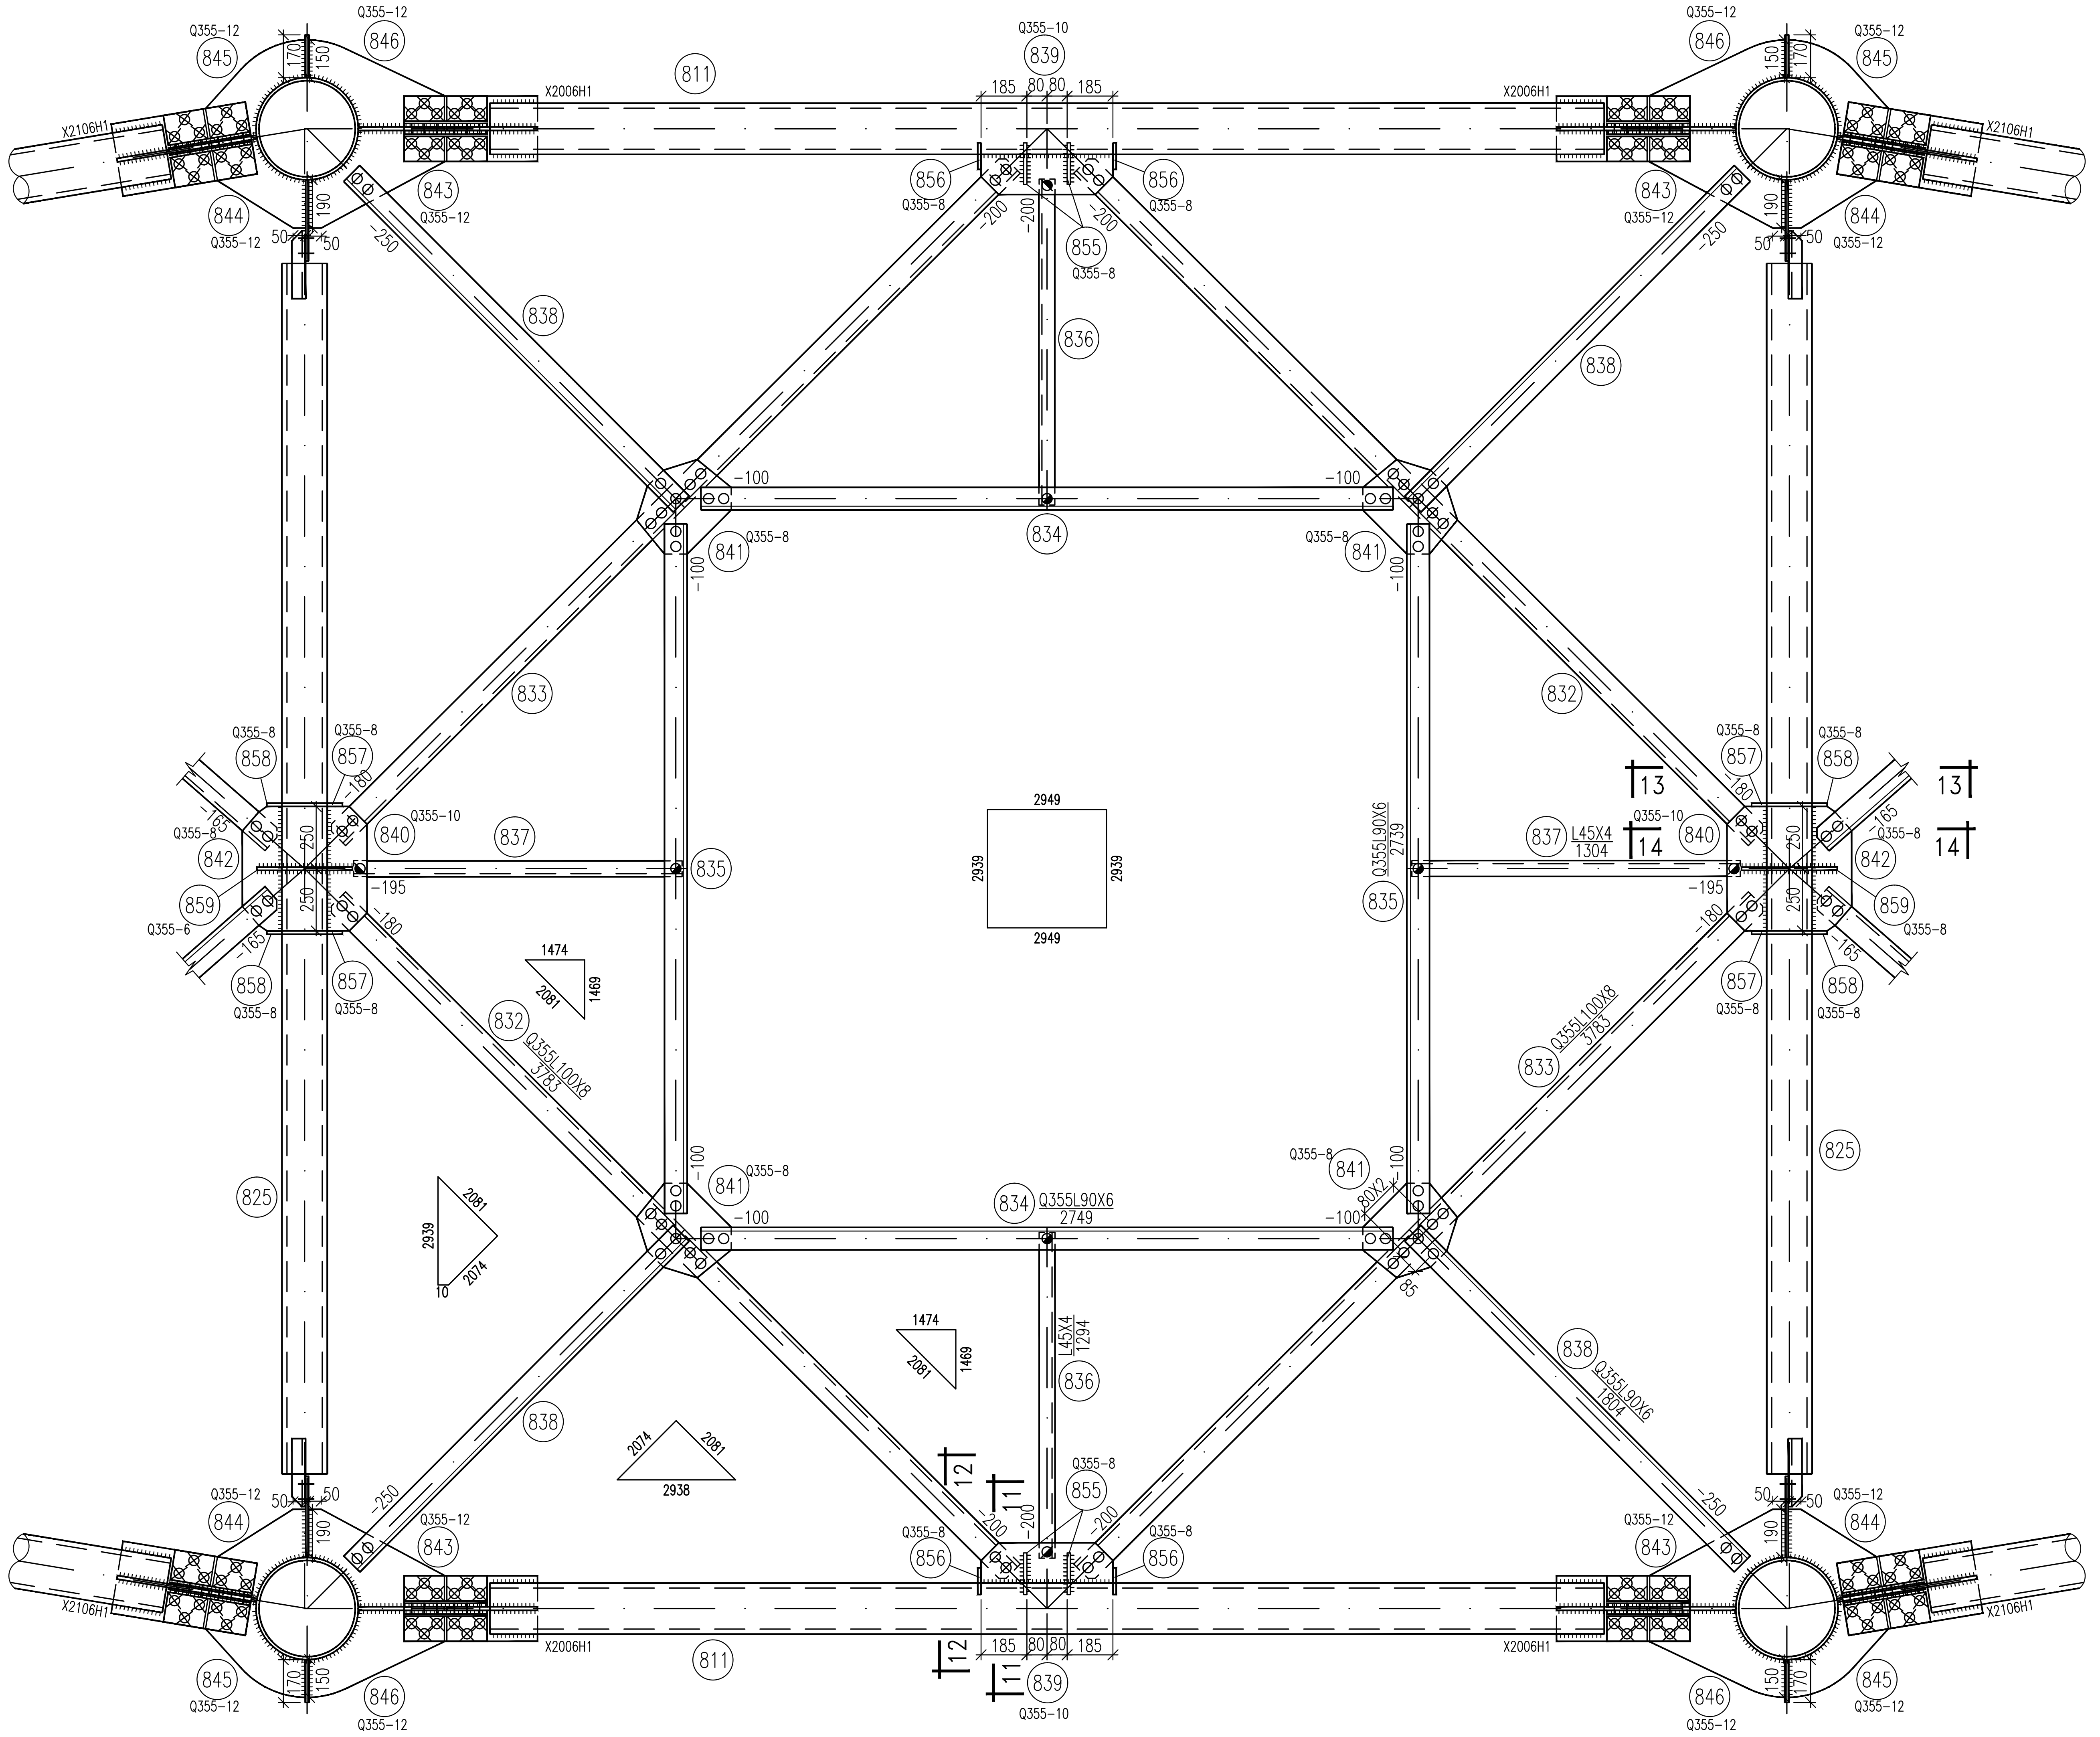
845
846
Q355-12
839
Q355-10
185
80
80
811
X2006H1
X2106H1
843
844
856
855
Q355-8
836
838
834
-100
841
833
832
857
858
842
840
837
835
859
Q355-6
L45X4
1304
Q355L90X6
2739
2949
2939
1474
1469
2081
Q355L100X8
2741
13
14
Q355L90X6
2749
12
11
2074
2938
825
1294
Q355L90X6
1804
-250
-200
-195
-180
-165
190
170
150
50

1－1

山东电力工程咨询院有限公司				浙江特高压交流环网工程线路 工程	施工图	设计阶段
批　准		校　核		SZK31102A直线塔 身部结构图(2/3) ⑧		
审　核	高锡鹏					
		设计/勘测				
比　例		日　期	2026年 08月	图　号	37-SA36901S-T0121-021	版本