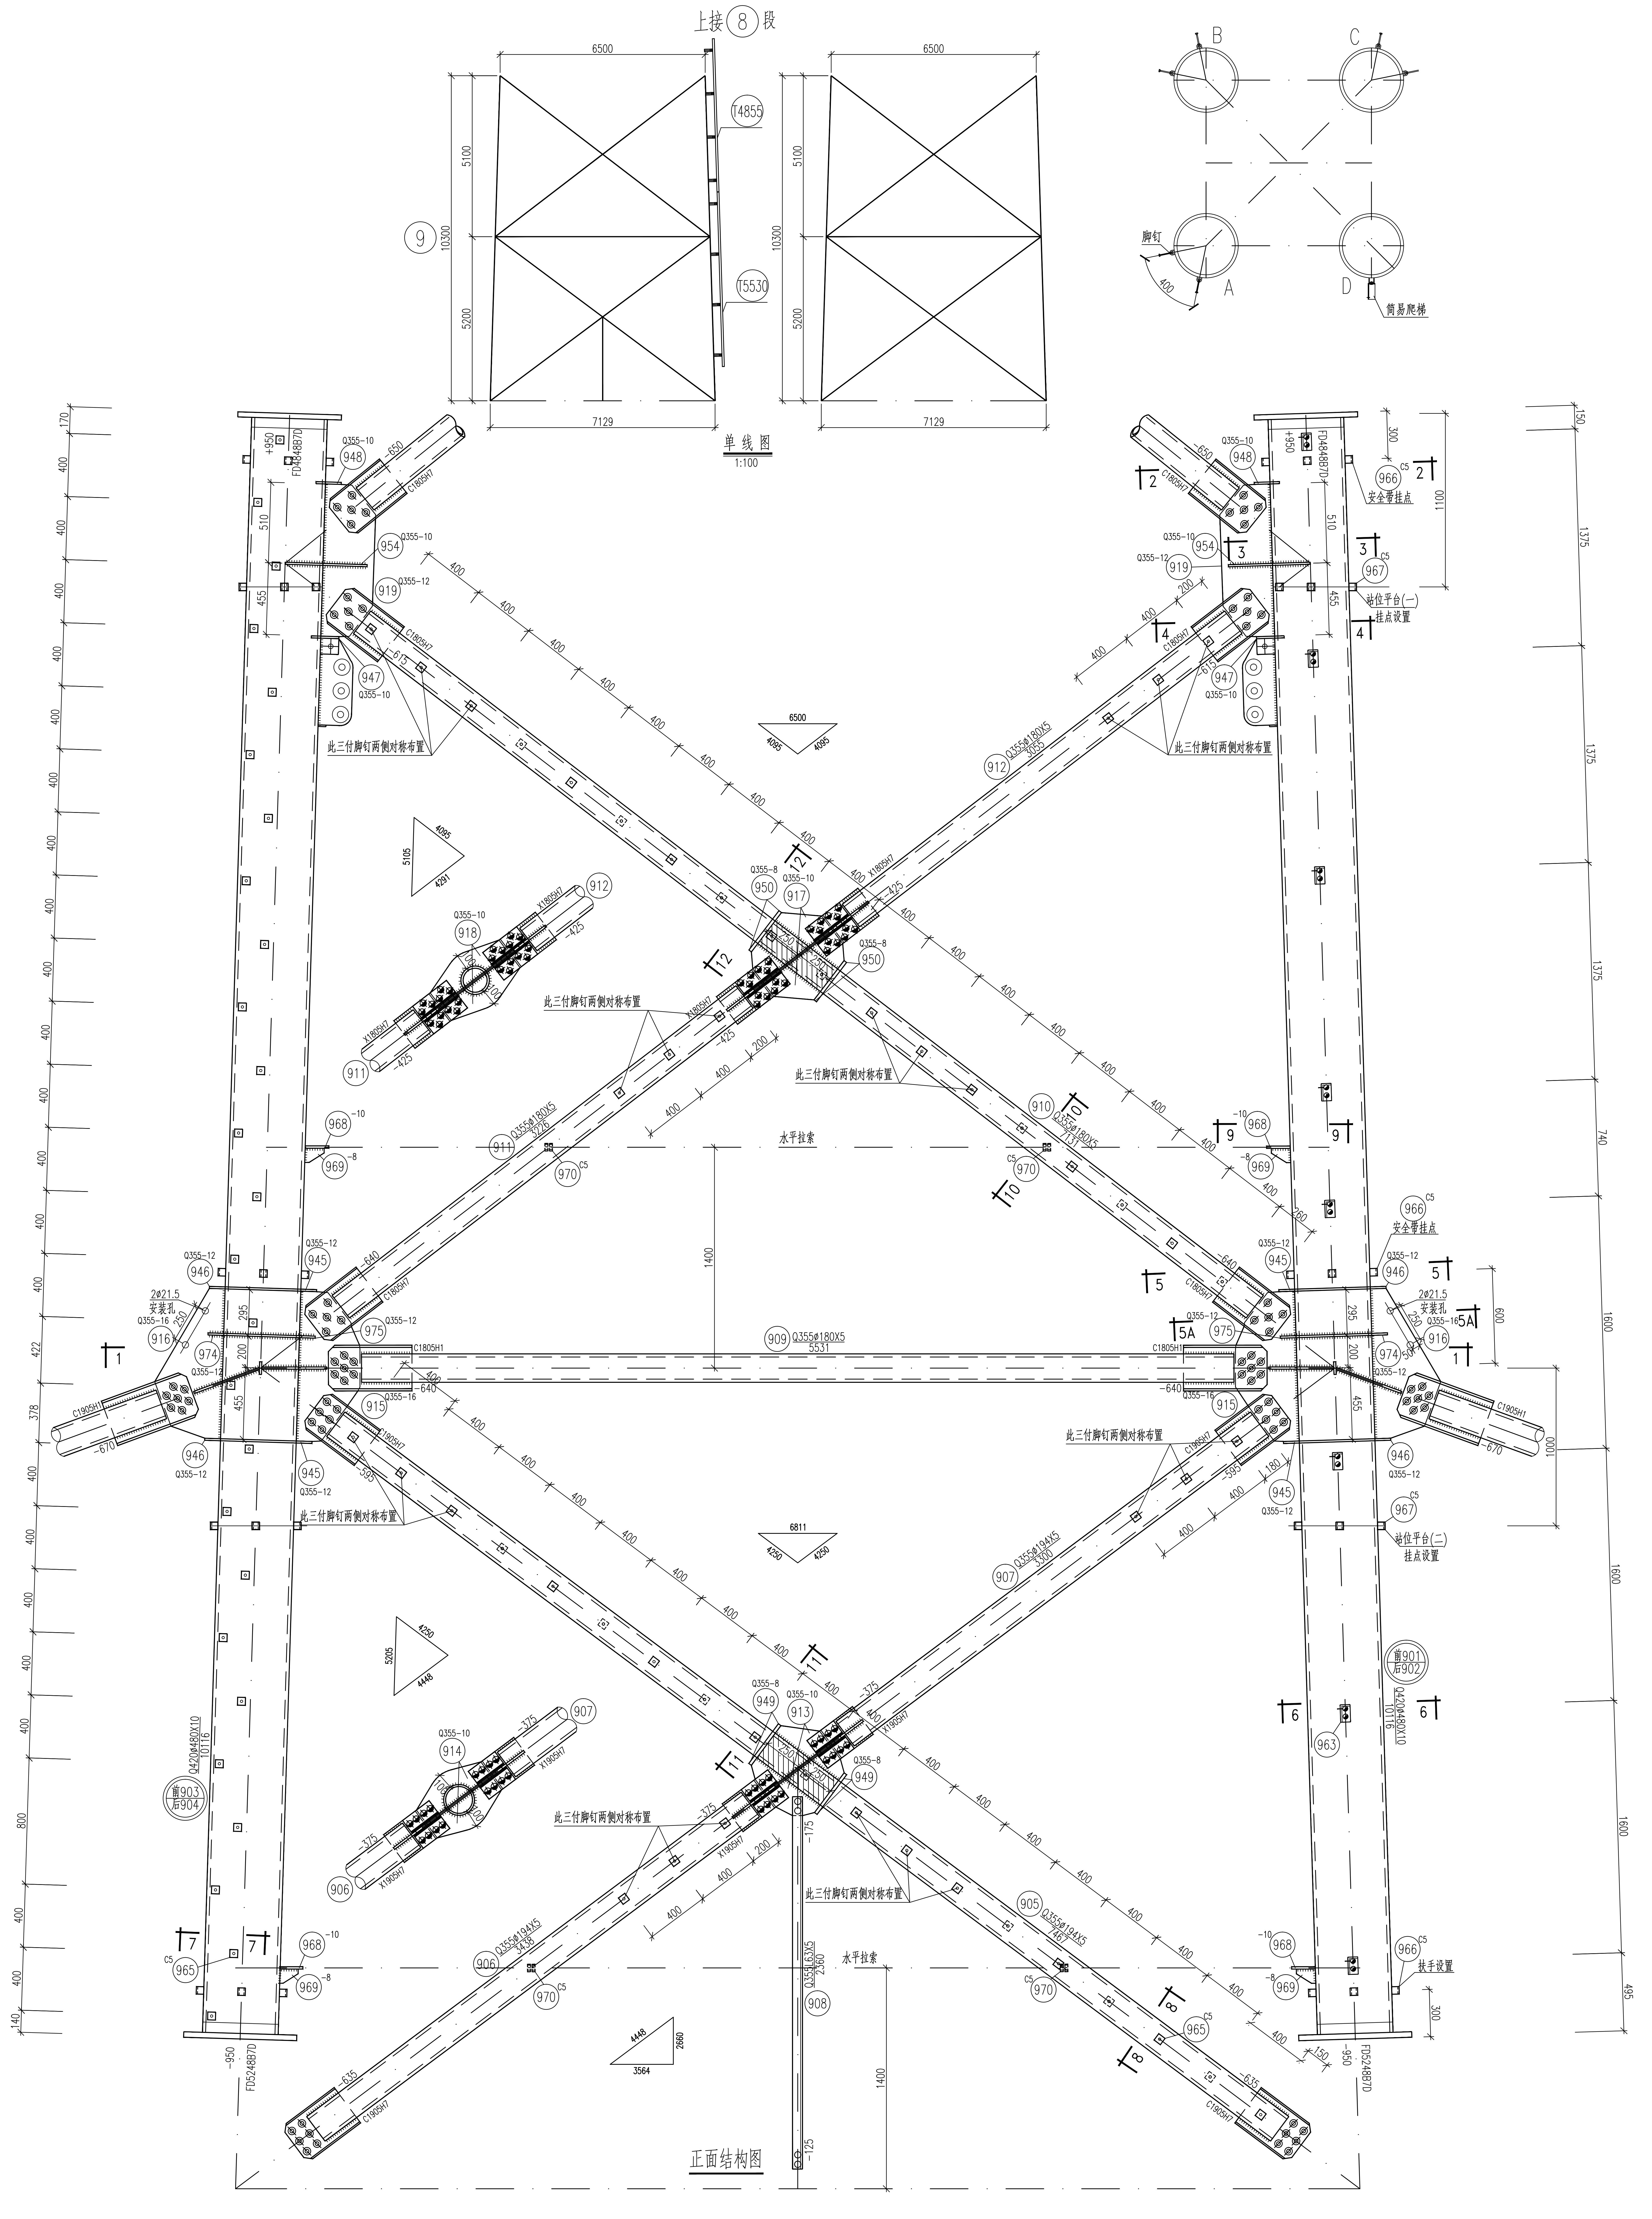
上接⑧段
6500
5100
10300
5200
7129
T4855
T5530
⑨
单线图
1:100
B
C
A
D
脚钉
简易爬梯
400
正面结构图
此三付脚钉两侧对称布置
水平拉索
安全带挂点
站位平台(一)挂点设置
站位平台(二)挂点设置
扶手设置
安装孔
2Ø21.5
Q355Ø180X5
Q355Ø194X5
Q420Ø480X10
Q355L63X5
FD4848B70
FD5248B70
C1805H7
C1905H7
X1805H7
X1905H7
C1805H1
C1905H1
1400
1375
1600
740
495
6811
4250
4095
5105
5205
4291
4448
3564
2860

山东电力工程咨询院有限公司		浙江特高压交流环网工程线路	工程	施工图	设计阶段
批　准	雷张	校　核	马一丹	SZK31102A直线塔 身部结构图(1/3) ⑨	
审　核	高锡鹏				
		设计/勘测	潘继光		
比　例		日　期	2026年 08月	图　号 37-SA36901S-T0121-023	版本