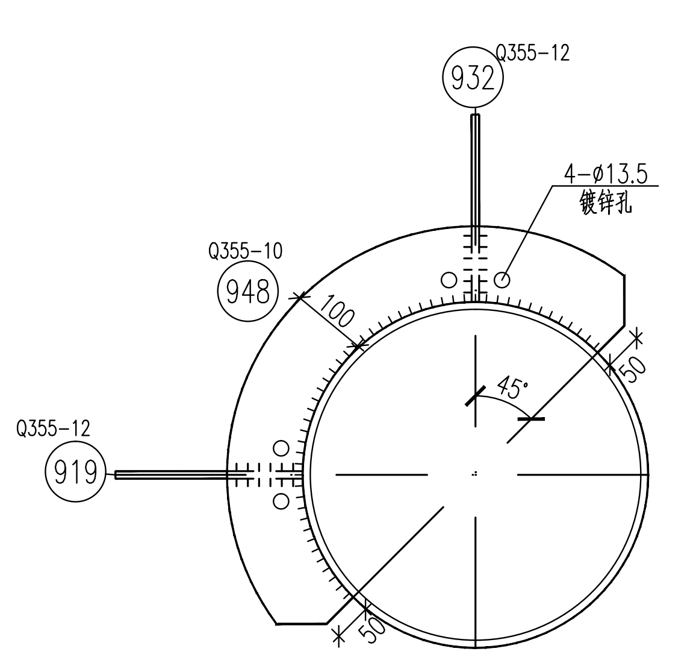
932
Q355-12
4-ø13.5
镀锌孔
948
Q355-10
919
Q355-12
45°
100
50

2--2
1:10

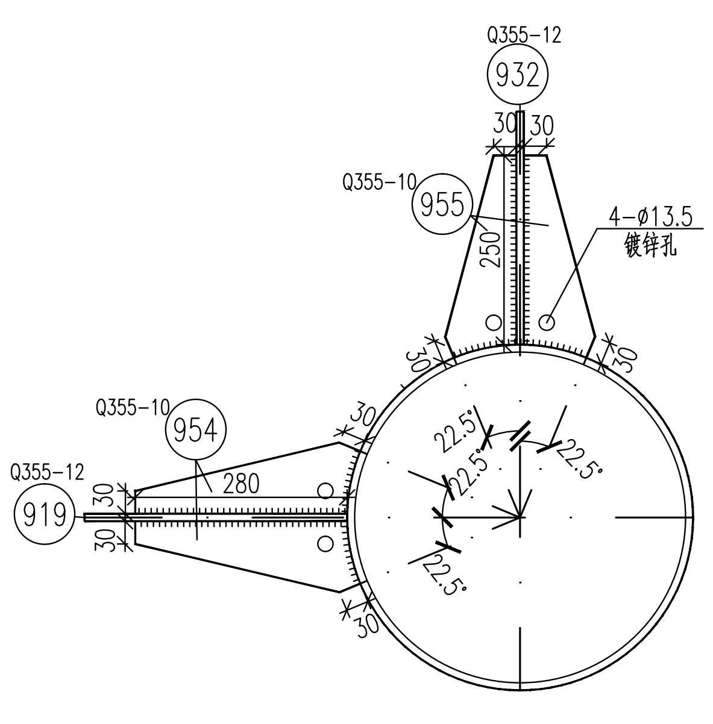
932
Q355-12
955
Q355-10
4-ø13.5
镀锌孔
954
Q355-10
919
Q355-12
280
22.5°

3--3
1:10

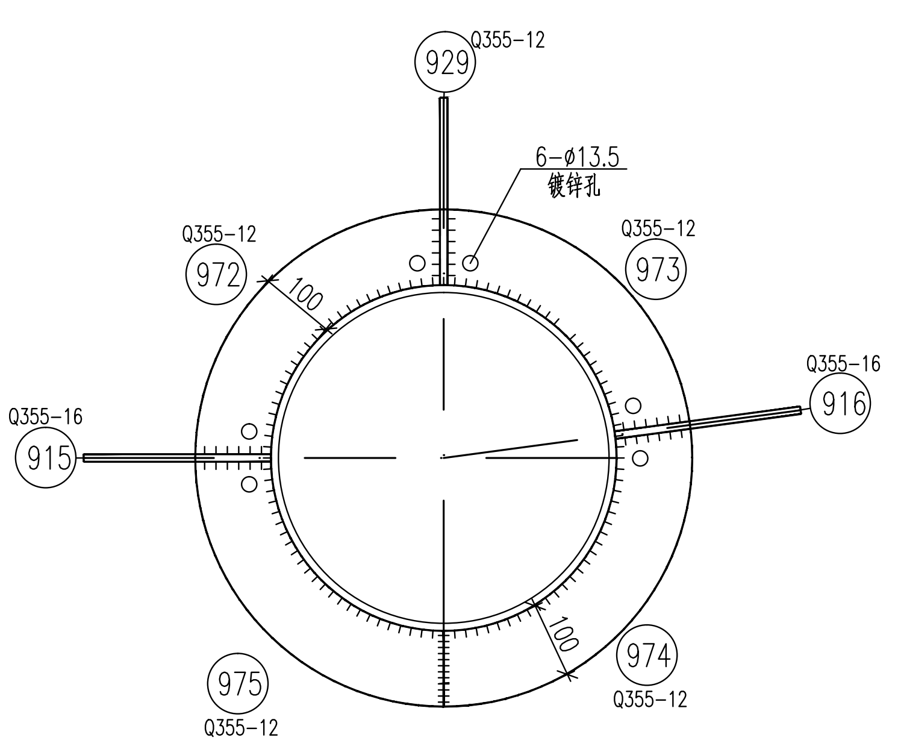
929
Q355-12
6-ø13.5
镀锌孔
972
973
916
Q355-16
915
Q355-16
975
974
100

5A--5A
1:10

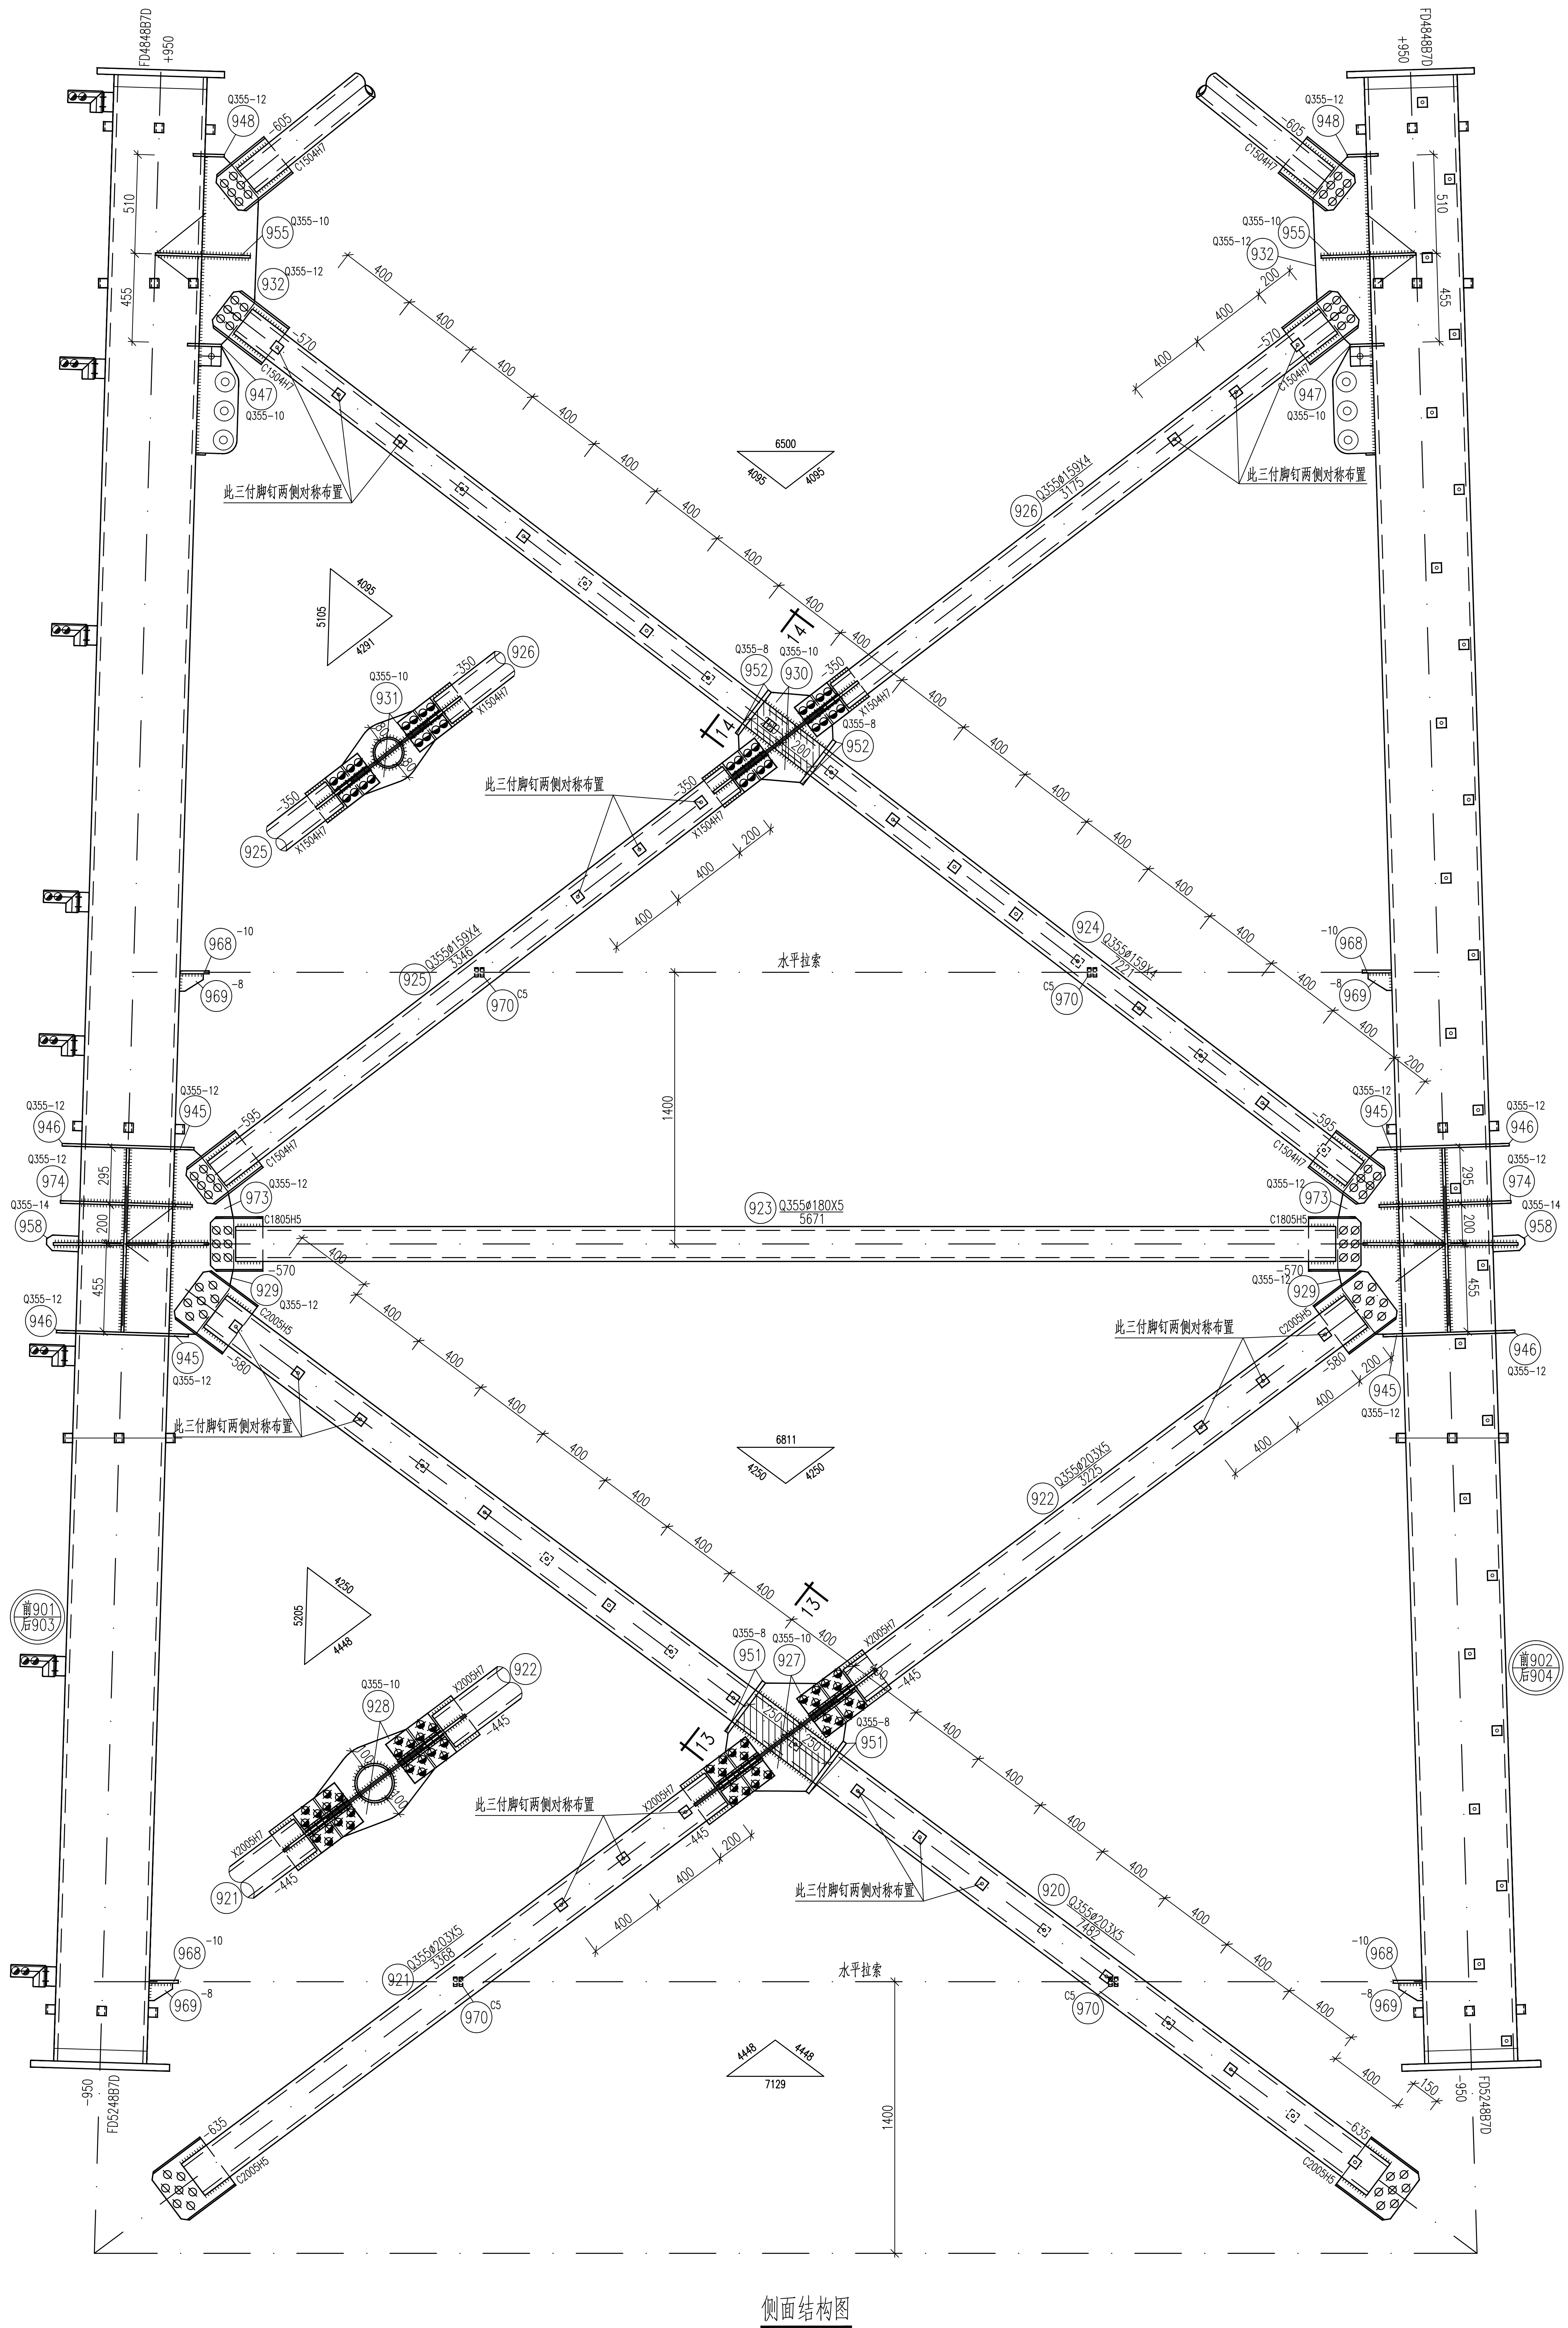
FD4848B7D
+950
FD5248B7D
-950
此三付脚钉两侧对称布置
水平拉索
923 Q355ø180X5 5671
924 Q355ø159X4
925 Q355ø159X4
926 Q355ø159X4
920 Q355ø203X5
921 Q355ø203X5
922 Q355ø203X5
6500
6811
7129
1400
5105
5205
T4
T3
圆901 后903
圆902 后904

侧面结构图

构件明细表

编号	规格	长度 (mm)	数量	重量(kg) 一件	重量(kg) 小计	备注
901	Q420ø480X10	10116	1	1172.54	1172.5	带爬梯
902	Q420ø480X10	10116	1	1172.54	1172.5	带脚钉
903	Q420ø480X10	10116	1	1172.54	1172.5	带脚钉
904	Q420ø480X10	10116	1	1172.54	1172.5	带脚钉
905	Q355ø194X5	7467	2	174.02	348.0	带脚钉
906	Q355ø194X5	3438	2	80.12	160.2	带脚钉
907	Q355ø194X5	3300	2	76.91	153.8	带脚钉
908	Q355L63X5	2360	2	11.38	22.8	
909	Q355ø180X5	5531	2	119.35	238.7	
910	Q355ø180X5	7131	2	153.88	307.8	带脚钉
911	Q355ø180X5	3226	2	69.61	139.2	带脚钉
912	Q355ø180X5	3055	2	65.92	131.8	带脚钉
913	Q355-10X550	561	2	24.22	48.4	
914	Q355-10X211	561	4	9.29	37.2	
915	Q355-16X423	1045	4	55.52	222.1	
916	Q355-16X469	1045	4	61.56	246.2	
917	Q355-10X550	605	2	26.12	52.2	
918	Q355-10X203	605	4	9.64	38.6	
919	Q355-12X354	1062	4	35.41	141.6	
920	Q355ø203X5	7482	2	182.67	365.3	带脚钉
921	Q355ø203X5	3368	2	82.23	164.5	带脚钉
922	Q355ø203X5	3225	2	78.74	157.5	带脚钉
923	Q355ø180X5	5671	2	122.37	244.7	
924	Q355ø159X4	7221	2	110.41	220.8	带脚钉
925	Q355ø159X4	3346	2	51.16	102.3	带脚钉
926	Q355ø159X4	3175	2	48.55	97.1	带脚钉
927	Q355-10X550	649	2	28.02	56.0	
928	Q355-10X215	649	4	10.95	43.8	
929	Q355-12X353	1045	4	34.75	139.0	
930	Q355-10X440	506	2	17.48	35.0	
931	Q355-10X173	506	4	6.87	27.5	
932	Q355-12X313	1062	4	31.31	125.2	
933	Q355L80X6	4484	2	33.08	66.2	切角
934	Q355L80X6	4484	2	33.08	66.2	切角
935	Q355L63X5	3481	2	16.79	33.6	
936	L45X4	1548	2	4.24	8.5	
937	Q355L63X5	2167	4	10.45	41.8	
938	Q355-8X167	528	2	5.54	11.1	
939	Q355-8X167	528	2	5.54	11.1	
940	Q355-6X232	261	4	2.85	11.4	
941	Q420-16X180	570	4	12.89	51.6	
942	Q420-16X180	548	4	12.39	49.6	
943	Q420-16X180	592	4	13.38	53.5	
944	Q420-16X180	570	4	12.89	51.6	
945	Q355-12X100	1002	8	9.44	75.5	
946	Q355-12X100	1002	8	9.44	75.5	
947	Q355-10X115	1029	4	9.29	37.2	
948	Q355-10X100	1002	4	7.87	31.5	
949	Q355-8X60	439	8	1.65	13.2	
950	Q355-8X60	415	8	1.56	12.5	
951	Q355-8X60	454	8	1.71	13.7	
952	Q355-8X60	378	8	1.42	11.4	
953	Q355-6X60	207	8	0.58	4.6	
954	Q355-10X94	310	8	2.29	18.3	
955	Q355-10X93	308	8	2.25	18.0	
956	Q355-6X72	174	4	0.59	2.4	
957	Q355-6X68	143	4	0.46	1.8	
958	Q355-14X80	200	4	1.76	7.0	
959	Q355-14X210	550	4	12.69	50.8	
960	Q355-38X104	104	12	3.23	38.8	
961	Q355-10X100	115	8	0.90	7.2	
962	Q355-6X50	100	4	0.24	1.0	
963	Q355L63X5	279	8	1.35	10.8	火曲 电焊
964	-6X100	180	8	0.85	6.8	火曲
965	C5	50	370	0.27	99.9	槽钢
966	C5	25	48	0.14	6.7	槽钢
967	C5	50	32	0.27	8.6	槽钢
968	-10X114	180	8	1.61	12.9	拉索附件
969	-8X80	95	8	0.48	3.8	拉索附件
970	C5	50	16	0.27	4.3	槽钢
971	-6X50	50	16	0.12	1.9	拉索附件
972	Q355-12X100	456	4	4.30	17.2	
973	Q355-12X100	416	4	3.92	15.7	
974	Q355-12X100	496	4	4.67	18.7	
975	Q355-12X100	456	4	4.30	17.2	
	GJ-50	6800	4	10.51	42.0	拉索附件
	GJ-50	7100	4	10.97	43.9	拉索附件
	NUT-2		8	3.20	25.6	拉索附件
	U-10		8	0.60	4.8	拉索附件
	NX-2.1		8	2.40	19.2	拉索附件
	JK-2		16	0.32	5.2	拉索附件
	FD4848B7D		4	50.8	203.2	
	FD5248B7D		4	74.4	297.6	
	C1504H7		8	9.61	76.9	
	C1805H1		4	23.88	95.5	
	C1805H5		4	7.12	28.5	
	C1805H7		8	13.82	110.6	
	C1905H7		8	13.85	110.8	
	C2005H5		8	9.74	77.9	
	X1504H7		4	13.1	52.4	
	X1805H7		4	21.6	86.4	
	X1905H7		4	17.9	71.6	
	X2005H7		4	24.4	97.6	
	T5530		1	28.8	28.8	
	T4855		1	25.0	25.0	
合计	11361.9 kg					

螺栓、脚钉、垫圈 明细表

名称	级别	规格	符号	数量	重量(kg)	备注
螺栓	6.8级	M16X45	⊘	36	6.1	
		M16X55	⊘	64	11.8	
		M16X65	⊗	256	51.4	
		M20X55	○	32	10.5	
		M20X65	⊘	148	52.2	
	8.8级	M24X75	⊘	140	83.0	
		M30X135	○	104	165.4	法兰螺栓
脚钉	6.8级	M16X185	⊖ ⊣	18	7.5	
垫圈	Q235	-3(ø22)	规格X个数	8	0.1	
合计		388.0 kg				

山东电力工程咨询院有限公司				浙江特高压交流环网工程线路 工程	施工图 设计阶段
批准	雷强	校核	马一丹	SZK31102A直线塔 身部结构图(2/3) ⑨	
审核	高锡鹏				
		设计/勘测	潘胜先		
比例		日期	2026年 08月	图号 37-SA36901S-T0121-024	版本