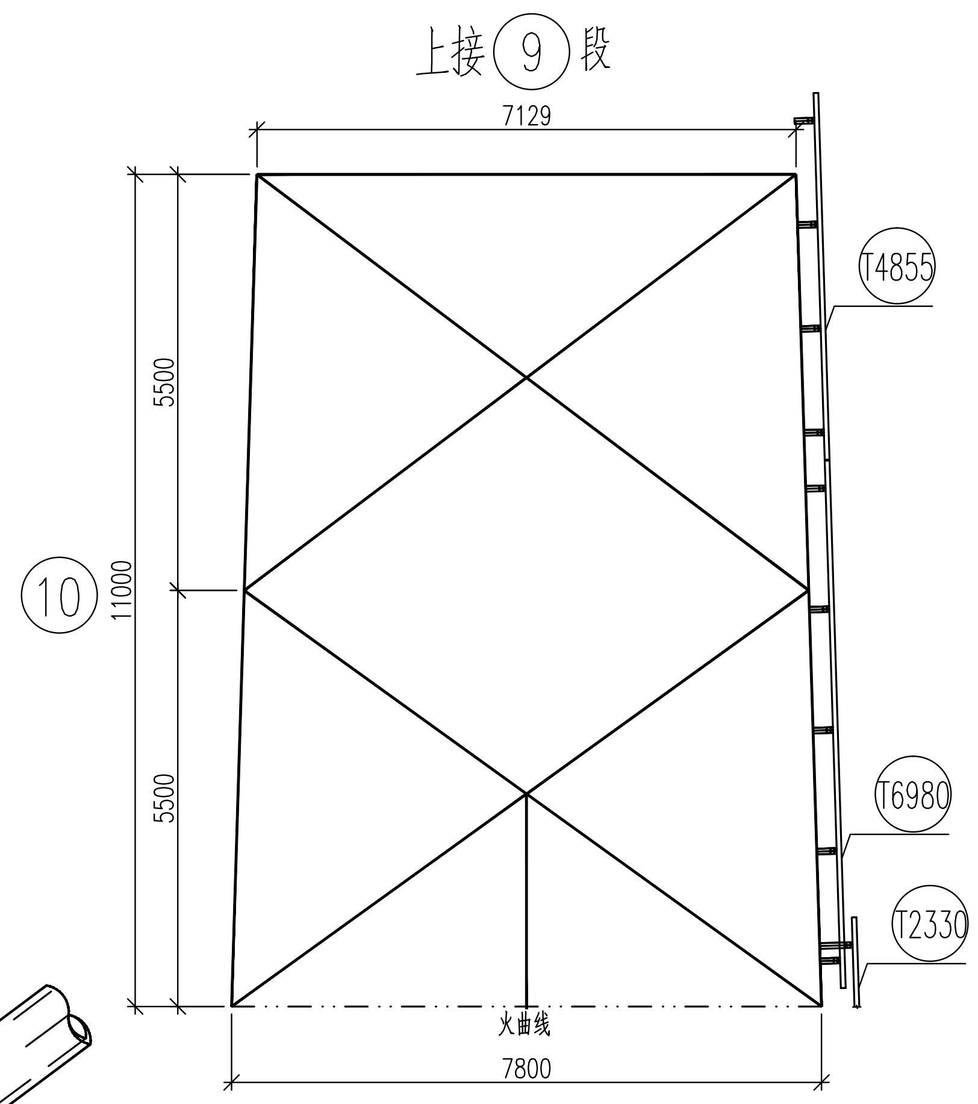

单线图
1:100

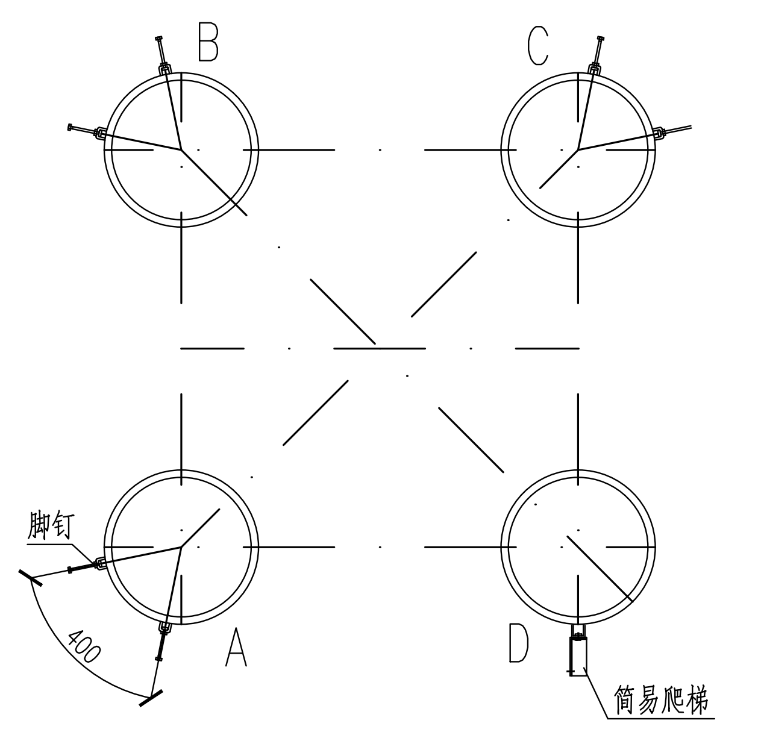

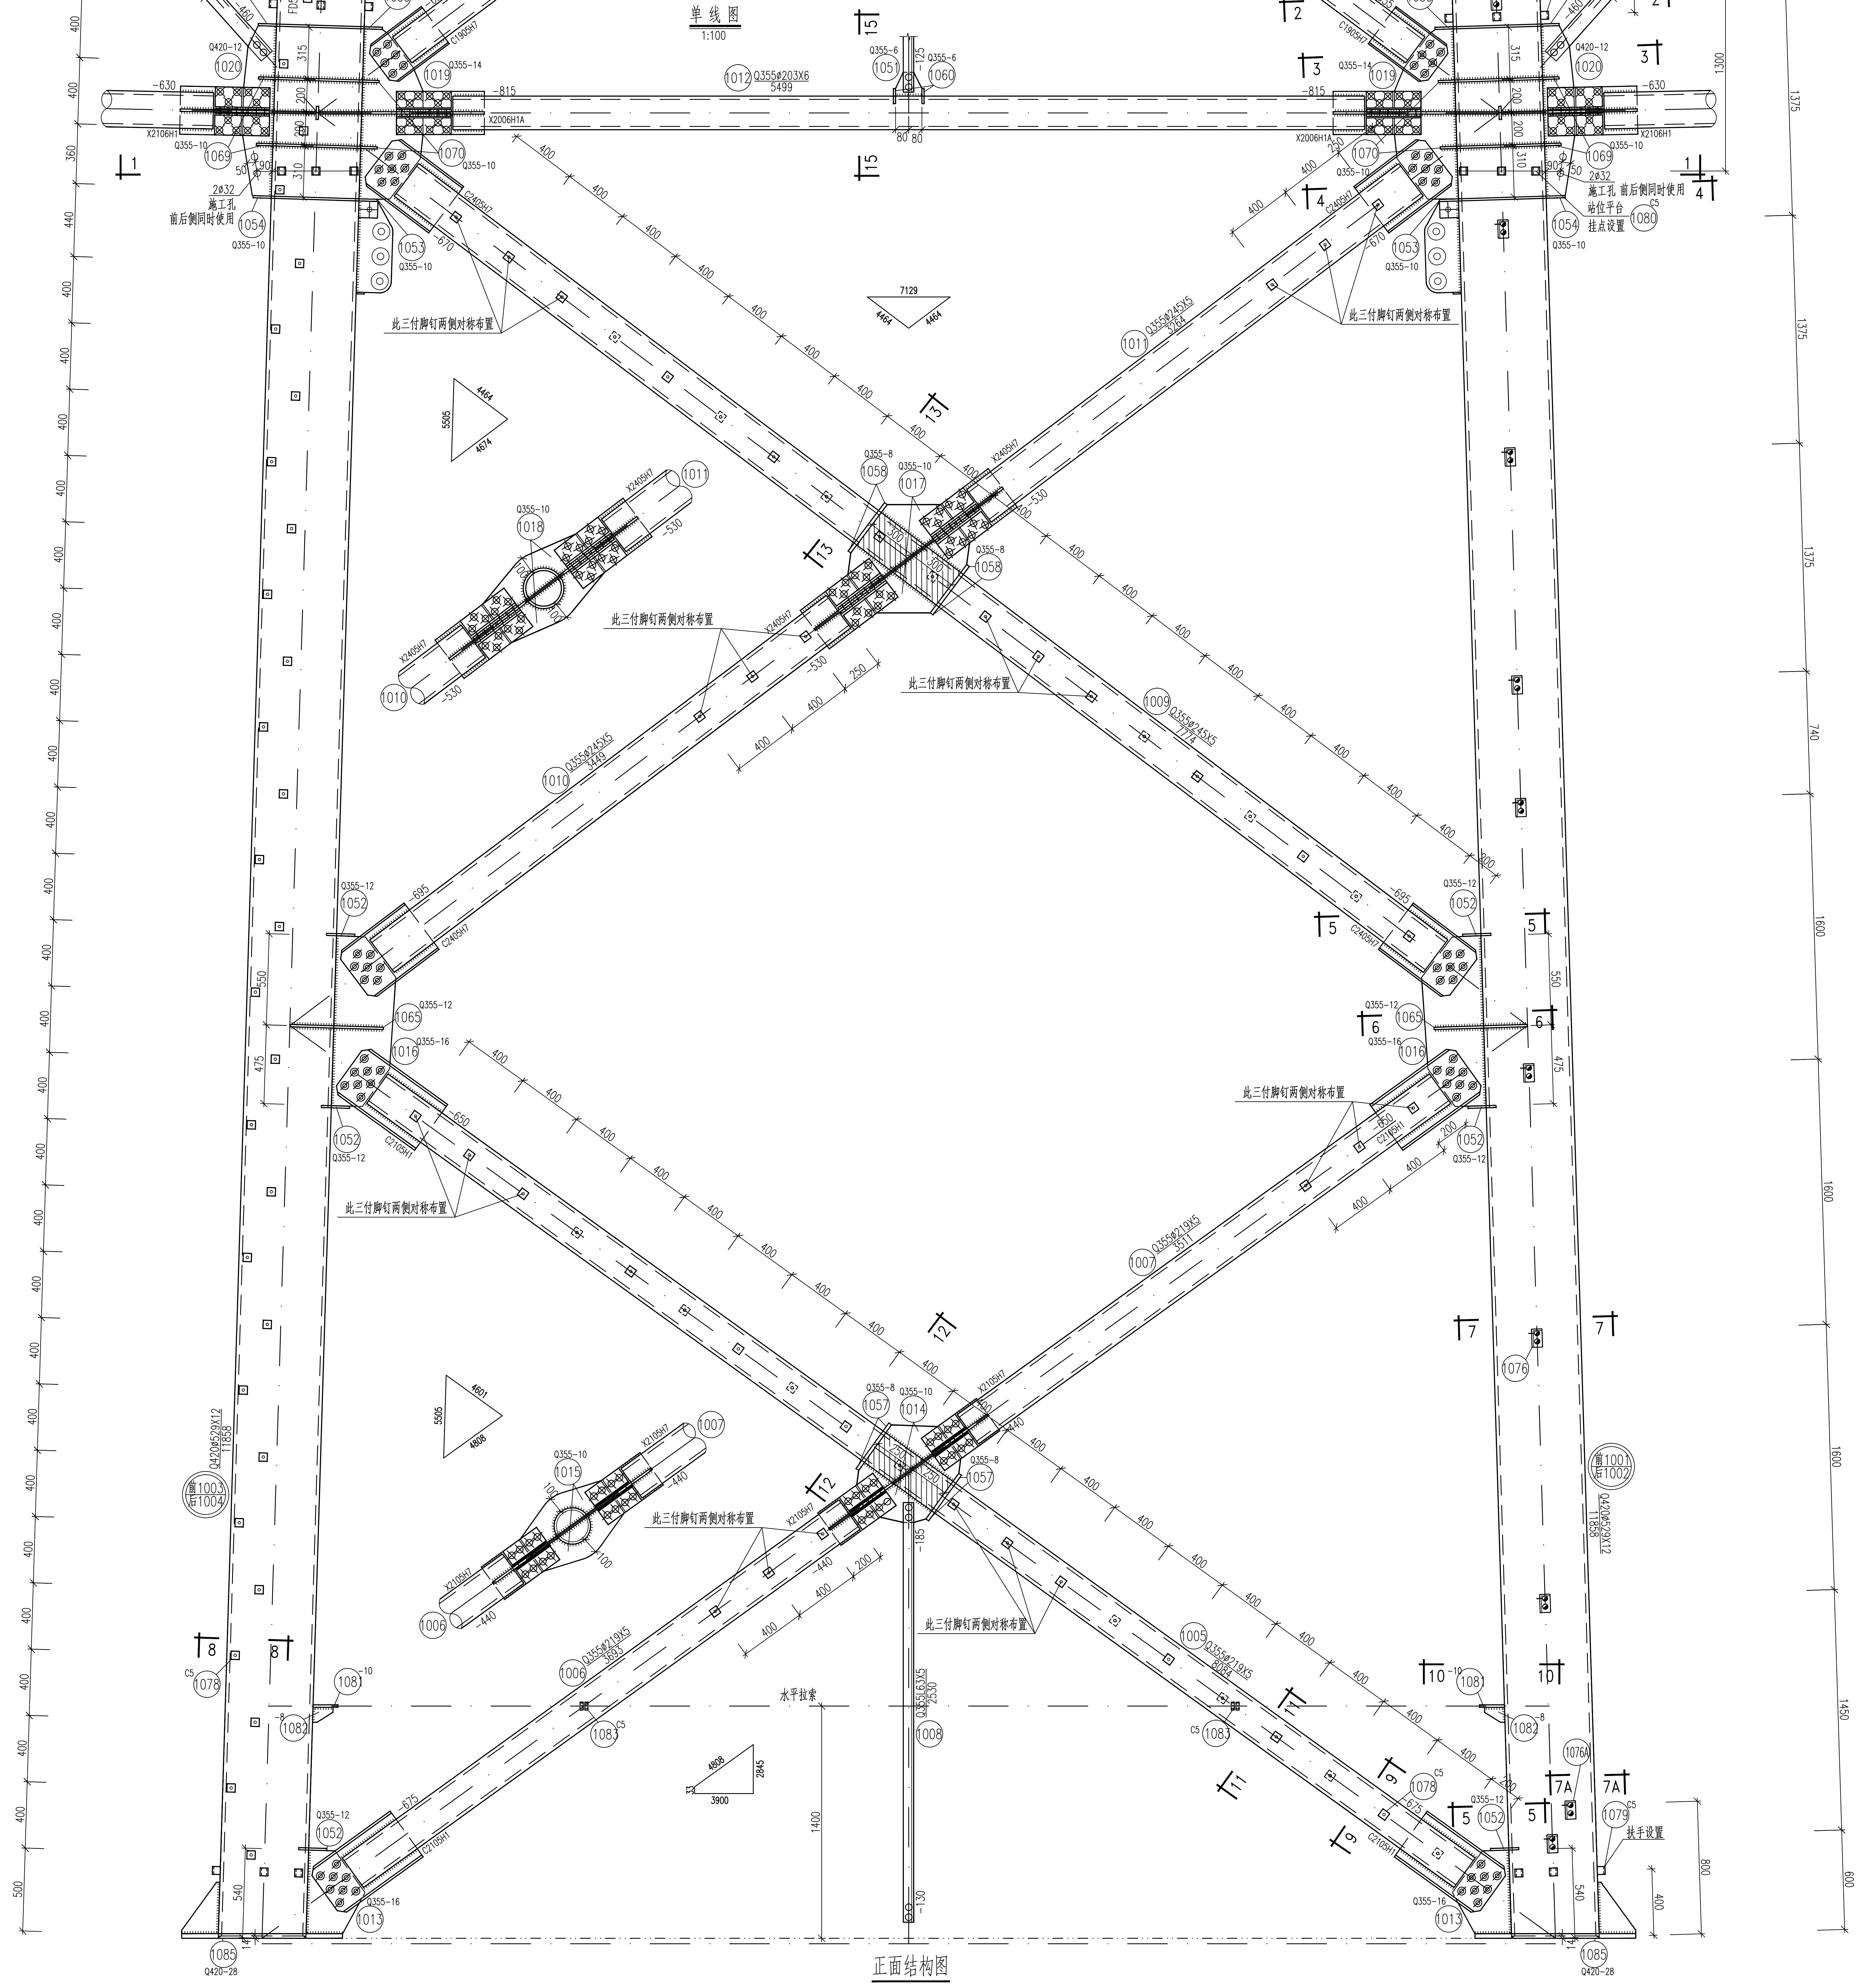

正面结构图

山东电力工程咨询院有限公司

				浙江特高压交流环网工程线路 工程	施工图	设计阶段
批　准	雷强	校　核	马一丹	SZK31102A直线塔 身部结构图(1/4) ⑩ 12.4		
审　核	高锡鹏	设计/勘测				
比　例		日　期	2026年 08月	图　号	37-SA36901S-T0121-026	版本