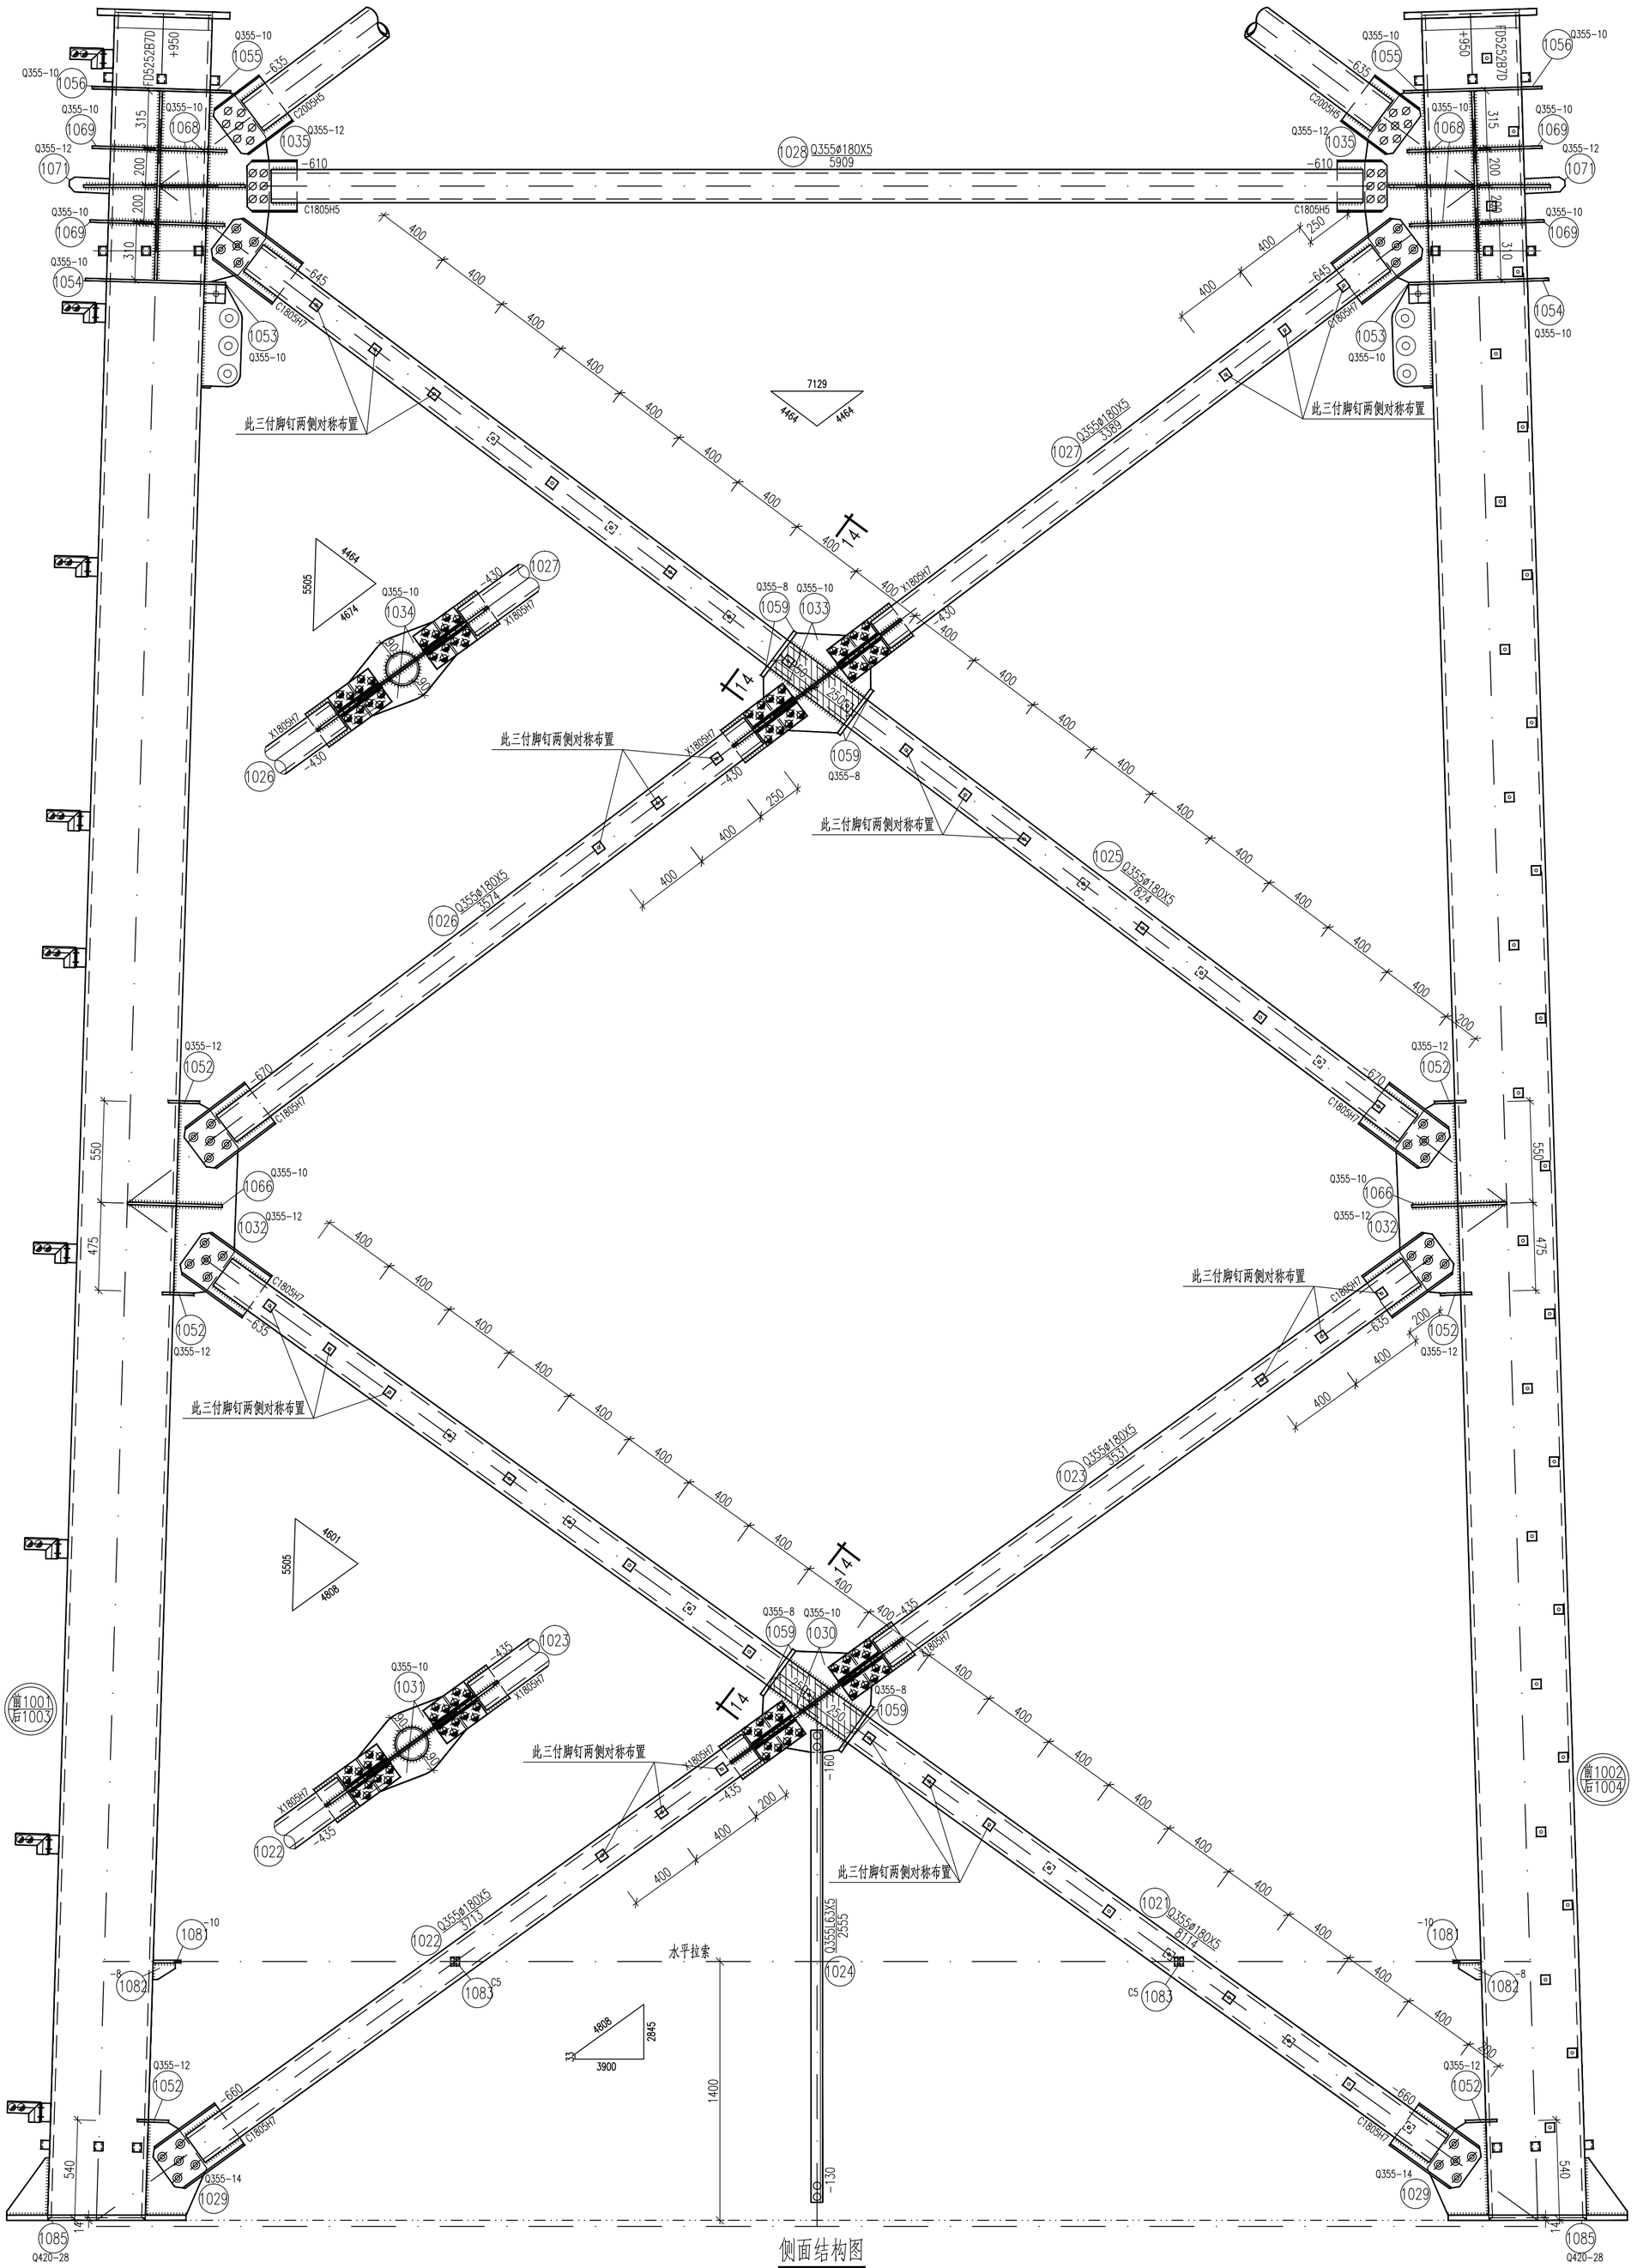


侧面结构图

山东电力工程咨询院有限公司				浙江特高压交流环网工程线路 工程	施工图 设计阶段
批 准		校 核		SZK31102A直线塔 身部结构图(2/4) ⑩	
审 核	高锡鹏	设计/勘测			
比 例		日 期	2026年 08月	图 号 37-SA36901S-T0121-027	版本