
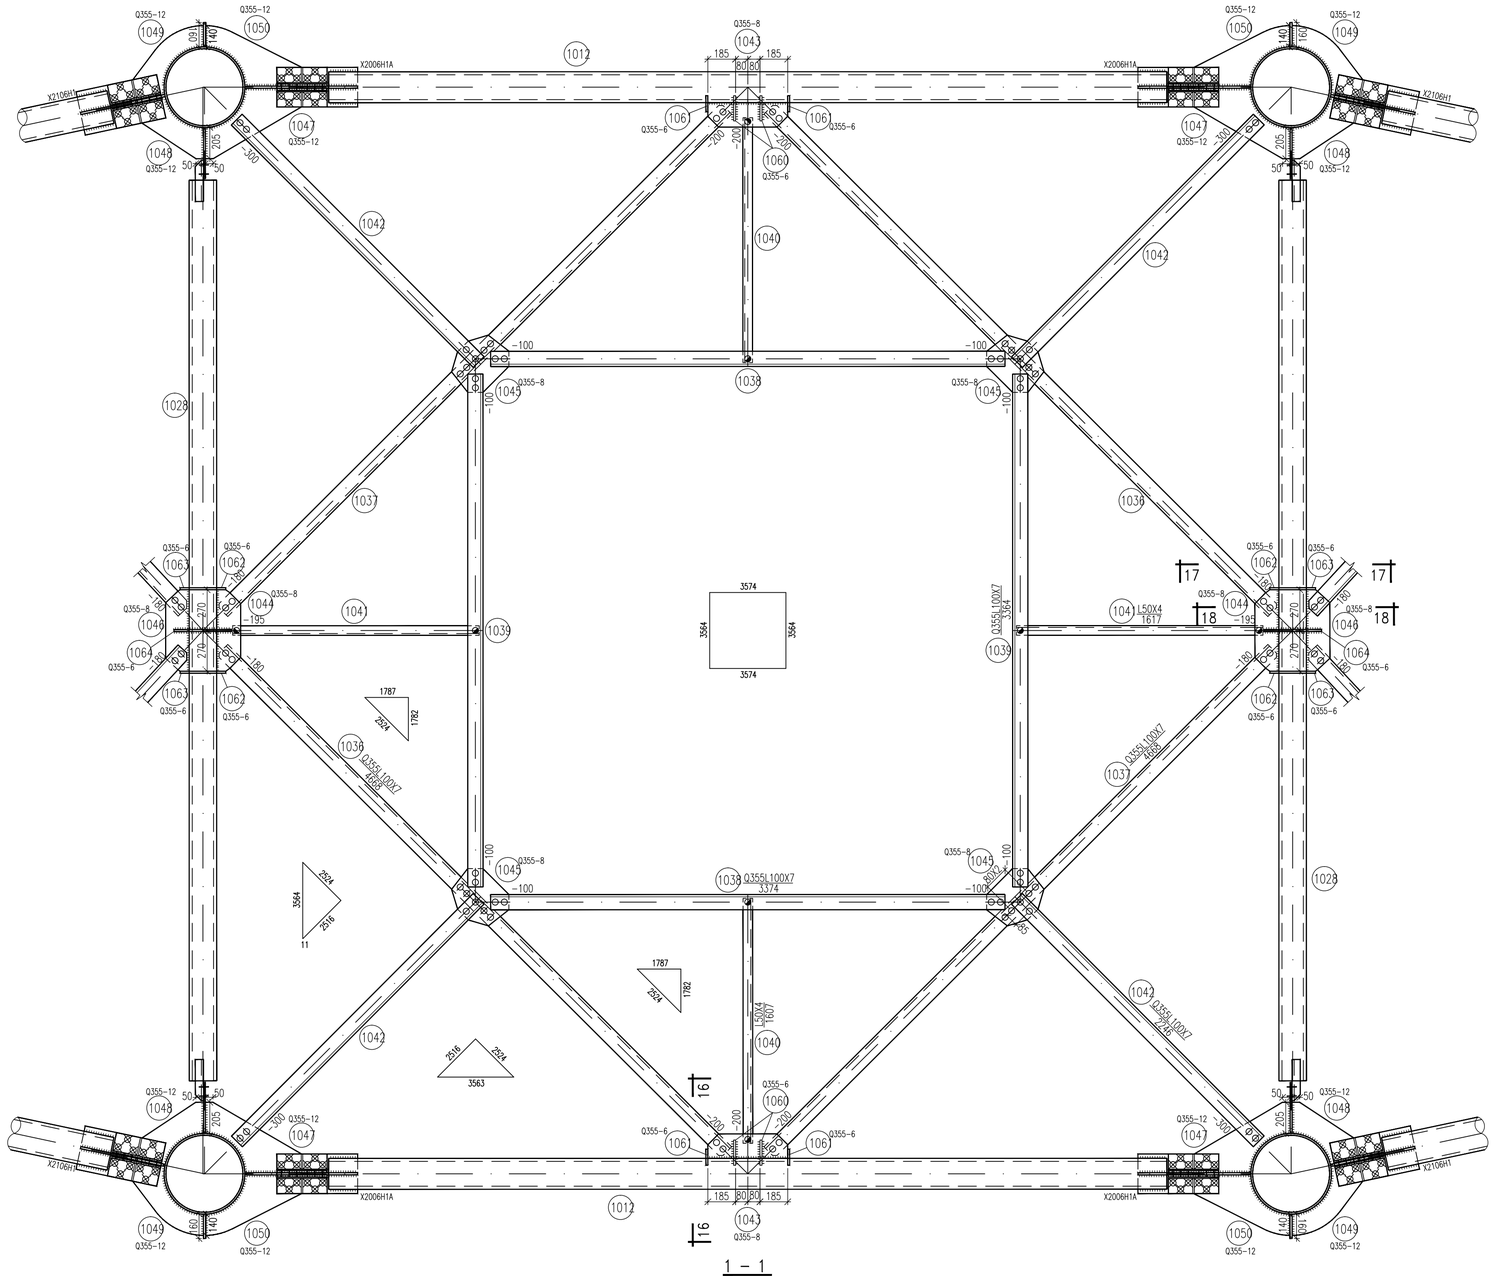


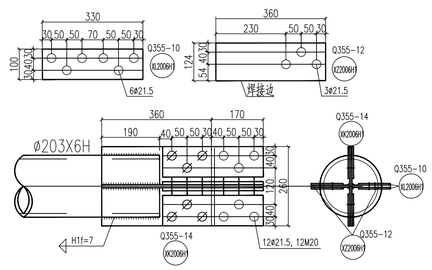

构件明细表

编号	规格	长度(mm)	数量	重量(kg) 一件	重量(kg) 小计	备注
1080	C5	50	16	0.27	4.3	槽钢
1081	-10X60	125	8	0.59	4.7	拉索附件
1082	-8X50	100	8	0.31	2.5	拉索附件
1083	C5	50	8	0.27	2.2	槽钢
1084	-6X50	50	8	0.12	1.0	拉索附件
1085	Q420-28X970	970	4	114.12	456.5	
1086	Q355-14X220	310	4	7.50	30.0	
1087	Q355-14X220	310	8	7.50	60.0	
1088	Q355-14X220	310	8	7.50	60.0	
1089	Q355-14X220	310	8	7.50	60.0	
1090	Q355-14X220	310	8	7.50	60.0	
1091	Q355-14X220	310	8	7.50	60.0	
1092	Q355-14X220	310	8	7.50	60.0	
1093	Q355-14X220	310	4	7.50	30.0	
	FD5252B7D		4	64.0	256.0	
	C1805H5		4	7.12	28.5	
	C1805H7		16	13.82	221.1	
	C2105H1		8	33.50	268.0	
	C2405H7		8	24.50	196.0	
	X1805H7		8	21.6	172.8	
	X2006H1A		4	39.40	178.0	
	X2105H7		4	22.9	91.6	
	X2405H7		4	33.9	135.6	
	T4855		1	25.0	25.0	
	T6980		1	36.2	36.2	
	T2330		1	12.4	12.4	
合计		16466.0 kg				

螺栓、脚钉、垫圈明细表

名称	级别	规格	符号	数量	重量(kg)	备注
螺栓	6.8级	M16X45		44	7.4	
		M16X65		192	38.6	
		M20X55		52	17.0	
		M20X65		98	34.6	
		M20X75		350	132.4	
	8.8级	M24X75		224	132.8	
		M33X150		104	220.3	法兰螺栓
脚钉	6.8级	M16X185		53	22.0	
垫圈	Q235		规格X个数			
合计			605.1 kg			

构件明细表

编号	规格	长度(mm)	数量	重量(kg) 一件	重量(kg) 小计	备注
1001	Q420Φ529X12	11858	1	1814.27	1814.3	带爬梯 一端切弧
1002	Q420Φ529X12	11858	1	1814.27	1814.3	带脚钉 一端切弧
1003	Q420Φ529X12	11858	1	1814.27	1814.3	带脚钉 一端切弧
1004	Q420Φ529X12	11858	1	1814.27	1814.3	带脚钉 一端切弧
1005	Q355Φ219X5	8084	2	213.32	426.6	带爬梯
1006	Q355Φ219X5	3693	2	97.45	194.9	带爬梯
1007	Q355Φ219X5	3511	2	92.65	185.3	带爬梯
1008	Q355L63X5	2530	2	12.20	24.4	
1009	Q355Φ245X5	7774	2	230.06	460.1	带爬梯
1010	Q355Φ245X5	3449	2	102.07	204.1	带爬梯
1011	Q355Φ245X5	3264	2	96.59	193.2	带爬梯
1012	Q355Φ203X6	5499	2	160.30	320.6	
1013	Q355-16X388	554	4	27.00	108.0	
1014	Q355-10X550	660	2	28.50	57.0	
1015	Q355-10X202	660	4	10.47	41.9	
1016	Q355-16X405	1128	4	57.38	229.5	
1017	Q355-10X660	770	2	39.89	79.8	
1018	Q355-10X236	770	4	14.27	57.1	
1019	Q355-14X404	1128	4	50.08	200.3	
1020	Q420-12X207	1128	4	22.00	88.0	
1021	Q355Φ180X5	8114	2	175.09	350.2	带脚钉
1022	Q355Φ180X5	3713	2	80.12	160.2	带脚钉
1023	Q355Φ180X5	3531	2	76.19	152.4	带脚钉
1024	Q355L63X5	2555	2	12.32	24.6	
1025	Q355Φ180X5	7824	2	168.83	337.7	带脚钉
1026	Q355Φ180X5	3574	2	77.12	154.2	带脚钉
1027	Q355Φ180X5	3389	2	73.13	146.3	带脚钉
1028	Q355Φ180X5	5909	2	127.51	255.0	
1029	Q355-14X354	554	4	21.55	86.2	
1030	Q355-10X550	627	2	27.07	54.1	
1031	Q355-10X193	627	4	9.50	38.0	
1032	Q355-12X355	1128	4	37.72	150.9	
1033	Q355-10X500	616	2	24.18	48.4	
1034	Q355-10X193	616	4	9.33	37.3	
1035	Q355-12X369	1128	4	39.21	156.8	
1036	Q355L100X7	4668	2	50.58	101.2	切角
1037	Q355L100X7	4668	2	50.58	101.2	切角
1038	Q355L100X7	3374	2	36.56	73.1	
1039	Q355L100X7	3364	2	36.45	72.9	
1040	L50X4	1607	2	4.92	9.8	
1041	L50X4	1617	2	4.95	9.9	
1042	Q355L100X7	2246	4	24.34	97.4	
1043	Q355-8X180	583	2	6.59	13.2	
1044	Q355-8X178	594	2	6.64	13.3	
1045	Q355-8X406	414	4	10.56	42.2	
1046	Q355-8X164	594	2	6.12	12.2	
1047	Q355-12X324	859	4	26.22	104.9	
1048	Q355-12X249	626	4	14.68	58.7	
1049	Q355-12X246	722	4	16.73	66.9	
1050	Q355-12X309	814	4	23.69	94.8	
1051	Q355-6X154	176	2	1.28	2.6	
1052	Q355-12X110	1104	12	11.44	137.3	
1053	Q355-10X115	1113	4	10.05	40.2	
1054	Q355-10X115	1113	4	10.05	40.2	
1055	Q355-10X110	1104	4	9.53	38.1	
1056	Q355-10X110	1104	4	9.53	38.1	
1057	Q355-8X60	482	8	1.82	14.6	
1058	Q355-8X60	527	8	1.99	15.9	
1059	Q355-8X60	415	16	1.56	25.0	
1060	Q355-6X150	374	4	2.64	10.6	
1061	Q355-6X60	228	4	0.64	2.6	
1062	Q355-6X60	415	4	1.17	4.7	
1063	Q355-6X60	415	4	1.17	4.7	
1064	Q355-6X100	484	4	2.28	9.1	
1065	Q355-12X106	367	8	3.66	29.3	
1066	Q355-10X105	316	8	2.60	20.8	
1067	Q355-10X100	543	8	4.26	34.1	
1068	Q355-10X100	521	8	4.09	32.7	
1069	Q355-10X100	565	8	4.44	35.5	
1070	Q355-10X100	543	8	4.26	34.1	
1071	Q355-12X80	154	4	1.16	4.6	
1072	Q355-14X210	550	4	12.69	50.8	
1073	Q355-38X104	104	12	3.23	38.8	
1074	Q355-10X100	115	8	0.90	7.2	
1075	Q355-6X50	100	4	0.24	1.0	
1076	Q355L63X5	255	9	1.23	11.1	火曲 电焊
1076A	Q355L63X5	270	1	1.30	1.3	火曲 电焊
1077	-6X100	180	10	0.85	7.6	火曲
1078	C5	50	387	0.27	104.5	槽钢
1079	C5	25	32	0.14	4.5	槽钢

构件明细表

插板编号	板件编号	主管规格	插板规格尺寸(mm)	数量	重量(kg) 单件	重量(kg) 小计	连接螺栓	承载力(kN)	备注
X2006H1A	XK2006H1	Φ203X6H	-14X360X260	1	10.29	39.4	12M20	1151	
	XZ2006H1		-12X360X124	2	4.21				
	XL2006H1		-10X330X100	8	2.59				

说明:1. 插板的材质为Q355B,
2. M16~M20螺栓为 6.8级,M24及以上螺栓为 8.8级.
3. M16 M20 M24螺栓分别用 ◪ ⊘ ◎ 表示,螺栓孔用 ⊠ 表示.
4. 十字交叉焊缝高度取同与管子焊缝的高度.

山东电力工程咨询院有限公司		浙江特高压交流环网工程线路	工程	施工图	设计阶段	
批准	曹强	校核	习一斗	SZK31102A直线塔 身部结构图(3/4)		⑩
审核	高鹏鸥					
比例		设计/勘测	潘旭光			
		日期	2026年 08月	图号	37-SA36901S-T0121-028	版本