

构件明细表


编号	规格	长度(mm)	数量	重量(kg) 一件	重量(kg) 小计	备注
1101	Q420ø584X12	5394	1	913.08	913.1	一端切弧 装爬梯
1102	Q420ø584X12	5394	3	913.08	2739.2	一端切弧 带脚钉
1103	Q355ø219X5	9357	4	246.91	987.6	带脚钉
1104	Q355ø219X5	4672	4	123.28	493.1	带脚钉
1105	Q355ø219X5	3806	4	100.43	401.7	带脚钉
1106	Q355ø219X5	6448	4	170.15	680.6	带脚钉
1107	Q355-10X440	660	4	22.80	91.2	
1108	Q355-10X235	660	8	12.18	97.4	
1109	Q355L125X8	5022	4	77.86	311.4	
1110	Q355L100X8	2276	4	27.94	111.8	
1111	Q355L110X8	3724	4	50.40	201.6	
1112	L50X4	1737	4	5.31	21.2	
1113	Q355-10X215	682	4	11.51	46.0	
1114	Q355-10X417	415	4	13.58	54.3	
1115	Q420-28X1155	1155	4	293.22	1172.9	
1116	Q355-14X193	310	4	6.58	26.3	
1117	Q355-14X193	310	8	6.58	52.6	
1118	Q355-14X352	480	8	18.57	148.6	
1119	Q355-14X193	310	8	6.58	52.6	
1120	Q355-14X193	310	8	6.58	52.6	
1121	Q355-14X193	310	8	6.58	52.6	
1122	Q355-14X193	310	8	6.58	52.6	
1123	Q355-14X193	310	8	6.58	52.6	
1124	Q355-14X193	310	4	6.58	26.3	
1125	Q355-10X120	1106	4	10.42	41.7	
1126	Q355-8X60	438	16	1.65	26.4	
1127	Q355-8X60	219	8	0.83	6.6	
1128	Q355L63X5	348	4	1.68	6.7	火曲
1128A	Q355L63X5	270	1	1.30	1.3	火曲
1129	Q355-6X100	180	5	0.85	4.2	火曲
1130	C5	50	207	0.27	55.9	槽钢
1131	C5	25	32	0.14	4.5	槽钢
1132	C5	50	16	0.27	4.3	槽钢
1133	Q355-14X210	550	4	12.69	50.8	
1134	Q355-38X104	104	12	3.23	38.8	
1135	Q355-10X100	115	8	0.90	7.2	
1136	Q355-6X50	100	4	0.24	1.0	
1137	Q355-6X141	160	4	1.06	4.2	
1138	Q355-6X60	207	8	0.58	4.6	
	C2105H5		16	14.54	232.6	
	C2105H7		8	16.79	134.3	
	X2105H7		8	22.9	183.2	
	FD5858B8D		4	105.0	420.0	
	T3930	–	1	20.70	20.7	主材安装爬梯
合计				10088.9 kg		


螺栓、脚钉、垫圈明细表


名称	级别	规格	符号	数量	重量(kg)	备注
螺栓	6.8级	M16X45		24	4.0	
		M16X55		4	0.7	
		M20X55		8	2.6	
		M20X65		48	16.9	
		M20X75		136	51.4	
		M20X105		8	3.6	
	8.8级	M24X75		40	23.7	
		M24X115		48	35.6	
		M42X155		64	261.8	法兰螺栓
脚钉	6.8级	M16X185		207	85.8	
垫圈	Q235	-4(ø21.5)	规格X个数	8	0.2	
合计				486.3 kg		

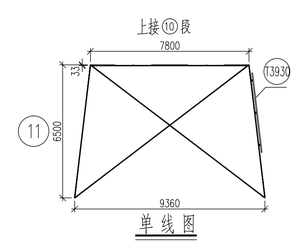


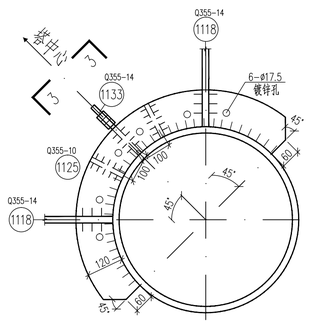


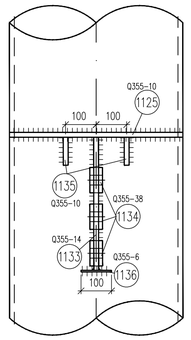


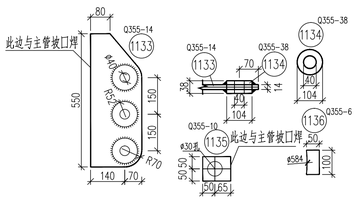


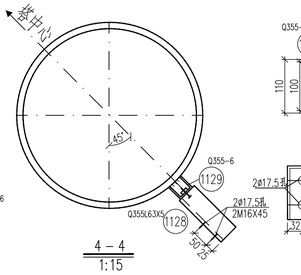


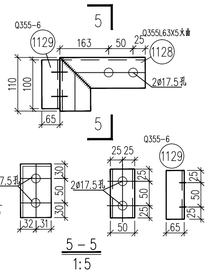


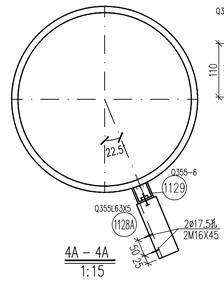

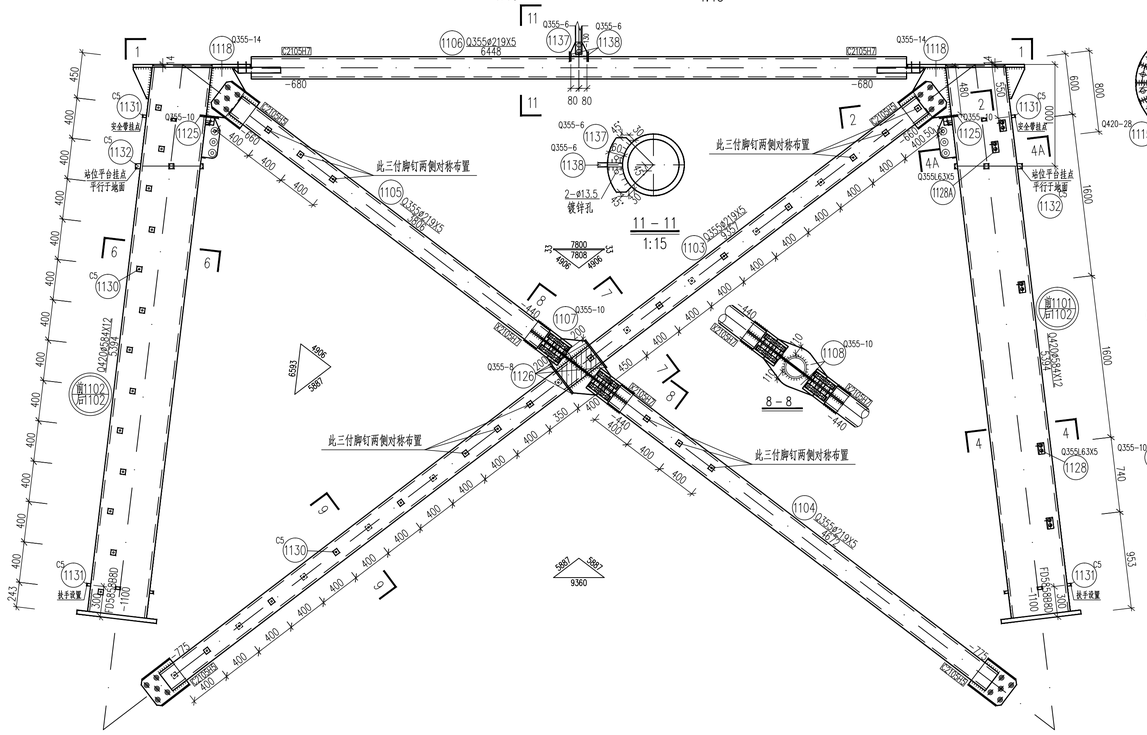

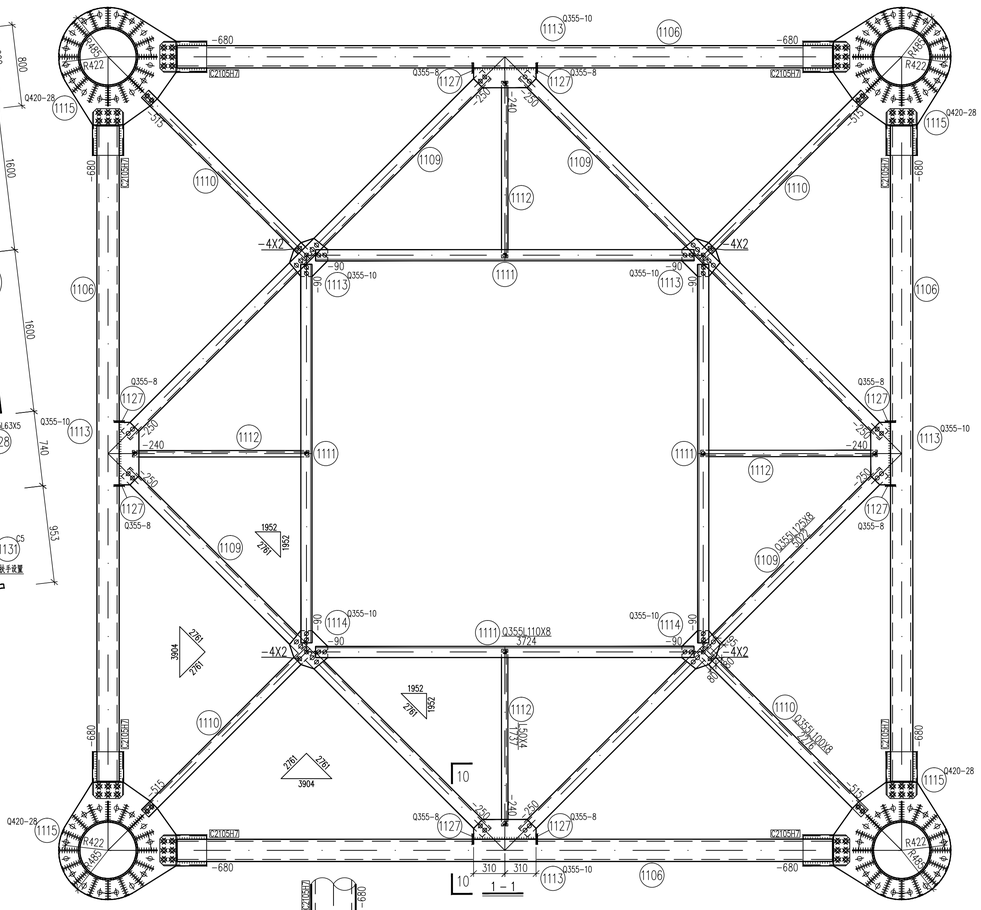

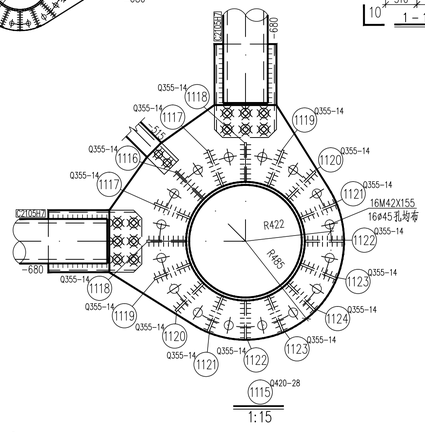

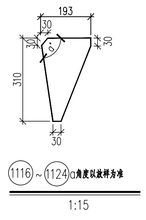

山东电力工程咨询院有限公司			浙江特高压交流环网工程线路	工程	施工图 设计阶段
批准	董强	校核	习一舟	SZK31102A双回路直线塔 身部结构图	11
审核	高鹏鸣				
比例	1:30	设计/勘测	潘旭光		
		日期	2026年 08月	图号 37-SA36901S-T0121-030	版本