


上接⑪段

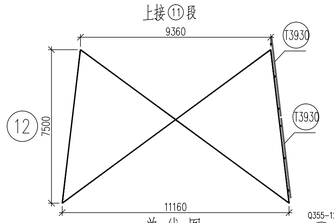


单线图 1:150

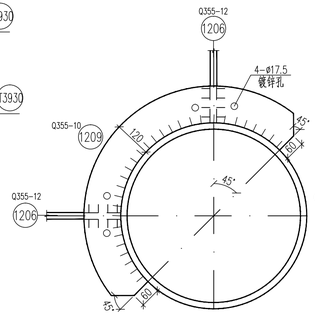


1－1 1:15

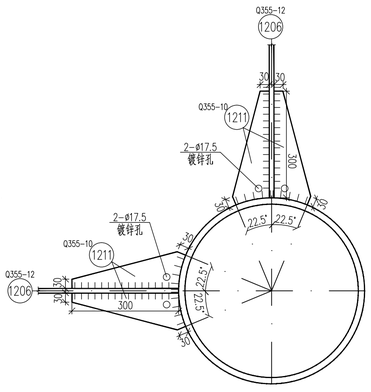


2－2 1:15

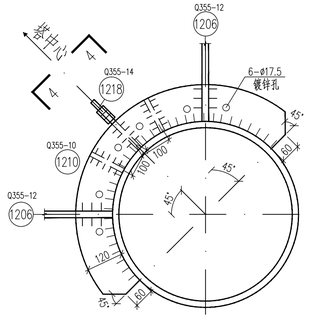


3－3 1:15

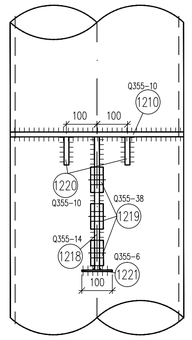


4－4 1:15

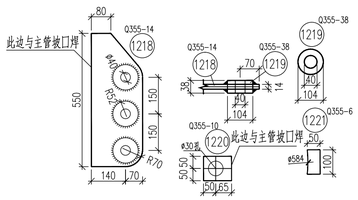


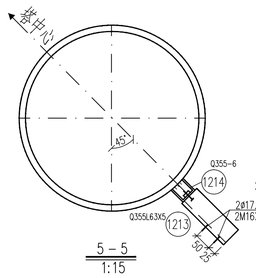



5－5 1:15

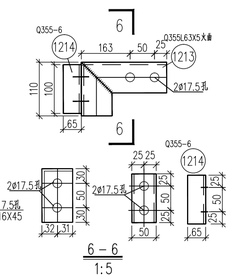


6－6 1:5

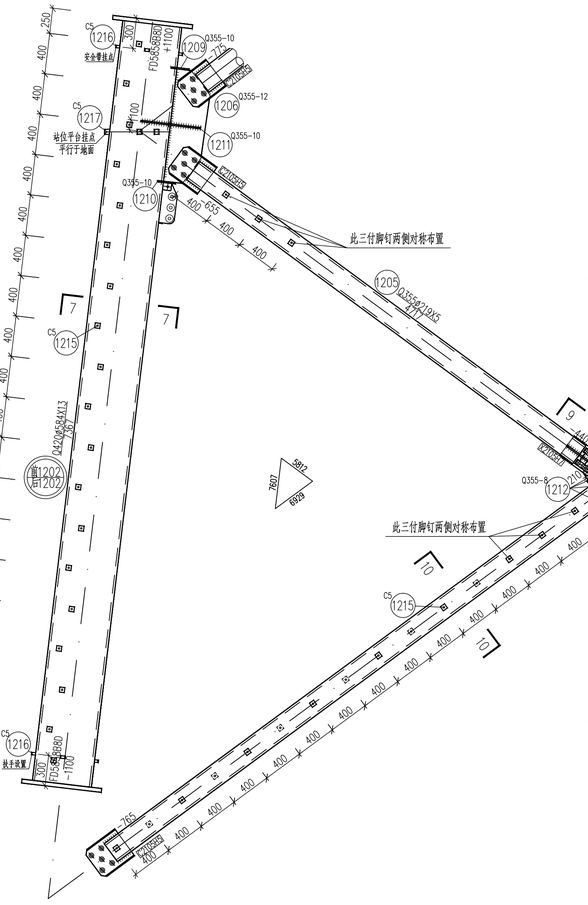

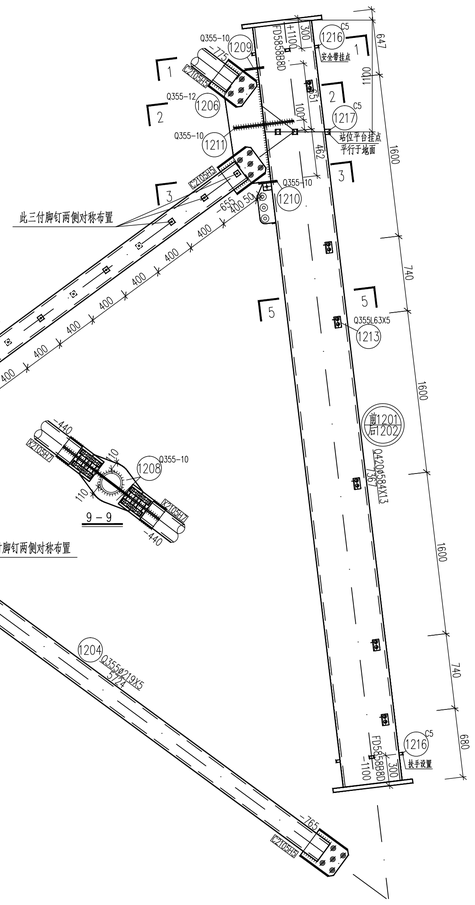


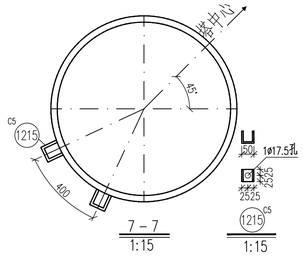


7－7 1:15 10－10 1:15

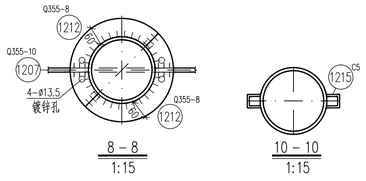


8－8 1:15

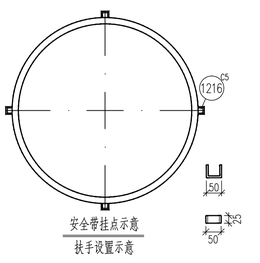

安全带挂点示意
扶手设置示意

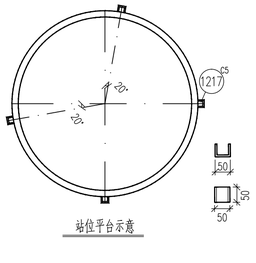

站位平台示意

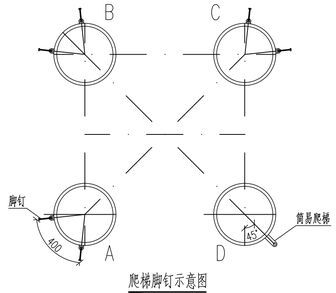

爬梯脚钉示意图

构件明细表

编号	规格	长度(mm)	数量	重量(kg) 一件	重量(kg) 小计	备注
1201	Q420ø584X13	7367	1	1348.62	1348.6	装爬梯
1202	Q420ø584X13	7367	3	1348.62	4045.9	带脚钉
1203	Q355ø219X5	11321	4	298.74	1195.0	带脚钉
1204	Q355ø219X5	5724	4	151.04	604.2	带脚钉
1205	Q355ø219X5	4717	4	124.47	497.9	带脚钉
1206	Q355-12X394	1179	8	43.76	350.1	
1207	Q355-10X460	660	4	23.83	95.3	
1208	Q355-10X215	660	8	11.14	89.1	
1209	Q355-10X120	1217	4	11.46	45.8	
1210	Q355-10X120	1217	4	11.46	45.8	
1211	Q355-10X123	330	16	3.19	51.0	
1212	Q355-8X60	482	16	1.82	29.1	
1213	Q355L63X5	348	6	1.68	10.1	火曲
1214	Q355-6X100	180	6	0.85	5.1	火曲
1215	C5	50	248	0.27	67.0	槽钢
1216	C5	25	32	0.14	4.5	槽钢
1217	C5	50	16	0.27	4.3	槽钢
1218	Q355-14X210	550	4	12.69	50.8	
1219	Q355-38X104	104	12	3.23	38.8	
1220	Q355-10X100	115	8	0.90	7.2	
1221	Q355-6X50	100	4	0.24	1.0	
	C2105H5		16	14.54	232.6	
	X2105H7		8	22.9	183.2	
	FD5858B8D		8	105.0	840.0	
	T3930	–	2	20.70	41.4	主材安装爬梯
合计				9883.8 kg		

螺栓、脚钉、垫圈明细表

名称	级别	规格	符号	数量	重量(kg)	备注
螺栓	6.8级	M16X45		24	4.0	
		M20X75		128	48.4	
	8.8级	M24X75		80	47.4	
		M39X180		104	374.2	法兰螺栓
脚钉	6.8级	M16X185		248	102.8	
垫圈	Q235		规格X个数			
合计				576.8 kg		

山东电力工程咨询院有限公司			浙江特高压交流环网工程线路 工程	施工图	设计阶段
批准		校核		SZK31102A双回路直线塔	12
审核		设计/勘测		身部结构图	
比例	1:30	日期	2026年 08月	图号 37-SA36901S-T0121-031	版本