






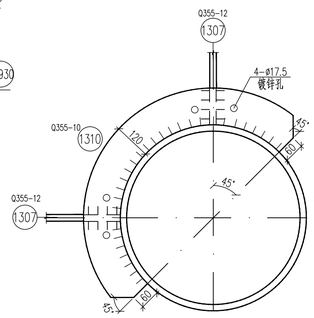


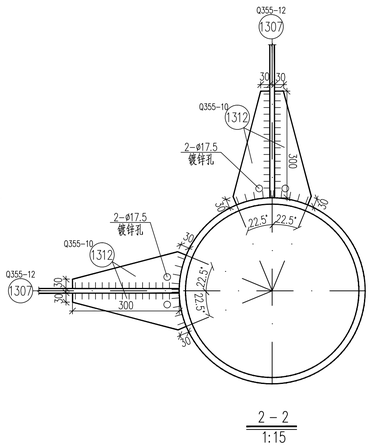


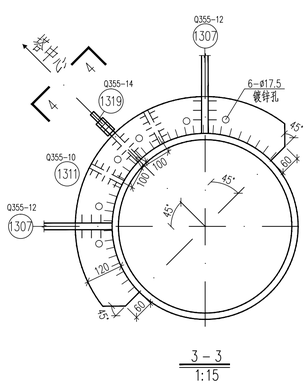


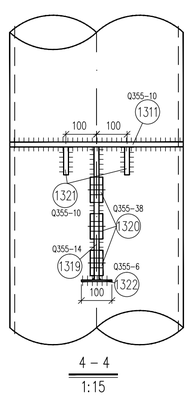


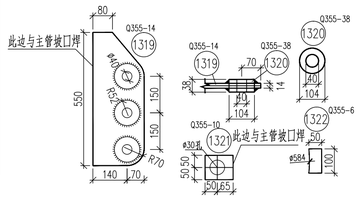


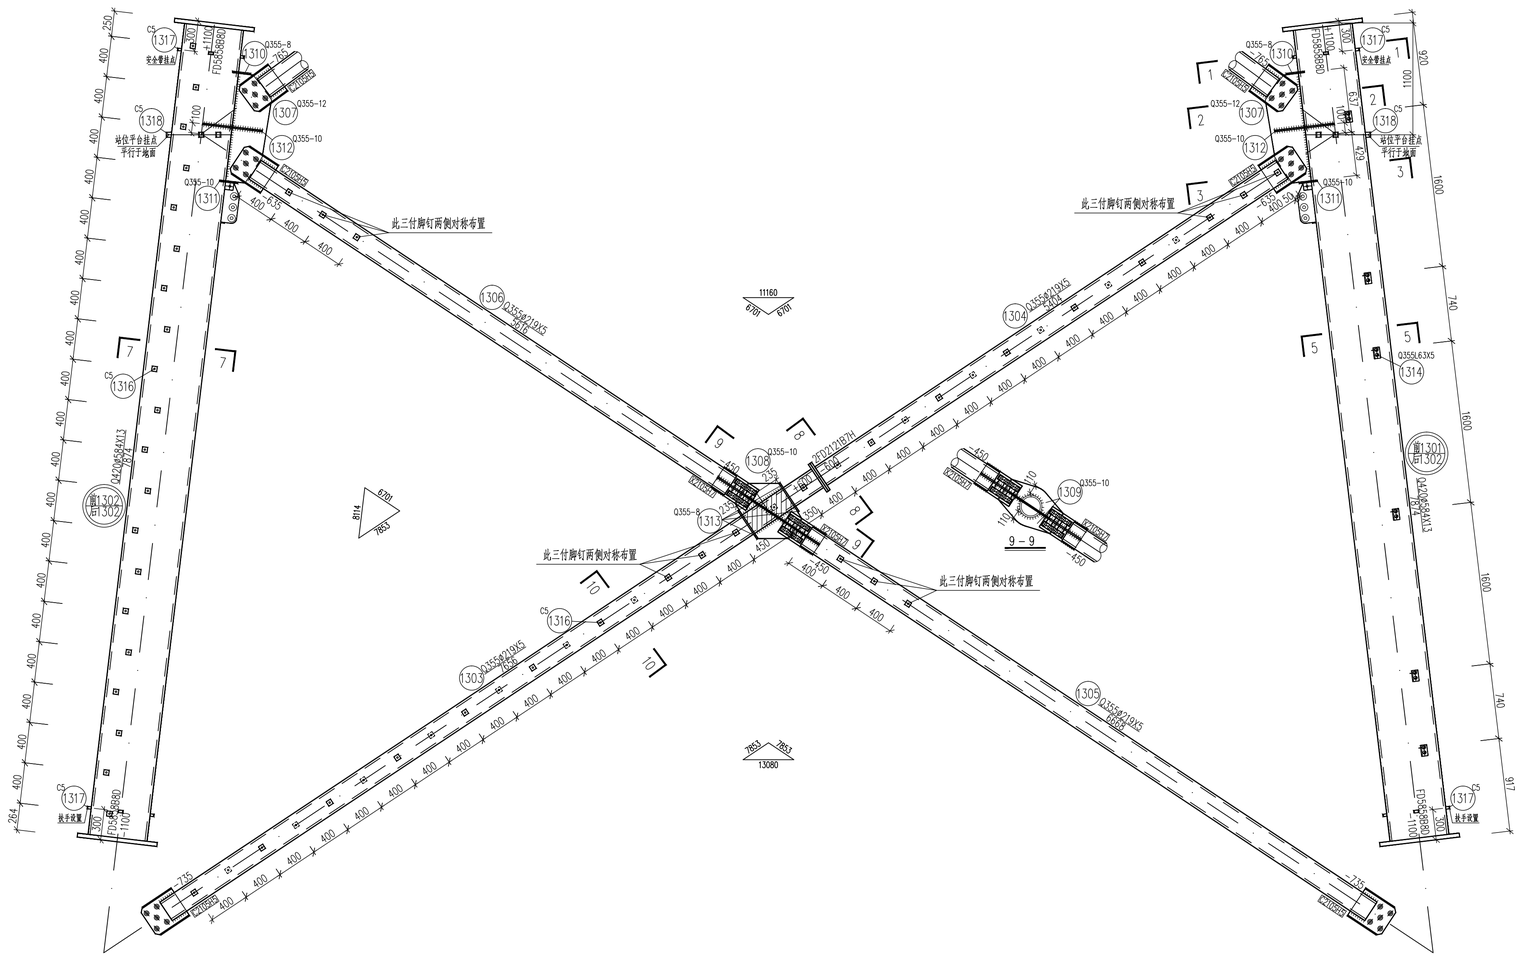


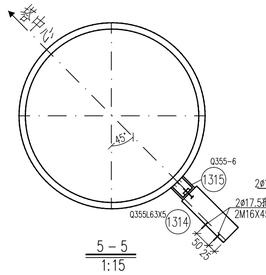


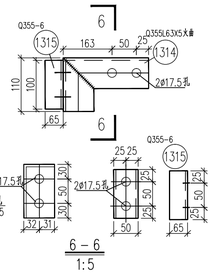


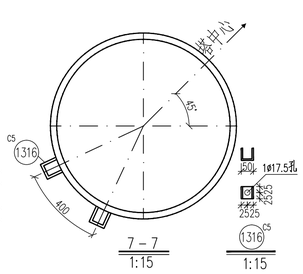


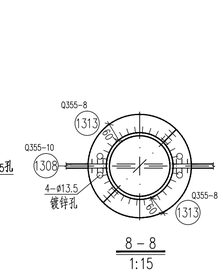

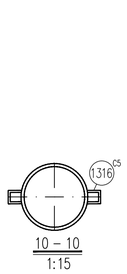

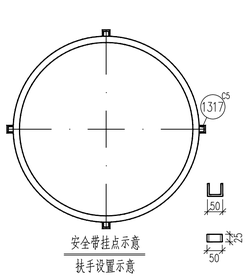

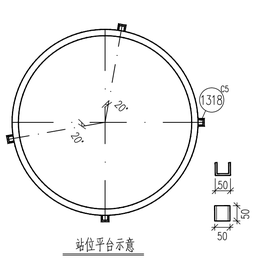

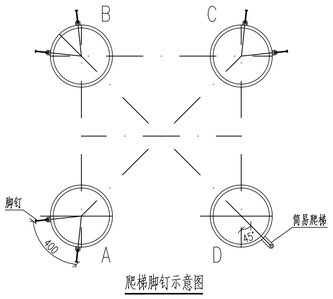

构件明细表

编号	规格	长度(mm)	数量	重量(kg) 一件	重量(kg) 小计	备注
1301	Q420ø584X13	7874	1	1441.43	1441.4	装爬梯
1302	Q420ø584X13	7874	3	1441.43	4324.3	带脚钉
1303	Q355ø219X5	7656	4	202.03	808.1	带脚钉
1304	Q355ø219X5	5404	4	142.60	570.4	带脚钉
1305	Q355ø219X5	6668	4	175.95	703.8	带脚钉
1306	Q355ø219X5	5616	4	148.19	592.8	带脚钉
1307	Q355-12X394	1128	8	41.87	335.0	
1308	Q355-10X520	682	4	27.84	111.4	
1309	Q355-10X215	682	8	11.51	92.1	
1310	Q355-10X120	1217	4	11.46	45.8	
1311	Q355-10X120	1217	4	11.46	45.8	
1312	Q355-10X123	330	16	3.19	51.0	
1313	Q355-8X60	482	16	1.82	29.1	
1314	Q355L63X5	348	6	1.68	10.1	大鱼
1315	Q355-6X100	180	6	0.85	5.1	大鱼
1316	C5	50	267	0.27	72.1	槽钢
1317	C5	25	32	0.14	4.5	槽钢
1318	C5	50	16	0.27	4.3	槽钢
1319	Q355-14X210	550	4	12.69	50.8	
1320	Q355-38X104	104	12	3.23	38.8	
1321	Q355-10X100	115	8	0.90	7.2	
1322	Q355-6X50	100	4	0.24	1.0	
	C2105H5		16	14.54	232.6	
	X2105H7		8	22.9	183.2	
	FD2121B7H		8	9.2	73.6	
	FD5858B8D		8	105.0	840.0	
	T3930	–	2	20.70	41.4	主材安装爬梯
合计				10715.7 kg		

螺栓、脚钉、垫圈明细表

名称	级别	规格	符号	数量	重量(kg)	备注
螺栓	6.8级	M16X45	◪	24	4.0	
		M20X75	⊠	128	48.4	
	8.8级	M24X75	⊘	80	47.4	
		M20X90	○	56	26.4	法兰螺栓
		M39X180	○	104	374.2	法兰螺栓
脚钉	6.8级	M16X185	⊖	267	110.7	
垫圈	Q235		规格X个数			
合计				611.1 kg		

山东电力工程咨询院有限公司			浙江特高压交流环网工程线路	工程	施工图 设计阶段
批准	曹强	校核	习一舟	SZK31102A双回路直线塔 身部结构图	13
审核	高鹏鹏	设计/勘测	张旭光		
比例	1:30	日期	2026年08月	图号 37-SA36901S-T0121-032	版本