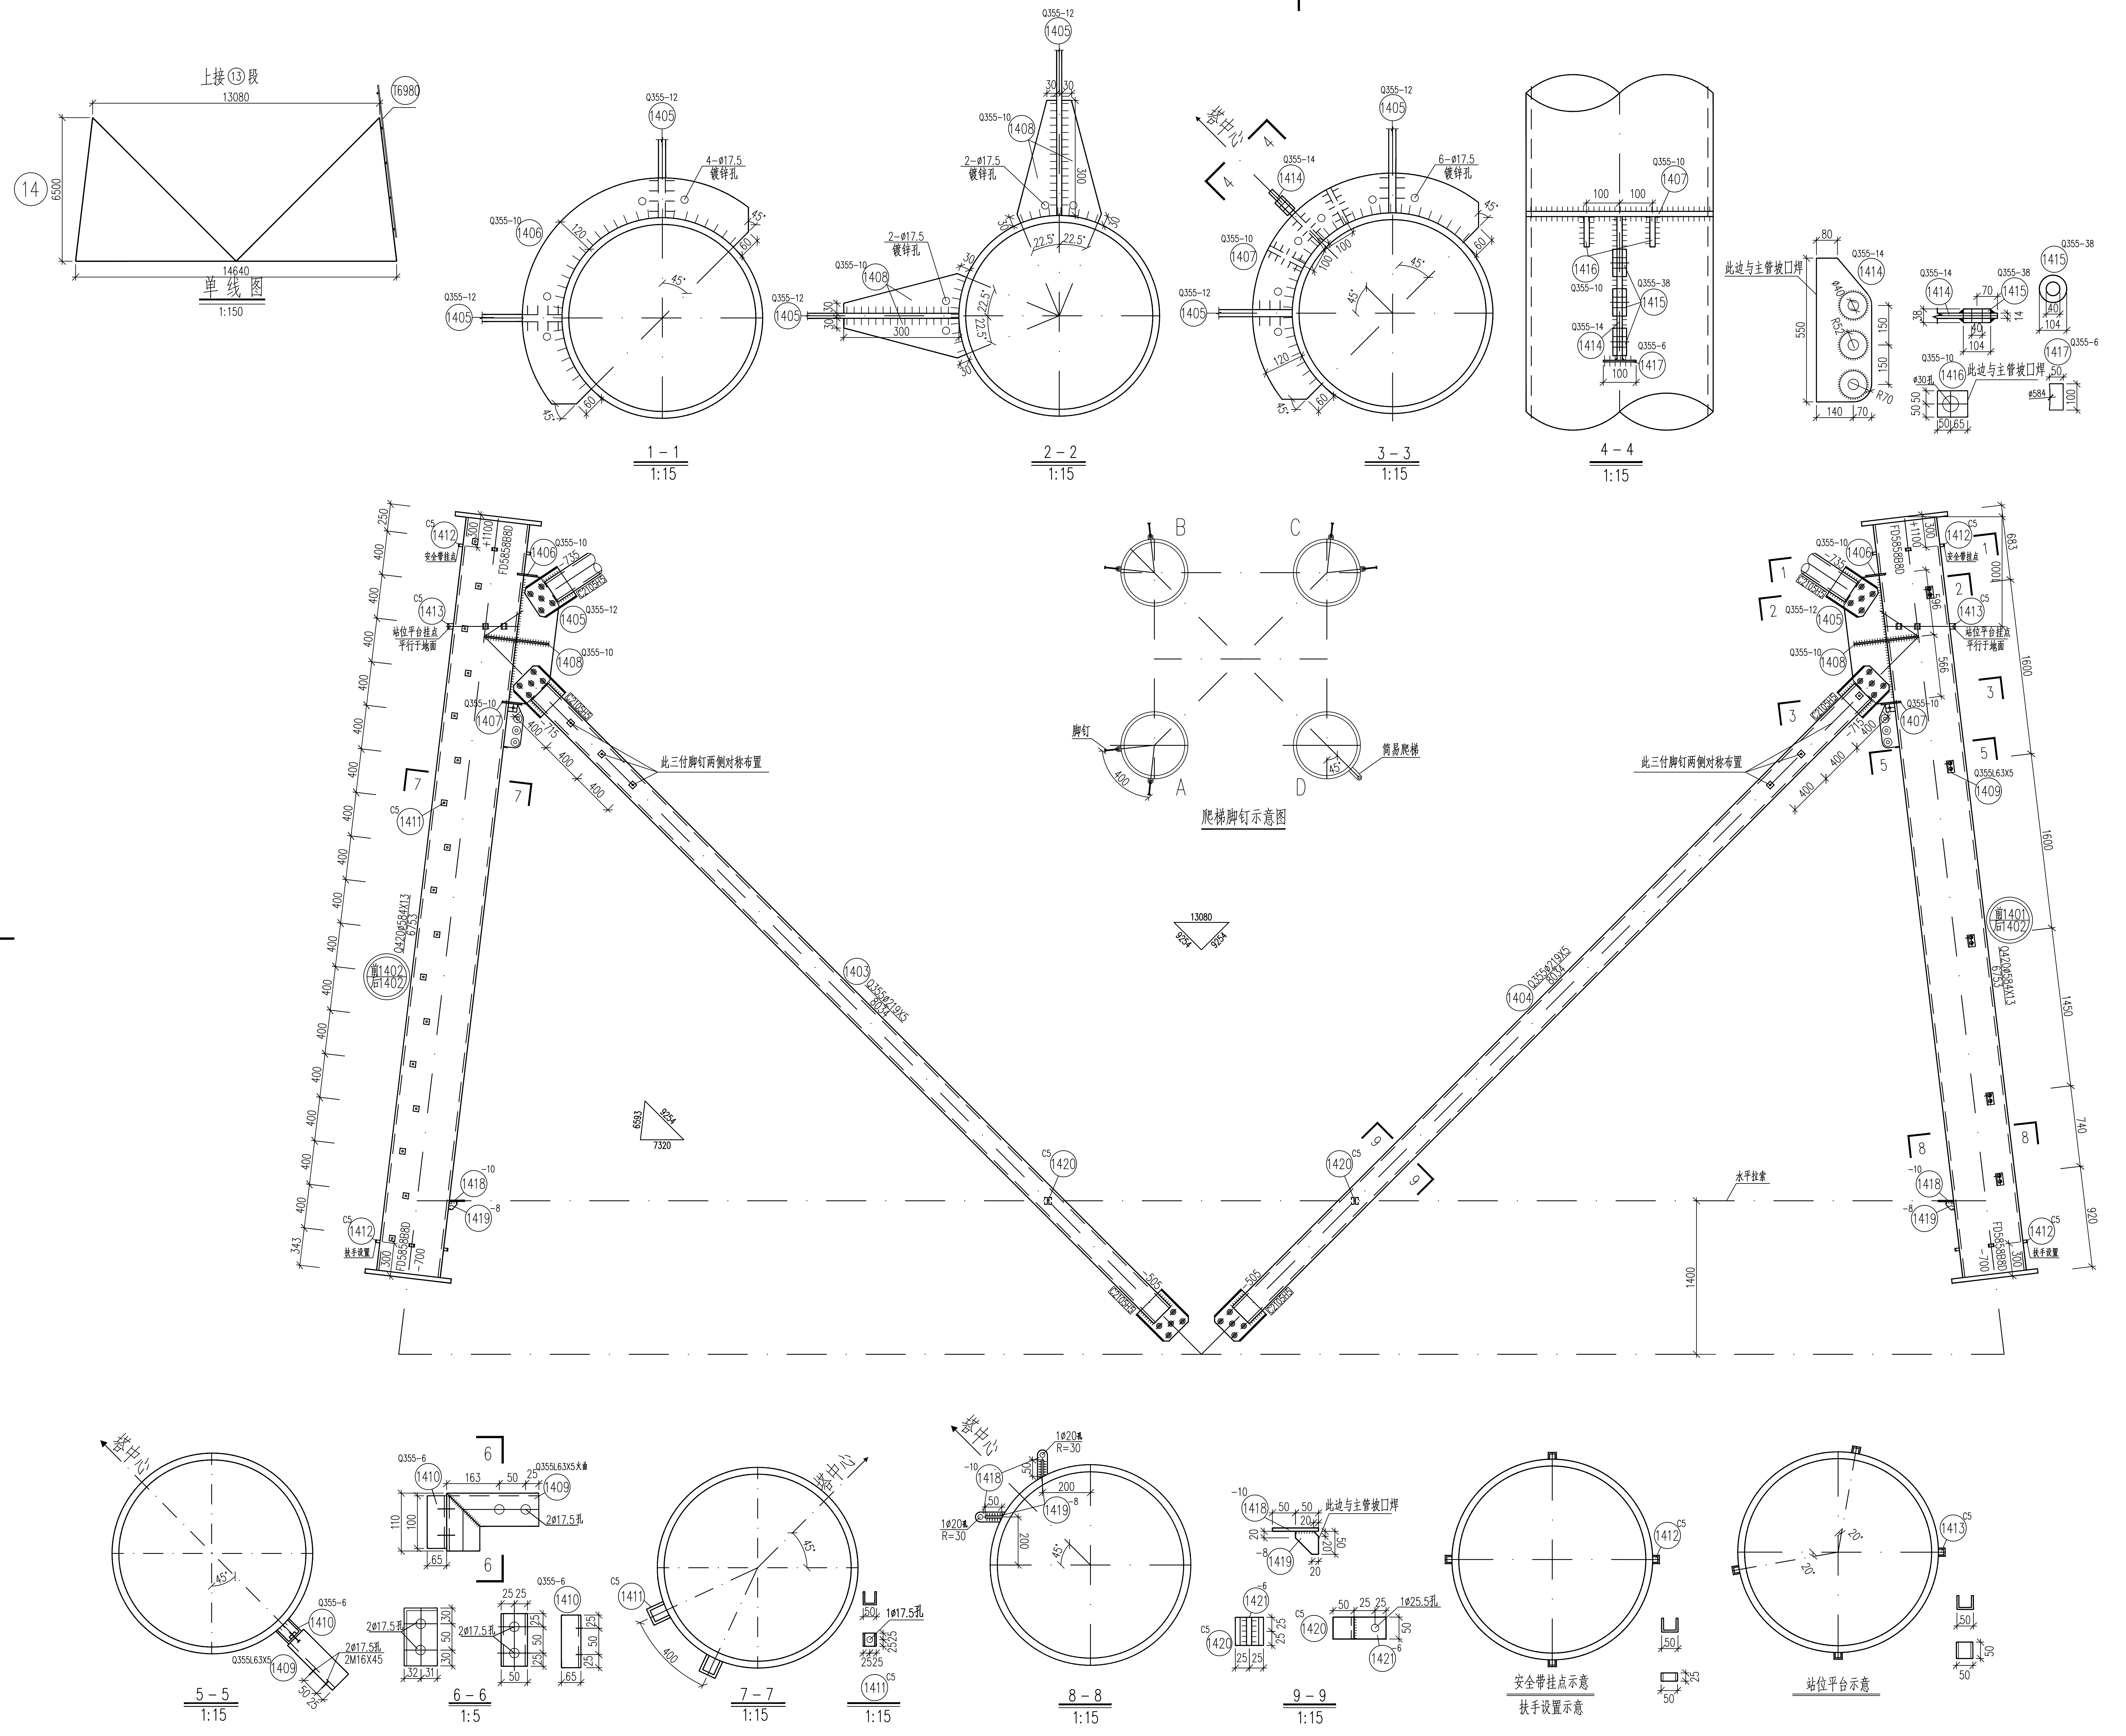

构 件 明 细 表

编号	规 格	长 度 (mm)	数量	重 量(kg) 一 件	小 计	备 注
1401	Q420ø584X13	6753	1	1236.22	1236.2	装爬梯
1402	Q420ø584X13	6753	3	1236.22	3708.7	带脚钉
1403	Q355ø219X5	8034	4	212.00	848.0	带脚钉
1404	Q355ø219X5	8034	4	212.00	848.0	带脚钉
1405	Q355-12X390	1234	8	45.33	362.6	
1406	Q355-10X120	1217	4	11.46	45.8	
1407	Q355-10X120	1217	4	11.46	45.8	
1408	Q355-10X123	330	16	3.19	51.0	
1409	Q355L63X5	348	5	1.68	8.4	火曲
1410	Q355-6X100	180	5	0.85	4.2	火曲
1411	C5	50	102	0.27	27.5	槽钢
1412	C5	25	32	0.14	4.5	槽钢
1413	C5	50	16	0.27	4.3	槽钢
1414	Q355-14X210	550	4	12.69	50.8	
1415	Q355-38X104	104	12	3.23	38.8	
1416	Q355-10X100	115	8	0.90	7.2	
1417	Q355-6X50	100	4	0.24	1.0	
1418	-10X60	92	8	0.43	3.4	拉索附件
1419	-8X50	50	8	0.16	1.3	拉索附件 切角
1420	C5	50	8	0.27	2.2	拉索附件 槽钢
1421	-6X50	50	8	0.12	1.0	拉索附件
	GJ-50	14400	4	6.05	24.2	拉索附件
	NUT-2		4	3.20	12.8	拉索附件
	U-10		4	0.60	2.4	拉索附件
	NX-2.1		4	2.40	9.6	拉索附件
	JK-2		8	0.32	2.6	拉索附件
	C2105H5		16	14.54	232.6	
	FD5858B8D		8	105.0	840.0	
	T6980	-	1	36.20	36.2	主材安装爬梯
合 计		8461.1 kg				

螺栓、脚钉、垫圈明细表

名称	级别	规 格	符 号	数量	重量(kg)	备 注
螺栓	6.8级	M16X45	◍	20	3.4	
	8.8级	M24X75	⊘	80	47.4	
		M39X180	○	104	374.2	法兰螺栓
脚钉	6.8级	M16X185	⊖ ⊣	102	42.3	
垫圈	Q235		规格X个数			
合 计			467.3 kg			

山东电力工程咨询院有限公司				浙江特高压交流环网工程线路 工程	施工图	设计阶段
批 准		校 核	马一丹	SZK31102A双回路直线塔 身部结构图 ⑭		
审 核	高锡鹏					
		设计/勘测	潘胜光			
比 例	1:30	日 期	2026年 08月	图 号 37-SA36901S-T0121-033	版本	