






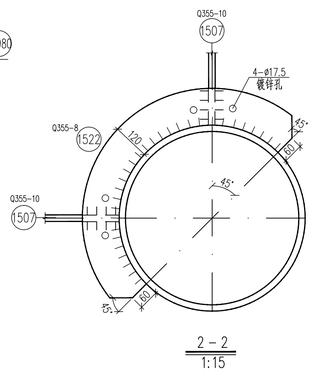


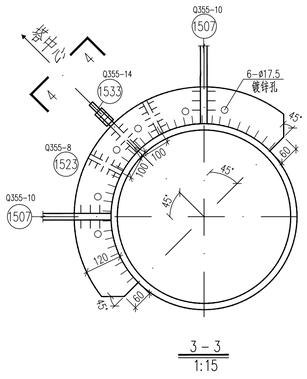


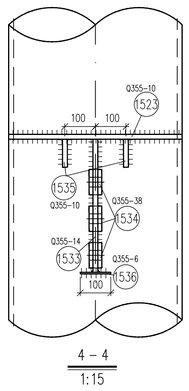

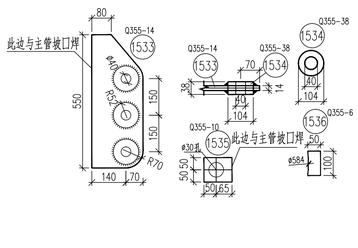

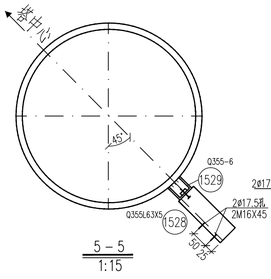

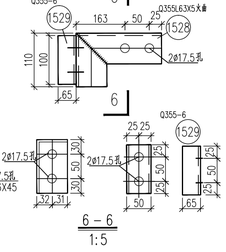

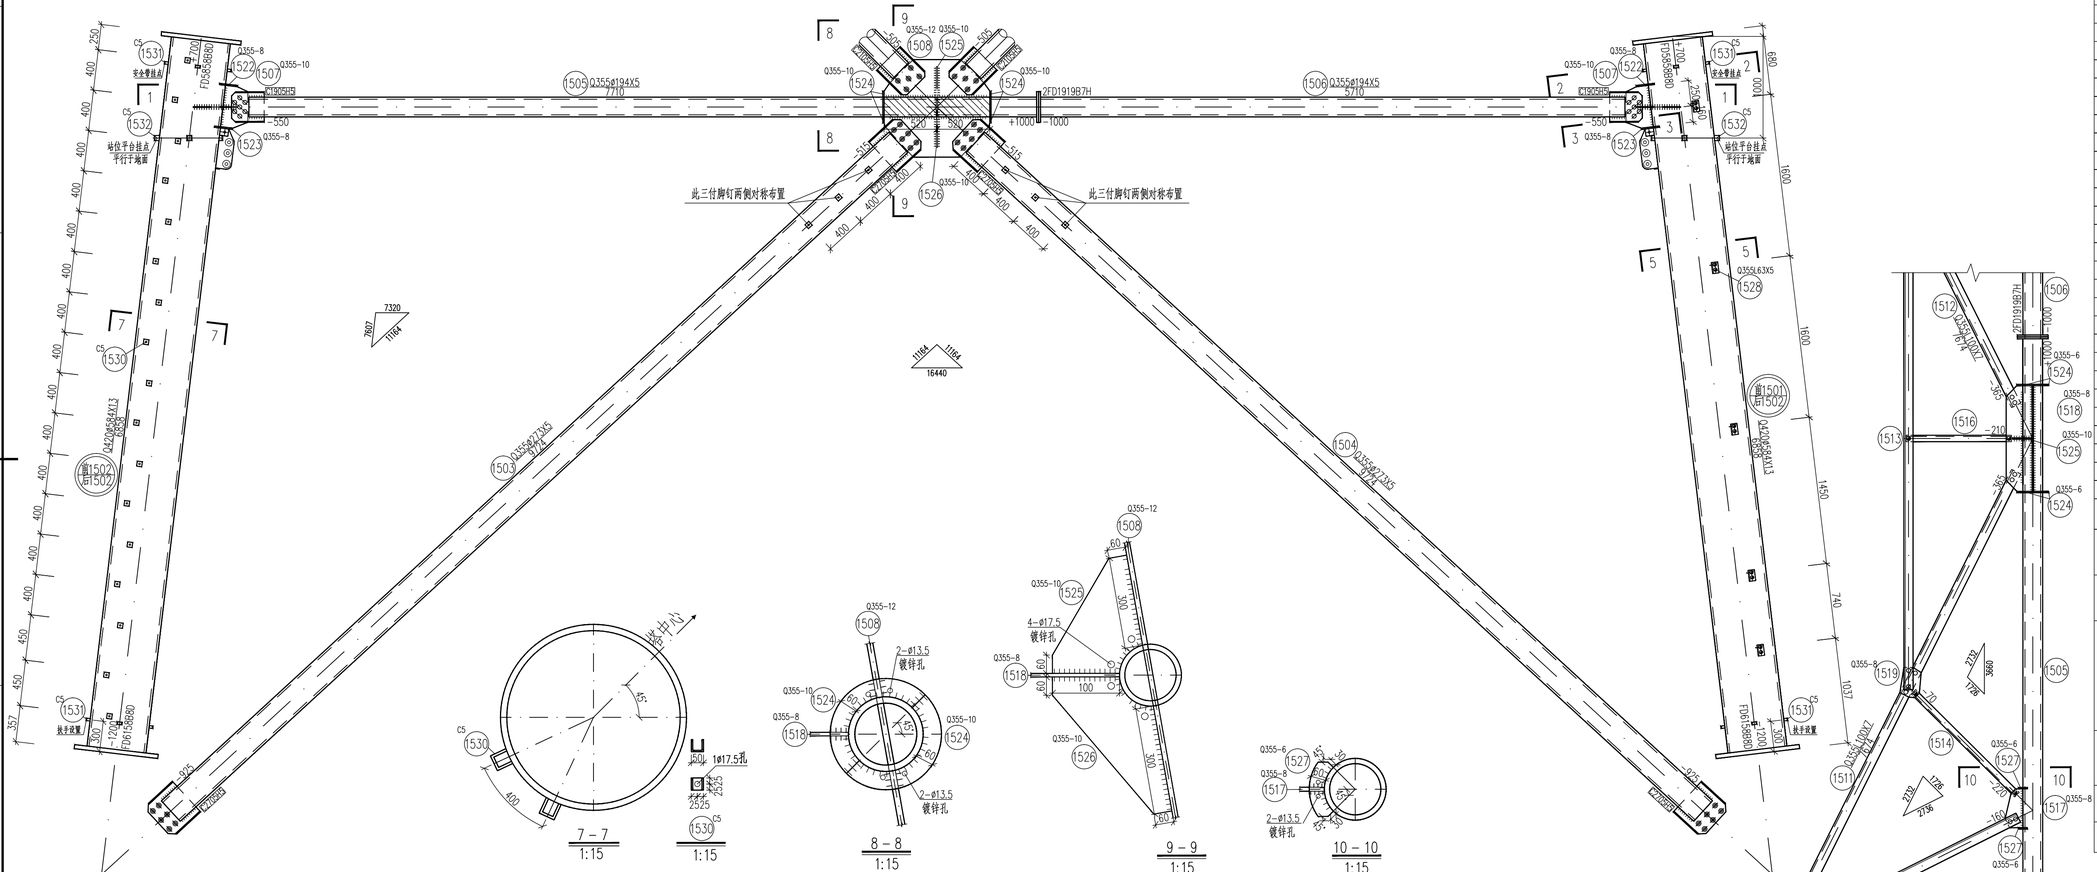

构件明细表

编号	规格	长度(mm)	数量	重量(kg) 一件	重量(kg) 小计	备注
1501	Q420ø584X13	6858	1	1255.44	1255.4	装爬梯
1502	Q420ø584X13	6858	3	1255.44	3766.3	带脚钉
1503	Q355ø273X5	9724	4	321.34	1285.4	带脚钉
1504	Q355ø273X5	9724	4	321.34	1285.4	带脚钉
1505	Q355ø194X5	7710	4	179.68	718.7	
1506	Q355ø194X5	5710	4	133.07	532.3	
1507	Q355-10X289	451	8	10.23	81.8	
1508	Q355-12X407	1066	4	40.87	163.5	
1509	Q355L100X7	7674	2	83.16	166.3	
1510	Q355L100X7	7674	2	83.16	166.3	
1511	Q355L100X7	7674	2	83.16	166.3	
1512	Q355L100X7	7674	2	83.16	166.3	
1513	Q355L90X7	4945	4	47.75	191.0	
1514	L50X4	1436	8	4.39	35.1	
1515	Q355L90X7	3054	4	29.49	118.0	
1516	L45X4	1038	4	2.84	11.4	
1517	Q355-8X196	421	8	5.18	41.4	
1518	Q355-8X185	1040	4	12.08	48.3	
1519	Q355-8X231	328	8	4.76	38.1	
1520	Q355-8X370	373	4	8.67	34.7	
1521	Q355-8X246	586	4	9.05	36.2	
1522	Q355-8X120	1217	4	9.17	36.7	
1523	Q355-8X120	1217	4	9.17	36.7	
1524	Q355-10X60	439	16	2.07	33.1	
1525	Q355-10X191	430	4	6.45	25.8	
1526	Q355-10X191	430	4	6.45	25.8	
1527	Q355-6X60	219	16	0.62	9.9	
1528	Q355L63X5	348	5	1.68	8.4	火曲
1529	Q355-6X100	180	5	0.85	4.2	火曲
1530	C5	50	102	0.27	27.5	槽钢
1531	C5	25	32	0.14	4.5	槽钢
1532	C5	50	16	0.27	4.3	槽钢
1533	Q355-14X210	550	4	12.69	50.8	
1534	Q355-38X104	104	12	3.23	38.8	
1535	Q355-10X100	115	8	0.90	7.2	
1536	Q355-6X50	100	4	0.24	1.0	
	C1905H5		8	8.84	70.7	
	C2705H5		16	18.20	291.2	
	FD1919B7H		8	8.1	64.8	
	FD5858B8D		4	105.0	420.0	
	FD6158B8D		4	127.0	508.0	
	T6980	–	1	36.20	36.2	主材安装爬梯
合计				12013.8 kg		

螺栓、脚钉、垫圈明细表

名称	级别	规格	符号	数量	重量(kg)	备注
螺栓	6.8级	M16X45	◪	44	7.4	
		M20X55	○	88	28.8	
		M20X65	∅	68	24.0	
	8.8级	M24X75	⊘	88	52.2	
		M20X90	○	48	22.7	法兰螺栓
		M39X180	○	104	374.2	法兰螺栓
脚钉	6.8级	M16X185	⊣	102	42.3	
垫圈	Q235		规格X个数			
合计				551.6 kg		

山东电力工程咨询院有限公司

浙江特高压交流环网工程线路 工程 施工图 设计阶段

批准		校核	
审核		设计/勘测	
比例	1:30	日期	2026年08月

SZK31102A双回路直线塔 身部结构图 (15)

图号 37-SA36901S-T0121- 034 版本