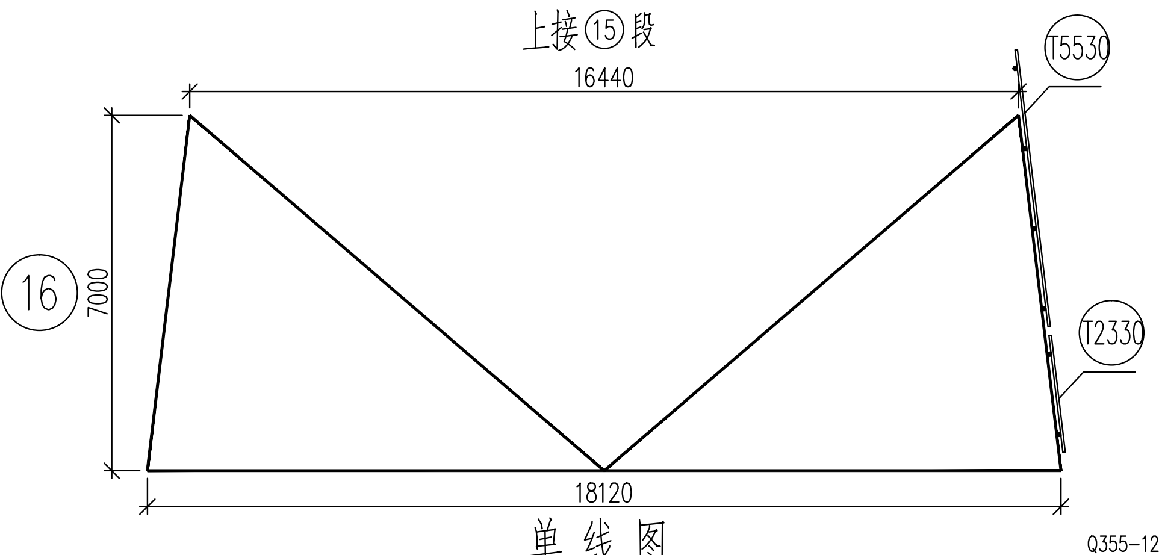
上接⑮段
16440
T5530
16
7000
T2330
18120

单线图
1:150

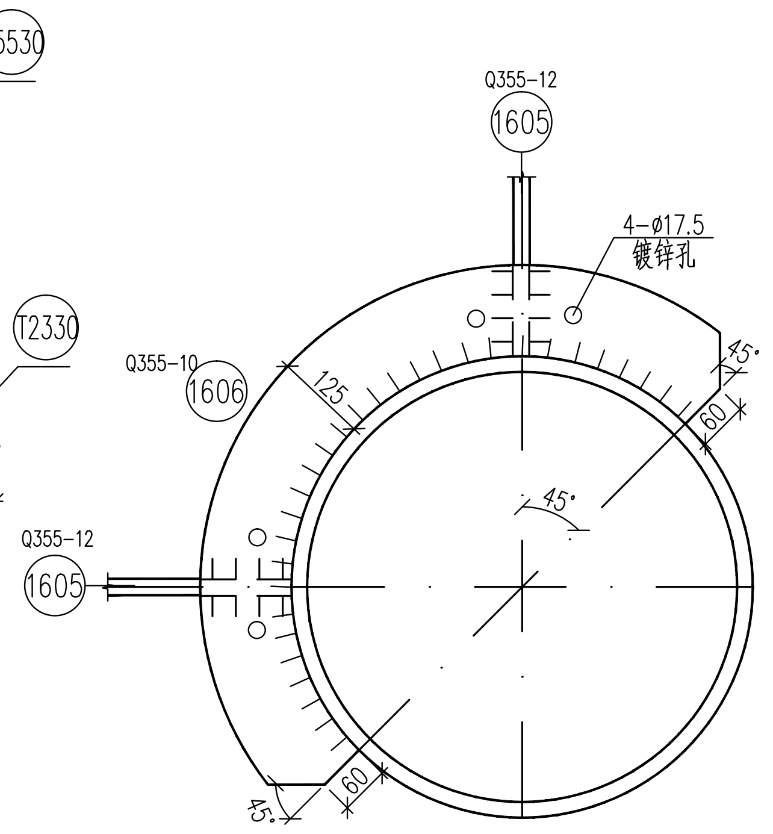
Q355-12
1605
4-ø17.5
镀锌孔
Q355-10
1606
45°
Q355-12
1605

1-1
1:15

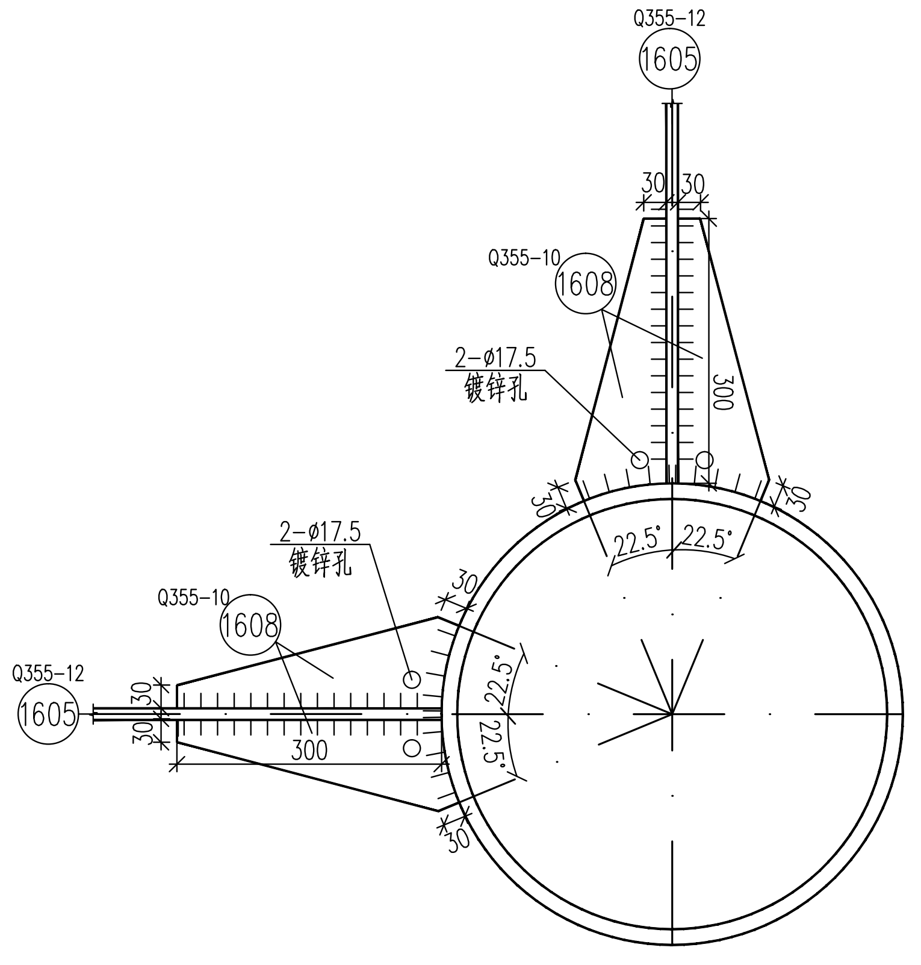
Q355-12
1605
Q355-10
1608
2-ø17.5
镀锌孔
2-ø17.5
镀锌孔
Q355-10
1608
Q355-12
1605
22.5°
300

2-2
1:15

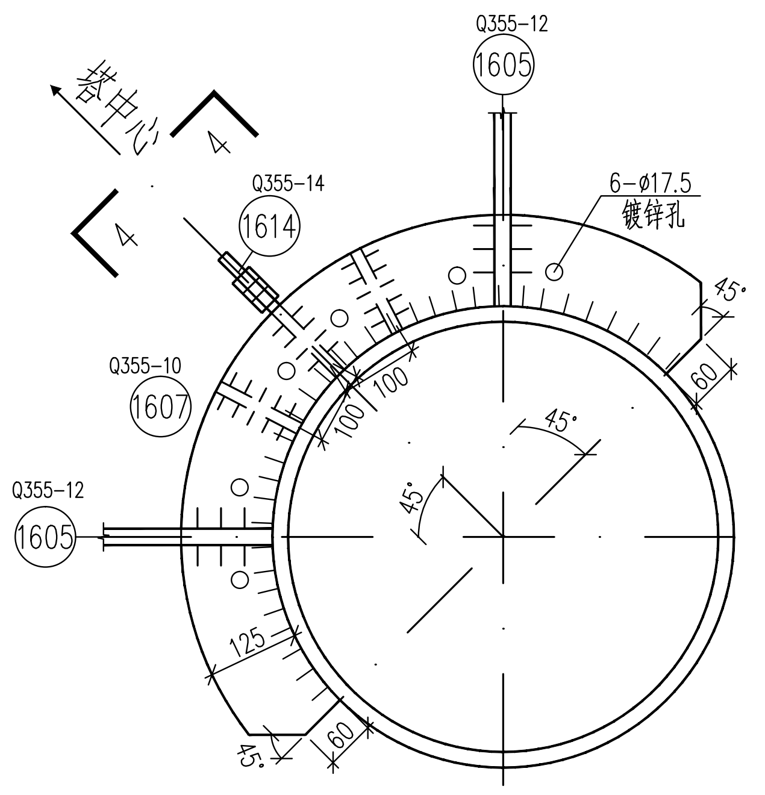
塔中心
4
Q355-12
1605
Q355-14
1614
6-ø17.5
镀锌孔
Q355-10
1607
Q355-12
1605
45°

3-3
1:15

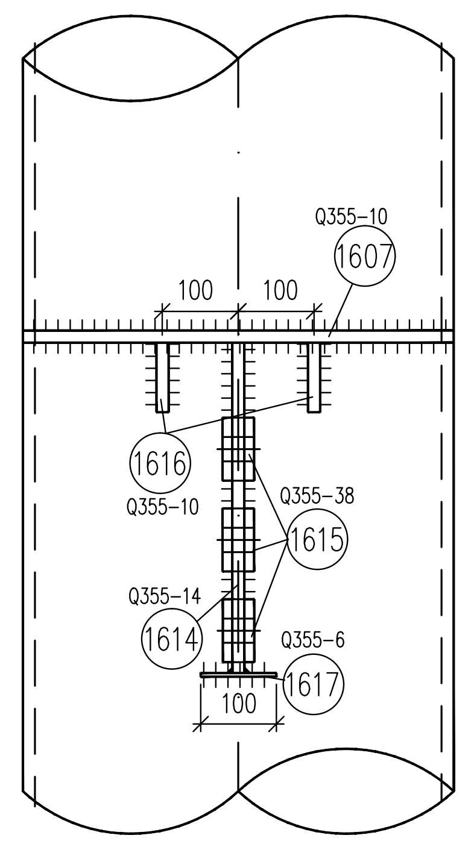
Q355-10
1607
100
1616
Q355-10
1615
Q355-38
Q355-14
1614
Q355-6
1617
100

4-4
1:15

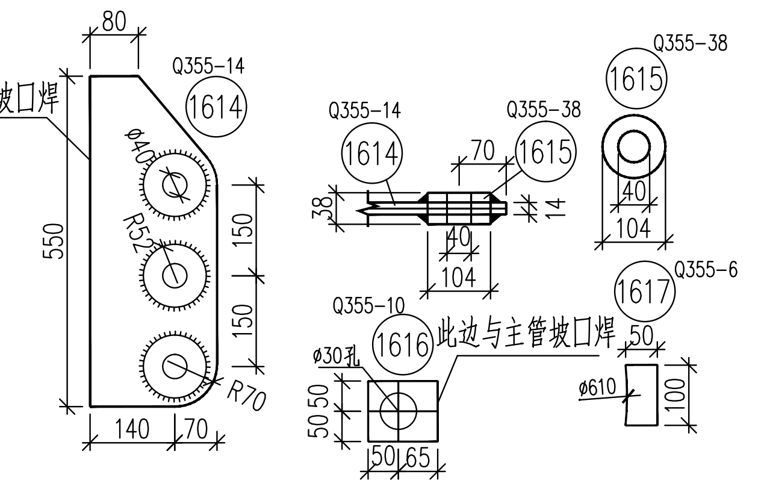
80
Q355-14
1614
此边与主管坡口焊
550
Q355-14
1614
Q355-38
1615
Q355-38
1615
Q355-6
1617
Q355-10
1616
此边与主管坡口焊
ø610
140
R70

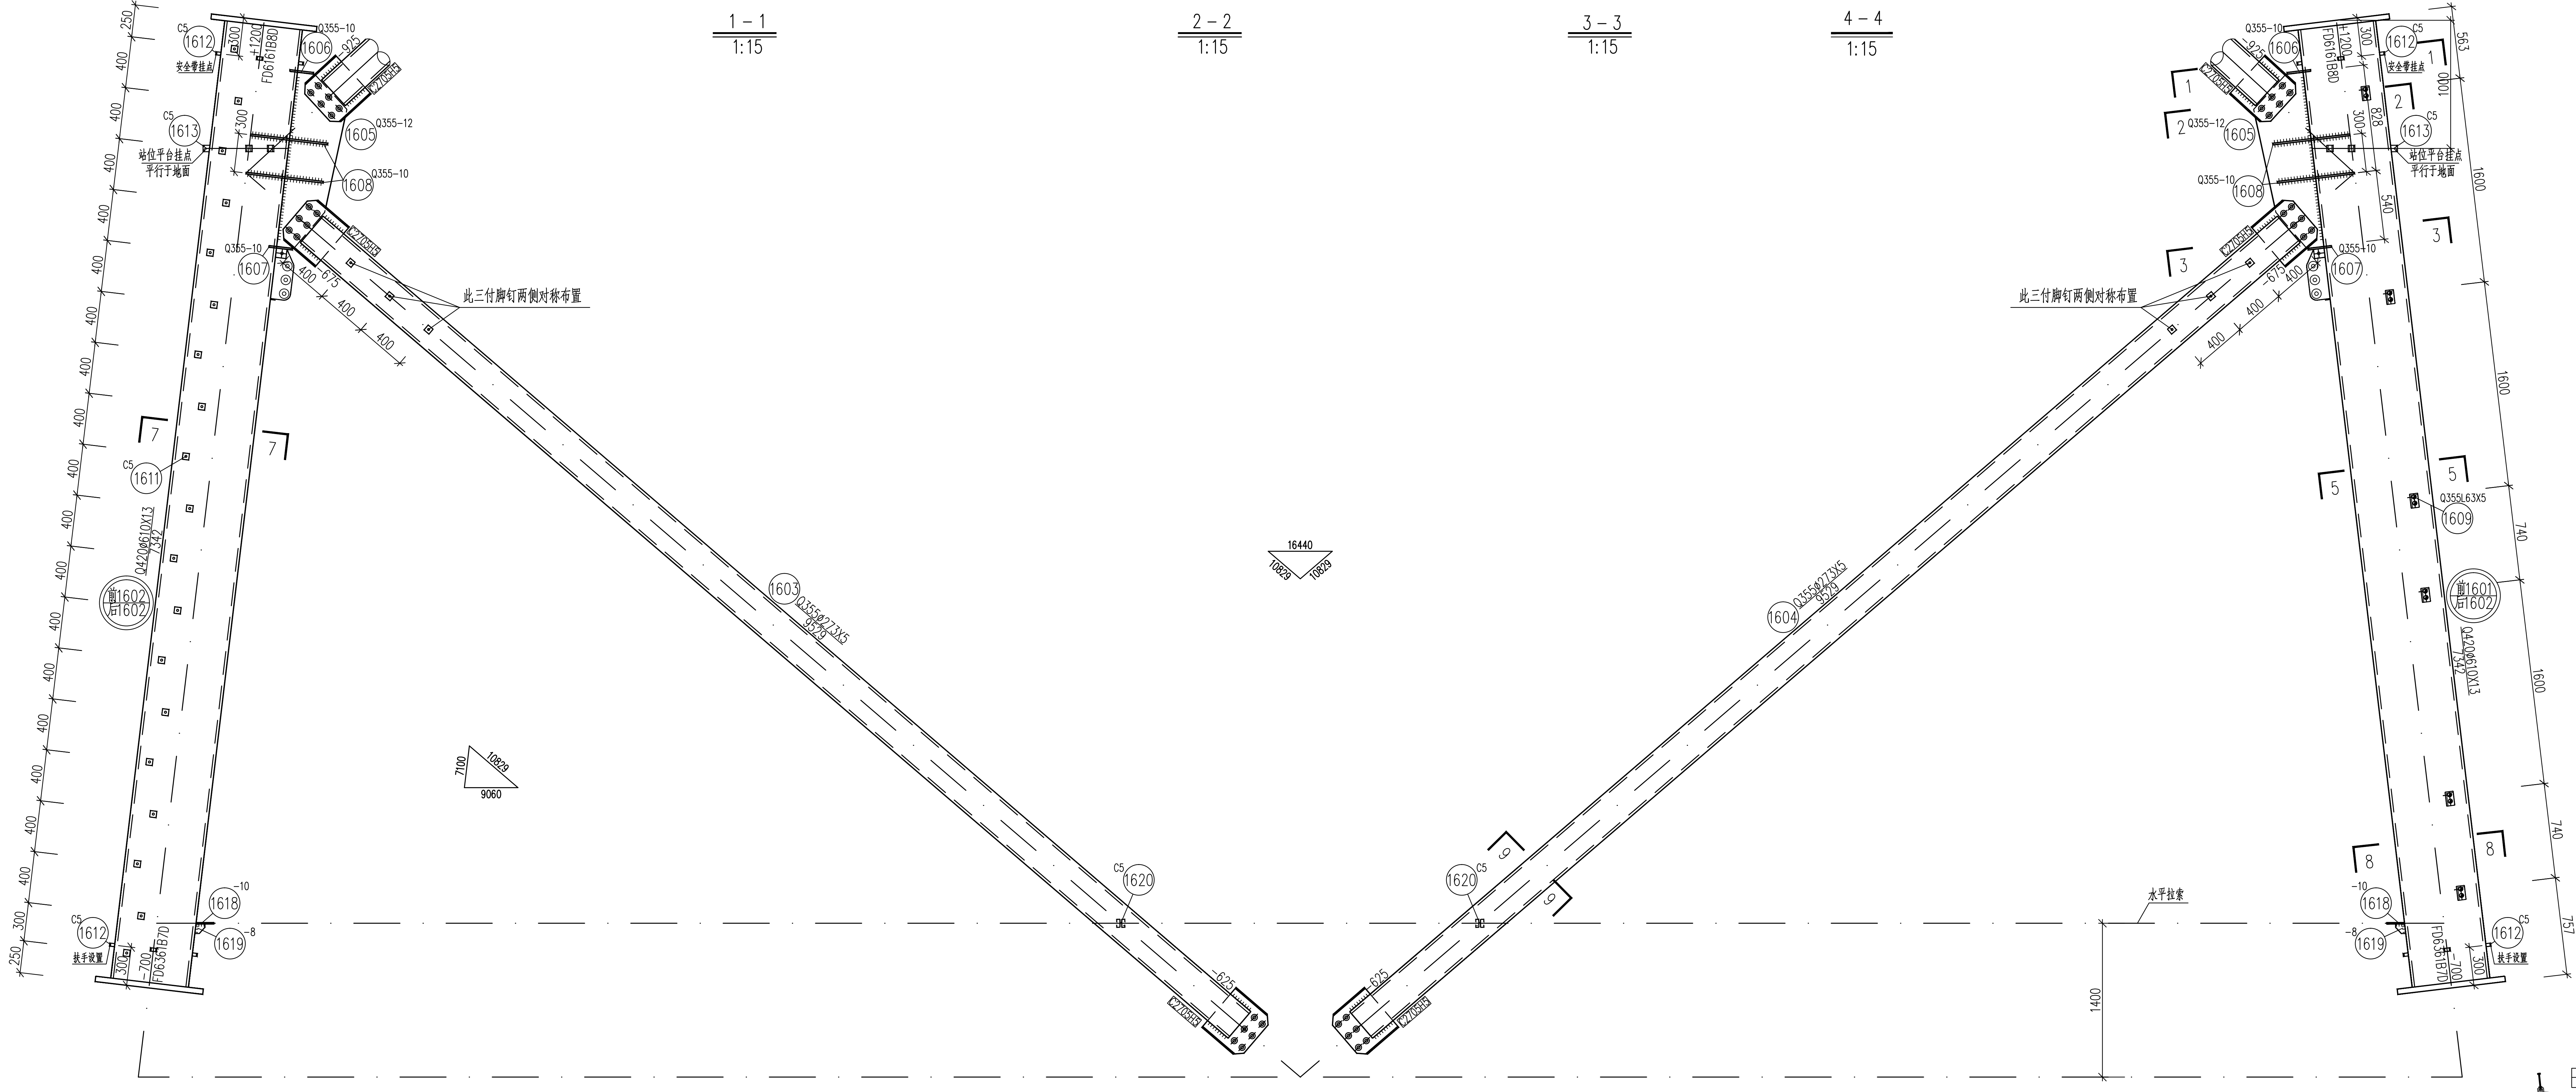
C5
1612
安全带挂点
1606
Q355-10
C5
1613
站位平台挂点
平行于地面
Q355-12
1605
1608
Q355-10
Q355-10
1607
此三付脚钉两侧对称布置
7
C5
1611
1601
1602
Q420ø610X13
7342
1603
Q355ø273X5
1604
Q355ø273X5
16440
7100
10829
9060
C5
1620
1618
1619
扶手设置
水平拉索
1400
3
5
6
8
1609
Q355L63X5
FD6161B8D
FD6361B7D
1600
740

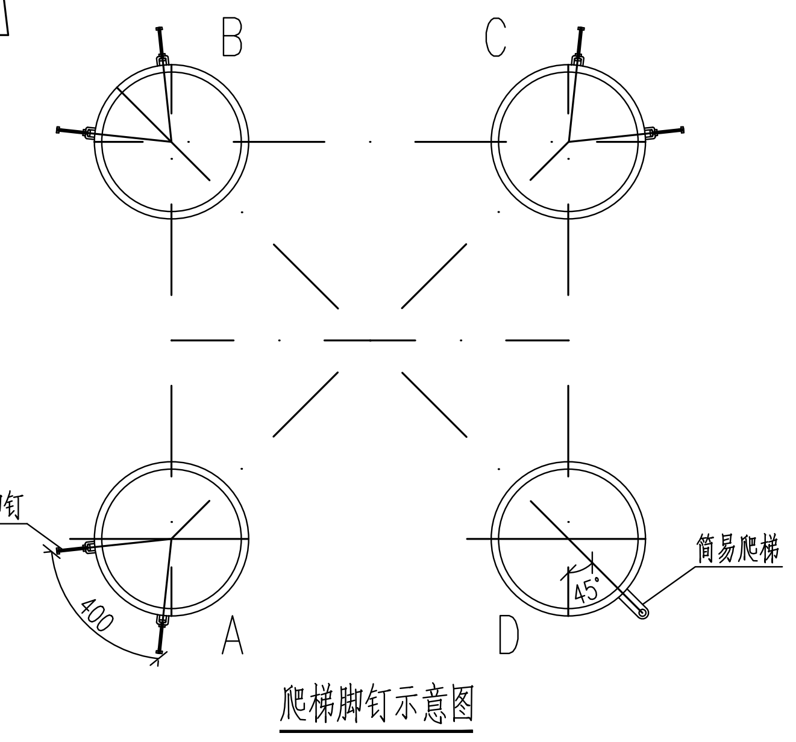
B
C
A
D
脚钉
爬梯
45°
400

爬梯脚钉示意图

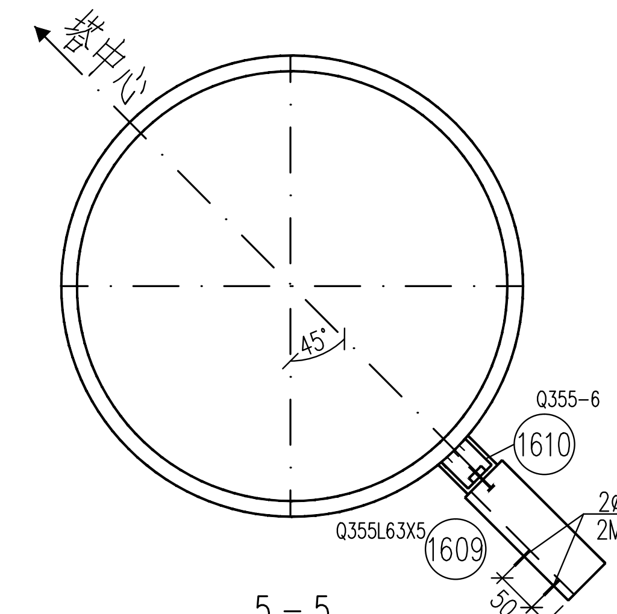
塔中心
45°
Q355-6
1610
Q355L63X5
1609
2ø17.5孔
2M16X45

5-5
1:15

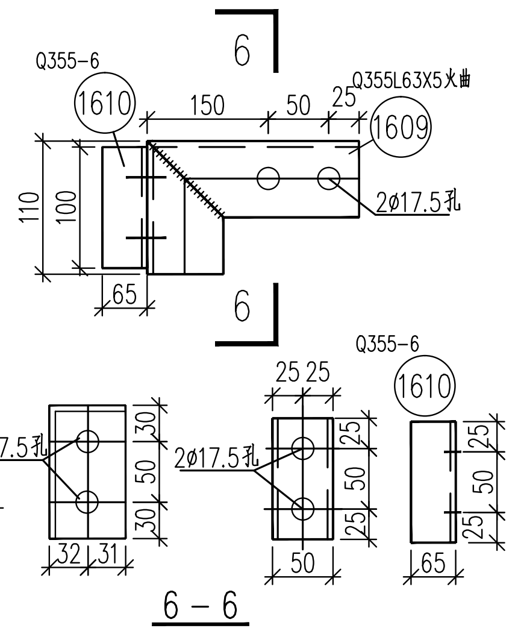
Q355-6
1610
150
Q355L63X5火曲
1609
2ø17.5孔
6
6
2ø17.5孔
Q355-6
1610

6-6
1:5

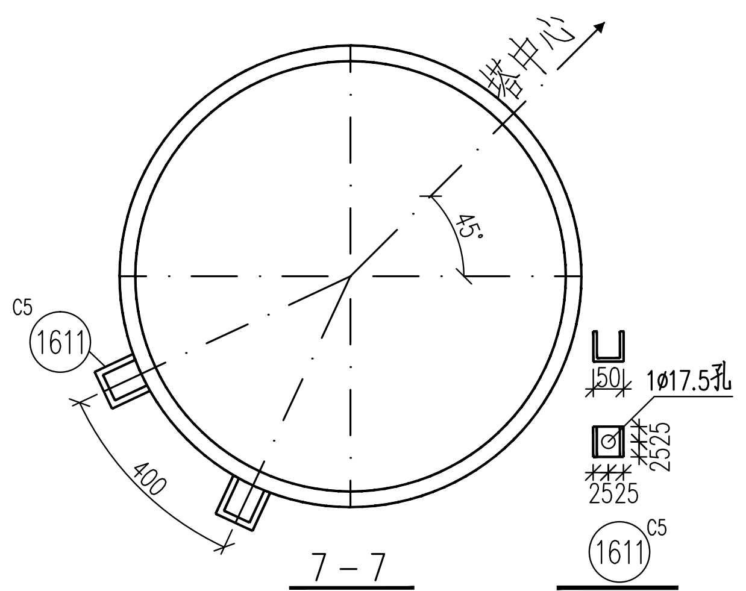
塔中心
45°
C5
1611
400

7-7
1:15

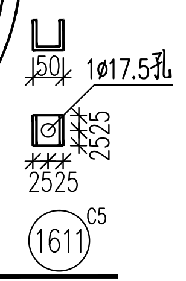
1ø17.5孔
1611
C5

1:15

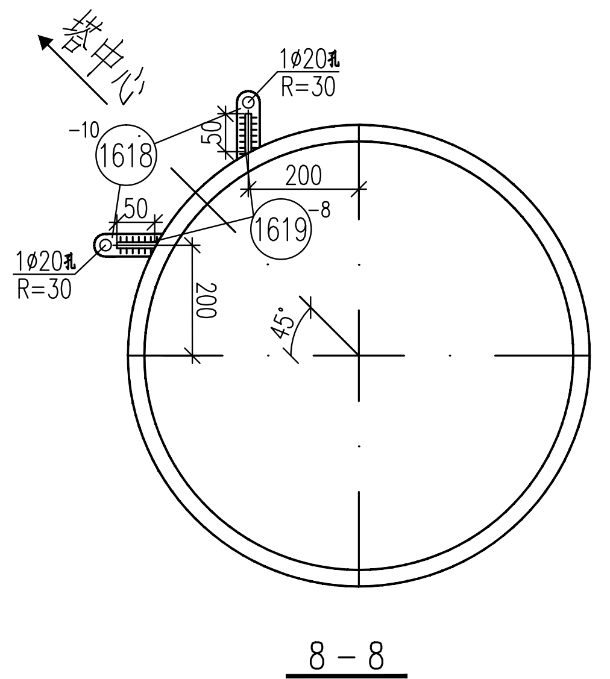
塔中心
1ø20
R=30
-10
1618
-8
1619
200
1ø20
R=30
45°

8-8
1:15

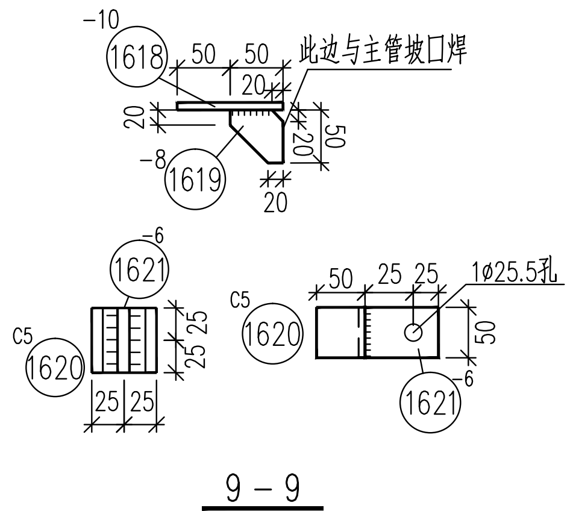
-10
1618
此边与主管坡口焊
-8
1619
-6
1621
C5
1620
C5
1620
1ø25.5孔
1621

9-9
1:15

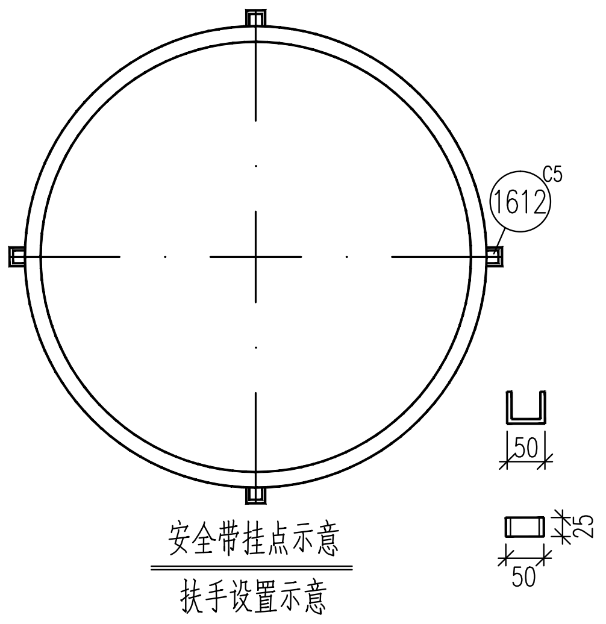

安全带挂点示意

扶手设置示意

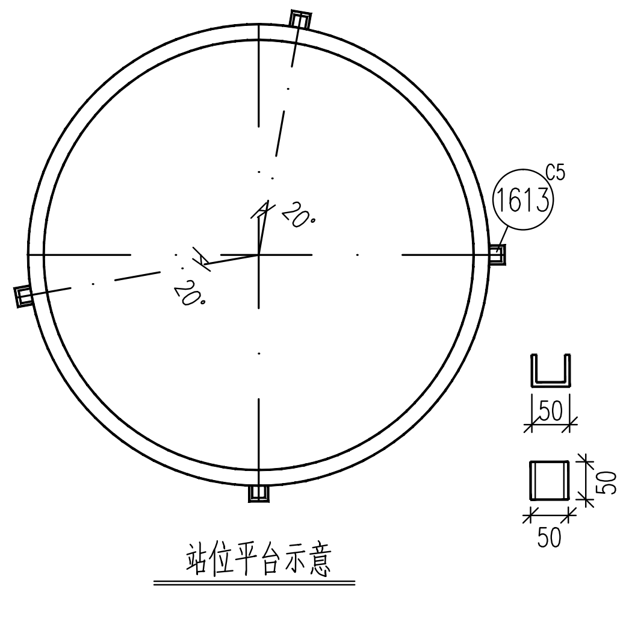

站位平台示意

构　件　明　细　表

编号	规　格	长度(mm)	数量	重量(kg) 一件	重量(kg) 小计	备　注
1601	Q420ø610X13	7342	1	1405.24	1405.2	装爬梯
1602	Q420ø610X13	7342	3	1405.24	4215.7	带脚钉
1603	Q355ø273X5	9529	4	314.90	1259.6	带脚钉
1604	Q355ø273X5	9529	4	314.90	1259.6	带脚钉
1605	Q355-12X457	1442	8	62.08	496.6	
1606	Q355-10X125	1271	4	12.47	49.9	
1607	Q355-10X125	1271	4	12.47	49.9	
1608	Q355-8X128	330	32	2.65	84.8	
1609	Q355L63X5	335	6	1.62	9.7	火曲
1610	Q355-6X100	180	6	0.85	5.1	火曲
1611	C5	50	108	0.27	29.2	槽钢
1612	C5	25	32	0.14	4.5	槽钢
1613	C5	50	16	0.27	4.3	槽钢
1614	Q355-14X210	550	4	12.69	50.8	
1615	Q355-38X104	104	12	3.23	38.8	
1616	Q355-10X100	115	8	0.90	7.2	
1617	Q355-6X50	100	4	0.24	1.0	
1618	-10X60	92	8	0.43	3.4	拉索附件
1619	-8X50	50	8	0.16	1.3	拉索附件 切角
1620	C5	50	8	0.27	2.2	拉索附件 槽钢
1621	-6X50	50	8	0.12	1.0	拉索附件
	GJ-50	17900	4	7.52	30.1	拉索附件
	NUT-2		4	3.20	12.8	拉索附件
	U-10		4	0.60	2.4	拉索附件
	NX-2.1		4	2.40	9.6	拉索附件
	JK-2		8	0.32	2.6	拉索附件
	C2705H5		16	18.20	291.2	
	FD6161B8D		4	120.0	480.0	
	FD6361B7D		4	111.2	444.8	
	T2330	–	1	12.40	12.4	主材安装爬梯
	T5530	–	1	28.80	28.8	主材安装爬梯
合　计		10294.5 kg				

螺栓、脚钉、垫圈明细表

名称	级别	规　格	符　号	数量	重量(kg)	备　注
螺栓	6.8级	M16X45	◎	24	4.0	
	8.8级	M24X75	⌀	96	56.9	
		M45X195	○	96	519.3	法兰螺栓
脚钉	6.8级	M16X185	⊖ ⊣	108	44.8	
垫圈	Q235		规格X个数			
合　计			625.0 kg			

山东电力工程咨询院有限公司

浙江特高压交流环网工程线路 工程				施工图	设计阶段
批　准		校　核		SZK31102A双回路直线塔 身部结构图	⑯
审　核	高锡鹏				
		设计/勘测			
比　例	1:30	日　期	2026年 08月	图　号 37-SA36901S-T0121- 035	版本