





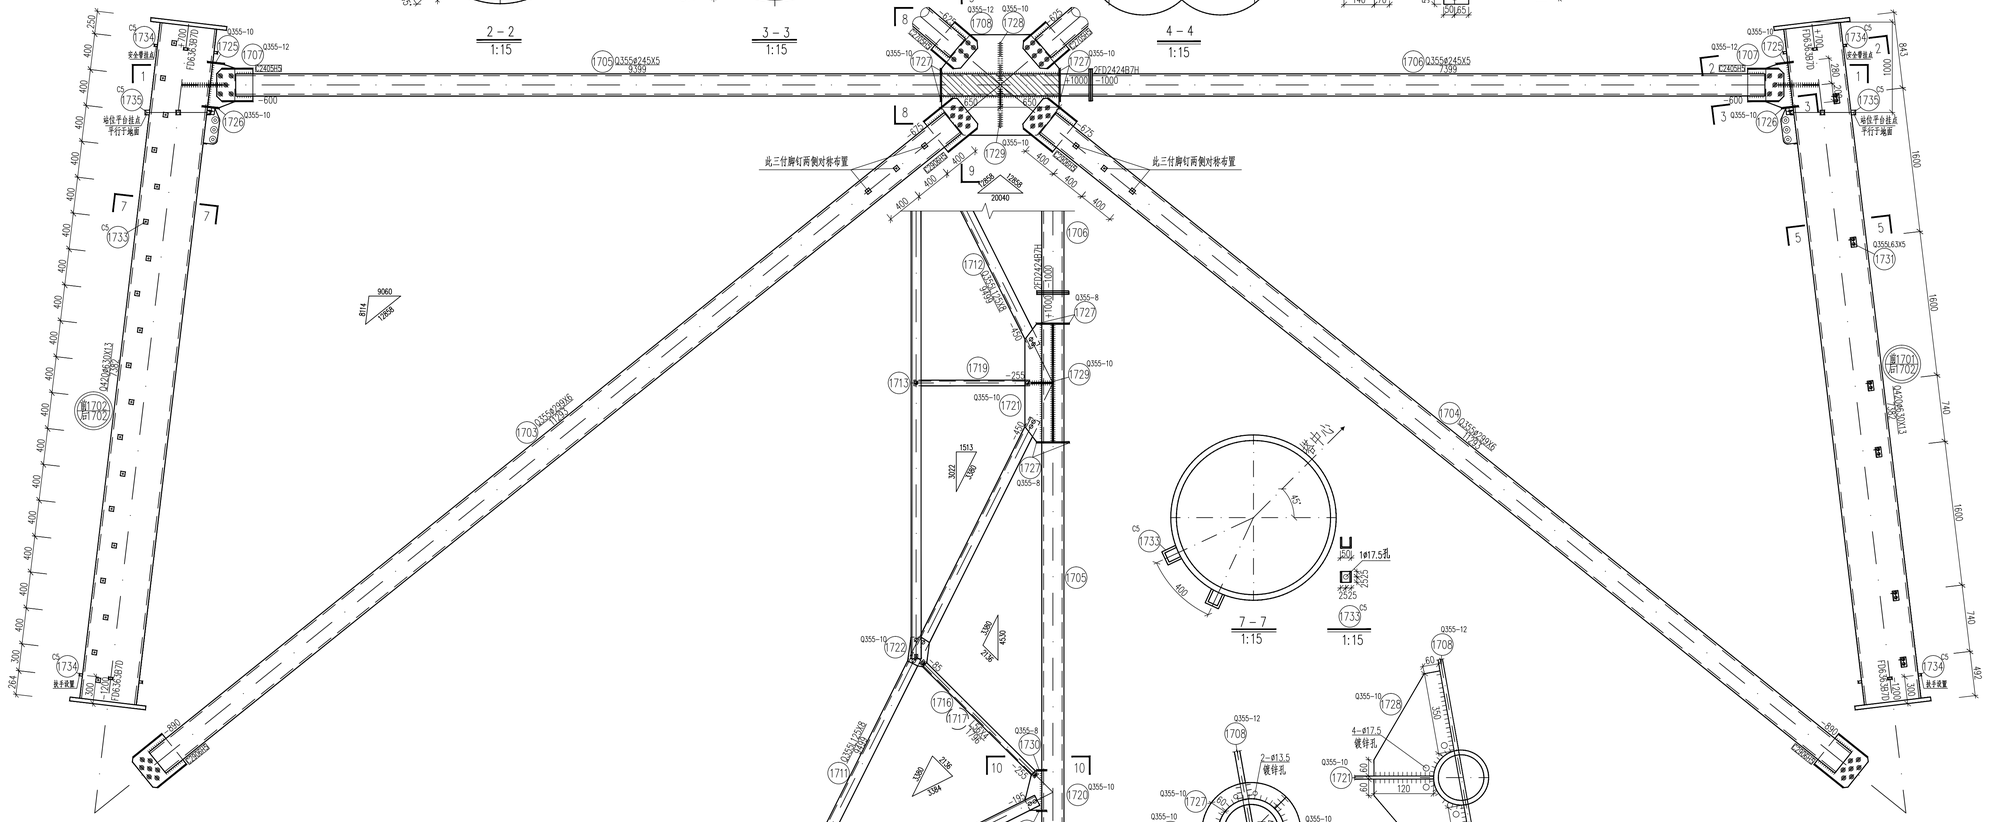

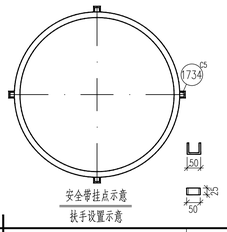

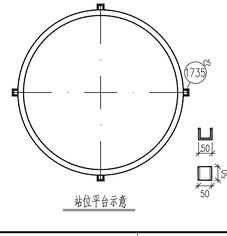

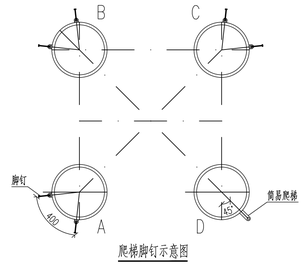

爬梯脚钉示意图

构 件 明 细 表

编号	规 格	长度(mm)	数量	重量(kg) 一件	重量(kg) 小计	备 注
1701	Q420ø630X13	7382	1	1460.23	1460.2	装爬梯
1702	Q420ø630X13	7382	3	1460.23	4380.7	带脚钉
1703	Q355ø299X6	11293	4	489.61	1958.4	带脚钉
1704	Q355ø299X6	11293	4	489.61	1958.4	带脚钉
1705	Q355ø245X5	9399	4	278.15	1112.6	
1706	Q355ø245X5	7399	4	218.96	875.8	
1707	Q355-12X319	528	8	15.87	127.0	
1708	Q355-12X1300	1113	4	136.30	545.2	
1709	Q355L125X8	9499	2	147.27	294.5	
1710	Q355L125X8	9499	2	147.27	294.5	
1711	Q355L125X8	9499	2	147.27	294.5	
1712	Q355L125X8	9499	2	147.27	294.5	
1713	Q355L110X8	6105	4	82.62	330.5	
1714	L56X4	1796	2	6.19	12.4	
1715	L56X4	1796	2	6.19	12.4	
1716	L56X4	1796	2	6.19	12.4	
1717	L56X4	1796	2	6.19	12.4	
1718	Q355L110X8	3830	4	51.83	207.3	
1719	L45X4	1283	4	3.51	14.0	
1720	Q355-10X206	480	8	7.76	62.1	
1721	Q355-10X206	1300	4	21.02	84.1	
1722	Q355-10X262	361	8	7.42	59.4	
1723	Q355-10X418	419	4	13.75	55.0	
1724	Q355-10X255	638	4	12.77	51.1	
1725	Q355-10X130	1313	4	13.40	53.6	
1726	Q355-10X130	1313	4	13.40	53.6	
1727	Q355-10X60	527	16	2.48	39.7	
1728	Q355-10X257	514	4	10.37	41.5	
1729	Q355-10X257	514	4	10.37	41.5	
1730	Q355-8X60	264	16	0.99	15.8	
1731	Q355L63X5	325	6	1.57	9.4	火曲
1732	Q355-6X100	180	6	0.85	5.1	火曲
1733	C5	50	108	0.27	29.2	槽钢
1734	C5	25	32	0.14	4.5	槽钢
1735	C5	50	16	0.27	4.3	槽钢
1736	Q355-14X210	550	4	12.69	50.8	
1737	Q355-38X104	104	12	3.23	38.8	
1738	Q355-10X100	115	8	0.90	7.2	
1739	Q355-6X50	100	4	0.24	1.0	
	C2405H5		8	17.27	138.2	
	C2906H5		16	23.31	373.0	
	FD2424B7H		8	10.4	83.2	
	FD6363B7D		8	103.2	825.6	
	T2330	–	1	12.40	12.4	主材安装爬梯
	T5530	–	1	28.80	28.8	主材安装爬梯
合 计					16366.6 kg	

螺栓、脚钉、垫圈明细表

名称	级别	规 格	符号	数量	重量(kg)	备 注
螺栓	6.8级	M16X45		28	4.7	
		M16X55		20	3.7	
		M20X65		88	31.1	
		M20X75		12	4.5	
		M24X75		140	83.0	
	8.8级	M20X90		56	26.4	法兰螺栓
		M39X175		104	369.3	法兰螺栓
脚钉	6.8级	M16X185		108	44.8	
垫圈	Q235		规格X个数			
合 计					567.5 kg	

山东电力工程咨询院有限公司			浙江特高压交流环网工程线路	工程	施工图 设计阶段
批 准	曹振	校 核	刘一舟	SZK31102A双回路直线塔	17
审 核	高鹏鹏	设计/勘测	陈旭光	身部结构图	
比 例	1:30	日 期	2026年 08月	图 号	37-SA36901S-T0121-036 版本