






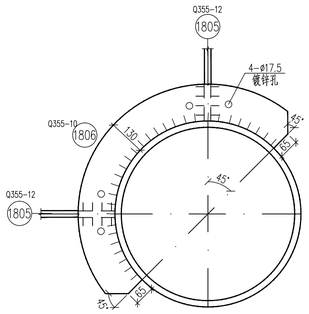


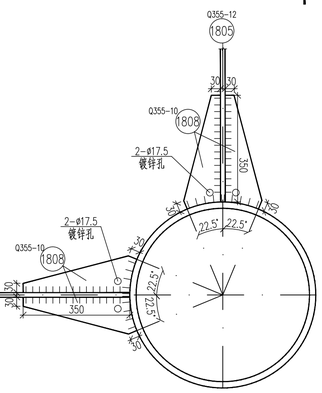

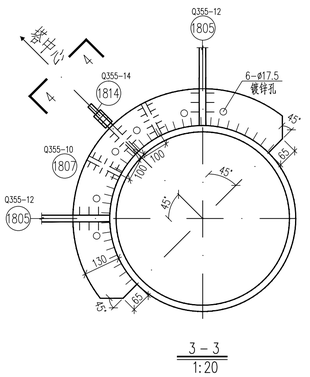

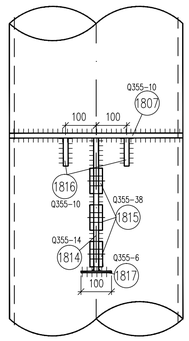

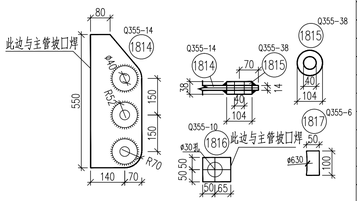

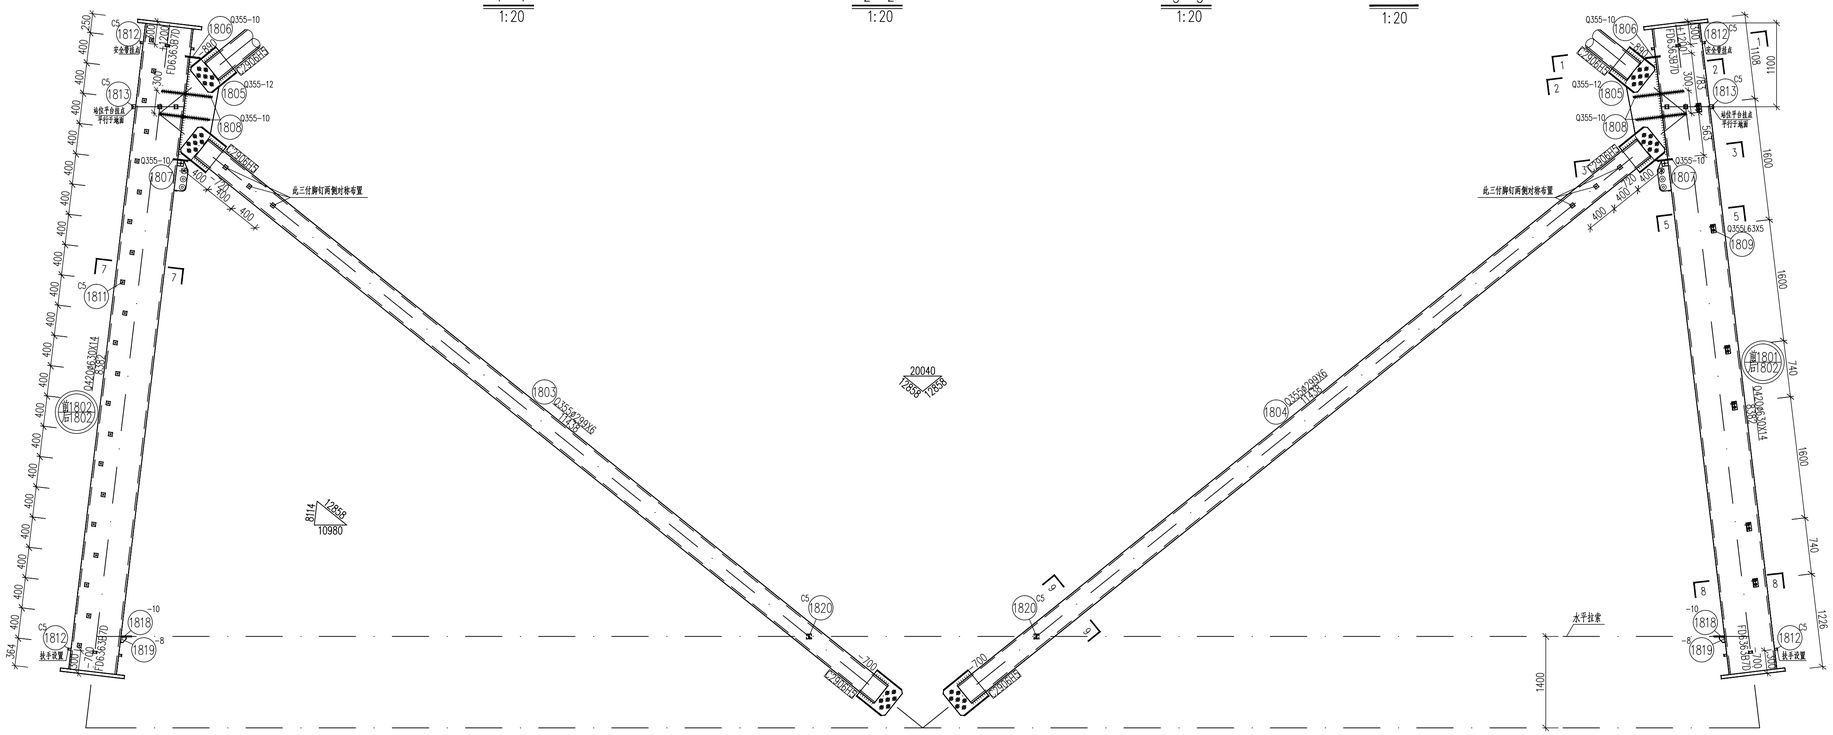



构件明细表


编号	规格	长度(mm)	数量	重量(kg) 一件	重量(kg) 小计	备注
1801	Q420ø630X14	8382	1	1782.69	1782.7	装爬梯
1802	Q420ø630X14	8382	3	1782.69	5348.1	带脚钉
1803	Q355ø299X6	11438	4	495.89	1983.6	带脚钉
1804	Q355ø299X6	11438	4	495.89	1983.6	带脚钉
1805	Q355-12X469	1411	8	62.34	498.7	
1806	Q355-10X130	1313	4	13.40	53.6	
1807	Q355-10X130	1313	4	13.40	53.6	
1808	Q355-10X148	385	32	4.47	71.5	
1809	Q355L63X5	325	6	2.24	13.4	火曲
1810	Q355-6X100	180	6	0.85	5.1	火曲
1811	C5	50	114	0.27	30.8	槽钢
1812	C5	25	32	0.14	4.5	槽钢
1813	C5	50	16	0.27	4.3	槽钢
1814	Q355-14X210	550	4	12.69	50.8	
1815	Q355-38X104	104	12	3.23	38.8	
1816	Q355-10X100	115	8	0.90	7.2	
1817	Q355-6X50	100	4	0.24	1.0	
1818	-10X60	92	8	0.43	3.4	拉索附件
1819	-8X50	50	8	0.16	1.3	拉索附件 切角
1820	C5	50	8	0.27	2.2	拉索附件 槽钢
1821	-6X50	50	8	0.12	1.0	拉索附件
	GJ-50	21700	4	9.11	36.4	拉索附件
	NUT-2		4	3.20	12.8	拉索附件
	U-10		4	0.60	2.4	拉索附件
	NX-2.1		4	2.40	9.6	拉索附件
	JK-2		8	0.32	2.6	拉索附件
	C2906H5		16	23.31	373.0	
	FD6363B7D		8	103.2	825.6	
	T2330	–	1	12.40	12.4	主材安装爬梯
	T5530	–	1	28.80	28.8	主材安装爬梯
合计				13242.8 kg		


螺栓、脚钉、垫圈明细表


名称	级别	规格	符号	数量	重量(kg)	备注
螺栓	6.8级	M16X45	◪	24	4.0	
	8.8级	M24X75	⊘	112	66.4	
		M39X175	○	104	369.3	法兰螺栓
脚钉	6.8级	M16X185	⊕	114	47.3	
垫圈	Q235		规格X个数			
合计				487.0 kg		

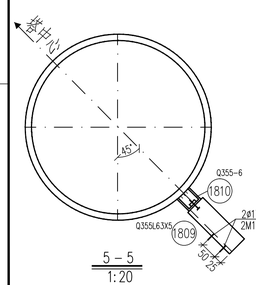


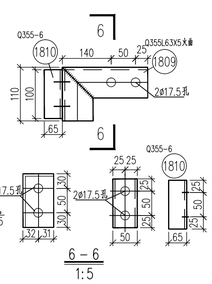


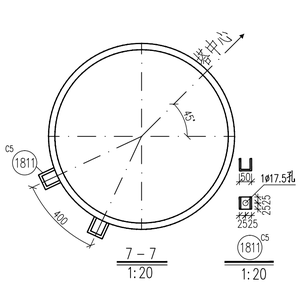


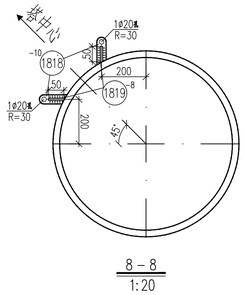

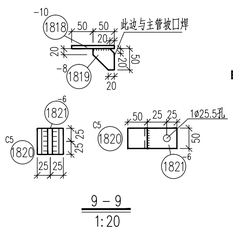

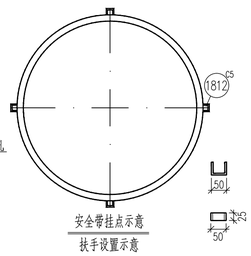

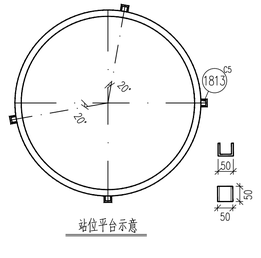

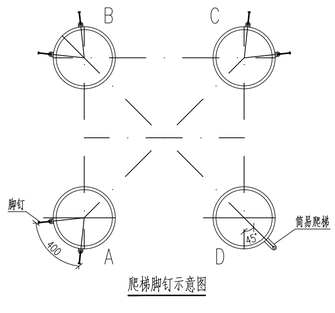

山东电力工程咨询院有限公司				浙江特高压交流环网工程线路 工程	施工图 设计阶段
批准	曹强	校核	刘一舟	SZK31102A双回路直线塔 身部结构图	18
审核	高鹏鹏	设计/勘测	潘旭光		
比例	1:40	日期	2026年 08月	图号 37-SA36901S-T0121-037	版本