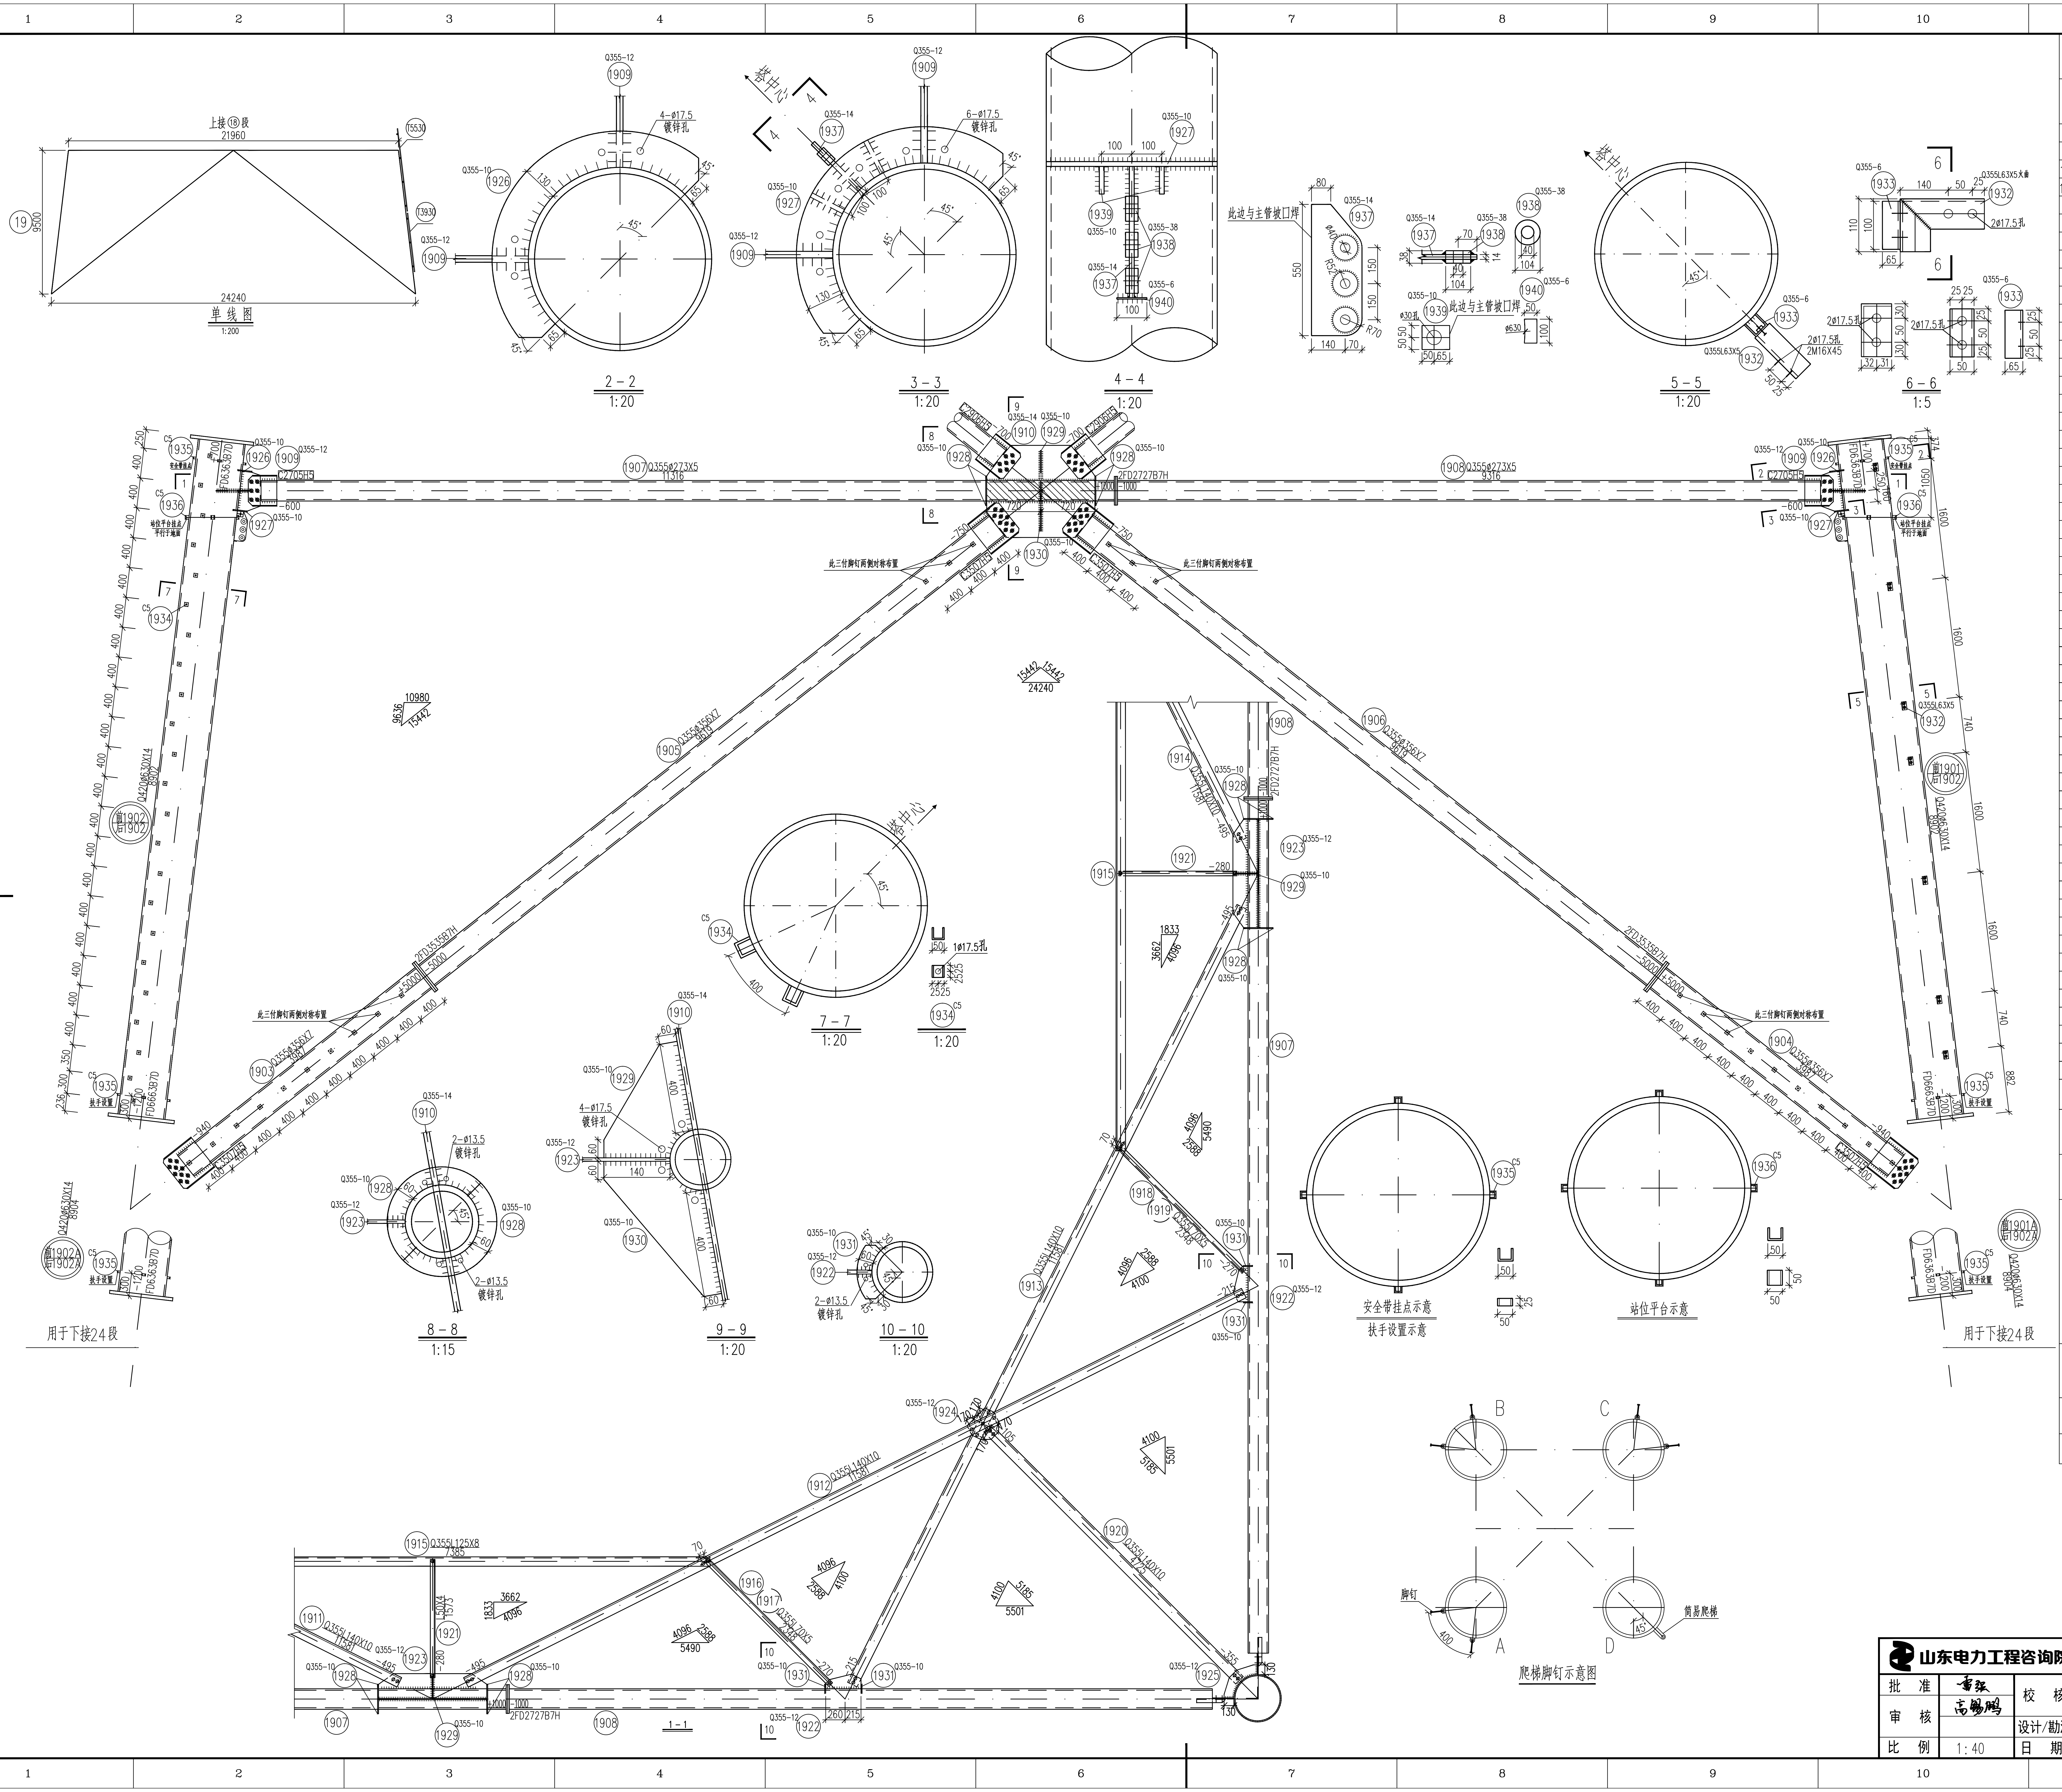

构件明细表

编号	规格	长度 (mm)	数量	重量(kg) 一件	重量(kg) 小计	备注
1901	Q420ø630X14	8902	1	1893.28	1893.3	装爬梯
1902	Q420ø630X14	8902	3	1893.28	5679.8	带脚钉
1901A	Q420ø630X14	8904	1	0.00	0.0	装爬梯 用于下接24段
1902A	Q420ø630X14	8904	3	0.00	0.0	带脚钉 用于下接24段
1903	Q355ø356X7	3987	4	240.21	960.8	带脚钉
1904	Q355ø356X7	3987	4	240.21	960.8	带脚钉
1905	Q355ø356X7	9619	4	579.53	2318.1	带脚钉
1906	Q355ø356X7	9619	4	579.53	2318.1	带脚钉
1907	Q355ø273X5	11316	4	373.95	1495.8	
1908	Q355ø273X5	9316	4	307.86	1231.4	
1909	Q355-12X321	572	8	17.30	138.4	
1910	Q355-14X1226	1440	4	194.02	776.1	
1911	Q355L140X10	11581	2	248.85	497.7	
1912	Q355L140X10	11581	2	248.85	497.7	
1913	Q355L140X10	11581	2	248.85	497.7	
1914	Q355L140X10	11581	2	248.85	497.7	
1915	Q355L125X8	7385	4	114.50	458.0	
1916	Q355L70X5	2348	2	12.67	25.3	
1917	Q355L70X5	2348	2	12.67	25.3	
1918	Q355L70X5	2348	2	12.67	25.3	
1919	Q355L70X5	2348	2	12.67	25.3	
1920	Q355L140X10	4725	4	101.53	406.1	
1921	L50X4	1573	4	4.81	19.2	
1922	Q355-12X201	510	8	9.66	77.3	
1923	Q355-12X208	1440	4	28.21	112.8	
1924	Q355-12X440	453	4	18.78	75.1	
1925	Q355-12X254	607	4	14.52	58.1	
1926	Q355-10X130	1313	4	13.40	53.6	
1927	Q355-10X130	1313	4	13.40	53.6	
1928	Q355-10X60	575	16	2.71	43.4	
1929	Q355-10X270	583	4	12.36	49.4	
1930	Q355-10X270	583	4	12.36	49.4	
1931	Q355-10X60	288	16	1.36	21.8	
1932	Q355L63X5	325	7	1.57	11.0	火曲
1933	Q355-6X100	180	7	0.85	6.0	火曲
1934	C5	50	224	0.27	60.5	槽钢
1935	C5	25	32	0.14	4.5	槽钢
1936	C5	50	16	0.27	4.3	槽钢
1937	Q355-14X210	550	4	12.69	50.8	
1938	Q355-38X104	104	12	3.23	38.8	
1939	Q355-10X100	115	8	0.90	7.2	
1940	Q355-6X50	100	4	0.24	1.0	
	C2705H5		8	18.20	145.6	
	C3507H5		16	36.27	580.3	
	FD2727B7H		8	12.2	97.6	
	FD3535B7H		16	22.1	353.6	
	FD6363B7D		4	103.2	412.8	
	FD6663B7D		4	125.3	501.2	
	FD6363B7D		8	0.00	0.0	用于下接24段
	T3930	–	1	20.70	20.7	主材安装爬梯
	T5530	–	1	28.80	28.8	主材安装爬梯
合计	23667.1 kg					

螺栓、脚钉、垫圈明细表

名称	级别	规格	符号	数量	重量(kg)	备注
螺栓	6.8级	M16X45	◍	32	5.4	
		M16X55	◍	4	0.7	
		M20X65	∅	88	31.1	
		M20X75	⊗	4	1.5	
	8.8级	M24X75	⊘	184	109.1	
		M20X95	○	80	38.7	法兰螺栓
		M24X115	○	176	147.8	法兰螺栓
		M39X175	○	104	369.3	法兰螺栓
脚钉	6.8级	M16X185	⊖ ⊣	224	92.9	
垫圈	Q235		规格X个数			
合计			796.5 kg			

山东电力工程咨询院有限公司				浙江特高压交流环网工程线路 工程	施工图 设计阶段
批准		校核	马一丹	SZK31102A双回路直线塔 身部结构图 ⑲	
审核	高锡鹏				
		设计/勘测			
比例	1:40	日期	2026年 08月	图号 37-SA36901S-T0121-038	版本