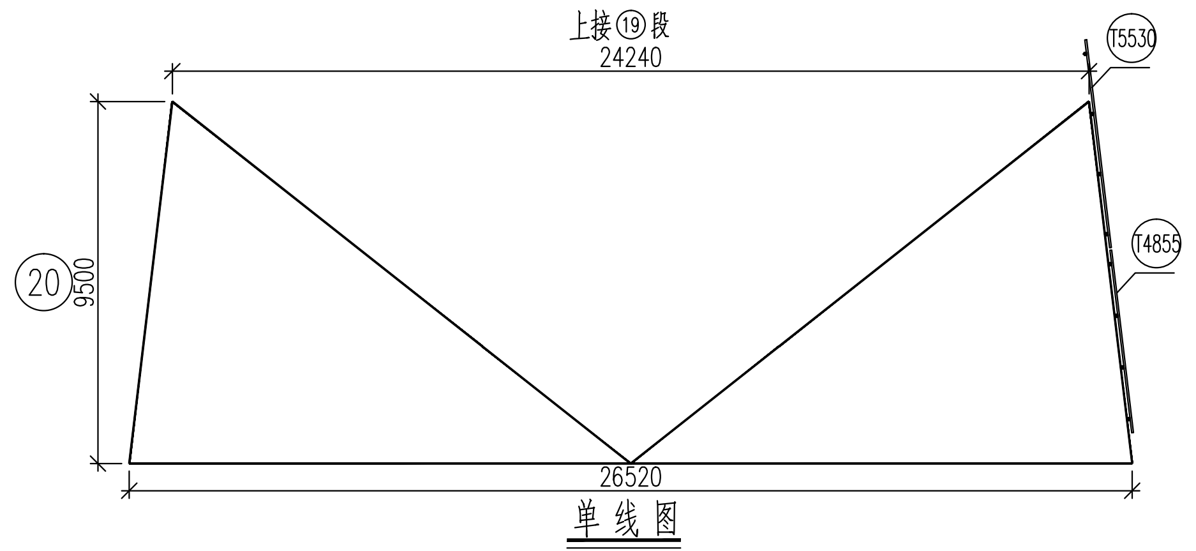
上接⑲段
24240
T5530
9500
⑳
T4855
26520

单线图
1:200

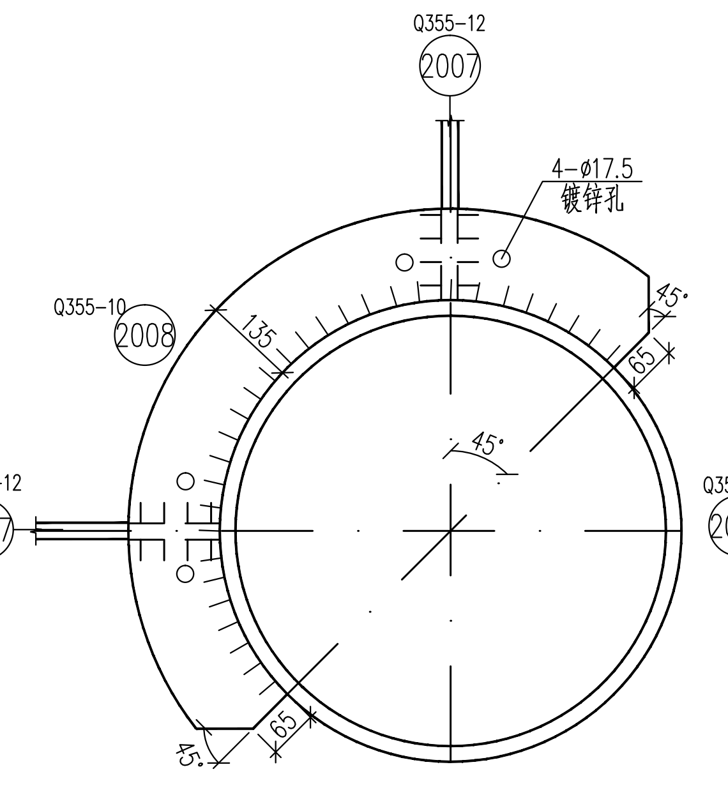
Q355-12
2007
4-ø17.5
镀锌孔
Q355-10
2008
45°
135
2007
45°
65

1－1
1:20

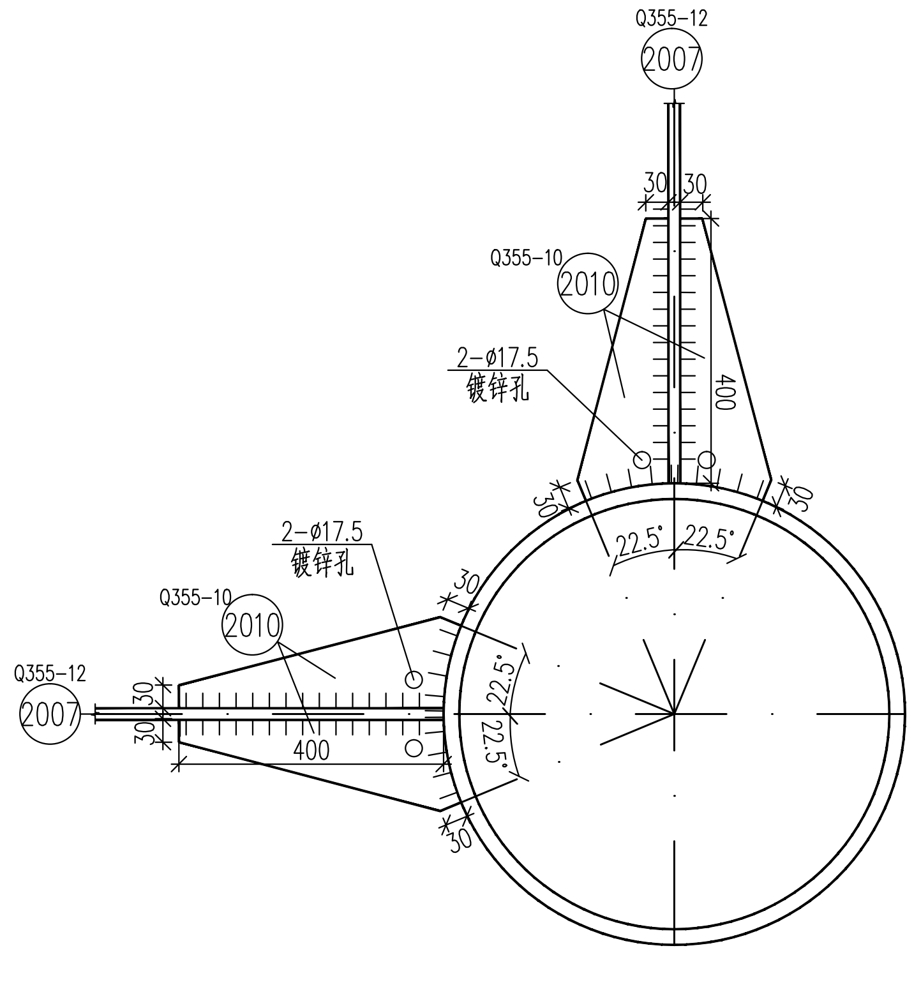
Q355-12
2007
Q355-10
2010
2-ø17.5
镀锌孔
2010
400
22.5°
2007

2－2
1:20

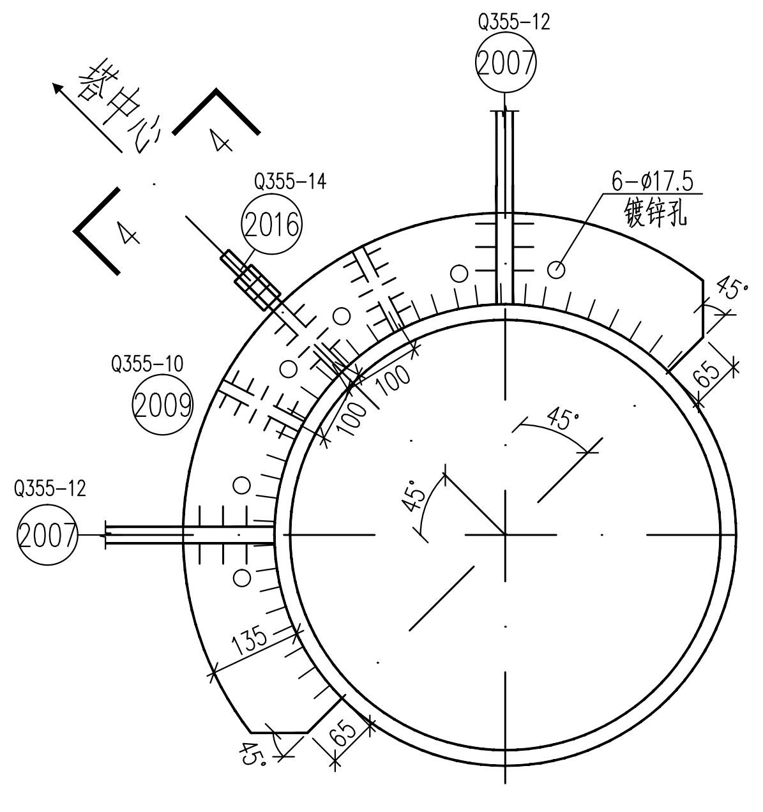
塔中心
4
Q355-14
2016
Q355-12
2007
6-ø17.5
镀锌孔
Q355-10
2009
45°
135
2007

3－3
1:20

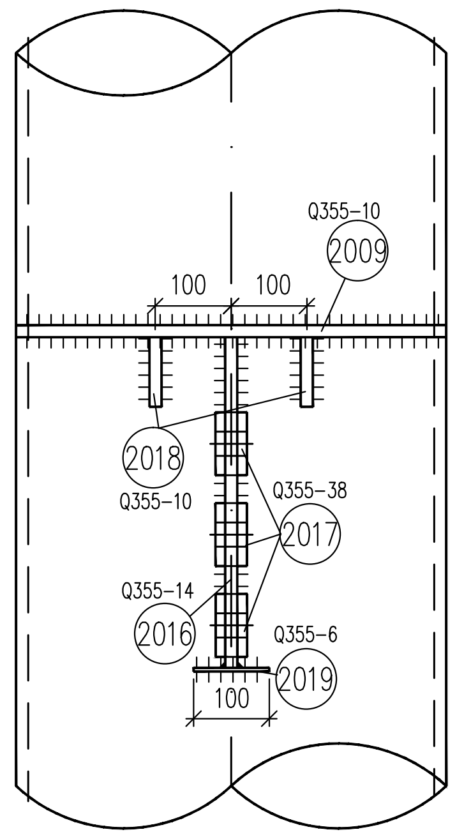
Q355-10
2009
100
100
2018
Q355-38
2017
2016
Q355-6
2019

4－4
1:20

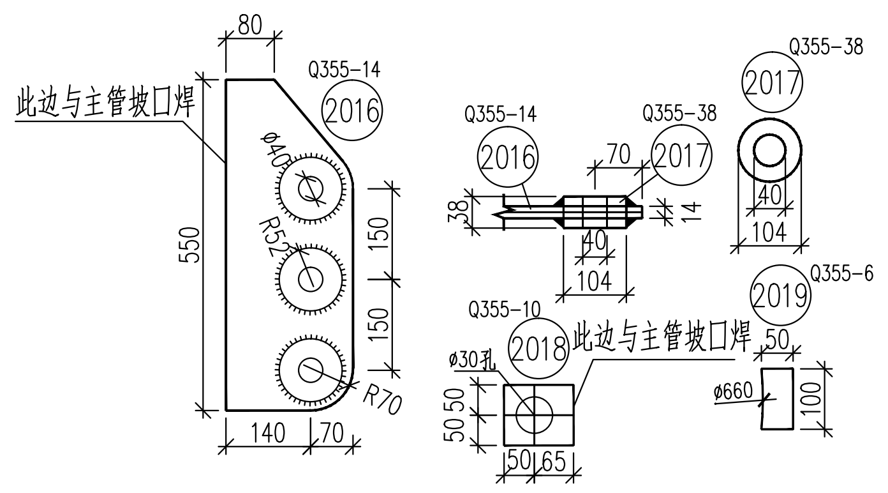
80
Q355-14
2016
此边与主管坡口焊
550
140
70
R70
Q355-14
2016
Q355-38
2017
70
104
Q355-38
2017
Q355-10
2018
此边与主管坡口焊
Q355-6
2019
ø60

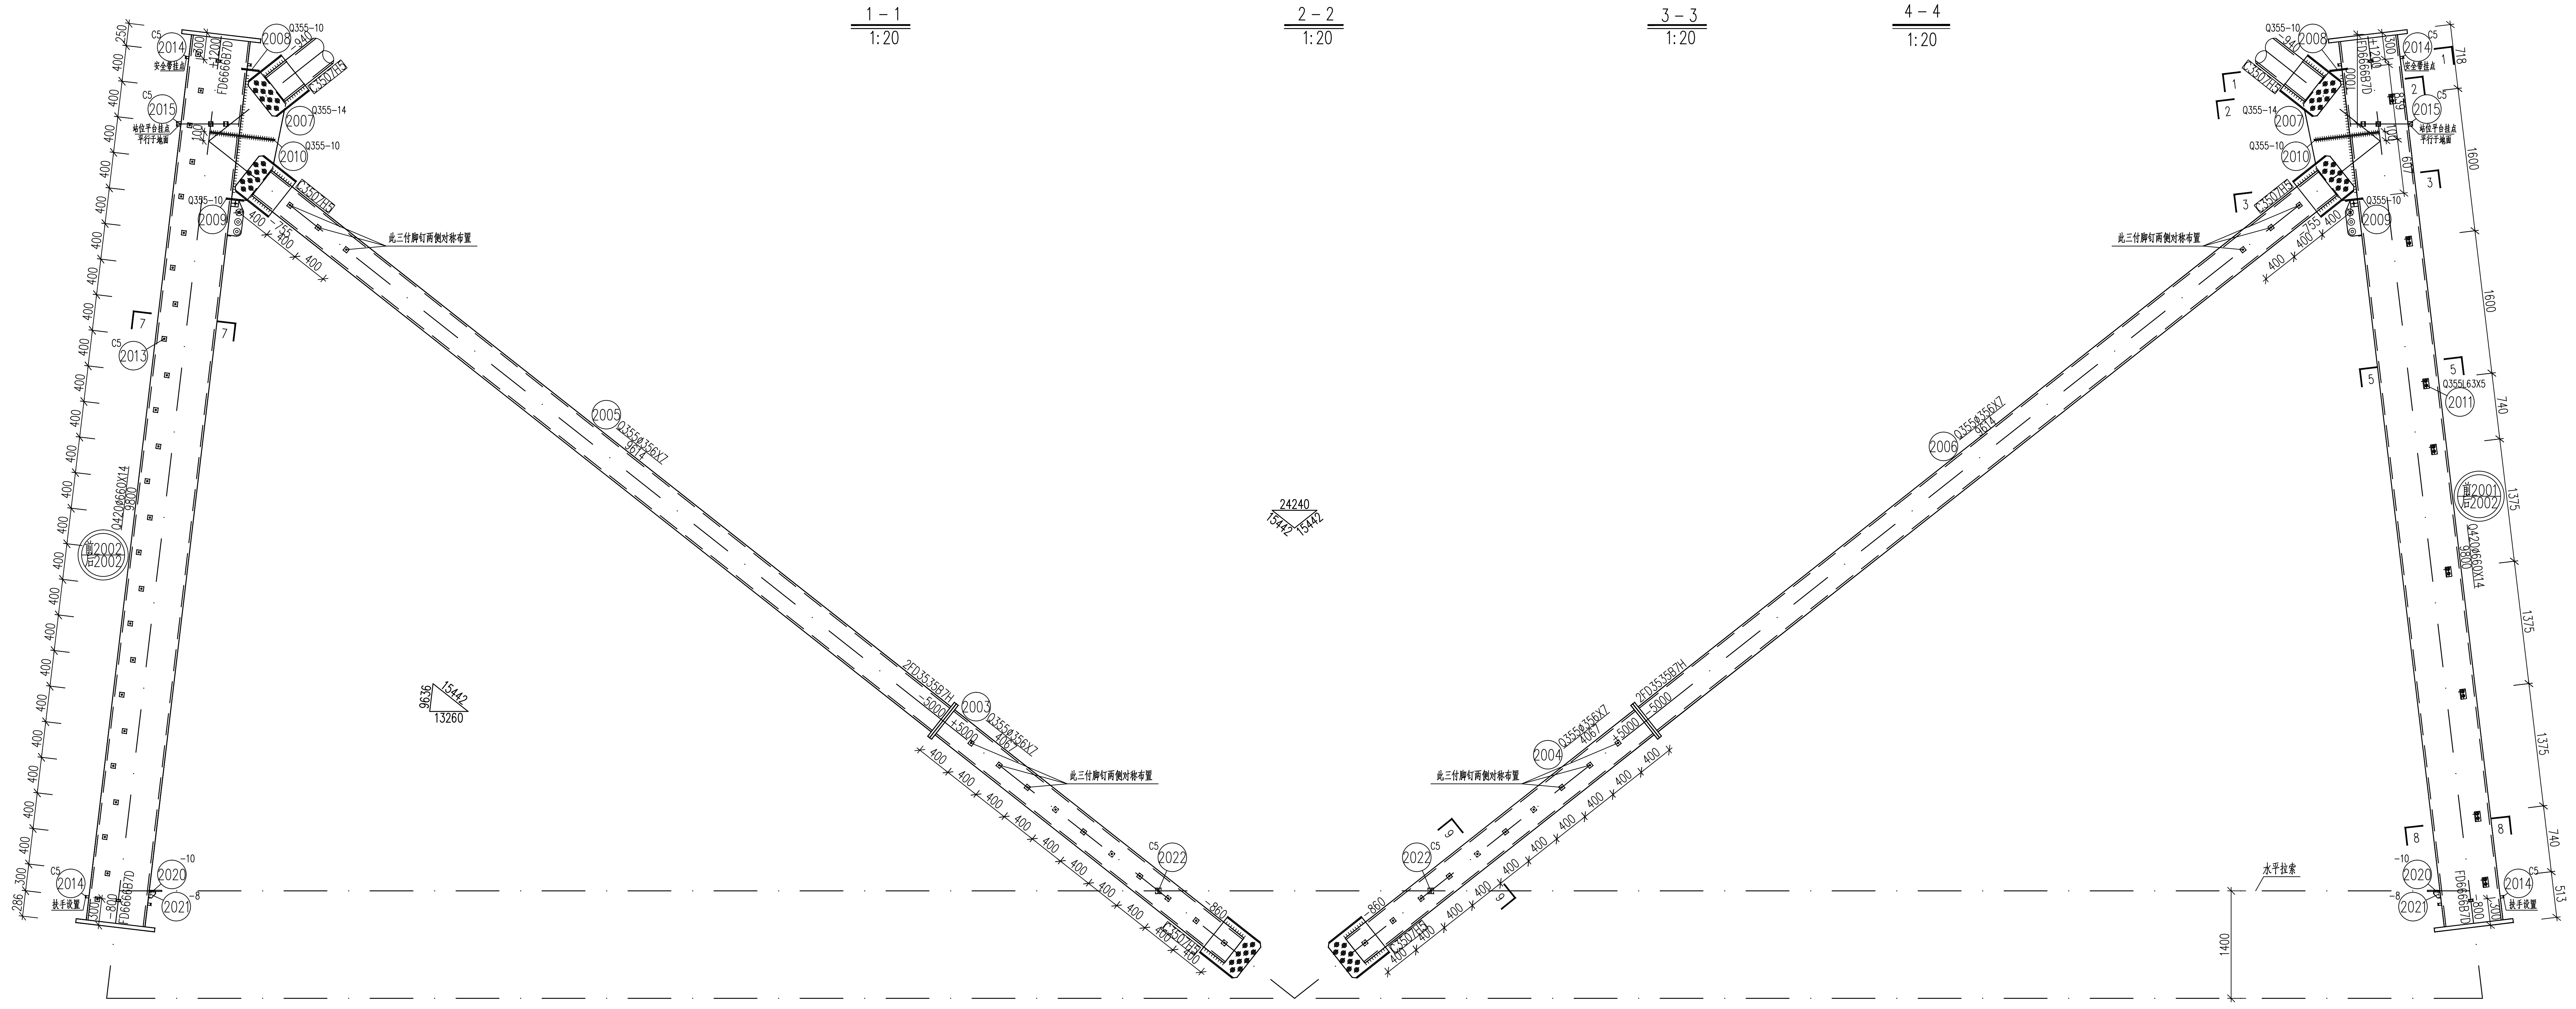
Q355-10
2008
2014
FD6666B7D
C3507H5
2015
Q355-14
2007
Q355-10
2010
2009
此三份脚钉两侧对称布置
2013
2005
Q355ø356X7
9614
Q420ø660X14
9800
2001
2002
24240
15442
15442
9636
13260
2FD3535B7H
2003
Q355ø356X7
4067
2022
2014
2020
2021
2006
2004
2011
水平拉索
1400
1
2
3
4
5
6
7
8

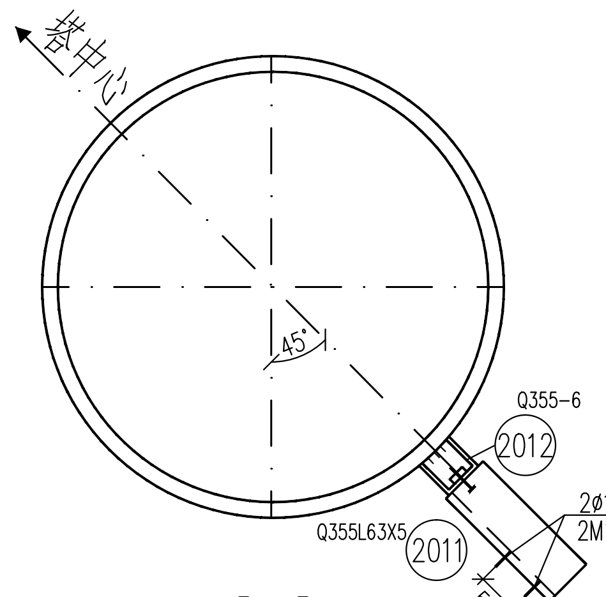
塔中心
45°
Q355-6
2012
Q355L63X5
2011
2M16X45

5－5
1:20

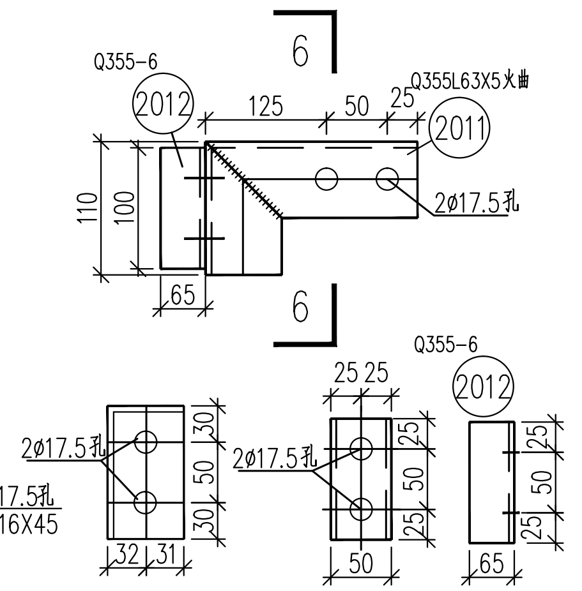
6
Q355-6
2012
125
50
Q355L63X5火曲
2011
2ø17.5孔
110
65
6
2ø17.5孔
2ø17.5孔
Q355-6
2012
50
25

6－6
1:5

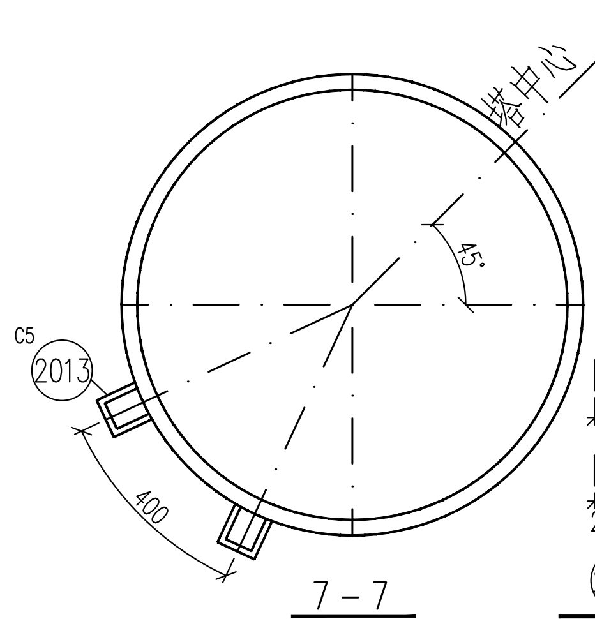
塔中心
45°
C5
2013
400

7－7
1:20

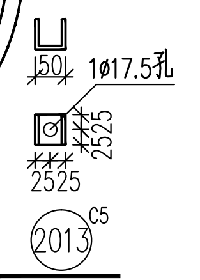
1ø17.5孔
25
25
C5

2013
1:20

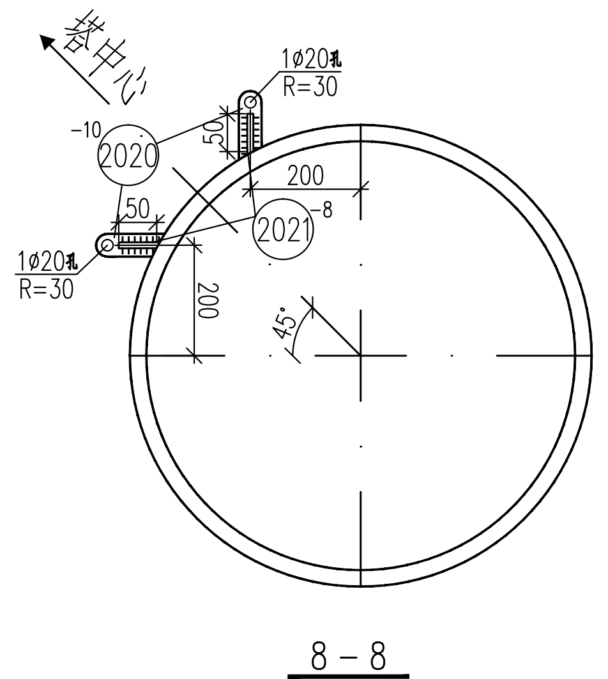
塔中心
1ø20
R=30
-10
2020
-8
2021
200
1ø20
R=30
200
45°

8－8
1:20

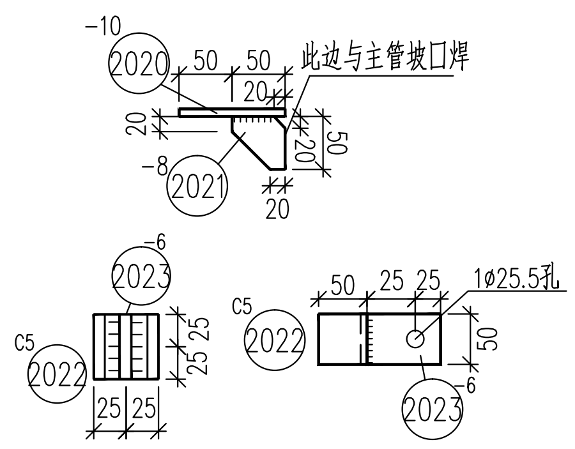
-10
2020
此边与主管坡口焊
-8
2021
-6
2023
C5
2022
C5
2022
1ø25.5孔
2023

9－9
1:20

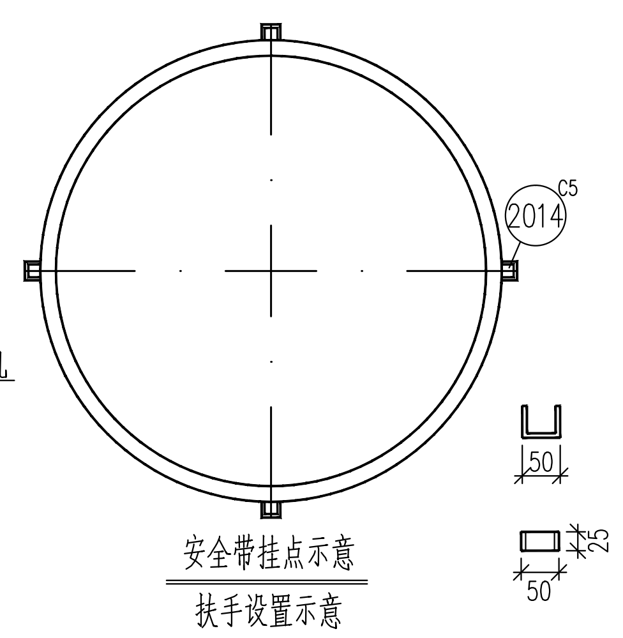
C5
2014
50
25

安全带挂点示意
扶手设置示意

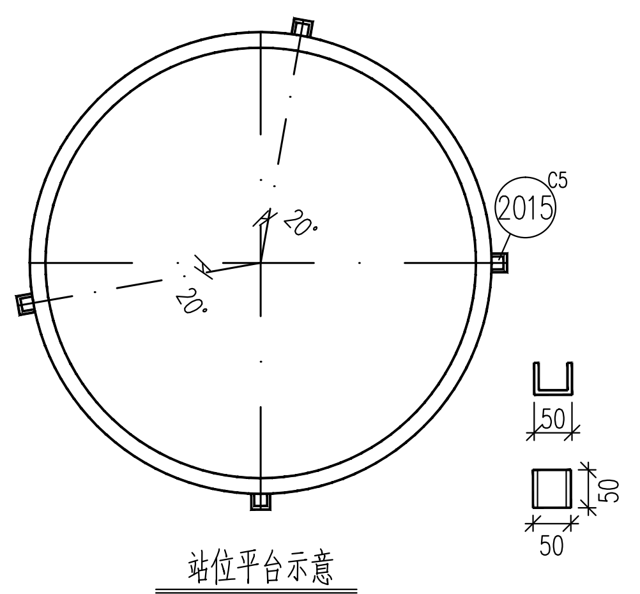
20°
20°
C5
2015
50
50

站位平台示意

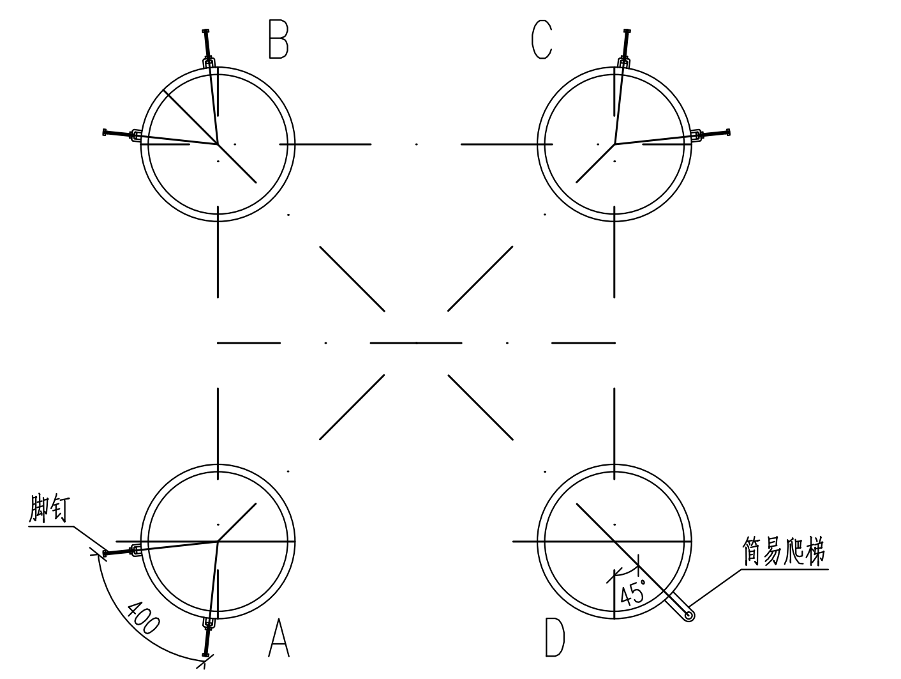
B
C
脚钉
400
A
45°
D
简易爬梯

爬梯脚钉示意图

构　件　明　细　表

编号	规　格	长度 (mm)	数量	重量(kg) 一件	重量(kg) 小计	备　注
2001	Q420ø660X14	9800	1	2185.78	2185.8	装爬梯
2002	Q420ø660X14	9800	3	2185.78	6557.3	带脚钉
2003	Q355ø356X7	4067	4	245.03	980.1	带脚钉
2004	Q355ø356X7	4067	4	245.03	980.1	带脚钉
2005	Q355ø356X7	9614	4	579.22	2316.9	带脚钉
2006	Q355ø356X7	9614	4	579.22	2316.9	带脚钉
2007	Q355-14X524	1509	8	86.90	695.2	
2008	Q355-10X135	1374	4	14.56	58.2	
2009	Q355-10X135	1374	4	14.56	58.2	
2010	Q355-10X148	440	16	5.11	81.8	
2011	Q355L63X5	310	8	2.14	17.1	火曲
2012	Q355-6X100	180	8	0.85	6.8	火曲
2013	C5	50	230	0.27	62.1	槽钢
2014	C5	25	32	0.14	4.5	槽钢
2015	C5	50	16	0.27	4.3	槽钢
2016	Q355-14X210	550	4	12.69	50.8	
2017	Q355-38X104	104	12	3.23	38.8	
2018	Q355-10X100	115	8	0.90	7.2	
2019	Q355-6X50	100	4	0.24	1.0	
2020	-10X60	92	8	0.43	3.4	拉索附件
2021	-8X50	50	8	0.16	1.3	拉索附件 切角
2022	C5	50	8	0.27	2.2	拉索附件 槽钢
2023	-6X50	50	8	0.12	1.0	拉索附件
	GJ-50	26300	4	11.05	44.2	拉索附件
	NUT-2		4	3.20	12.8	拉索附件
	U-10		4	0.60	2.4	拉索附件
	NX-2.1		4	2.40	9.6	拉索附件
	JK-2		8	0.32	2.6	拉索附件
	C3507H5		16	36.27	580.3	
	FD3535B7H		16	22.1	353.6	
	FD6666B7D		8	116.5	932.0	
	T4855	–	1	25.00	25.0	主材安装爬梯
	T5530	–	1	28.80	28.8	主材安装爬梯
合　计		18422.3 kg				

螺栓、脚钉、垫圈 明细表

名称	级别	规　格	符 号	数量	重量(kg)	备　注
螺栓	6.8级	M16X45	◎	32	5.4	
	8.8级	M24X75	∅	160	94.8	
		M24X115	○	176	147.8	法兰螺栓
		M39X175	○	112	397.7	法兰螺栓
脚钉	6.8级	M16X185	⊖ ⊣	230	95.4	
垫圈	Q235		规格X个数			
合　　计			741.1 kg			

山东电力工程咨询院有限公司				浙江特高压交流环网工程线路　工程　施工图　设计阶段
批　准	雷强	校　核	马一丹	SZK31102A双回路直线塔 ⑳ 身部结构图
审　核	高锡鹏			
		设计/勘测		
比　例	1:40	日　期	2026年 08月	图　号 37-SA36901S-T0121-039　版本