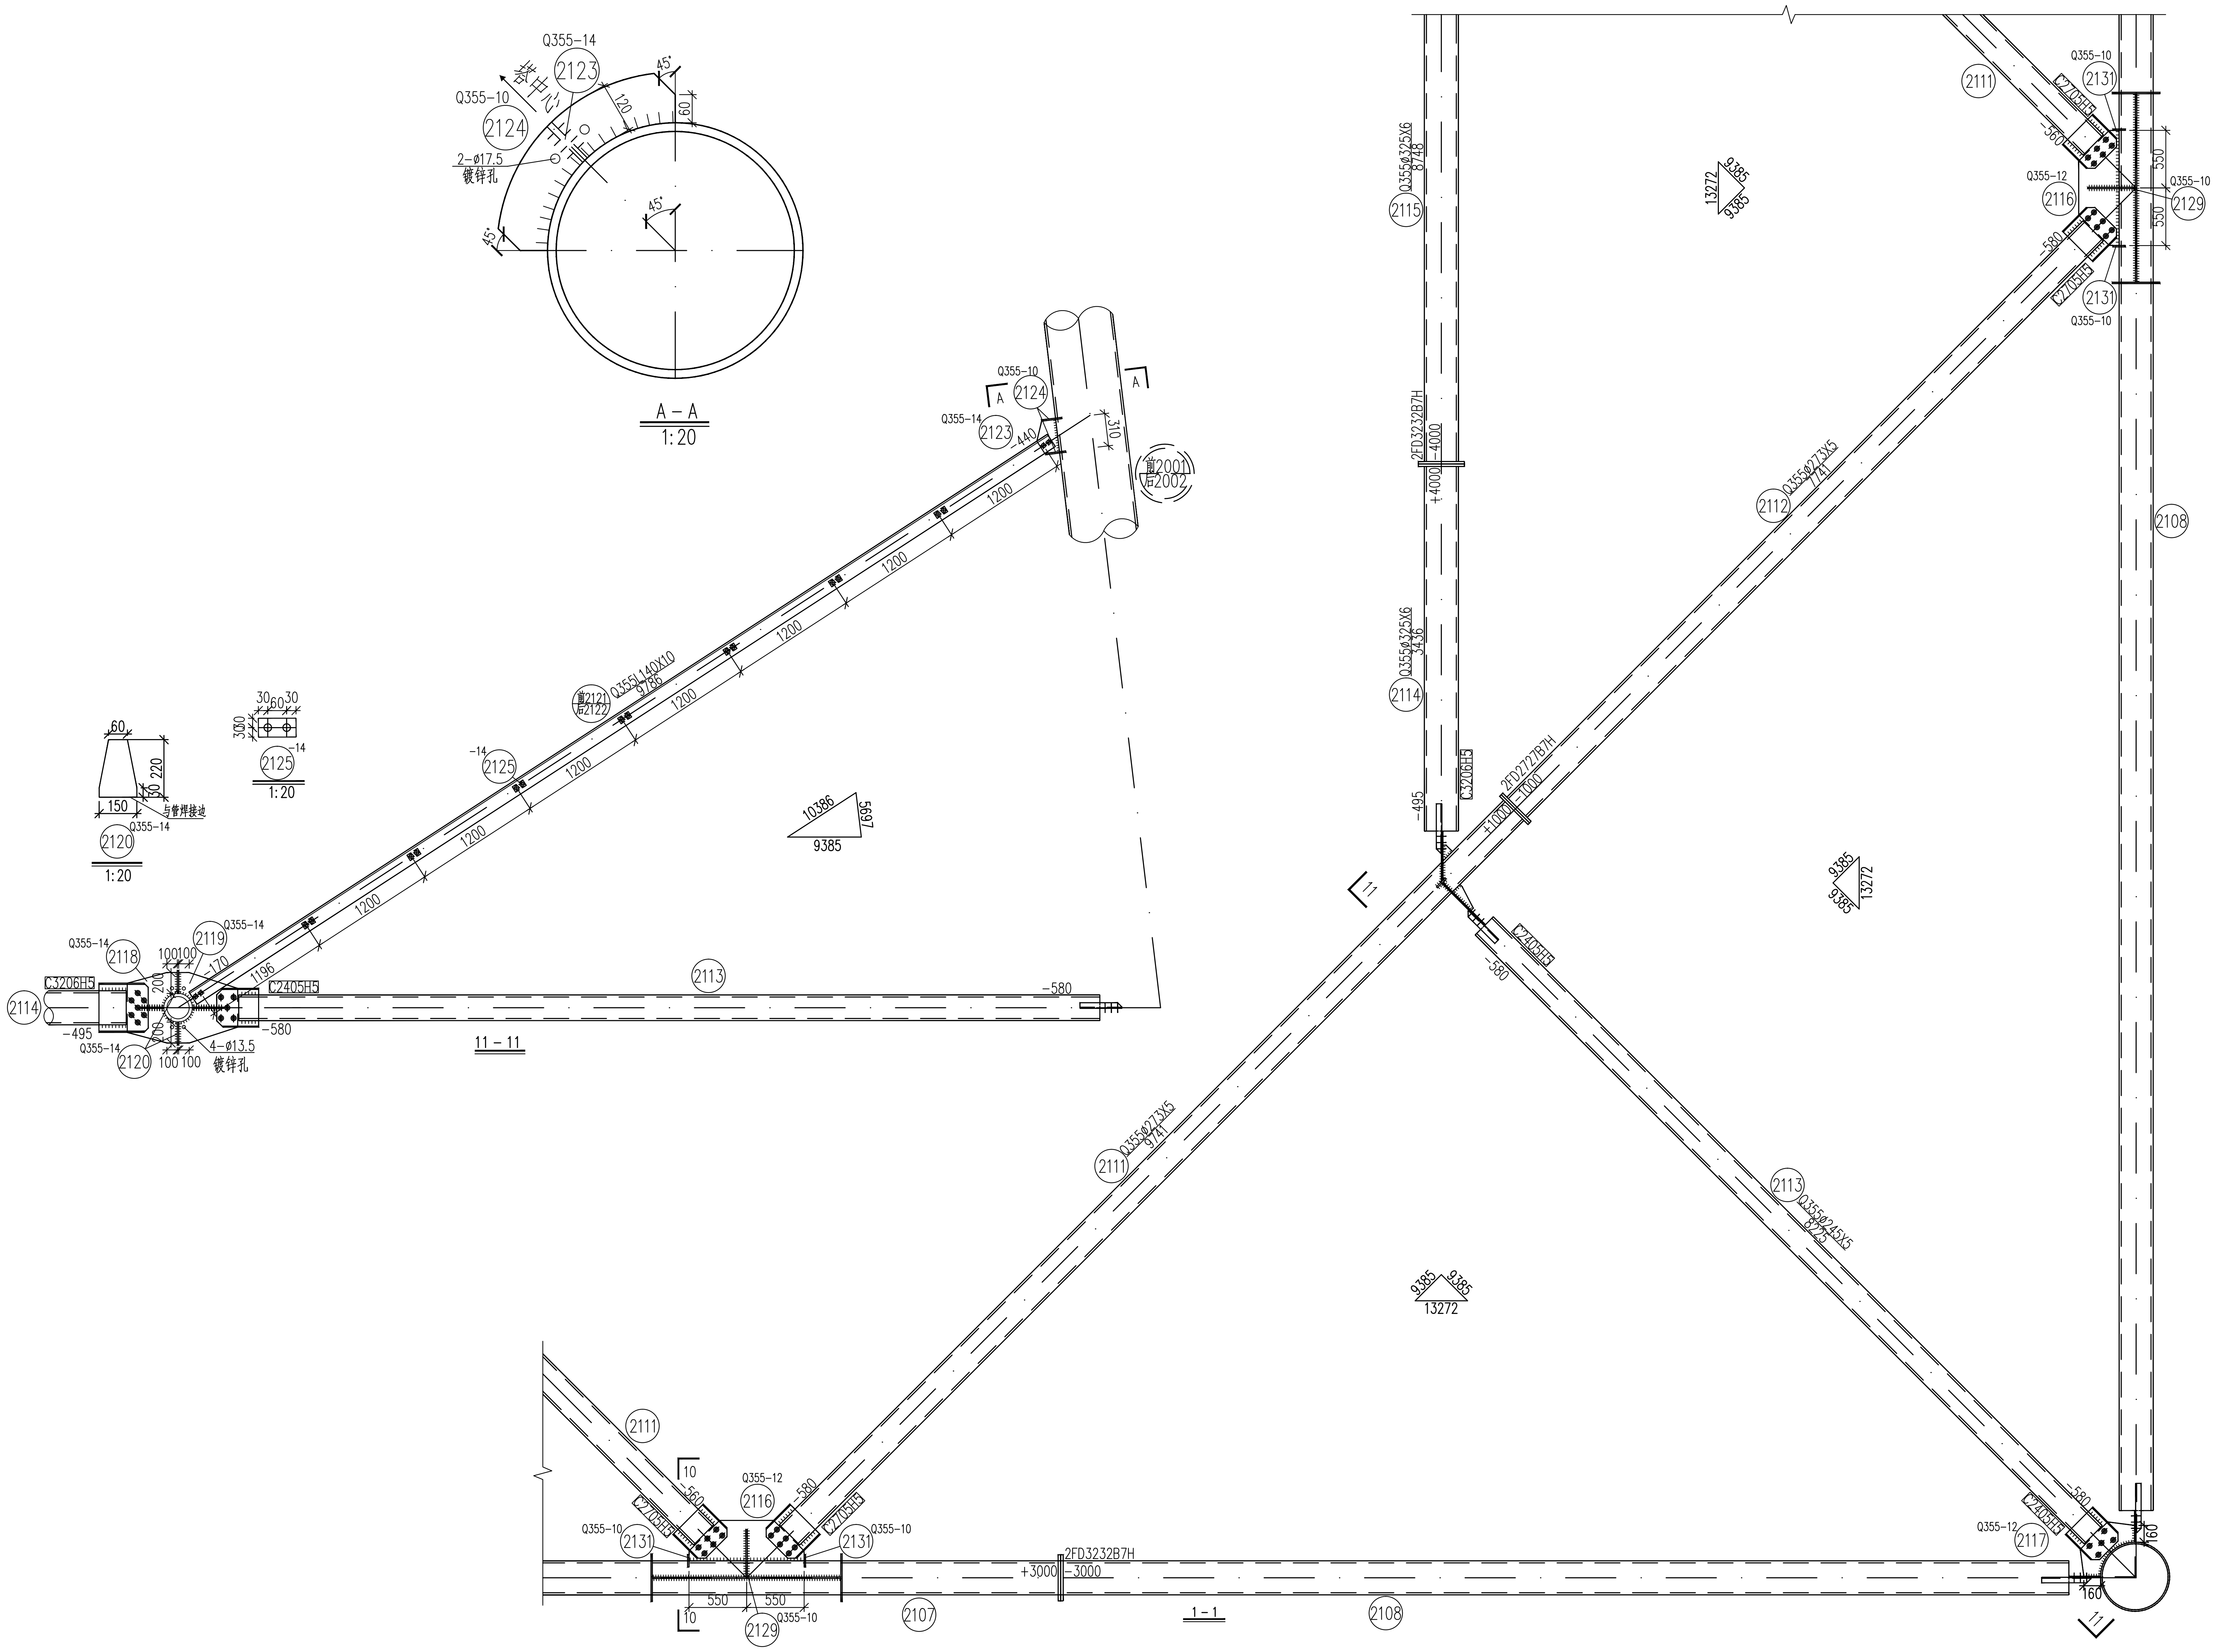
A－A
1:20
Q355－14
2123
Q355－10
2124
2－ø17.5
镀锌孔
45°
120
60
2120
1:20
2125
1:20
11－11
1－1
2101
2114
2118
2119
2113
2121
2122
2125
2111
2112
2115
2116
2117
2129
2131
2107
2108
Q355ø273X5
Q355ø245X5
Q355ø325X6
Q355L140X10
C3206H5
C2405H5
C2705H5
2FD3232B7H
2FD2727B7H
+3000
－3000
+4000
－580
－495
4－ø13.5
镀锌孔
9385
13272
10386
5657
1200
550
160

构 件 明 细 表

编号	规 格	长 度 (mm)	数量	重 量 (kg) 一 件	重 量 (kg) 小 计	备 注
2101	Q420ø660X15	9451	1	2255.01	2255.0	装爬梯
2102	Q420ø660X15	9451	3	2255.01	6765.0	带脚钉
2101A	Q420ø660X15	9457	1	0.00	0.0	装爬梯 用于下接26段
2102A	Q420ø660X15	9457	3	0.00	0.0	带脚钉 用于下接26段
2103	Q355ø406X8	4937	4	387.66	1550.6	带脚钉
2104	Q355ø406X8	4937	4	387.66	1550.6	带脚钉
2103A	Q355ø406X8	4817	4	0.00	0.0	带脚钉 用于下接26段
2104A	Q355ø406X8	4817	4	0.00	0.0	带脚钉 用于下接26段
2105	Q355ø406X8	10594	4	831.86	3327.4	带脚钉
2106	Q355ø406X8	10594	4	831.86	3327.4	带脚钉
2107	Q355ø325X6	5862	4	276.70	1106.8	
2108	Q355ø325X6	9561	8	451.30	3610.4	
2109	Q355－14X338	682	8	25.33	202.6	
2110	Q355－14X1505	1800	4	297.72	1190.9	
2111	Q355ø273X5	9741	4	321.91	1287.6	
2112	Q355ø273X5	7741	4	255.81	1023.2	
2113	Q355ø245X5	8225	4	243.41	973.6	
2114	Q355ø325X6	3436	2	162.19	324.4	
2115	Q355ø325X6	8748	2	412.92	825.8	
2116	Q355－12X398	1210	4	45.36	181.4	
2117	Q355－12X349	754	4	24.79	99.2	
2118	Q355－14X743	526	4	42.95	171.8	
2119	Q355－12X743	620	4	43.39	173.6	
2120	Q355－14X150	220	8	3.63	29.0	
2121	Q355L140X10	9786	4	210.28	841.1	
2122	Q355L140X10	9786	4	210.28	841.1	
2123	Q355－14X223	341	4	8.36	33.4	
2124	Q355－10X155	686	8	8.35	66.8	
2125	－14X60	120	28	0.79	22.1	垫块
2126	Q355－10X135	1374	4	14.56	58.2	
2127	Q355－10X135	1374	4	14.56	58.2	
2128	Q355－10X65	677	16	3.45	55.2	
2129	Q355－10X456	667	4	23.88	95.5	
2130	Q355－10X456	667	4	23.88	95.5	
2131	Q355－10X65	337	8	1.72	13.8	
2132	Q355L63X5	310	7	1.49	10.4	火曲
2133	Q355－6X100	180	7	0.85	6.0	火曲
2134	C5	50	243	0.27	65.6	槽钢
2135	C5	25	32	0.14	4.5	槽钢
2136	C5	50	16	0.27	4.3	槽钢
2137	Q355－14X210	550	4	12.69	50.8	
2138	Q355－38X104	104	12	3.23	38.8	
2139	Q355－10X100	115	8	0.90	7.2	
2140	Q355－6X50	100	4	0.24	1.0	
	C2405H5		8	17.27	138.2	
	C2705H5		8	18.20	145.6	
	C3206H5		12	31.43	377.2	
	C4008H5		16	45.59	729.4	
	FD2727B7H		8	12.2	97.6	
	FD3232B7H		20	16.8	336.0	
	FD4040B7H		16	26.5	424.0	
	FD6666B7D		4	116.5	466.0	
	FD7166B7D		4	161.1	644.4	
	FD6666B7D		8	0.00	0.0	用于下接26段
	T3930	－	1	20.70	20.7	主材安装爬梯
	T5530	－	1	28.80	28.8	主材安装爬梯
合 计		35753.7 kg				

螺栓、脚钉、垫圈 明细表

名称	级别	规 格	符 号	数量	重量(kg)	备 注
螺栓	6.8级	M16X45	◎	28	4.7	
		M20X55	○	8	2.6	
		M20X75	⊗	72	27.2	
	8.8级	M24X75	⊘	356	211.0	
		M20X95	○	80	38.7	法兰螺栓
		M20X100	○	220	109.1	法兰螺栓
		M24X115	○	208	174.7	法兰螺栓
		M39X175	○	112	397.7	法兰螺栓
脚钉	6.8级	M16X185	⊖	243	100.7	
垫圈	Q235		规格X个数			
合 计			1066.4 kg			

山东电力工程咨询院有限公司			浙江特高压交流环网工程线路 工程	施工图	设计阶段
批 准		校 核	SZK31102A双回路直线塔 身部结构图(2/2) ㉑		
审 核	高锡鹏				
		设计/勘测			
比 例	1:40	日 期	2026年 08月	图 号	37－SA36901S－T0121－041
				版本	