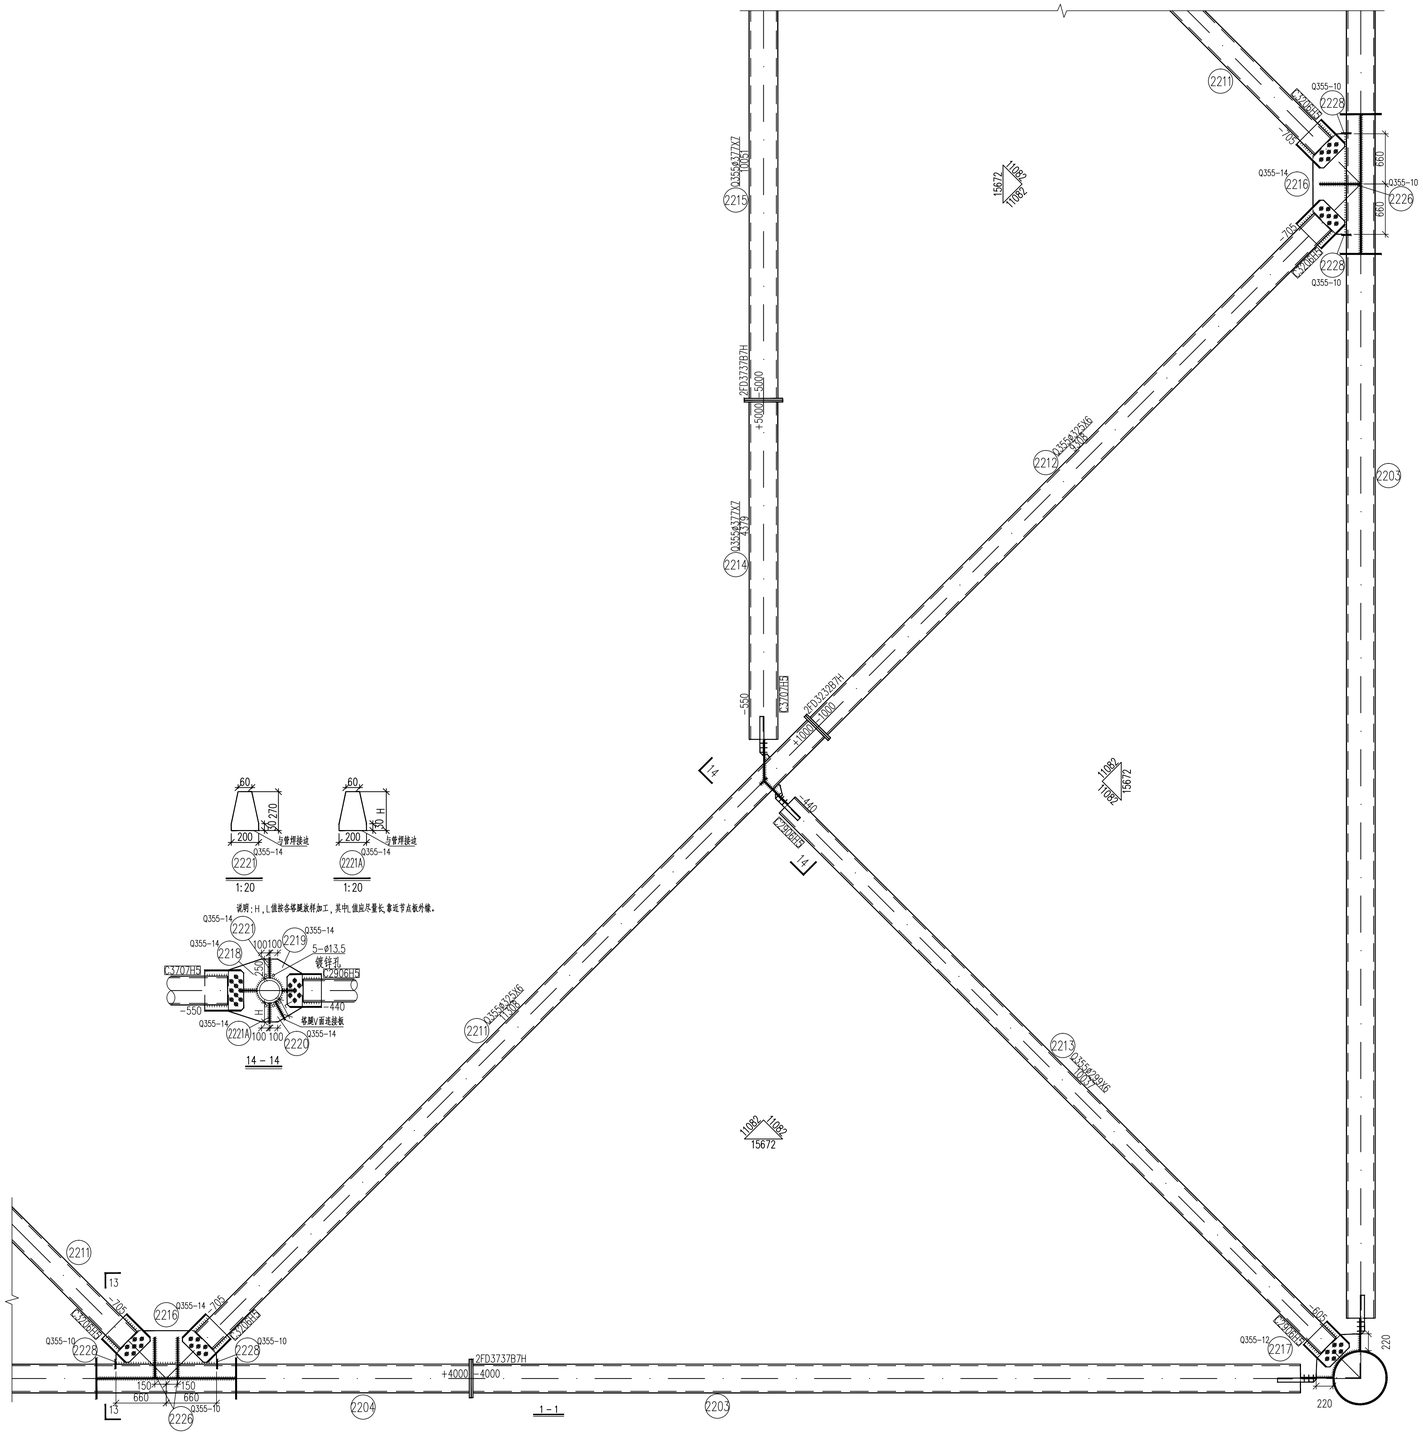


构 件 明 细 表

编号	规 格	长度(mm)	数量	重量(kg) 一件	重量(kg) 小计	备 注
2201	Q420φ711X15	10345	1	2663.49	2663.5	装爬梯
2202	Q420φ711X15	10345	3	2663.49	7990.5	带脚钉
2203	Q355φ377X7	10809	8	690.41	5523.3	
2204	Q355φ377X7	7858	4	501.92	2007.7	
2205	Q355φ406X8	4932	4	387.27	1549.1	带脚钉
2206	Q355φ406X8	4932	4	387.27	1549.1	带脚钉
2207	Q355φ406X8	10729	4	842.46	3369.8	带脚钉
2208	Q355φ406X8	10729	4	842.46	3369.8	带脚钉
2209	Q355-14X1548	1820	4	309.63	1238.5	
2210	Q355-14X555	1505	8	91.80	734.4	
2211	Q355φ325X6	11308	4	533.76	2135.0	
2212	Q355φ325X6	9308	4	439.36	1757.4	
2213	Q355φ299X6	10037	4	435.15	1740.6	
2214	Q355φ377X7	4379	2	279.70	559.4	
2215	Q355φ377X7	10051	2	641.99	1284.0	
2216	Q355-14X479	1452	4	76.44	305.8	
2217	Q355-12X366	888	4	30.62	122.5	
2218	Q355-14X584	908	4	58.28	233.1	
2219	Q355-14X464	849	4	43.29	173.2	
2220	Q355-14X250	196	4	5.39	21.6	
2221	Q355-14X200	270	4	6.04	24.2	
2221A	Q355-14X200	270	4	6.04	24.2	
2222	Q355-10X145	1480	4	16.85	67.4	
2223	Q355-10X145	1480	4	16.85	67.4	
2224	Q355-10X145	440	16	5.01	80.2	
2225	Q355-10X80	790	16	4.96	79.4	
2226	Q355-10X581	749	8	34.16	273.3	
2227	Q355-10X581	749	4	34.16	136.6	
2228	Q355-10X80	395	8	2.48	19.8	
2229	L75X6	285	8	1.97	15.8	火曲
2230	Q355-6X100	180	8	0.85	6.8	火曲
2231	C5	50	246	0.27	66.4	槽钢
2232	C5	25	32	0.14	4.5	槽钢
2233	C5	50	16	0.27	4.3	槽钢
2234	Q355-14X210	550	4	12.69	50.8	
2235	Q355-38X104	104	12	3.23	38.8	
2236	Q355-10X100	115	8	0.90	7.2	
2237	Q355-6X50	100	4	0.24	1.0	
2238	-10X60	92	8	0.43	3.4	拉索附件
2239	-8X50	50	8	0.16	1.3	拉索附件 切角
2240	C5	50	8	0.27	2.2	拉索附件 槽钢
2241	-6X50	50	8	0.12	1.0	拉索附件
	GJ-50	31100	4	13.06	52.2	拉索附件
	NUT-2		4	3.20	12.8	拉索附件
	U-10		4	0.60	2.4	拉索附件
	NX-2.1		4	2.40	9.6	拉索附件
	JK-2		8	0.32	2.6	拉索附件
	C2906H5		8	23.31	186.5	
	C3206H5		8	31.43	251.4	
	C3707H5		12	39.39	472.7	
	C4008H5		16	47.25	756.0	
	FD3232B7H		8	16.8	134.4	
	FD3737B7H		20	21.7	434.0	
	FD4040B7H		16	26.5	424.0	
	FD7171B7D		8	142.3	1138.4	
	T3605	–	1	19.00	19.0	主材安装爬梯
	T6980	–	1	36.20	36.2	主材安装爬梯
合 计					43236.5 kg	

螺栓、脚钉、垫圈 明细表

名称	级别	规 格	符号	数量	重量(kg)	备 注
螺栓	6.8级	M16X45		32	5.4	
	8.8级	M24X75		544	322.5	
		M20X100		88	43.6	法兰螺栓
		M24X110		220	181.1	法兰螺栓
		M24X115		208	174.7	法兰螺栓
		M42X190		112	501.4	法兰螺栓
脚钉	6.8级	M16X185		246	102.0	
垫圈	Q235		规格X个数			
合 计				1330.7 kg		

山东电力工程咨询院有限公司			浙江特高压交流环网工程线路 工程	施工图	设计阶段
批 准		校 核		SZK31102A双回路直线塔 身部结构图(2/2)	22
审 核		设计/勘测			
比 例	1:40	日 期	2026年 08月	图 号 37-SA36901S-T0121-043	版本