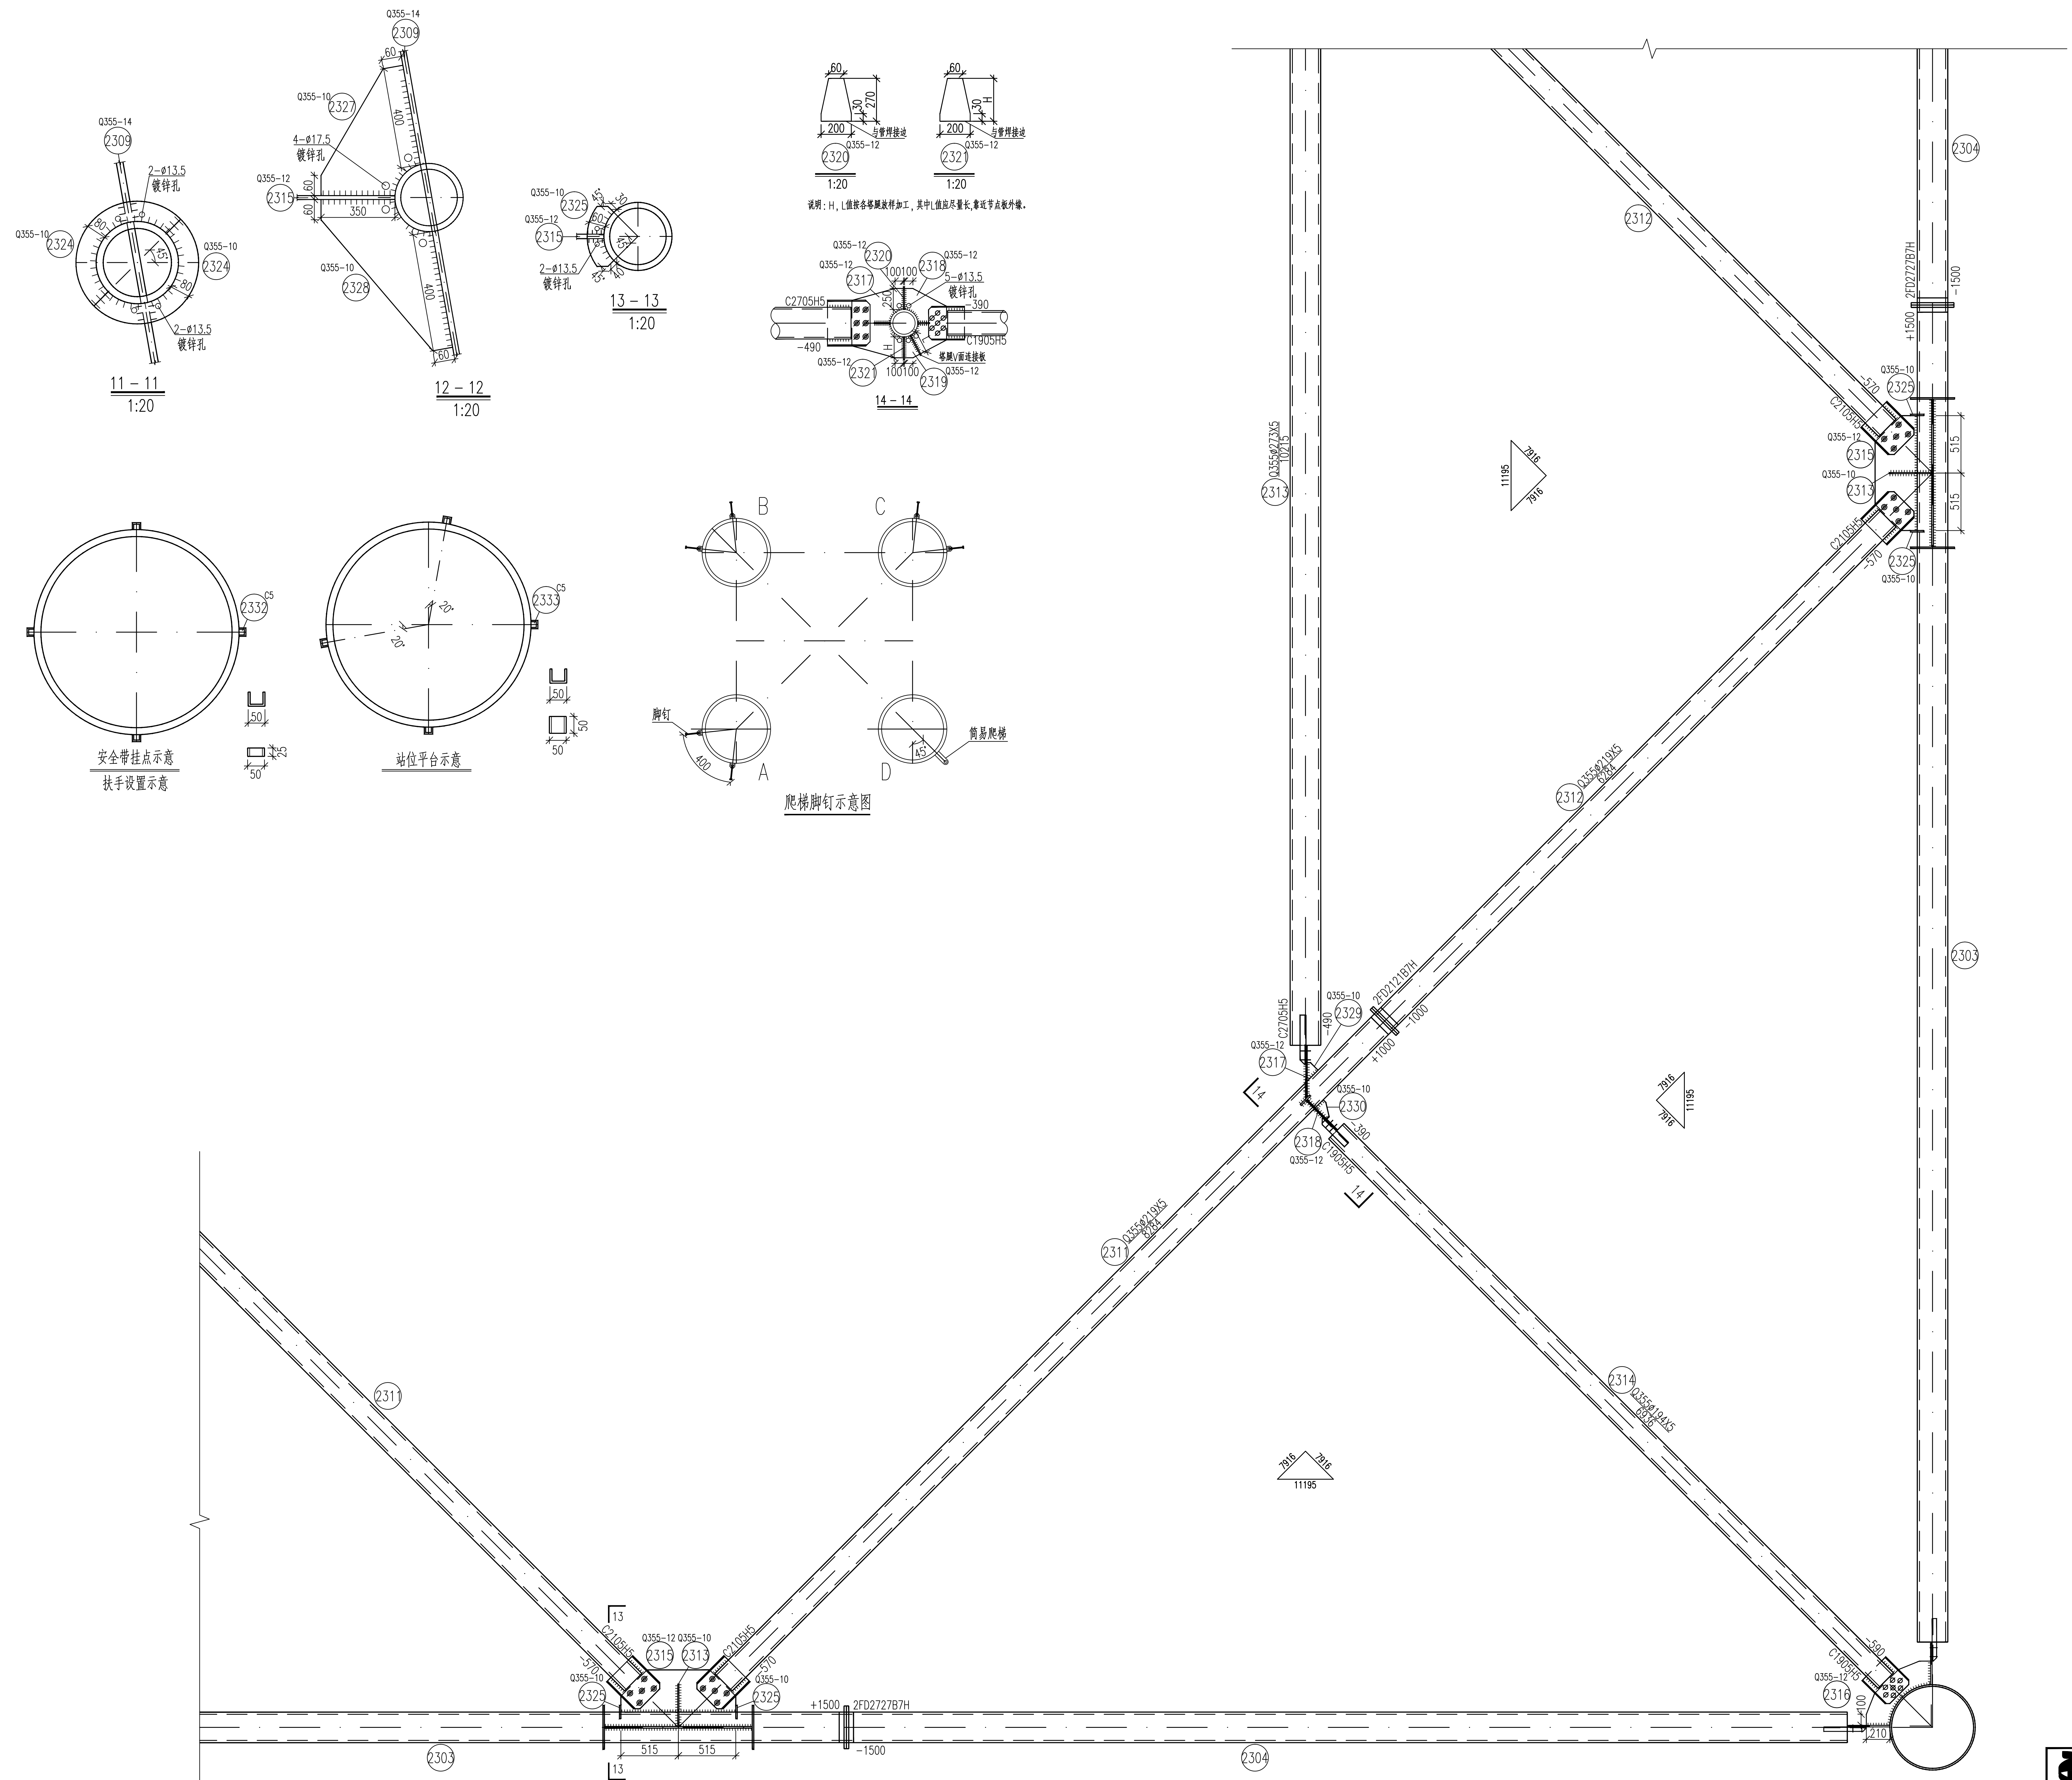
Q355-14
2309
2-ø13.5
镀锌孔
Q355-10
2324
80
45°
Q355-10
2324
80
2-ø13.5
镀锌孔

11－11

1:20

Q355-14
2309
60
Q355-10
2327
400
4-ø17.5
镀锌孔
Q355-12
2315
60
60
350
Q355-10
2328
400
60

12－12

1:20

Q355-10
2325
45°
30
60
Q355-12
2315
45
2-ø13.5
镀锌孔
45°
40

13－13

1:20

60
30
270
200
与管焊接边
Q355-12

2320

1:20

60
30
H
200
与管焊接边
Q355-12

2321

1:20

说明：H，L值按各塔腿放样加工，其中L值应尽量长,靠近节点板外缘。

Q355-12
2320
Q355-12
2318
Q355-12
2317
100100
5-ø13.5
镀锌孔
250
C2705H5
-390
-490
C1905H5
H
塔腿V面连接板
Q355-12
2321
100100
2319
Q355-12

14－14

2332
C5
50
25
50

安全带挂点示意

扶手设置示意

20°
20°
2333
C5
50
50
50

站位平台示意

B
C
脚钉
400
A
D
45°
简易爬梯

爬梯脚钉示意图

2304
2312
2313
Q355ø273X5
10215
11195
7916
7916
2FD2727B7H
-1500
+1500
-570
2325
Q355-10
C2105H5
Q355-12
2315
Q355-10
2313
515
515
C2105H5
2325
Q355-10
-570
2312
Q355ø219X5
6284
2303
C2705H5
-490
Q355-10
2329
2FD2121B7H
+1000
-1000
Q355-12
2317
14
Q355-10
2330
2318
Q355-12
C1905H5
-390
14
7916
7916
11195
2311
Q355ø219X5
8284
2311
2314
Q355ø194X5
6936
7916
7916
11195
13
C2105H5
Q355-12
2315
Q355-10
2313
C2105H5
-570
2325
Q355-10
-570
2325
Q355-10
+1500
2FD2727B7H
-1500
515
515
13
2303
2304
C1905H5
Q355-12
2316
-500
100
210

1－1

构 件 明 细 表

编号	规 格	长 度 (mm)	数量	重 量 (kg) 一 件	重 量 (kg) 小 计	备 注
2301	Q420ø630X14	10007	1	2128.30	2128.3	装爬梯
2302	Q420ø630X14	10007	3	2128.30	6384.9	带脚钉
2303	Q355ø273X5	11870	4	392.26	1569.0	
2304	Q355ø273X5	8870	4	293.12	1172.5	
2305	Q355ø325X6	5281	4	249.27	997.1	带脚钉
2306	Q355ø325X6	5281	4	249.27	997.1	带脚钉
2307	Q355ø325X6	7130	4	336.55	1346.2	带脚钉
2308	Q355ø325X6	7130	4	336.55	1346.2	带脚钉
2309	Q355-14X1322	1452	4	210.96	843.8	
2310	Q355-14X510	1595	8	89.40	715.2	
2311	Q355ø219X5	8284	4	218.60	874.4	
2312	Q355ø219X5	6284	4	165.82	663.3	
2313	Q355ø273X5	10215	2	337.57	675.1	
2314	Q355ø194X5	6936	4	161.64	646.6	
2315	Q355-12X416	1133	4	44.40	177.6	
2316	Q355-12X229	892	4	19.24	77.0	
2317	Q355-12X584	908	4	49.95	199.8	
2318	Q355-12X464	849	4	37.11	148.4	
2319	Q355-12X250	196	4	4.62	18.5	
2320	Q355-12X200	270	4	5.18	20.7	
2321	Q355-12X200	270	4	5.18	20.7	
2322	Q355-10X130	1313	4	13.40	53.6	
2323	Q355-10X130	1313	4	13.40	53.6	
2324	Q355-10X60	575	16	2.71	43.4	
2325	Q355-10X60	288	8	1.36	10.9	
2326	Q355-10X212	385	32	6.41	205.1	
2327	Q355-10X586	426	4	19.60	78.4	
2328	Q355-10X586	426	4	19.60	78.4	
2329	Q355-10X100	110	4	0.86	3.4	
2330	Q355-10X100	110	4	0.86	3.4	
2331	Q355L63X5	325	7	1.57	11.0	火曲
2332	Q355-6X100	180	7	0.85	6.0	火曲
2333	C5	50	265	0.27	71.6	槽钢
2334	C5	25	32	0.14	4.5	槽钢
2335	C5	50	16	0.27	4.3	槽钢
2336	Q355-14X210	550	4	12.69	50.8	
2337	Q355-38X104	104	12	3.23	38.8	
2338	Q355-10X100	115	8	0.90	7.2	
2339	Q355-6X50	100	4	0.24	1.0	
2340	-10X60	110	8	0.52	4.2	拉索附件
2341	-8X50	50	8	0.16	1.3	拉索附件 切角
2342	C5	50	8	0.27	2.2	拉索附件 槽钢
2343	-6X50	50	8	0.12	1.0	拉索附件
	GJ-50	22500	4	13.06	52.2	拉索附件
	NUT-2		4	3.20	12.8	拉索附件
	U-10		4	0.60	2.4	拉索附件
	NX-2.1		4	2.40	9.6	拉索附件
	JK-2		8	0.32	2.6	拉索附件
	C1905H5		8	8.80	70.40	
	C2705H5		12	18.10	217.20	
	C2105H5		8	14.54	116.32	
	C3206H5		16	31.43	502.88	
	FD3232B7H		16	16.8	268.80	
	FD2121B7H		8	9.20	73.6	
	FD2727B7H		8	12.2	97.6	
	FD6363B7D		8	103.00	824.00	
	T3930	–	1	20.70	20.70	主材安装爬梯
	T6980	–	1	36.20	36.20	主材安装爬梯
合 计		24063.8 kg				

螺栓、脚钉、垫圈 明细表

名称	级别	规 格	符 号	数量	重量(kg)	备 注
螺栓	6.8级	M16X45	◎	28	4.7	
		M20X65	∅	56	19.8	
	8.8级	M24X75	∅	288	170.7	
		M20X95	○	160	77.4	法兰螺栓
		M20X100	○	176	87.3	法兰螺栓
		M39X175	○	104	369.3	法兰螺栓
脚钉	6.8级	M16X185	⊖	265	102.0	
垫圈	Q235		规格X个数			
合 计			831.2 kg			

山东电力工程咨询院有限公司				浙江特高压交流环网工程线路 工程	施工图 设计阶段
批 准		校 核	马一丹	SZK31102A双回路直线塔身部结构图(2/2) ㉓	
审 核	高锡鹏				
		设计/勘测			
比 例	1：30	日 期	2026年 08月	图 号 37-SA36901S-T0121- 045	版本