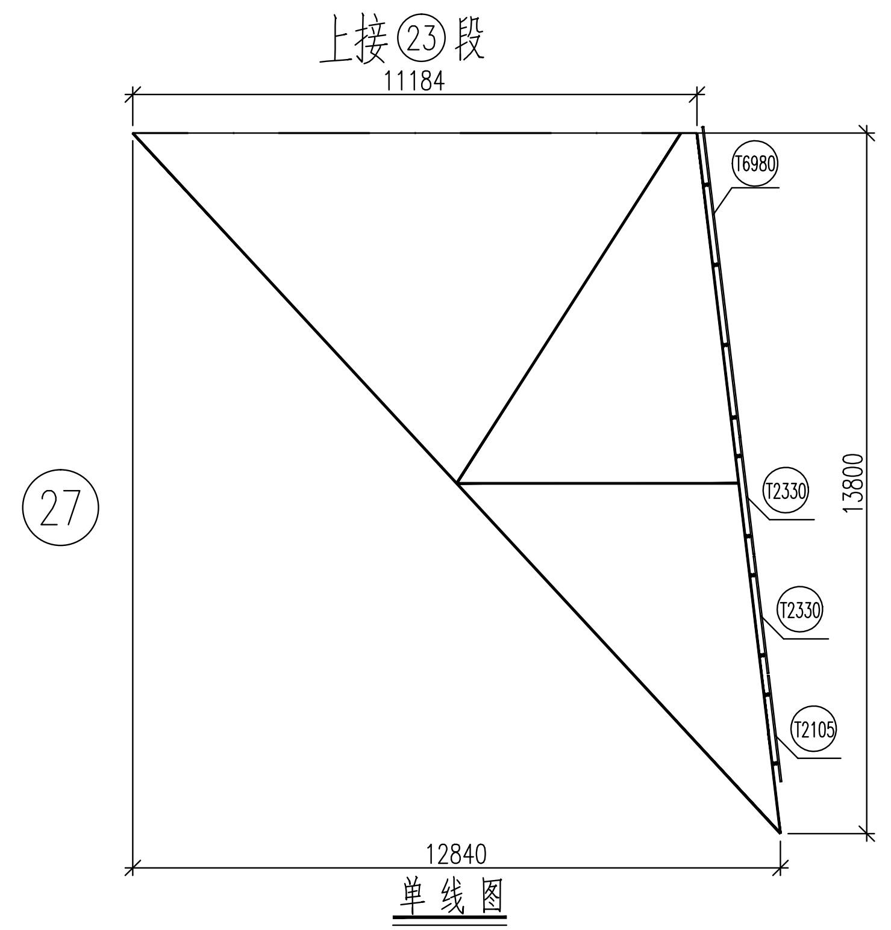

单线图
1:150

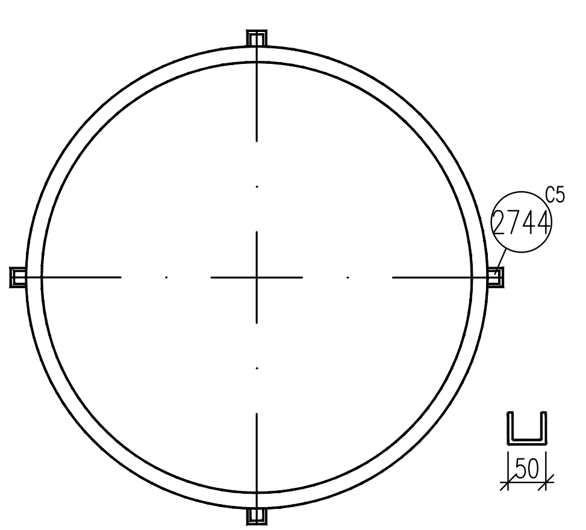

安全带挂点示意
扶手设置示意

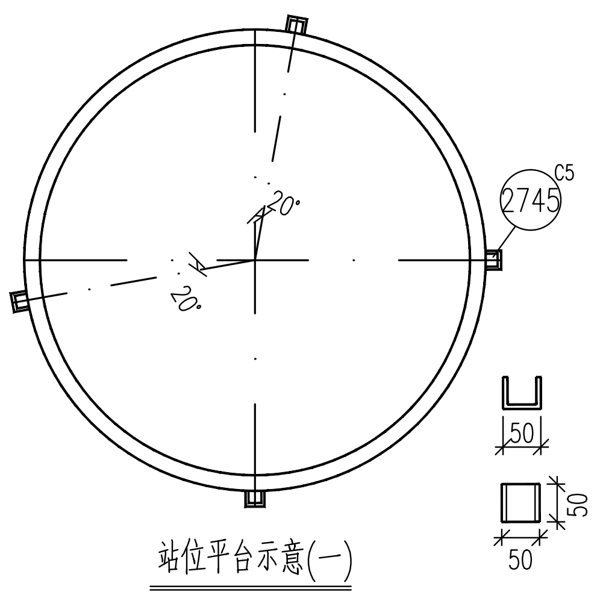

站位平台示意(一)

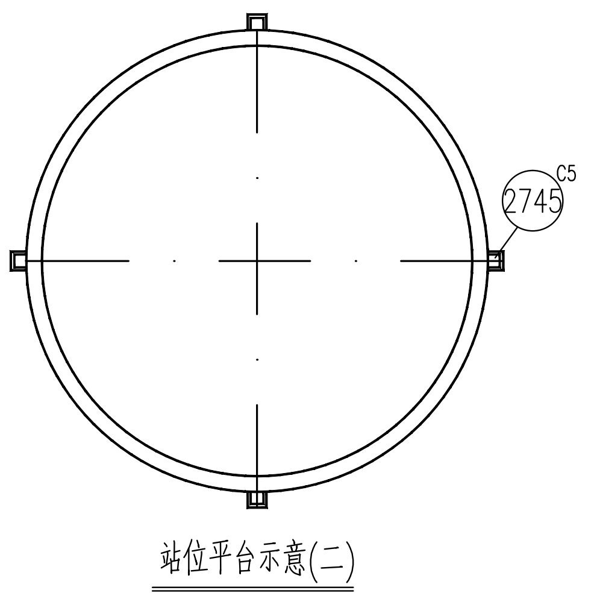

站位平台示意(二)

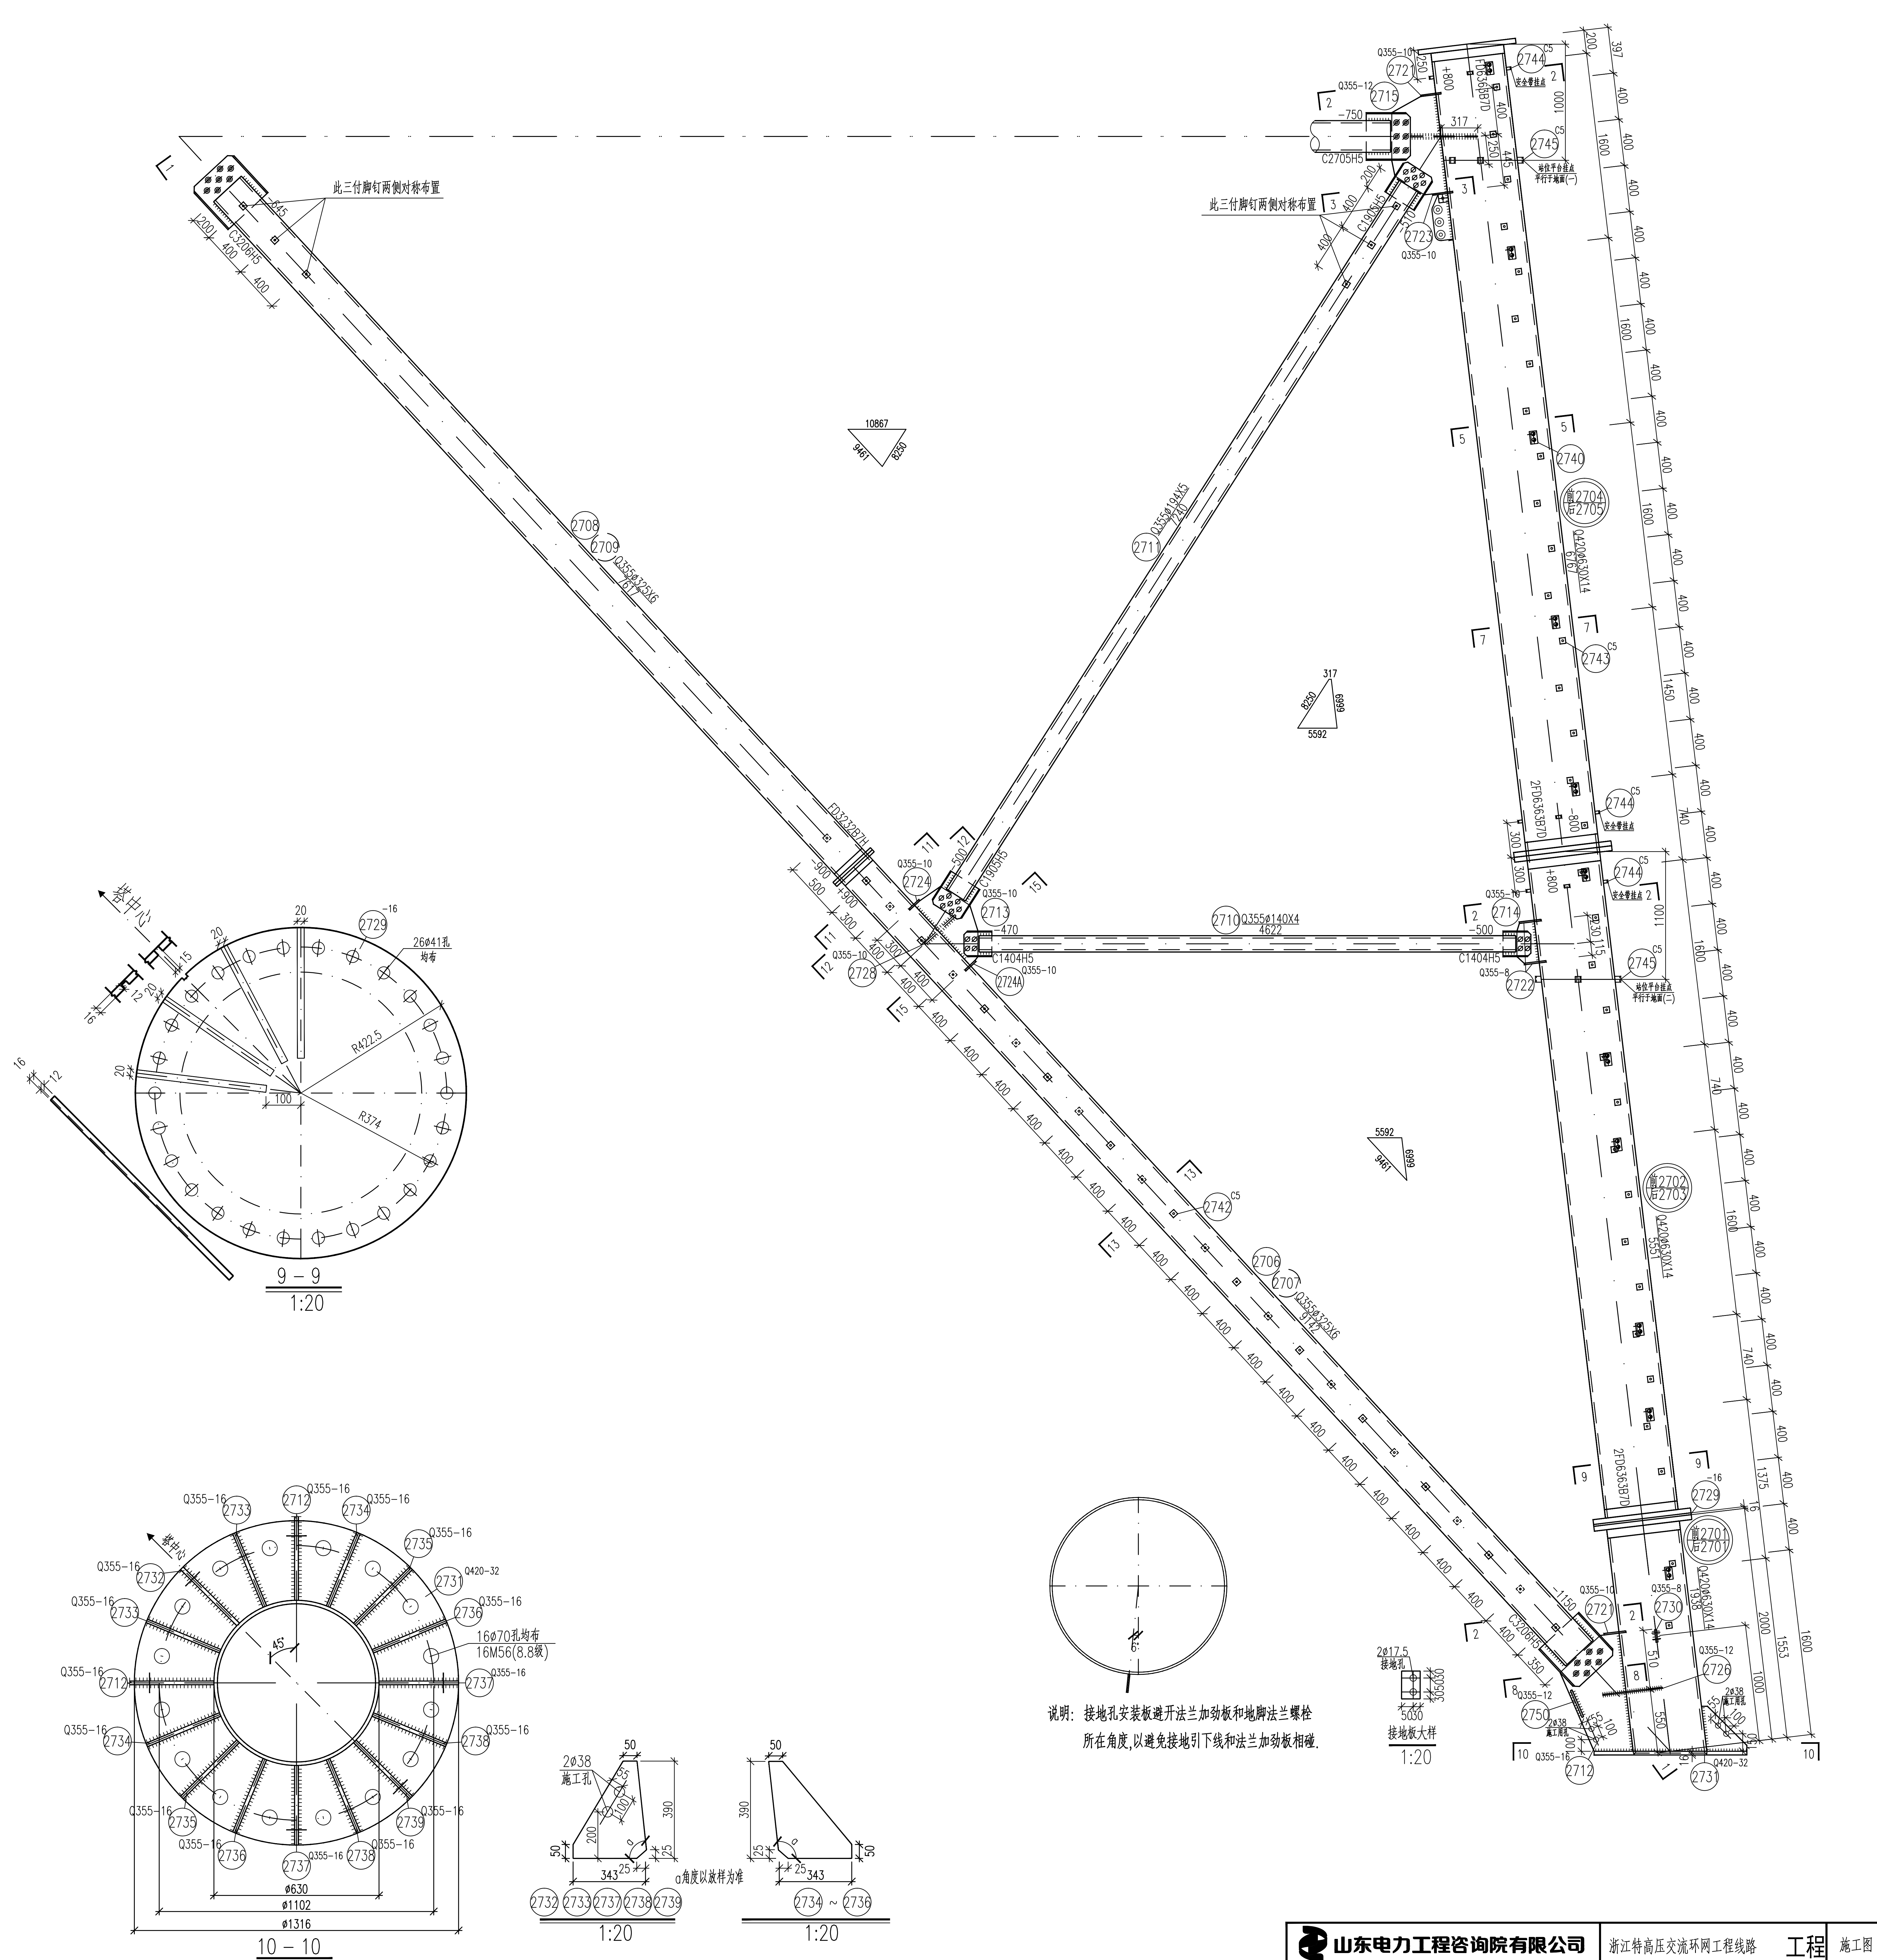

说明：接地孔安装板避开法兰加劲板和地脚法兰螺栓所在角度，以避免接地引下线和法兰加劲板相碰.

			山东电力工程咨询院有限公司		浙江特高压交流环网工程线路 工程	施工图	设计阶段
			批准	雷强	校核	马一丹	SZK31102A双回路直线塔 90.0-4.5m塔腿结构图(1/3) ㉗
			审核	高锡鹏			
电气	赵庆周	2026.08			设计/勘测	潘旺光	
专业	会签	日期	比例		日期	2026年 08月	图号 37-SA36901S-T0121-051 版本