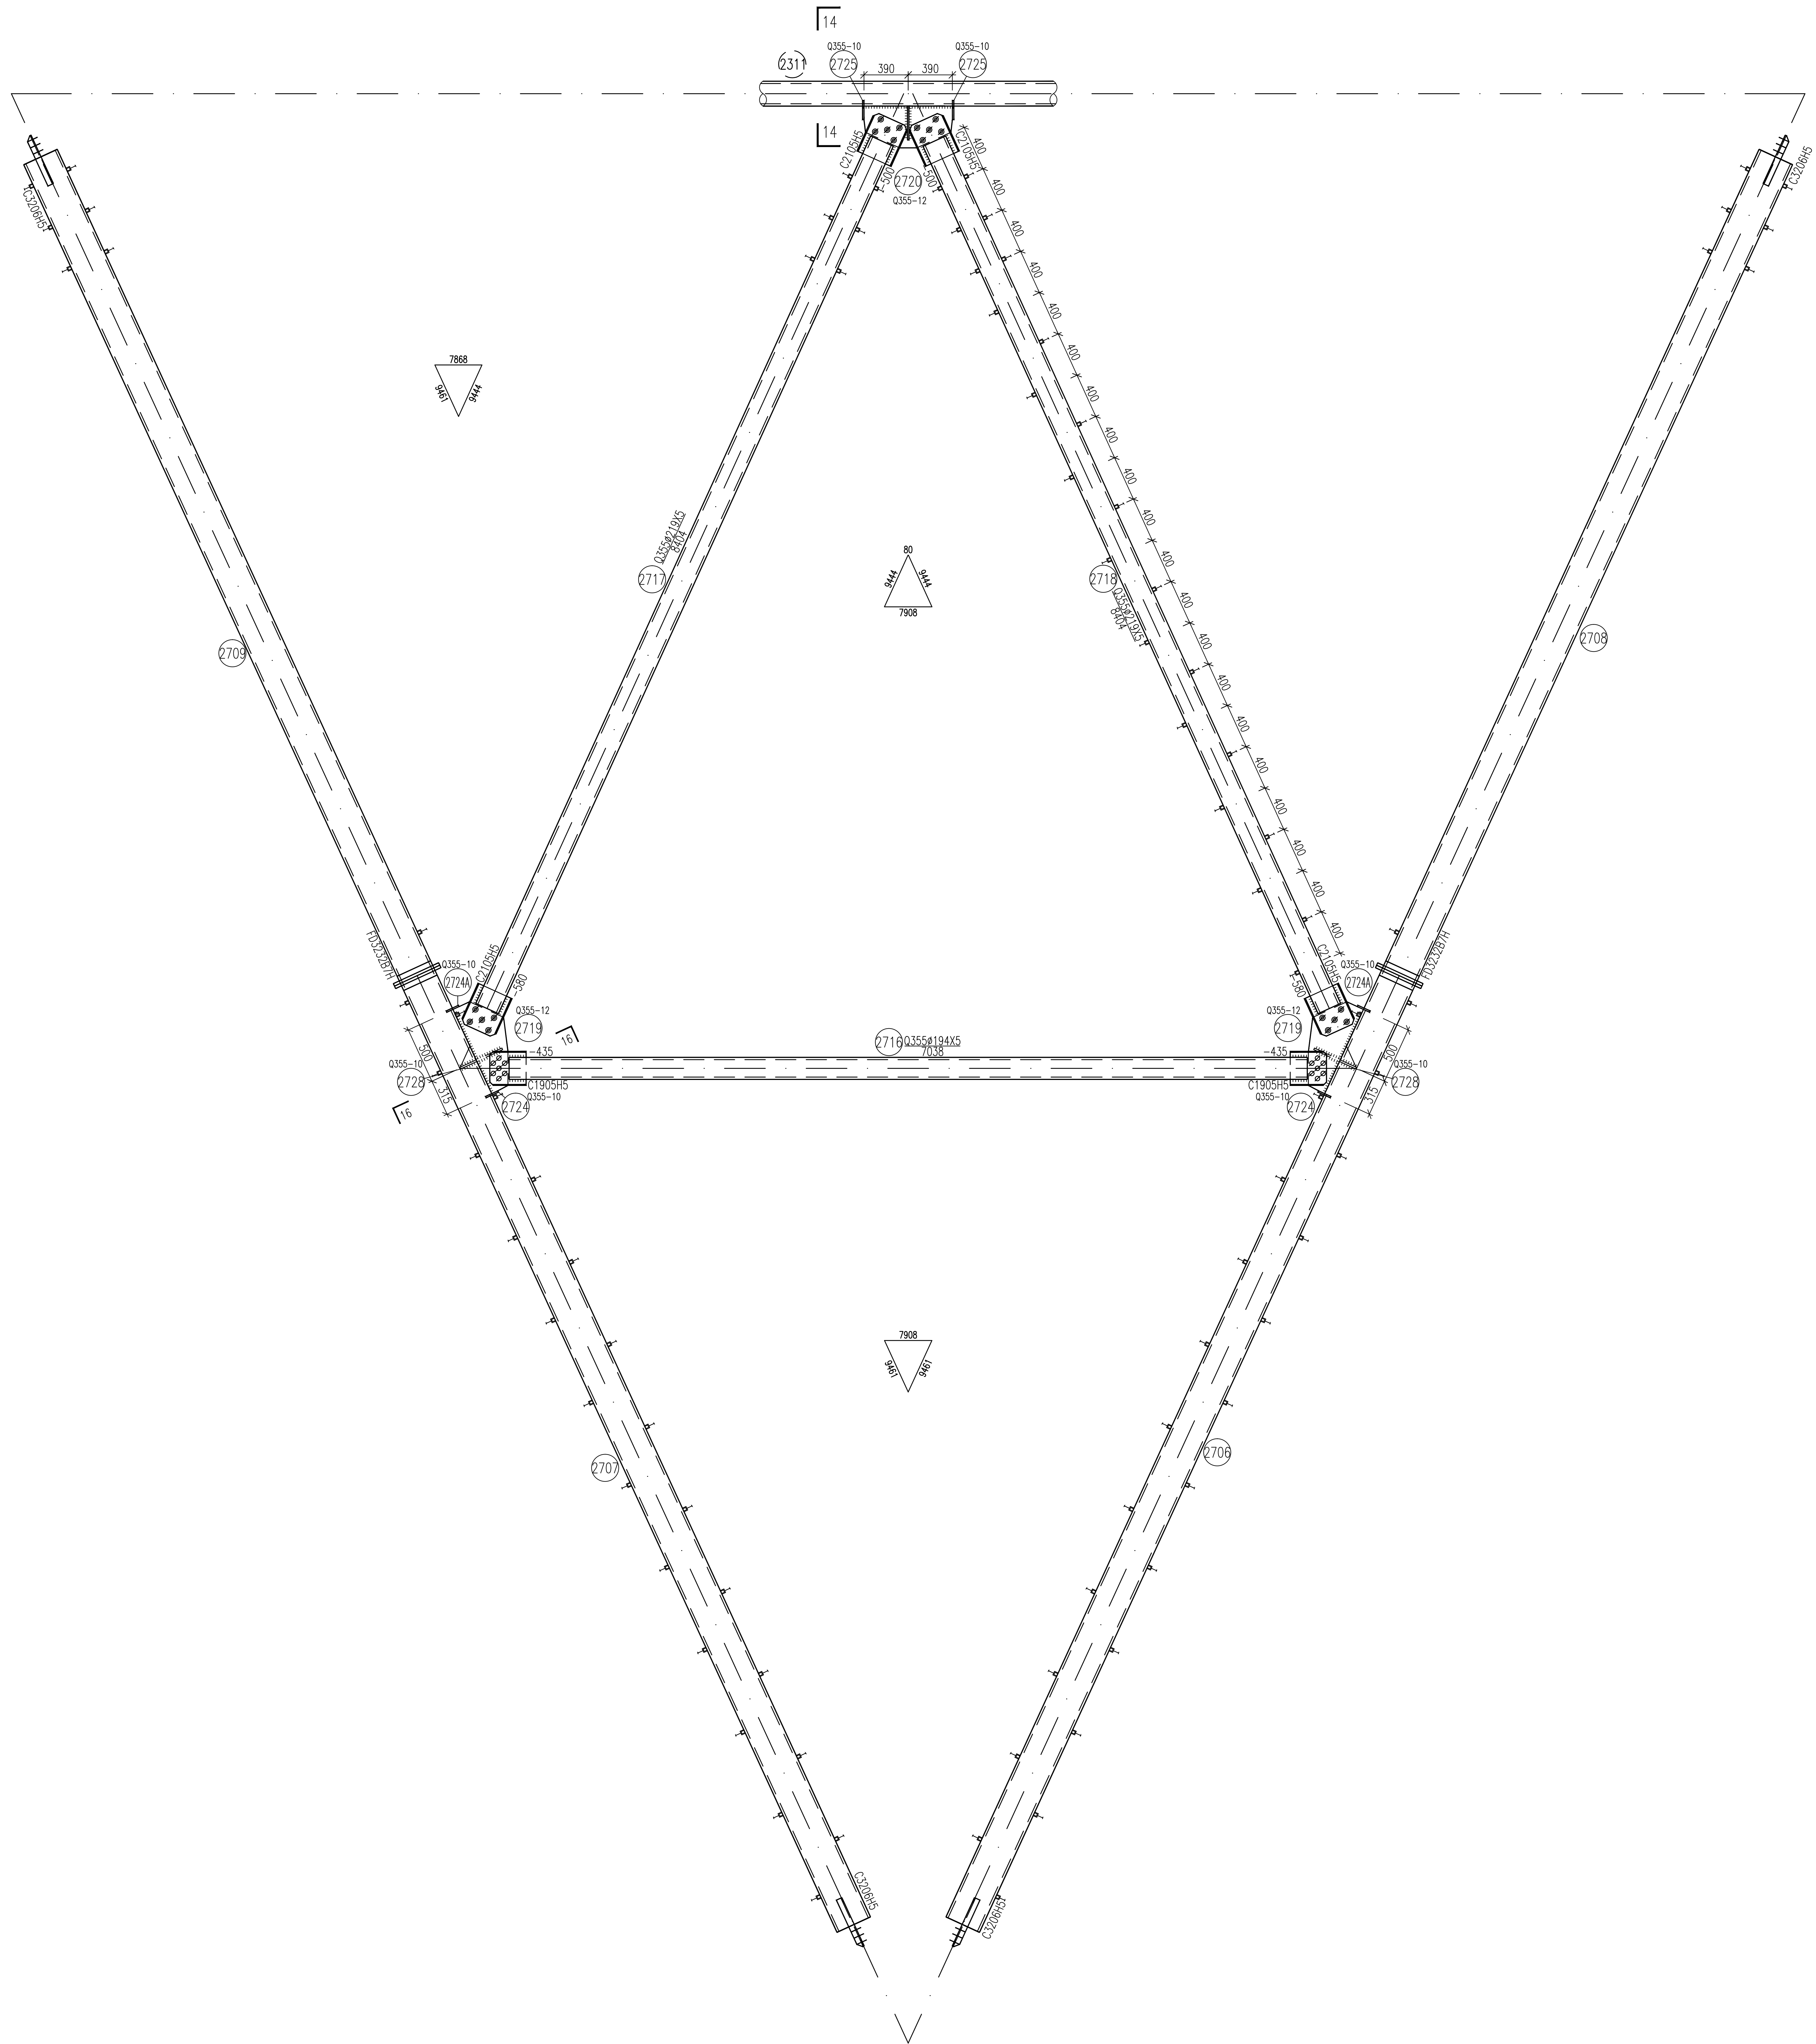
14
14
2311
Q355-10
2725
390
390
Q355-10
2725
C2105H5
C2105H5
-500
-500
2720
Q355-12
400
400
400
400
400
400
400
400
400
400
400
400
400
400
400
400
400
C3206H5
C3206H5
7868
9461
9444
Q355φ219X5
8404
2717
2709
80
9444
9444
7908
2718
Q355φ219X5
8404
2708
FD3232B7H
Q355-10
2724A
C2105H5
-580
Q355-12
2719
16
-435
2716
Q355φ194X5
7038
500
Q355-10
2728
315
C1905H5
Q355-10
2724
16
C2105H5
-580
Q355-10
2724A
FD3232B7H
Q355-12
2719
-435
C1905H5
Q355-10
2724
500
Q355-10
2728
315
7908
9461
9461
2707
2706
C3206H5
C3206H5

1-1

山东电力工程咨询院有限公司				浙江特高压交流环网工程线路 工程	施工图 设计阶段
批　准	雷强	校　核	马一丹	SZK31102A双回路直线塔 90.0-4.5m塔腿结构图(2/3) ㉗	
审　核	高锡鹏				
		设计/勘测	潘旺克		
比　例		日　期	2026年 08月	图　号 37-SA36901S-T0121-052	版本