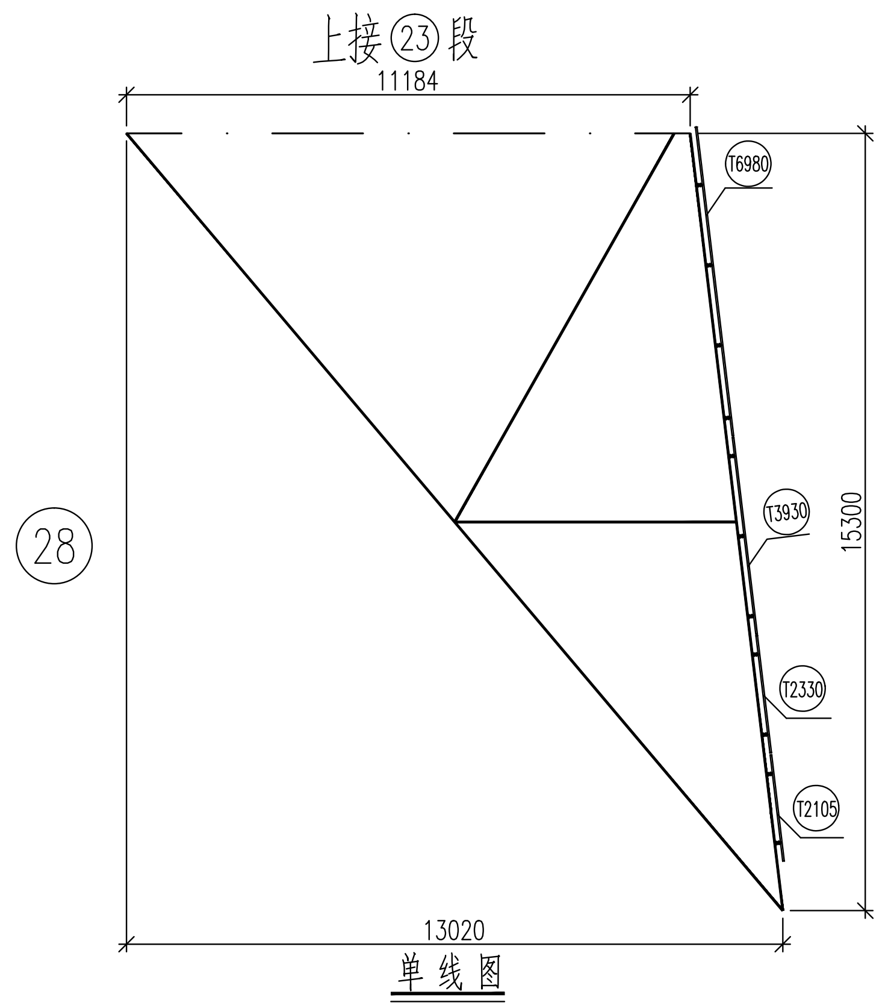
上接㉓段
11184
㉘
15300
T6980
T3930
T2330
T2105
13020

单线图

1:150

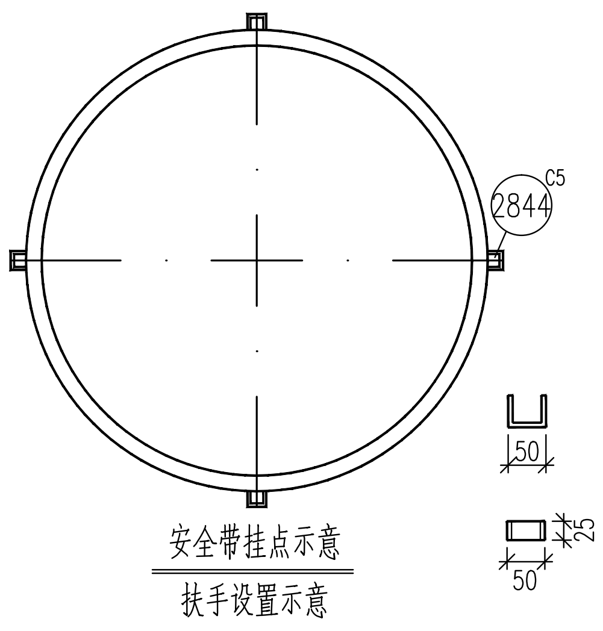

安全带挂点示意

扶手设置示意

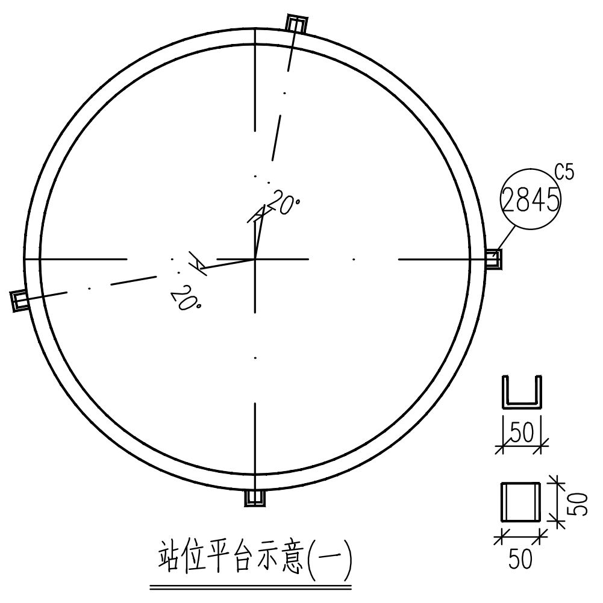
2845
C5
20°
50

站位平台示意(一)

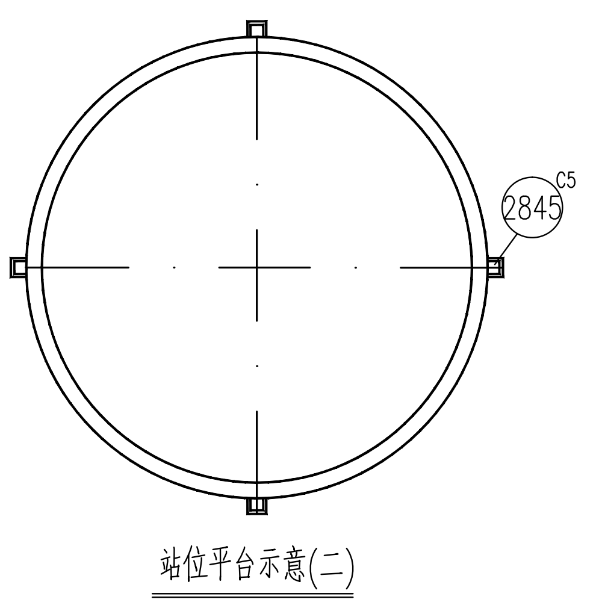

站位平台示意(二)

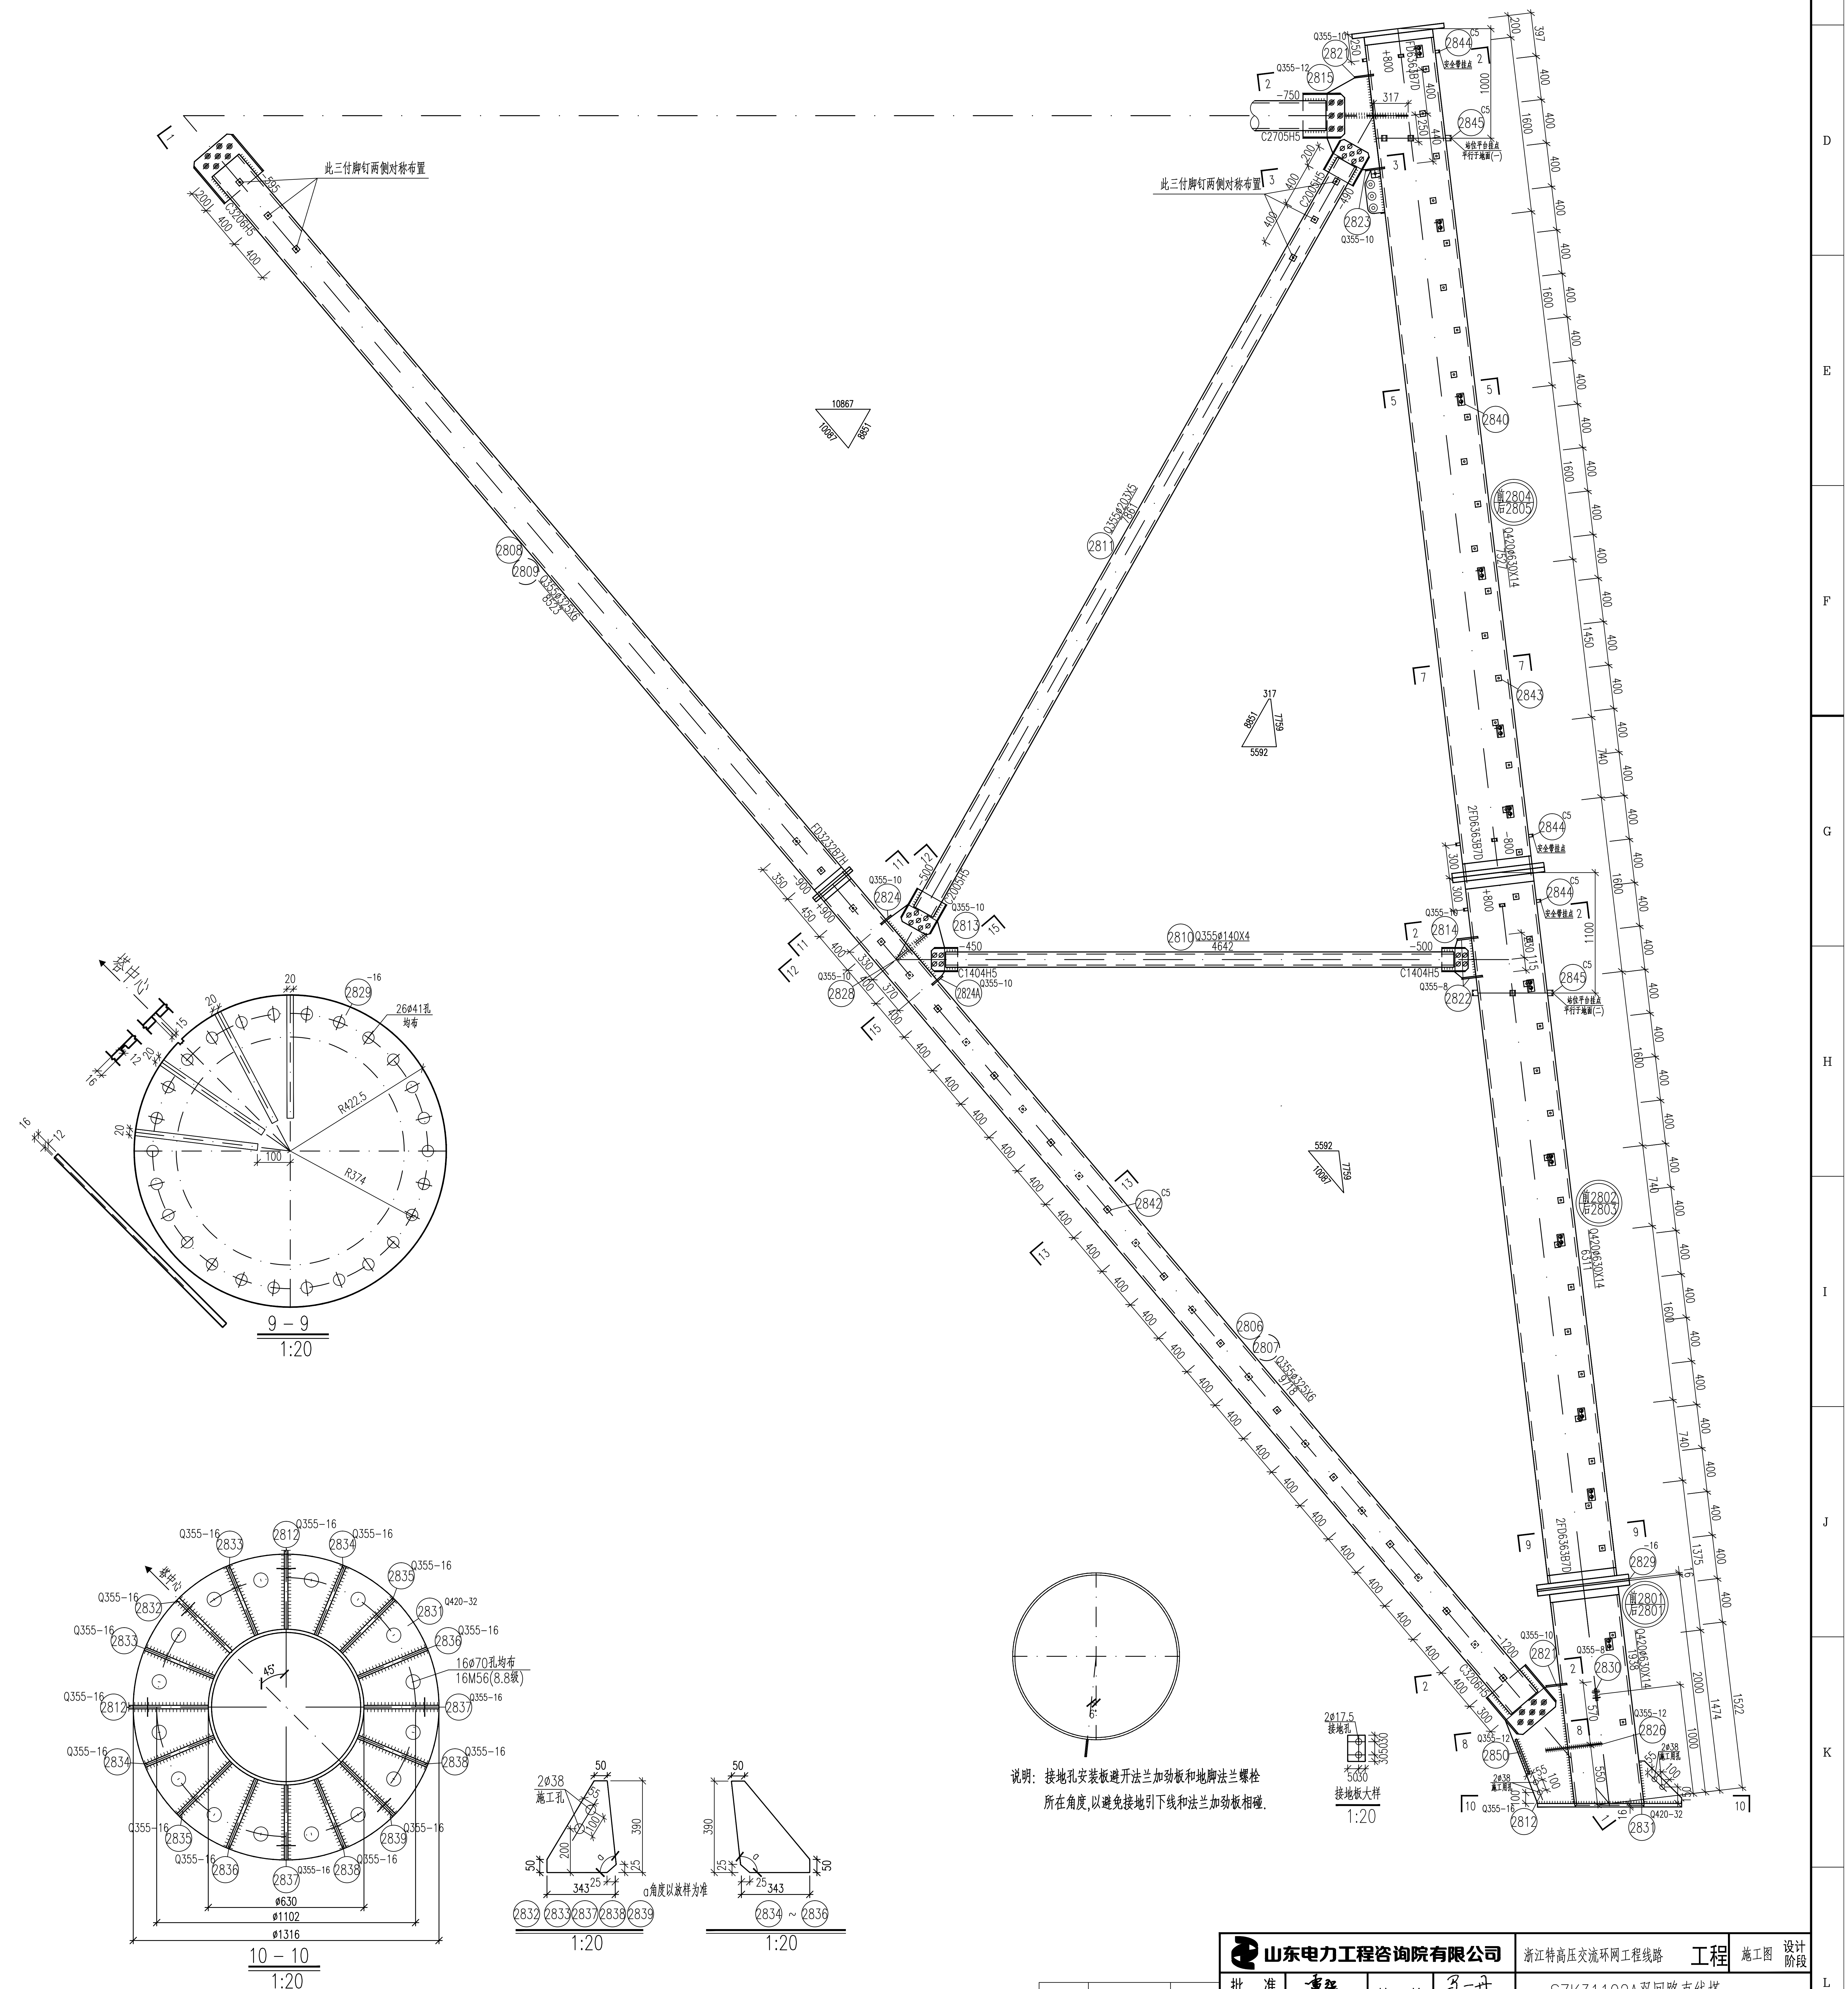
此三付脚钉两侧对称布置
2808
2809
2811
2806
2807
2810
Q355ф140X4
4642
2804
2805
2802
2803
2801
2840
2843
2842
2844
2845
2813
2814
2815
2821
2822
2823
2824
2826
2828
2829
2830
2831
2850
C1404H5
C2705H5
C3206H5
Q420ф630X14
Q355-10
Q355-12
Q355-16
Q420-32
10867
5592
7759
317
9 - 9
1:20
R422.5
R374
26ф41孔均布
塔中心
10 - 10
1:20
16ф70孔均布
16M56(8.8级)
ф630
ф1102
ф1316
2832
2833
2834
2835
2836
2837
2838
2839
2ф38
施工孔
343
390
α角度以放样为准
2834 ~ 2836
1:20
2ф17.5
接地孔
5030
305030

接地板大样

1:20

说明：接地孔安装板避开法兰加劲板和地脚法兰螺栓
所在角度，以避免接地引下线和法兰加劲板相碰.

			山东电力工程咨询院有限公司			浙江特高压交流环网工程线路 工程 | 施工图 | 设计阶段
			批 准	雷强	校 核	马一丹	SZK31102A双回路直线塔 90.0-3.0m塔腿结构图(1/3) ㉘
			审 核	高锡鹏		
电 气	赵庆周	2026.08			设计/勘测	潘旭光
专 业	会 签	日 期	比 例		日 期	2026年 08月	图 号 37-SA36901S-T0121-054 | 版本