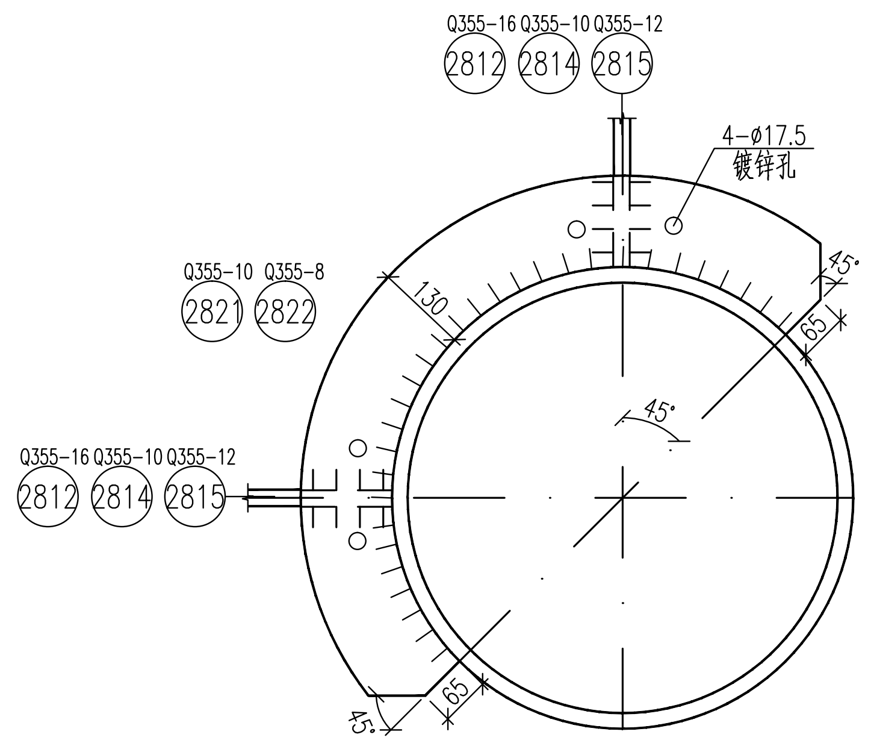
Q355-16 Q355-10 Q355-12
2812 2814 2815
4-ø17.5
镀锌孔
Q355-10 Q355-8
2821 2822
130
45°
45°
185
Q355-16 Q355-10 Q355-12
2812 2814 2815
45°
65
45

2 - 2
1:20

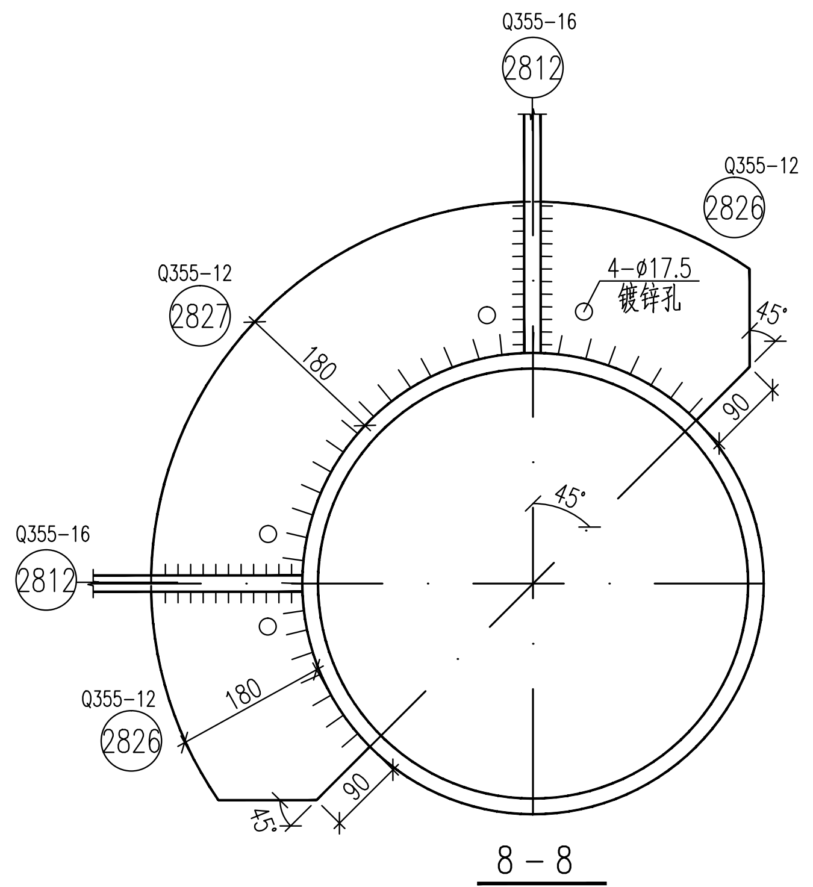
Q355-16
2812
Q355-12
2826
Q355-12
2827
4-ø17.5
镀锌孔
180
45°
90
45°
Q355-16
2812
Q355-12
2826
180
90
45

8 - 8
1:20

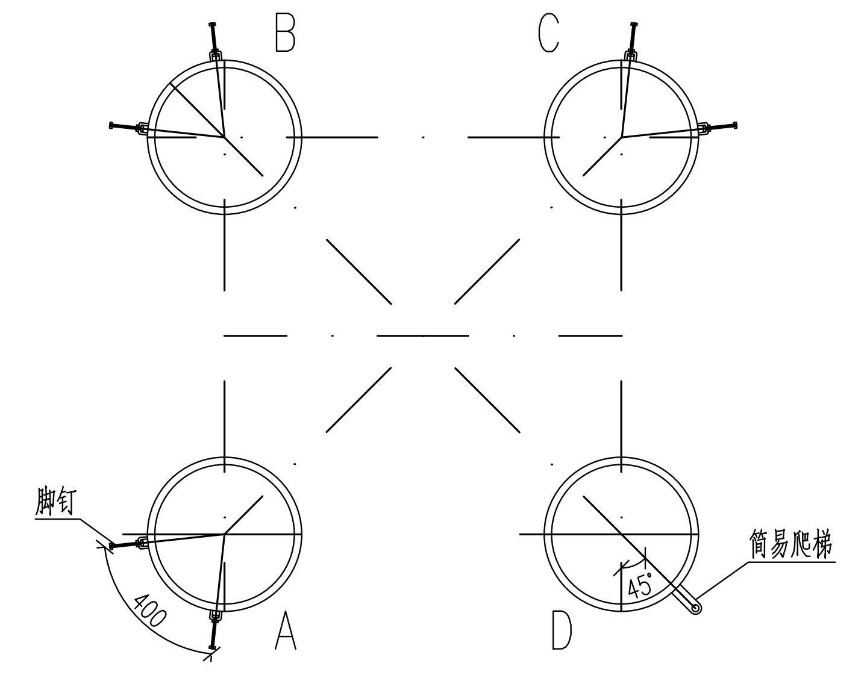
B
C
A
D
脚钉
400
45
筒易爬梯

爬梯脚钉示意图

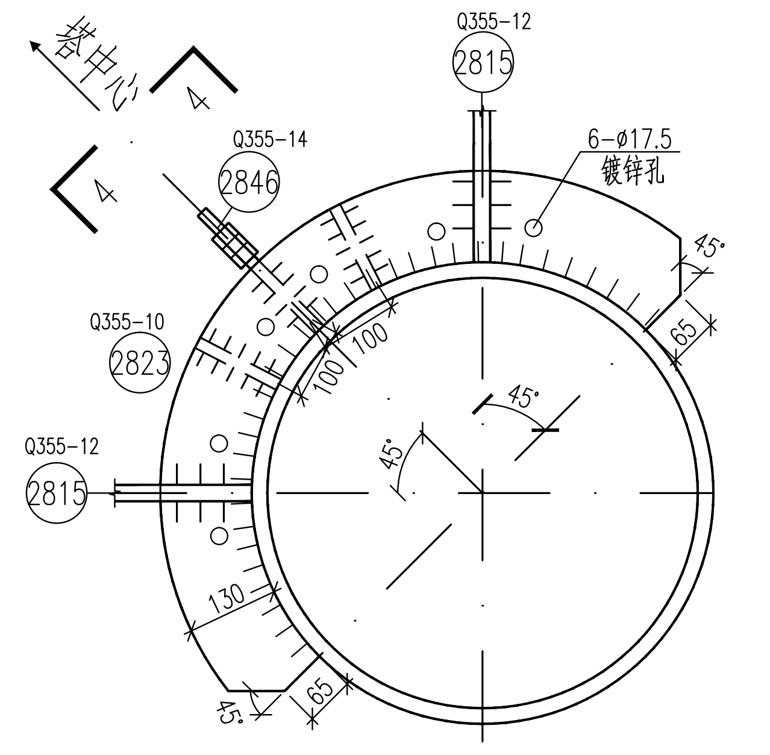
塔中心
4
4
Q355-12
2815
Q355-14
2846
6-ø17.5
镀锌孔
Q355-10
2823
100
100
45°
45°
Q355-12
2815
130
65
45

3 - 3
1:20

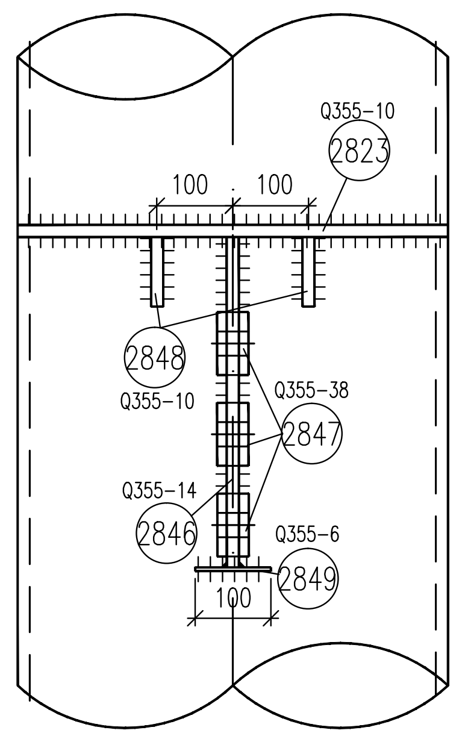
Q355-10
2823
100
100
2848
Q355-10
Q355-38
2847
Q355-14
2846
Q355-6
2849
100

4 - 4
1:20

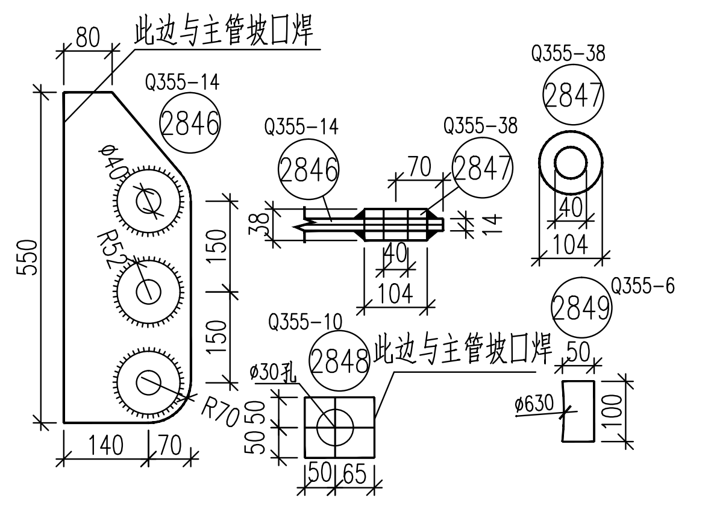
80
此边与主管坡口焊
Q355-14
2846
550
150
150
R70
140
70
Q355-14
2846
70
38
14
40
104
2847
Q355-38
2847
40
104
Q355-10
2848
此边与主管坡口焊
ø30
50
50
65
2849
Q355-6
ø30
100

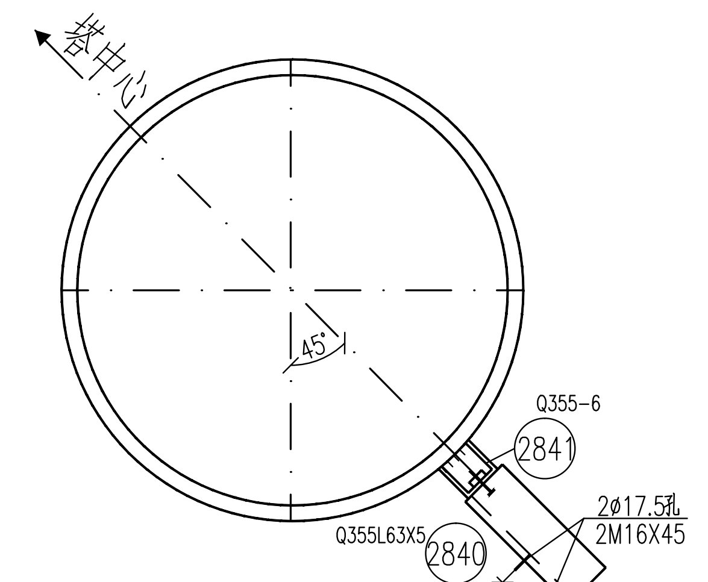
塔中心
45
Q355-6
2841
2ø17.5孔
2M16X45
Q355L63X5
2840
50
65

5 - 5
1:20

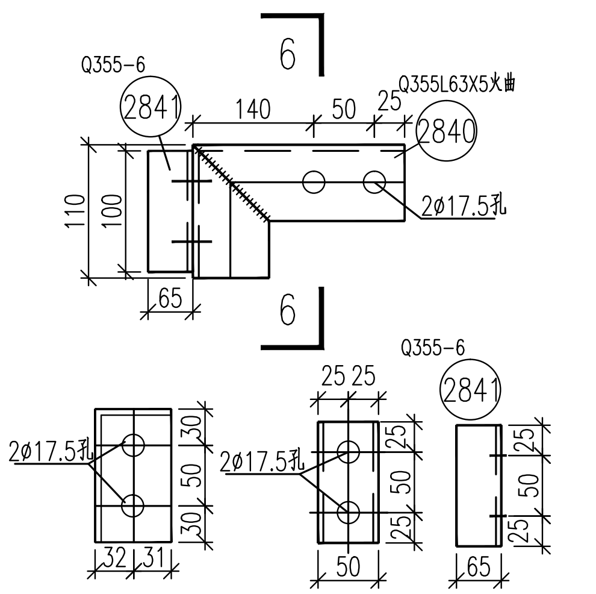
6
Q355-6
2841
140
50
25
Q355L63X5火曲
2840
2ø17.5孔
110
100
65
6
25 25
Q355-6
2841
2ø17.5孔
2ø17.5孔
30
50
30
25
50
25
32 31
50
65

6 - 6
1:5

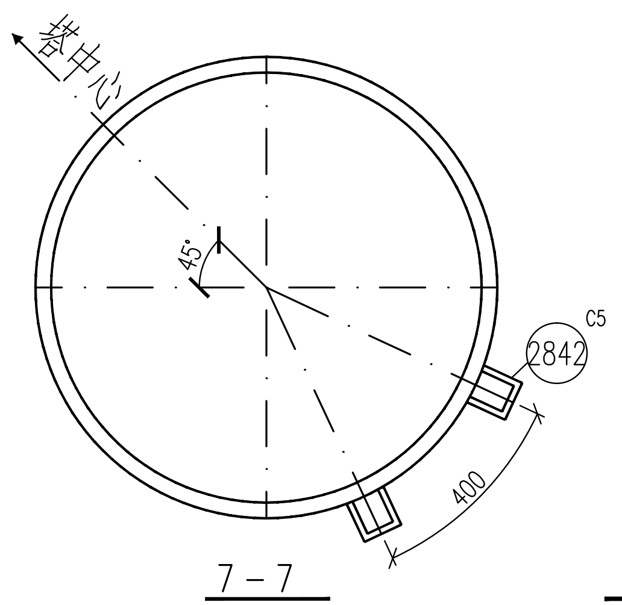
塔中心
45
C5
2842
400

7 - 7
1:20

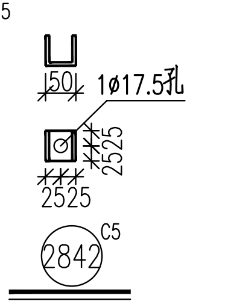
50
1ø17.5孔
25
25
2525
2842
C5

1:20

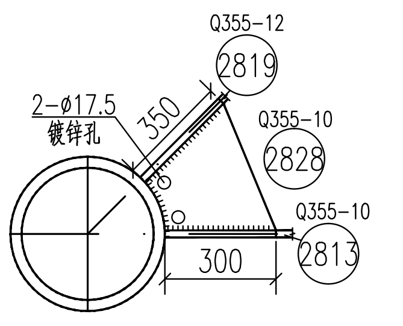
Q355-12
2819
2-ø17.5
镀锌孔
350
Q355-10
2828
Q355-10
2813
300

12 - 12
1:20

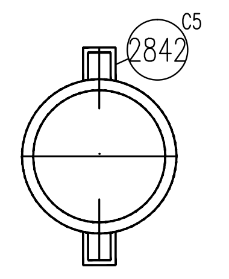

13 - 13
1:20

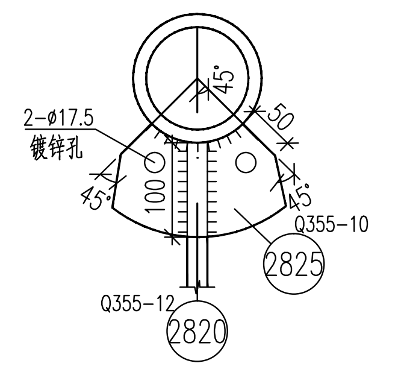
2-ø17.5
镀锌孔
45
100
45
50
Q355-10
2825
Q355-12
2820

14 - 14
1:20

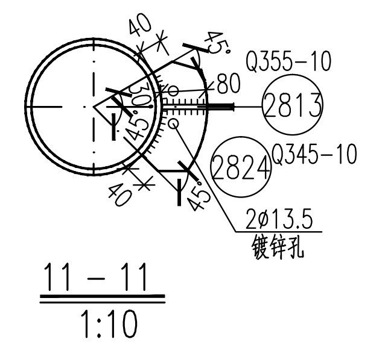
40
45
Q355-10
2813
80
2824
Q345-10
2ø13.5
镀锌孔

11 - 11
1:10

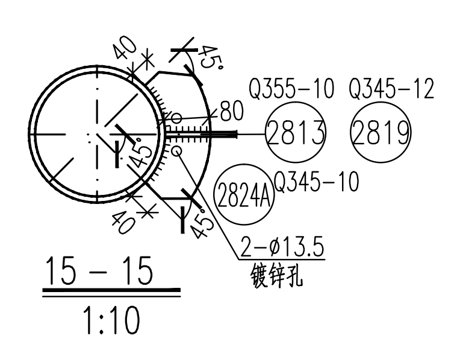
40
45
80
Q355-10
2813
Q345-12
2819
2824A
Q345-10
2-ø13.5
镀锌孔

15 - 15
1:10

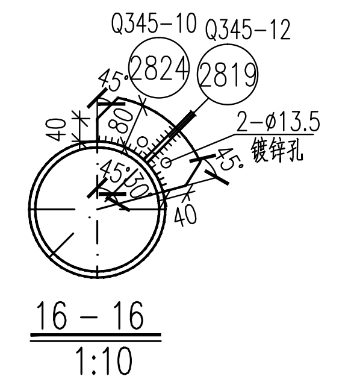
Q345-10
2824
Q345-12
2819
2-ø13.5
镀锌孔
40
45

16 - 16
1:10

## 构件明细表

| 编号 | 规格 | 长度 (mm) | 数量 | 重量 (kg) |  | 备注 |
|---|---|---|---|---|---|---|
|  |  |  |  | 一件 | 小计 |  |
| 2801 | Q420ø630X14 | 1938 | 1 | 412.18 | 412.2 | 一端切弧 带脚钉 |
| 2802 | Q420ø630X14 | 6311 | 1 | 1342.23 | 1342.2 | 装爬梯 |
| 2803 | Q420ø630X14 | 6311 | 0 | 1342.23 | 0.0 | 带脚钉 |
| 2804 | Q420ø630X14 | 7527 | 1 | 1600.85 | 1600.9 | 装爬梯 |
| 2805 | Q420ø630X14 | 7527 | 0 | 1600.85 | 0.0 | 带脚钉 |
| 2806 | Q355ø325X6 | 9718 | 1 | 458.71 | 458.7 | 带脚钉 |
| 2807 | Q355ø325X6 | 9718 | 1 | 458.71 | 458.7 | 带脚钉 |
| 2808 | Q355ø325X6 | 8523 | 1 | 402.30 | 402.3 | 带脚钉 |
| 2809 | Q355ø325X6 | 8523 | 1 | 402.30 | 402.3 | 带脚钉 |
| 2810 | Q355ø140X4 | 4642 | 2 | 62.28 | 124.6 |  |
| 2811 | Q355ø203X5 | 7861 | 2 | 191.93 | 383.9 | 带脚钉 |
| 2812 | Q355-16X593 | 1232 | 2 | 91.76 | 183.5 |  |
| 2813 | Q355-10X390 | 770 | 2 | 23.57 | 47.1 |  |
| 2814 | Q355-10X205 | 380 | 2 | 6.12 | 12.2 |  |
| 2815 | Q355-12X495 | 935 | 2 | 43.60 | 87.2 |  |
| 2816 | Q355ø194X5 | 7028 | 1 | 163.79 | 163.8 |  |
| 2817 | Q355ø245X5 | 8911 | 1 | 263.71 | 263.7 | 带脚钉 |
| 2818 | Q355ø245X5 | 8911 | 1 | 263.71 | 263.7 | 带脚钉 |
| 2819 | Q355-12X446 | 957 | 2 | 40.21 | 80.4 |  |
| 2820 | Q355-12X491 | 946 | 1 | 43.75 | 43.8 |  |
| 2821 | Q355-10X130 | 1313 | 2 | 13.40 | 26.8 |  |
| 2822 | Q355-8X130 | 1313 | 2 | 10.72 | 21.4 |  |
| 2823 | Q355-10X130 | 1313 | 1 | 13.40 | 13.4 |  |
| 2824 | Q355-10X65 | 255 | 4 | 1.30 | 5.2 |  |
| 2824A | Q355-10X65 | 306 | 4 | 1.56 | 6.2 |  |
| 2825 | Q355-10X100 | 276 | 2 | 2.17 | 4.3 |  |
| 2826 | Q355-12X180 | 306 | 2 | 5.19 | 10.4 |  |
| 2827 | Q355-12X180 | 613 | 1 | 10.39 | 10.4 |  |
| 2828 | Q355-10X200 | 275 | 2 | 4.32 | 8.6 |  |
| 2829 | -16X845 | 845 | 1 | 70.43 | 70.4 | 遮水板 |
| 2830 | Q355-8X80 | 110 | 1 | 0.55 | 0.6 |  |
| 2831 | Q420-32X1316 | 1316 | 1 | 263.37 | 263.4 |  |
| 2832 | Q355-16X343 | 390 | 1 | 16.80 | 16.8 |  |
| 2833 | Q355-16X343 | 390 | 2 | 16.80 | 33.6 |  |
| 2834 | Q355-16X343 | 390 | 2 | 16.80 | 33.6 |  |
| 2835 | Q355-16X343 | 390 | 2 | 16.80 | 33.6 |  |
| 2836 | Q355-16X343 | 390 | 2 | 16.80 | 33.6 |  |
| 2837 | Q355-16X343 | 390 | 2 | 16.80 | 33.6 |  |
| 2838 | Q355-16X343 | 390 | 2 | 16.80 | 33.6 |  |
| 2839 | Q355-16X343 | 390 | 1 | 16.80 | 16.8 |  |
| 2840 | Q355L63X5 | 325 | 12 | 1.57 | 18.8 | 火曲 (用于主材装爬梯) |
| 2841 | Q355-6X100 | 180 | 12 | 0.85 | 10.2 | 火曲 (用于主材装爬梯) |
| 2842 | C5 | 50 | 110 | 0.27 | 29.7 | 槽钢 (用于主材装爬梯) |
| 2843 | C5 | 50 | 149 | 0.27 | 40.2 | 槽钢 (用于主材带脚钉) |
| 2844 | C5 | 25 | 12 | 0.14 | 1.7 | 槽钢 |
| 2845 | C5 | 50 | 8 | 0.27 | 2.2 | 槽钢 |
| 2846 | Q355-14X210 | 550 | 1 | 12.69 | 12.7 |  |
| 2847 | Q355-38X104 | 104 | 3 | 3.23 | 9.7 |  |
| 2848 | Q355-10X100 | 115 | 2 | 0.90 | 1.8 |  |
| 2849 | Q355-6X50 | 100 | 1 | 0.24 | 0.2 |  |
| 2850 | Q355-12X80 | 335 | 2 | 2.52 | 5.0 |  |
|  | C1905H5 |  | 2 | 8.80 | 17.60 |  |
|  | C2405H5 |  | 4 | 17.27 | 69.08 |  |
|  | C1404H5 |  | 4 | 4.80 | 19.20 |  |
|  | C2005H5 |  | 4 | 9.74 | 38.96 |  |
|  | C3206H5 |  | 4 | 31.43 | 125.72 |  |
|  | FD3232B7H |  | 4 | 16.80 | 67.2 |  |
|  | FD6363B7D |  | 5 | 103.00 | 515.0 |  |
|  | T2105 | – | 1 | 11.50 | 11.50 | 主材安装爬梯 |
|  | T2330 | – | 1 | 12.40 | 12.40 | 主材安装爬梯 |
|  | T3930 | – | 1 | 20.70 | 20.70 | 主材安装爬梯 |
|  | T6980 | – | 1 | 36.20 | 36.20 | 主材安装爬梯 |
|  |  |  |  |  |  |  |
|  |  |  |  |  |  |  |
|  |  |  |  |  |  |  |
| 合计 |  | 8333.8 kg (用于主材带脚钉) |  |  |  |  |
| 合计 |  | 8433.1 kg (用于主材装爬梯) |  |  |  |  |

## 螺栓、脚钉、垫圈明细表

| 名称 | 级别 | 规格 | 符号 | 数量 | 重量(kg) | 备注 |
|---|---|---|---|---|---|---|
| 螺栓 | 6.8级 | M16X45 | ◍ | 48 | 8.1 | 用于主材装爬梯 |
|  |  | M20X65 | ⊘ | 58 | 20.5 |  |
|  | 8.8级 | M24X75 | ⦻ | 46 | 27.3 |  |
|  |  | M20X100 | ○ | 44 | 21.8 | 法兰螺栓 |
|  |  | M39X175 | ○ | 52 | 184.6 | 法兰螺栓 |
|  |  | M39X190 | ○ | 26 | 96.0 | 法兰螺栓 |
| 脚钉 | 6.8级 | M16X185 | ⊖ | 110 | 45.6 | 用于主材装爬梯 |
|  |  | M16X185 |  | 149 | 61.8 | 用于主材带脚钉 |
|  |  |  |  |  |  |  |
| 垫圈 | Q235 |  | 规格X个数 |  |  |  |
|  |  |  |  |  |  |  |
| 合计 |  |  | 412.0 kg (用于主材带脚钉) |  |  |  |
| 合计 |  |  | 403.9 kg (用于主材装爬梯) |  |  |  |

说明：1.材料表为一个塔腿的重量。
2.本段塔腿为铁塔D腿，安装爬梯，当为A、B、C腿时需焊接脚钉连接槽钢。

| 山东电力工程咨询院有限公司 |  |  |  | 浙江特高压交流环网工程线路 工程 | 施工图 | 设计阶段 |
|---|---|---|---|---|---|---|
| 批准 |  | 校核 | 马一丹 | SZK31102A双回路直线塔<br>90.0-3.0m塔腿结构图(3/3) ㉘ |  |  |
| 审核 | 高锡鹏 |  |  |  |  |  |
|  |  | 设计/勘测 |  |  |  |  |
| 比例 |  | 日期 | 2026年 08月 | 图号 | 37-SA36901S-T0121-056 | 版本 |